

A REMODEL FOR:

BLUE LAKES URGENT CARE
1309 BLUE BLAKES BLVD TWIN FALLS, ID

Sheet List	
Sheet Number	Sheet Name
A0-0	TITLE SHEET
A2-1	NEW FLOOR PLAN
A3-0	DEMO EXTERIOR ELEVATIONS
A3-1	DEMO EXTERIOR ELEVATIONS
A1-0	DEMOLITION SITE PLAN
A1-1	NEW SITE PLAN
A3-3	NEW EXTERIOR ELEVATIONS
A3-4	NEW EXTERIOR ELEVATIONS
SUP 1.0	SUP SITE PLAN
SUP 3.0	COLORED EXTERIOR ELEVATIONS
SUP 3.1	COLORED EXTERIOR ELEVATIONS
A3-5	NEW EXTERIOR ELEVATIONS
A3-2	DEMO EXTERIOR ELEVATIONS
A7-0	CEILING PLAN
A8-0	INTERIOR ELEVATIONS
A2-2	DIMENSION FLOOR PLAN
A8-1	INTERIOR ELEVATIONS
A8-2	INTERIOR ELEVATIONS
A8-3	INTERIOR ELEVATIONS
A10-2	INTERIOR DETAILS
A8-4	INTERIOR ELEVATIONS
A9-0	ROOM FINISH SCHEDULE
A9-2	DOOR & WINDOW TYPES
A10-0	CASEWORK DETAILS
A9-1	FINISH FLOOR PLAN
A10-1	CASEWORK DETAILS
A6-1	WALL SECTIONS & TYPES
A6-0	WALL TYPES PLAN
A10-3	ROOF DETAILS

ABBREVIATIONS

AC	ACOUSTICAL CEILING	DIA	DIAMETER	GYP BD	GYPSUM BOARD	PL	PLATE, PLASTIC LAMINATE	T	THREAD
ADJ	ADJUSTABLE - ADJACENT	DIM	DIMENSION	HB	HOSE BIB	P-LAM	PLASTIC LAMINATE	TBB	TILE BACKER BOARD
AFF	ABOVE FINISH FLOOR	DF	DRINKING FOUNTAIN	HC	HANDICAPPED	PLWD	PLYWOOD	T&G	TONGUE AND GROOVE
AL	ALUMINUM	DP	DEEP	HDR	HEADER	PNL	PANEL	TO	TO OF
ALT	ALTERNATE	DR	DOOR	HM	HOLLOW METAL	PORC. TILE	PORCELAIN TILE	TOW	TOP OF WALL
ANOD	ANODIZED	DS	DOWNSPOUT	HORIZ	HORIZONTAL	PR	PAIR	TPD	TOILET PAPER DISPENSER
AP	ACOUSTICAL WALL PANEL	DWG	DRAWING	HT	HEIGHT	PSF	POUNDS PER SQUARE FOOT	TSCD	TOILET SEAT COVER DISPENSER
APPROX	APPROXIMATE	E	EAST	HVAC	HEATING/VENTILATING/	PSI	POUNDS PER SQUARE INCH	TT	TIRE TREAD
ARCH	ARCHITECT (-URAL)	(E)	EXISTING		AIR CONDITIONING	PT	PAINT, PRESSURE TREATED	TYP	TYPICAL
AW	ACOUSTICAL WALL	EA	EACH	ILO	IN LIEU OF	PTD	PAPER TOWEL DISPENSER	UNO	UNLESS NOTED OTHERWISE
AWF	ACOUSTICAL WALL FABRIC	EJ	EXPANSION JOINT	INSUL	INSULATION	QT	QUARTZ TILE	U/S	UNDERSIDE
BLDG	BUILDING	EL	ELEVATION	INT	INTERIOR	R	RISER, RADIUS	VB	VAPOR BARRIER
BM	BEAM	ELEC	ELECTRIC (-AL)	JNT	JOINT	RB	RESILIENT BASE	VCT	VINYL COMPOSITION TILE
BOD	BOTTOM OF DECK	EP	ENAMEL PAINT	KD	KNOCK DOWN	RD	ROOF DRAIN	VERT	VERTICAL
BOT	BOTTOM	EQ	EQUAL	LAV	LAVATORY	RO	ROUGH OPENING	VGF	VINYL GYM FLOORING
BTWN	BETWEEN	EW	EACH WAY	MCFP	MULTI-COLORED FINISH	RR	RESTROOM	VIF	VINYL INDUSTRIAL FLOORING
CB	CATCH BASIN	EXG	EXISTING		PAINT SYSTEM	RSF	RUBBER SHEET FLOORING	VR	VAPOR RETARDER
CBT	CABINET	EXP	EXPANSION	MDO	MEDIUM DENSITY	S	SOUTH	VT	VINYL TILE
CG	CORNER GUARD	EXT	EXTERIOR		OVERLAY PLYWOOD	SC	SOLID CORE	WWF	VINYL WALL FABRIC
CJ	CONTROL JOINT	FA	FIRE ALARM	MECH	MECHANIC (-AL)	SCU	STRUCTURAL CLAY UNIT	W	WEST
CL	CENTERLINE	FD	FLOOR DRAIN	MFR	MANUFACTURE (-R)	SD	SOAP DISPENSER	W/C	WATER CLOSET
CLG	CEILING	FE	FIRE EXTINGUISHER	MIN	MINIMUM	SDSV	STATIC DISIPATIVE SHEET VINYL	WD	WOOD
CLR	CLEAR (-ANCE)	FEC	FIRE EXTINGUISHER CABINET	MISC	MISCELLANEOUS	SF	SPECIALTY FINISH	W/D	WASHER & DRYER
CMT	CERAMIC MOSAIC TILE	FF	FACTORY FINISH, FINISH FLOOR	MRGB	MOISTURE RESISTANT	SFGL	SAFETY GLASS	WDO	WINDOW
CMU	CONCRETE MASONRY UNIT	FIN	FINISH (-ED)		GYPSUM BOARD	SHTG	SHEDDING	WF	WALL FABRIC
CO	CLEAN OUT	FLR	FLOOR (-ING)	MTL	METAL	SIM	SIMILAR	WFFV	WOOD FACE VENEER
COL	COLUMN	FND	FOUNDATION	N	NORTH	SL	SLOPE	WG	WIRE GUARD
CONC	CONCRETE	FOC	FACE OF CONCRETE	(N)	NEW	SND	SANITARY NAPKIN DISPENSER	WGL	WIRED GLASS
CONT	CONTINUOUS, CONTINUE	FRP	FIBERGLASS REINFORCED	NA, N/A	NOT APPLICABLE	SP	SPACE (-S)	WM	WIRE MESH
CORR	CORRIDOR		PLASTIC PANEL	NIC	NOT IN CONTRACT	SPEC	SPECIFICATION	WO	WITHOUT
CP	CARPET	FRVR	FLAME RESISTANT VAPOR BARRIER	NDU	SANITARY NAPKIN	SQ	SQUARE	WOC	WALK-OFF CARPET
CS	CONCRETE SLAB, SEALED	FT	FOOT, FEET		DISPOSAL UNIT	S/S	STAINLESS STEEL	WP	WATERPROOFING
CT	CERAMIC TILE	FTG	FOOTING	NOM	NOMINAL	ST	STAIN	WPS	WALL PROTECTION SYSTEM
CTJ	CONTROL JOINT	FWC	FABRIC WALL COVERING	NTS	NOT TO SCALE	STL	STEEL	WR	WATER RESISTANT
CTR	COUNTER (-TOP)	GA	GAGE	OC	ON CENTER	STR	STRUCTURE (-AL)	WRGB	WATER RESISTANT GYPSUM
DBL	DOUBLE	GALV	GALVANIZED	OD	OUTSIDE DIAMETER	STRG	STORAGE		WALLBOARD
DET	DETAIL	GH	GARMENT HOOK	OPP	OPPOSITE	SV	SHEET VINYL FLOORING	WWF	WELDED WIRE FABRIC
		GMM	GLASS MESH MORTAR BOARD	PCMU	PRE-FACED CMU			W/	WITH

GENERAL NOTES:

- ALL WORK SHALL MEET CURRENT STATE, LOCAL CODES, ORDINANCES, & 2018 IBC
- ALL MECHANICAL, ELECTRICAL, & PLUMBING WORK SHALL MEET ALL CURRENT APPLICABLE STATE & LOCAL CODES.
- ALL UTILITIES SHALL BE PROPERLY IDENTIFIED & LOCATED BEFORE WORK BEGINS ON PROJECT.
- CONTRACTOR SHALL VERIFY ALL CONDITIONS & DIMENSIONS AT THE JOB SITE & NOTIFY THE ARCHITECT OF ANY DIMENSIONAL ERRORS, OMISSIONS, OR DISCREPANCIES BEFORE BEGINING OR FABRICATING ANY WORK.
- DO NOT SCALE DRAWINGS.
- ALL DOOR HANDLES SHALL BE LEVER TYPE, ALL DOOR HARDWARE SHALL BE A.D.A COMPLIANT AS PER CURRENT ANSI 117.1
- AT MAIN ENTRANCE DOOR SHALL HAVE SINGLE ACTION LOCKING DEVICE &/ OR SIGNED "THIS DOOR TO REMAIN UNLOCKED WHEN BUILDING IS OCCUPIED."

TWIN FALLS FIRE DEPARTMENT NOTES:

- IT SHALL BE THE RESPONSIBILITY OF THE GENERAL CONTRACTOR TO INSURE THAT ALL DEFERRED SUBMITTALS REQUIRED BY THE FIRE DEPARTMENT **HAVE BEEN APPROVED BY THE STATE PRIOR TO THE INSTALLATION OF A FIRE ALARM SYSTEM**, IT SHALL ALSO BE THE RESPONSIBILITY OF THE GENERAL CONTRACTOR TO VERIFY THAT ALL APPROPRIATE TESTING AND/OR INSPECTIONS HAVE BEEN PERFORMED BEFORE COVERING OR CALLING FOR A FINAL INSPECTION.
FIRE ALARM PLANS SHALL BE SENT TO THE STATE FIRE MARSHAL OFFICE AND DESIGNED IN ACCORDANCE WITH CURRENT NFPA 13 STANDARDS.
IDAHO STATE FIRE MARSHAL
700 WEST STATE STREET, 3RD FLOOR
BOISE, IDAHO 83720
PLANS SHALL MEET CURRENT IFC, NFPA 13R AND IDAHO STATE PLUMBING CODES, AND BE APPROVED PRIOR TO INSTALLATION.
-

PLAN ANALYSIS
Based on 2018 Edition of I.B.C

Architect of Record Laughlin Ricks Architecture, L.L.C.

Engineer:

Job Address:

Legal Description:

Occupancy Classification: Occupant Load Per Area:

Occupancy Use:

Allowable Stories Per Code: Provided: (IBC Table 505.4) Total:

Floor Area: Basement: 1st: Exits Required: Basement: 1st:

Mezzanine: 3rd: Total: 2nd: 3rd: 4th:

Required Exits Per Occupant Load: (IBC Table 1006.3.2)

Actual furthest travel distance to exit: (IBC Table 1017.2 & 1006.2.1)

Penetrations? Show Approved Listed Products on Plans:

Type of Construction: Allowable Building Height:

Seismic Design Category: Allowable Area Calc's:

Automatic Sprinkler System: Yes: No: (IBC Table 506.2)

Maximum Floor Area Allowed: Exit Signs: Yes: No:

Special Inspections Required? Yes: No: Emergency Lights: Yes: No:

Firewalls Required? Yes: No: Fire Extinguishers Shown: Yes: No: (IFC Section 906)

Occupancy Separation Use? Yes: No: Fire Hydrant Locations Shown: Yes: No:

Areas of Refuge Required? Yes: No: Vestibule Required: Yes: No: (IBC Section 1009.2,3,4)

Area Separation Required? Yes: No: Classified Areas? Yes: No: (Show on plans & Show Areas)

Fire Resistance Ratings of BLDG Elements : (IBC Table 601) (Specify Rating)

Minimum Roof Class: (IBC Table 1505.1) Exterior Wall Openings: (IBC 705.8)

Fire Doors: (IBC Table 716.1.2) Fire Alarm System: (IBC 907.2)

Fire Flow and Duration: Corridor Width: (IBC Table 1020.2)

Rated Structural Frame: Yes: No: Rated Corridors: Yes: No: (Roof Supports Only) (IBC Section 1020.1)

Rated Bearing Walls-Exterior: Yes: No: Rated Bearing Walls-Interior: Yes: No:

Rated Nonbearing Walls-Exterior: Yes: No: Rated Bearing Walls-Interior: Yes: No: (>30' Fire Separation) (Roof Supports Only)

Rated Nonbearing Walls-Exterior: Yes: No: Rated Nonbearing Walls-Interior: Yes: No: (10'-30' Fire Separation)

Rated Floor Construction: Yes: No: Rated Roof Construction: Yes: No:

Lighting Layout and COM Check? Yes: No:

Comments:

1 PLAN ANALYSIS
1/4" = 1'-0"

FIRE ALARM & DETECTION SYSTEM SHALL BE MODIFIED.

4.19.22

DATE

A REMODEL FOR:

BLUE LAKES URGENT CARE
1309 BLUE BLAKES BLVD TWIN FALLS, ID

TITLE SHEET

Laughlin Ricks Architecture
—architecture/planning—
134 3RD AVE. E. * Twin Falls, Idaho 83301
PHONE: (208) 736-8050

DATE: 4.19.22


NM

RCR


Drawn

Checked

A0-0

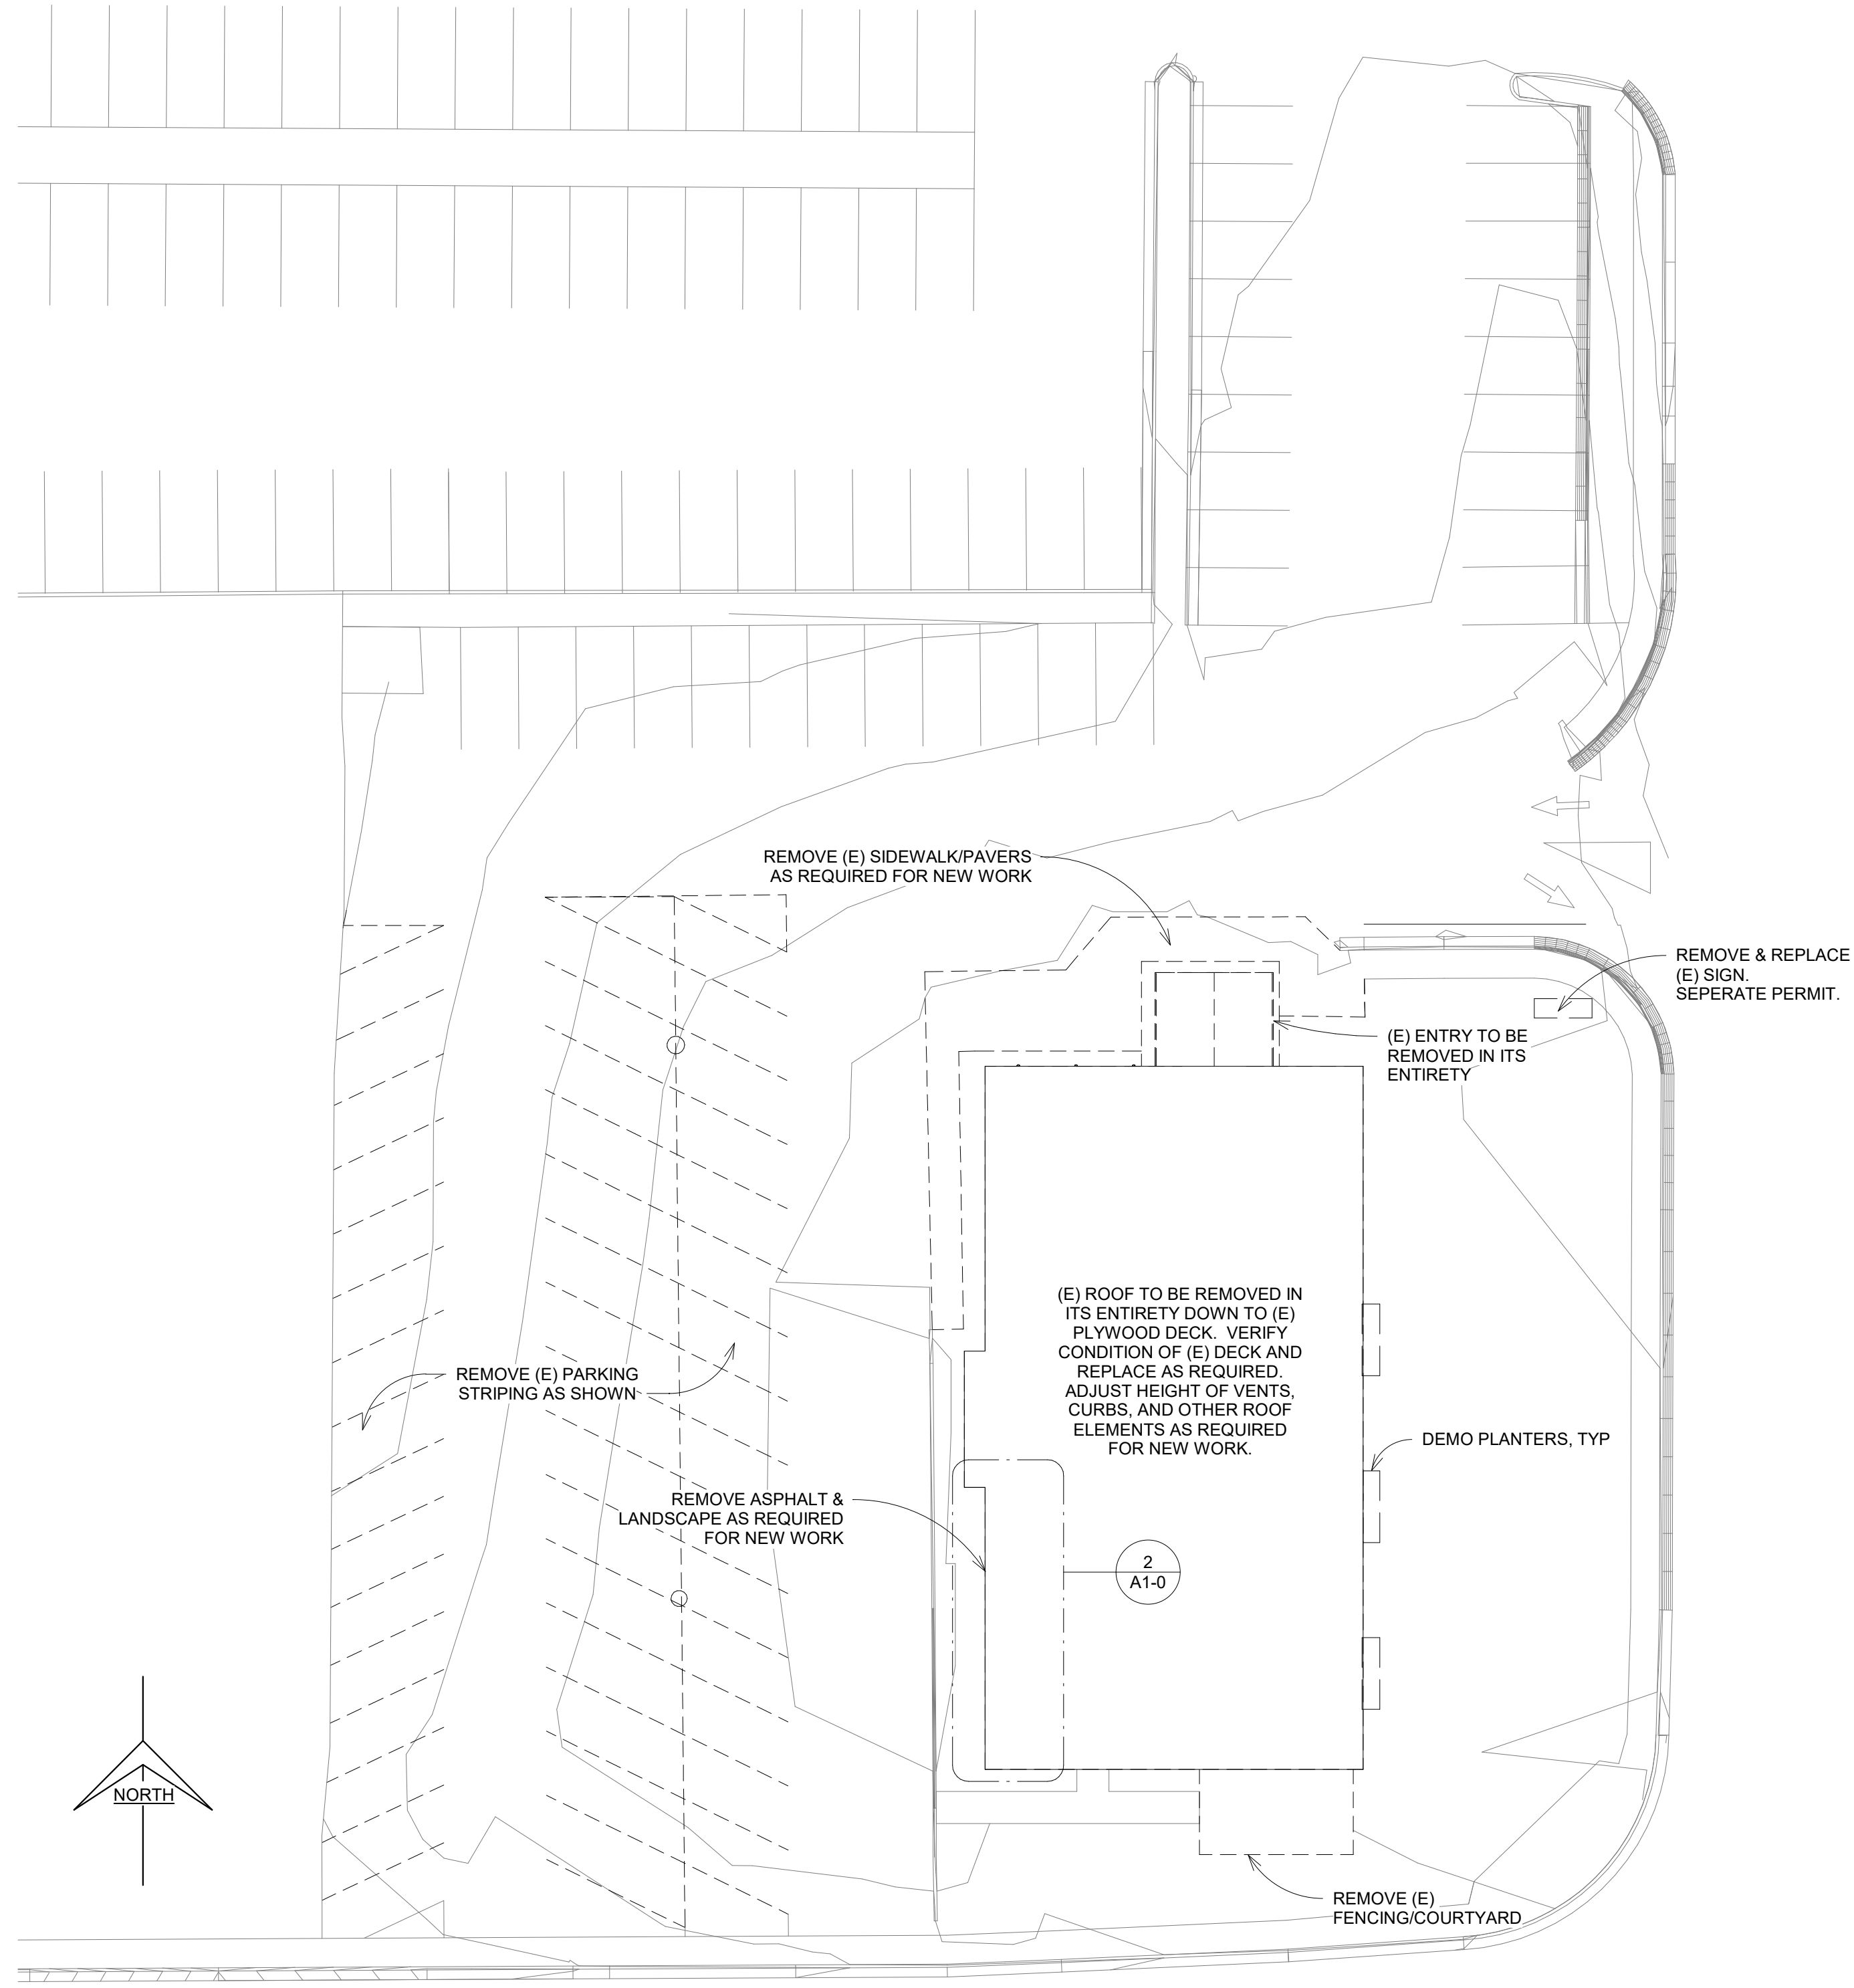

1 DEMO SITE PLAN
1" = 20'-0"

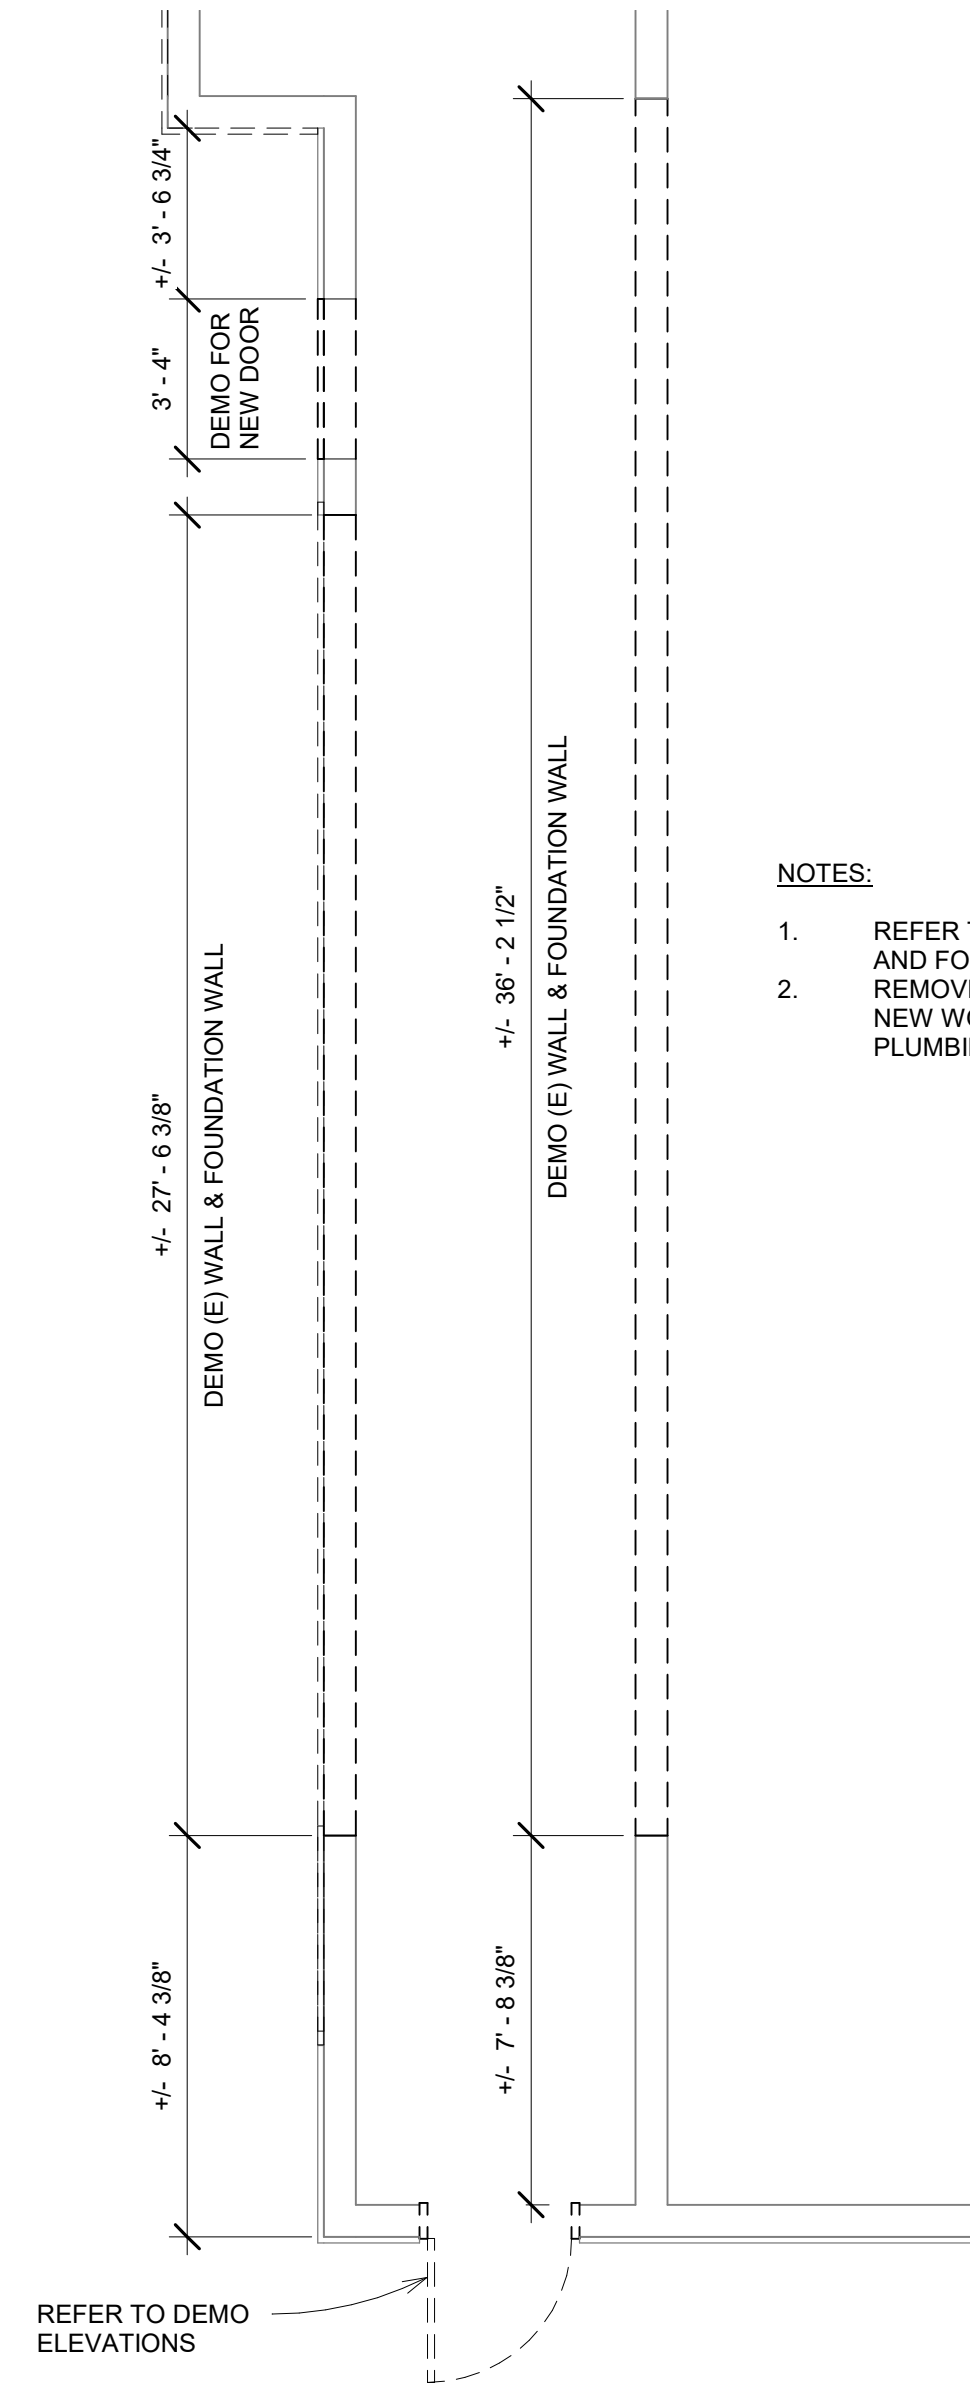

2 PARTIAL DEMO FLOOR PLAN
1/4" = 1'-0"

- NOTES:
1. REFER TO STRUCTURAL FOR NEW BEAMS, COLUMNS, AND FOUNDATION REQUIREMENTS
 2. REMOVE EXISTING CONCRETE SLAB AS REQUIRED FOR NEW WORK. REFER TO FLOOR PLAN FOR NEW PLUMBING ELEMENTS.

A REMODEL FOR:
BLUE LAKES URGENT CARE
1309 BLUE LAKES BLVD TWIN FALLS ID
DEMOLITION SITE PLAN

Laughlin Ricks Architecture
architecture/planning
134 3RD AVE. E. * Twin Falls, Idaho 83301
PHONE: (208) 736-8050

DATE: 4.19.22
NM RCR
Drawn Checked

A1-0

C-1 ZONE

1309 BLUE LAKES BLVD N
TWIN FALLS, ID 83301




SETBACKS
FRONT YARD: 35'
NO SET BACK SIDE & REAR

LANDSCAPE REQUIREMENT:
1 TREE PER 500 SF
1 BUSH PER 100 SF
50% OF THE REQUIRED TREES SHALL BE
EVERGREENS. ALL TREES
SHALL HAVE A HEIGHT OF AT LEAST FOUR FEET
(4') WHEN PLANTED.
50% OF THE REQUIRED BUSHES SHALL BE
EVERGREENS.

BLUE LAKES BLVD LANDSCAPE REQUIREMENTS:
1,158 SF LANDSCAPE PROVIDED
2 TREES REQUIRED
12 BUSHES REQUIRED

ON SITE LANDSCAPING REQUIRED:
1,198 SF REQUIRED
6,657 SF PROVIDED
2 TREES REQUIRED
12 BUSHES REQUIRED

PARKING REQUIREMENT
6,036/250=24 REQUIRED SPACES
27 PARKING SPACES PROVIDED

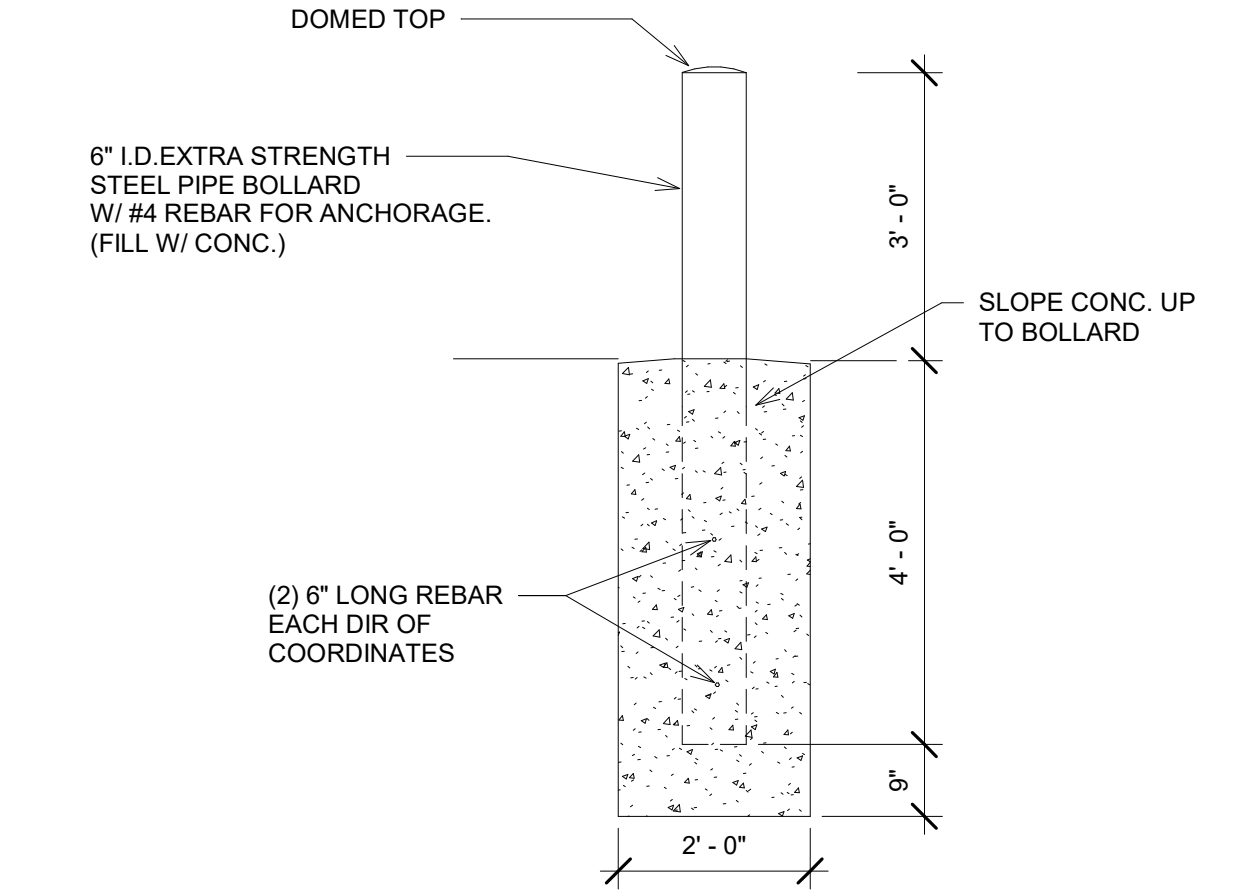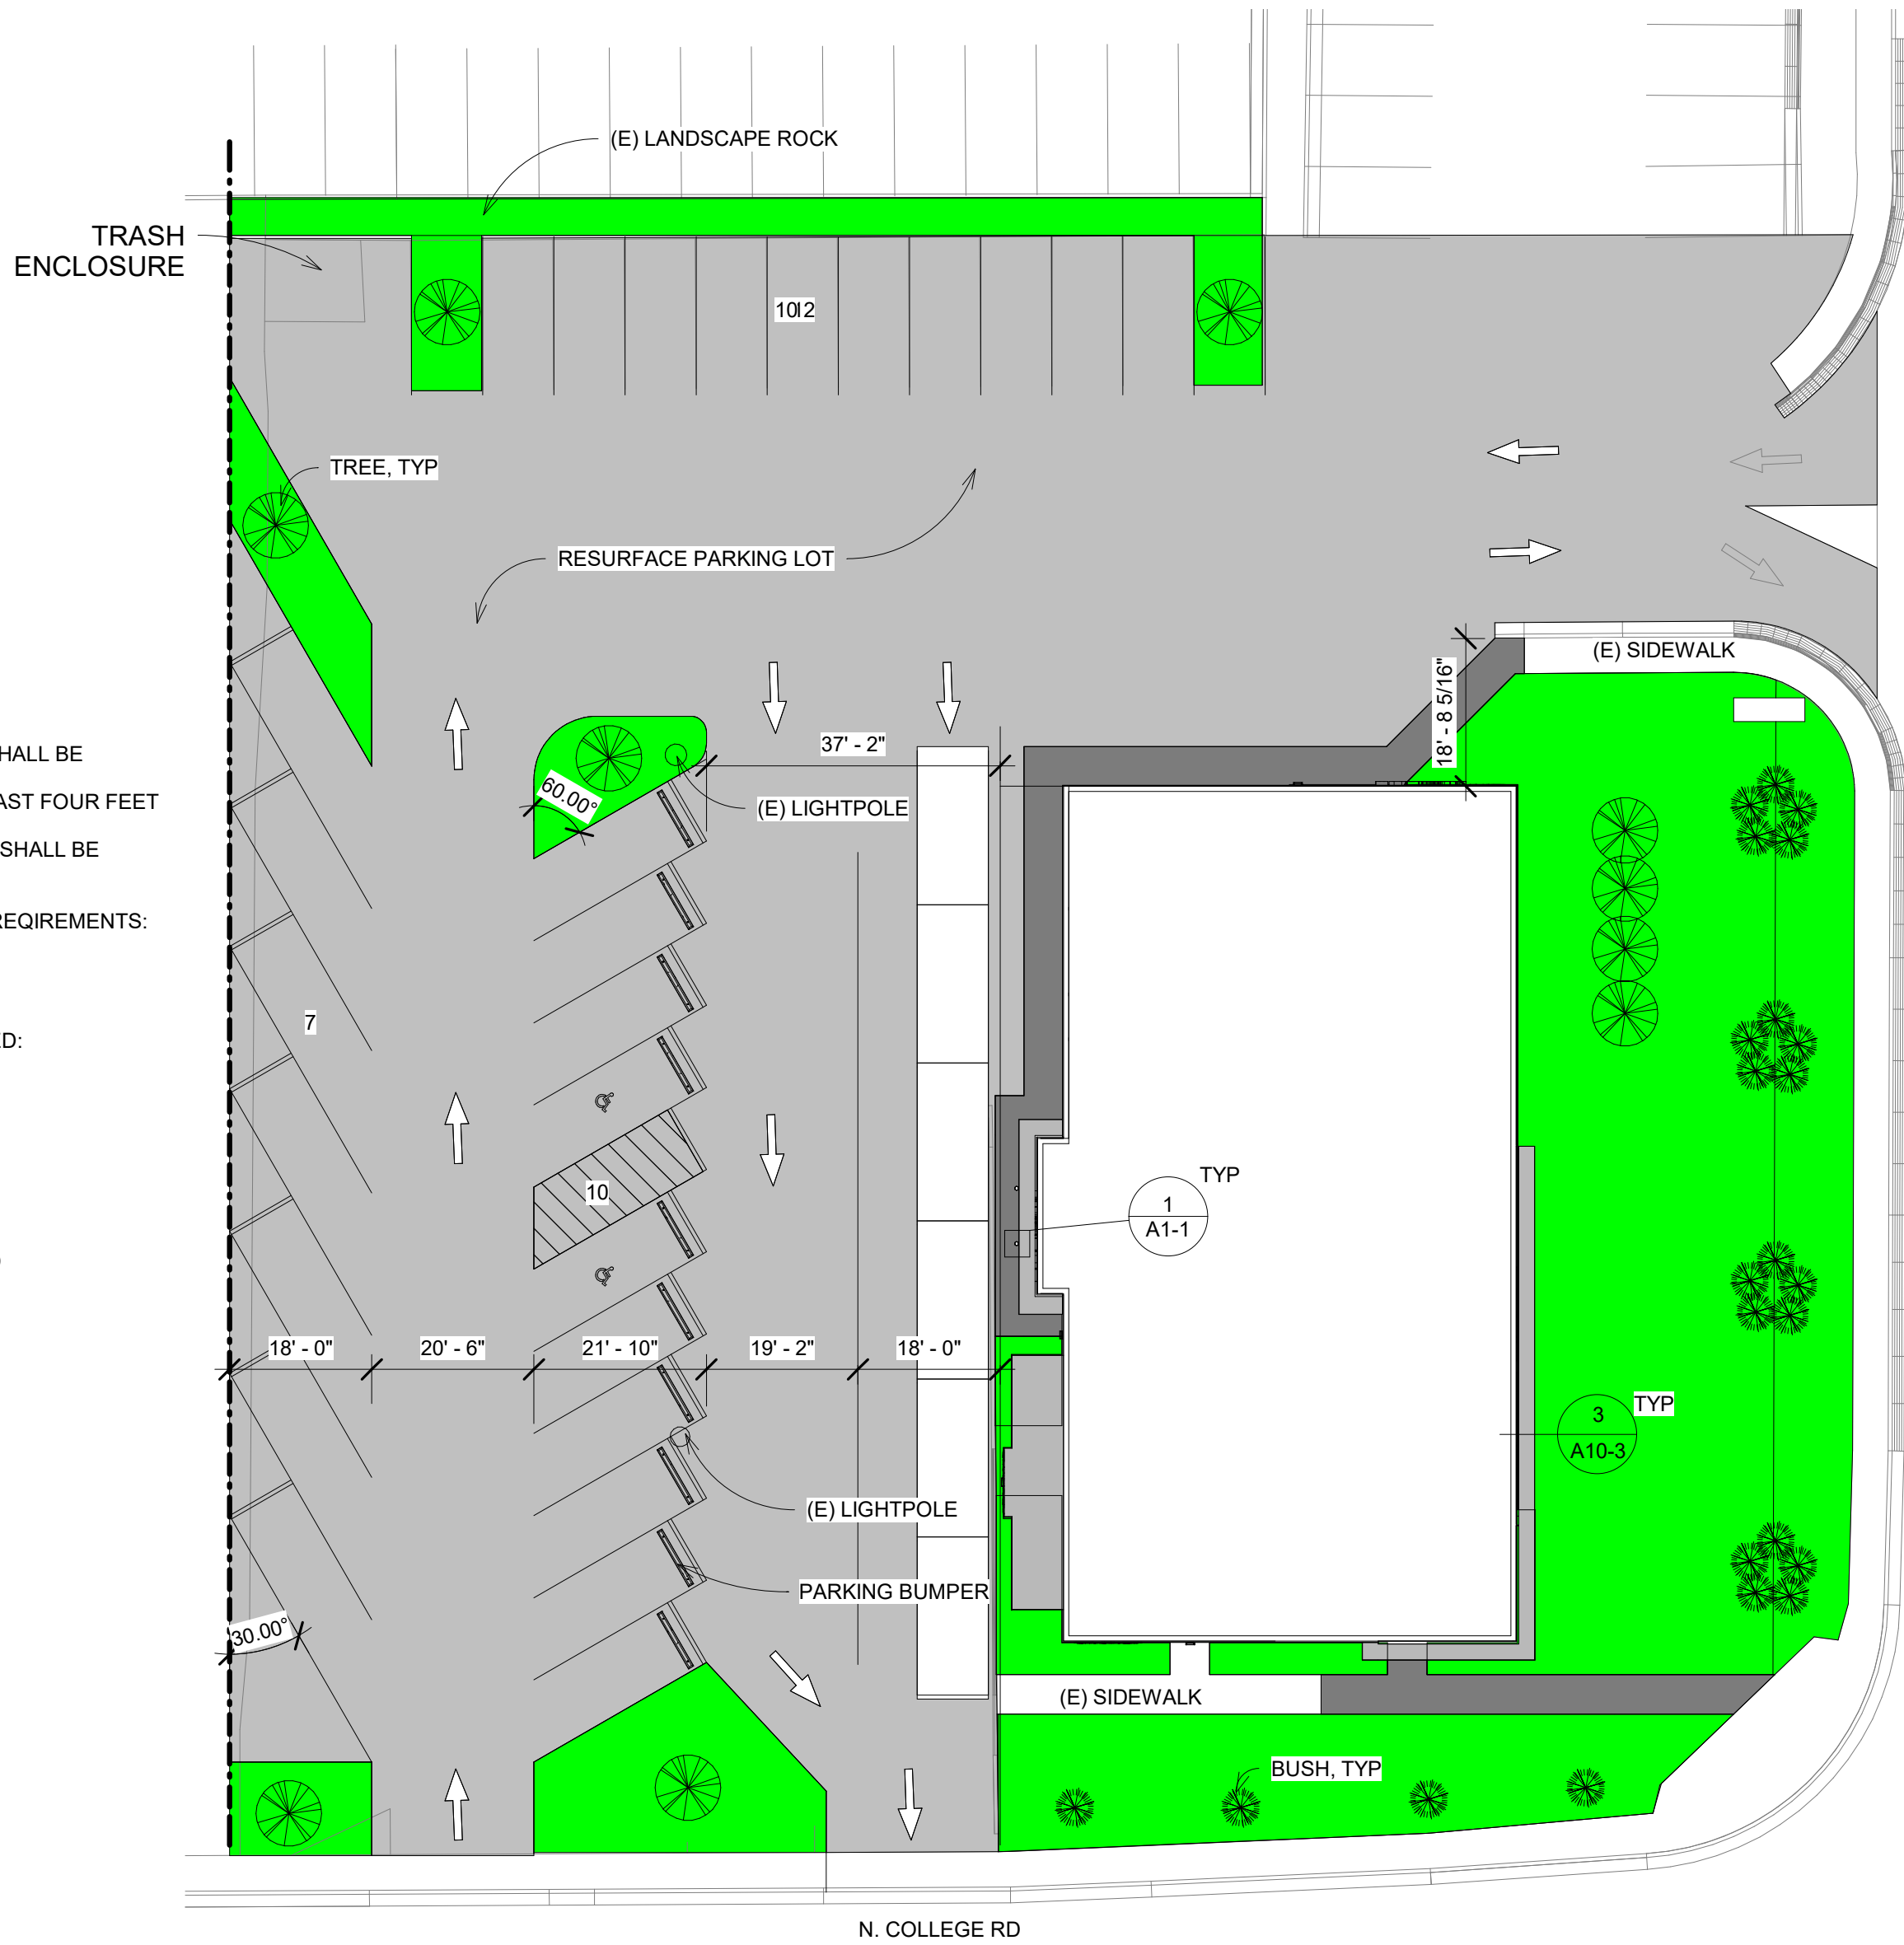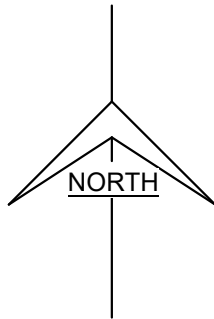

1 BOLLARD DETAIL
1/2" = 1'-0"

2 NEW SITE PLAN
1" = 20'-0"

4.19.22

DATE


A REMODEL FOR:
BLUE LAKES URGENT CARE
1309 BLUE LAKES BLVD TWIN FALLS, ID
NEW SITE PLAN

Laughlin Ricks Architecture
architecture/planning
134 3RD AVE. E. * Twin Falls, Idaho 83301
PHONE: (208) 736-8050


DATE: 4.19.22

NM RCR
Drawn Checked

A1-1

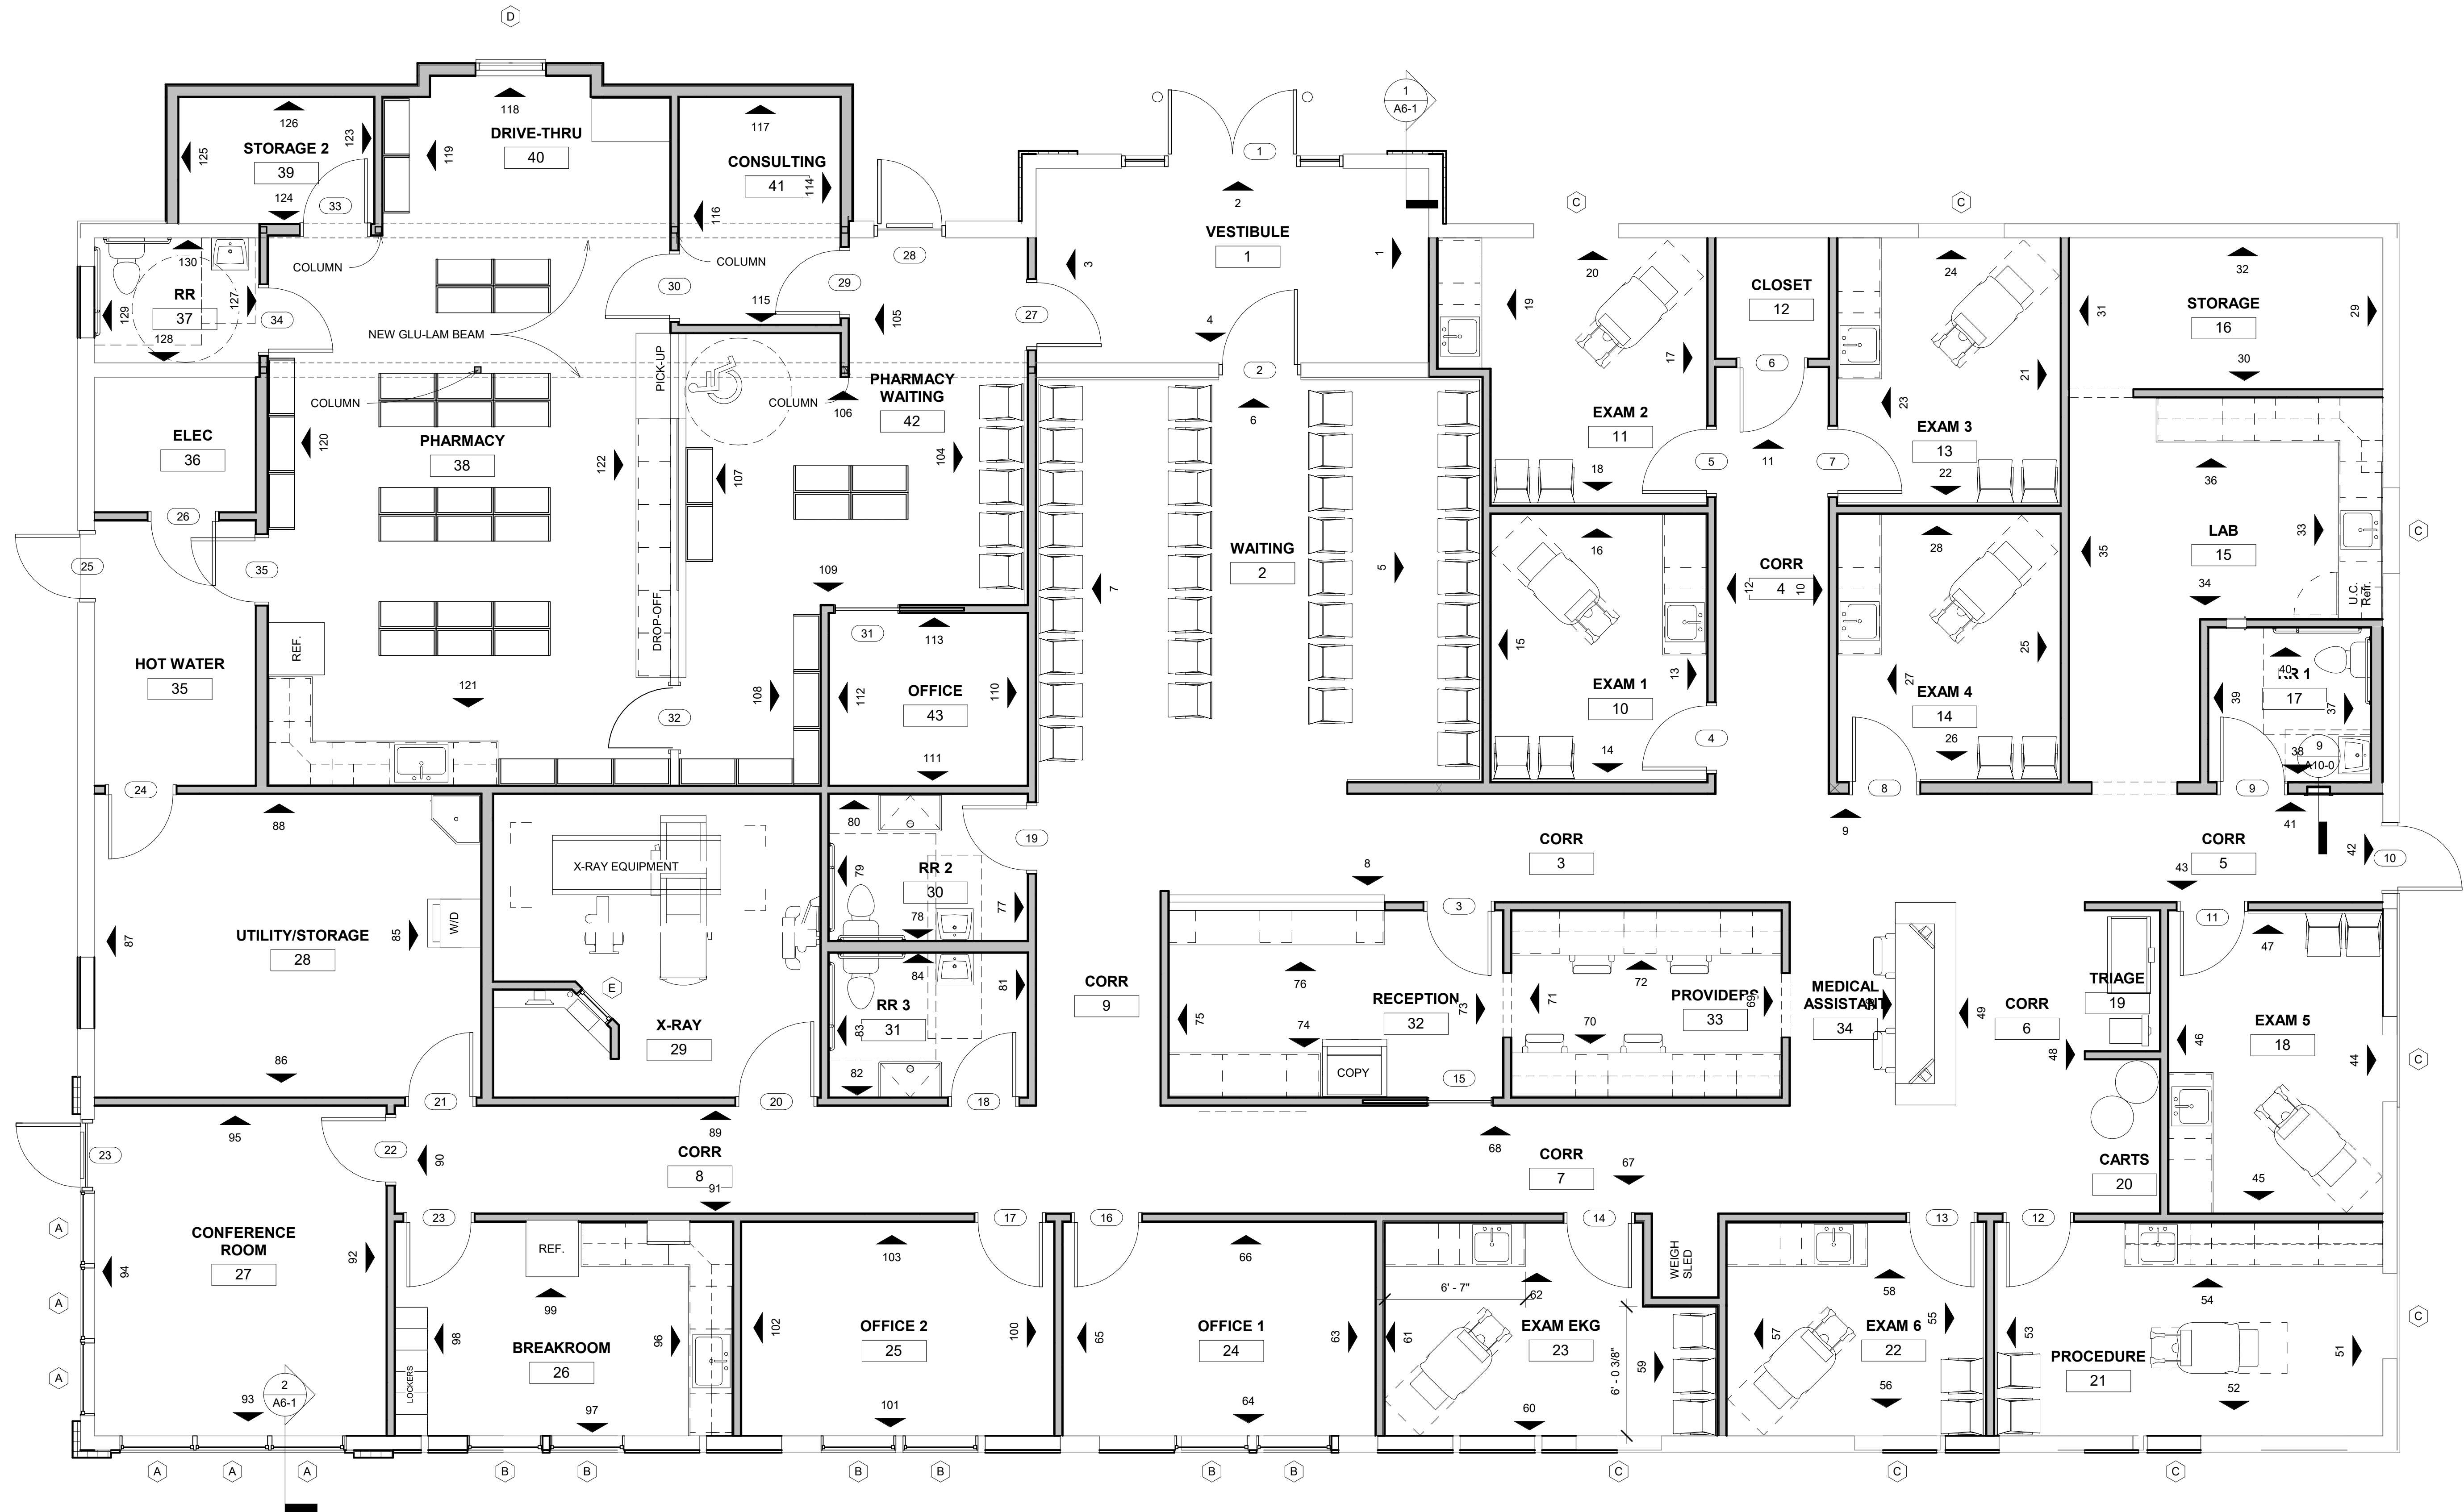

1 NEW FLOOR PLAN
1/4" = 1'-0"

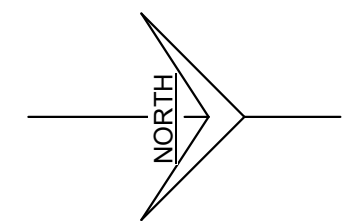

4.19.22

DATE


A REMODEL FOR:
BLUE LAKES URGENT CARE
1309 BLUE LAKES BLVD TWIN FALLS, ID
NEW FLOOR PLAN

Laughlin Ricks Architecture
architecture/planning
134 3RD AVE. E. * Twin Falls, Idaho 83301
PHONE: (208) 736-8050

DATE: 4.19.22

NM RCR
Drawn Checked

A2-1

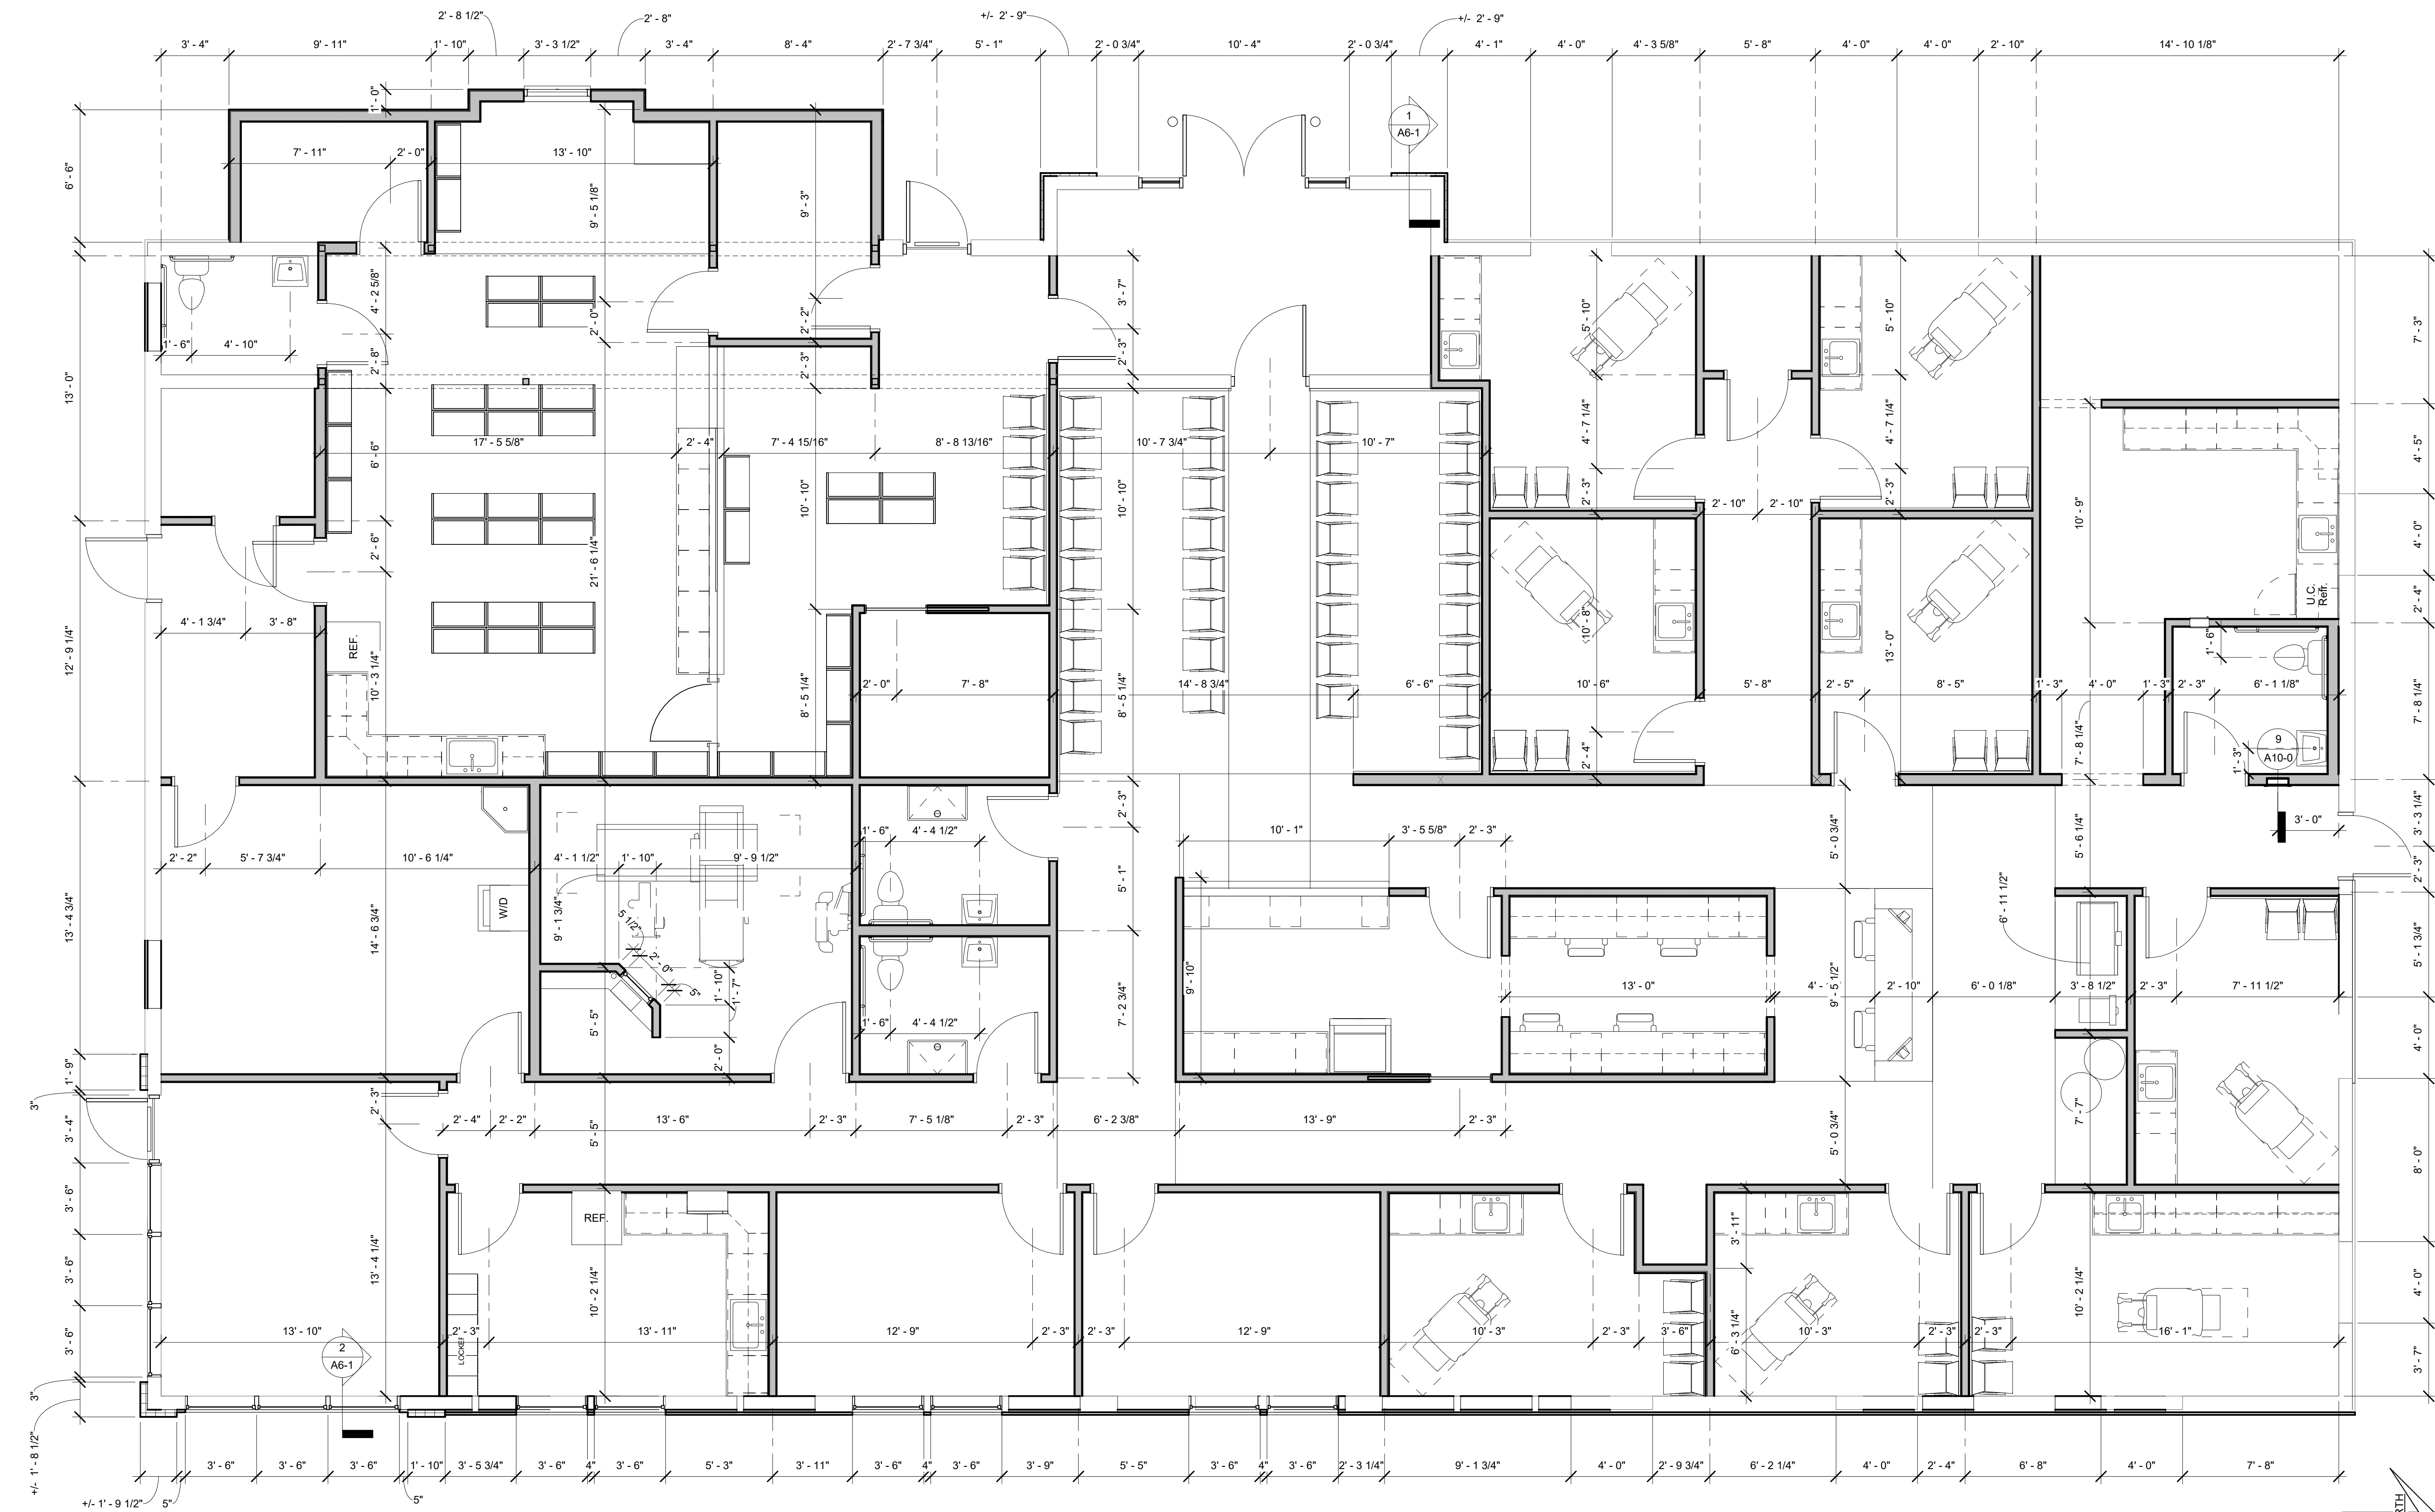

1 DIM NEW FLOOR PLAN
1/4" = 1'-0"

4.19.22

DATE


A REMODEL FOR:
BLUE LAKES URGENT CARE
1309 BLUE LAKES BLVD TWIN FALLS, ID
DIMENSION FLOOR PLAN

Laughlin Ricks Architecture
architecture/planning
134 3RD AVE. E. * Twin Falls, Idaho 83301
PHONE: (208) 736-8050


DATE: 4.19.22

NM RCR
Drawn Checked

A2-2

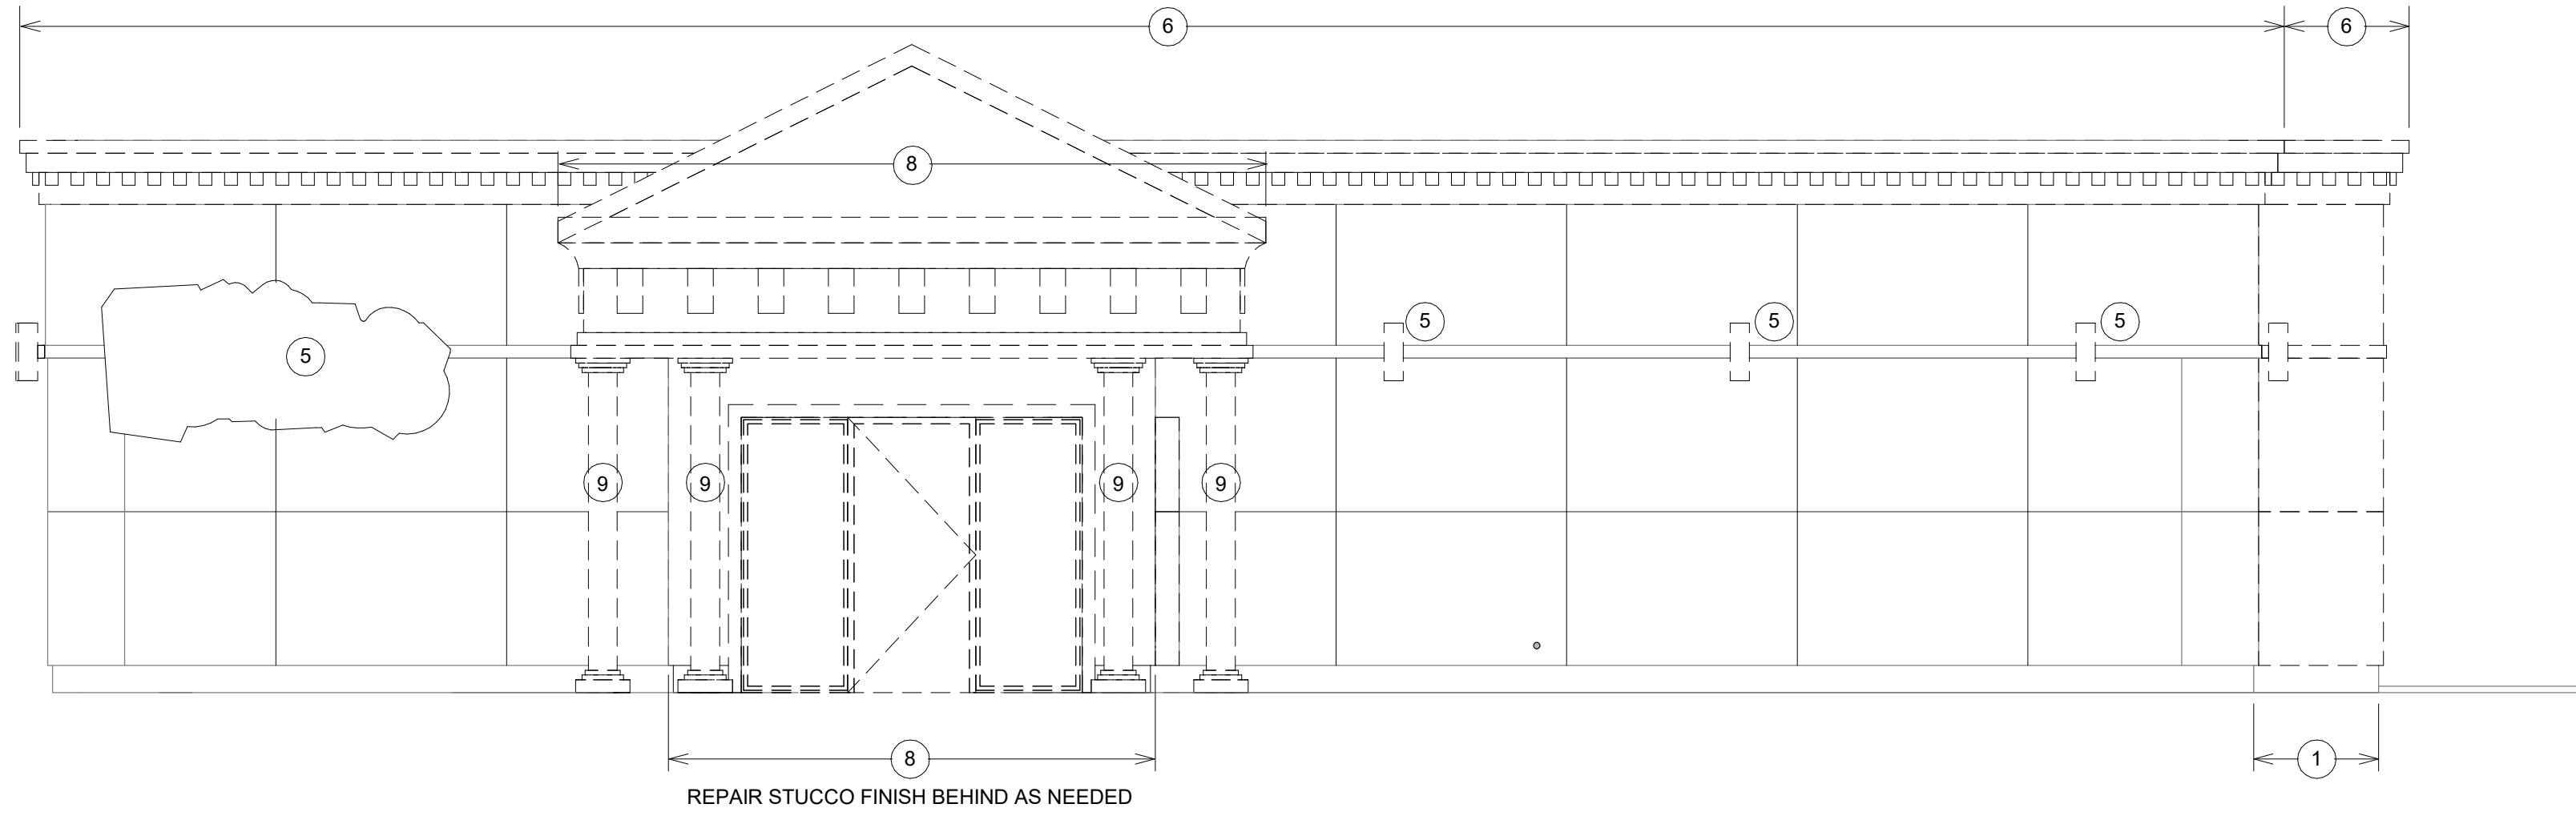

1 NORTH DEMO ELEVATION
1/4" = 1'-0"

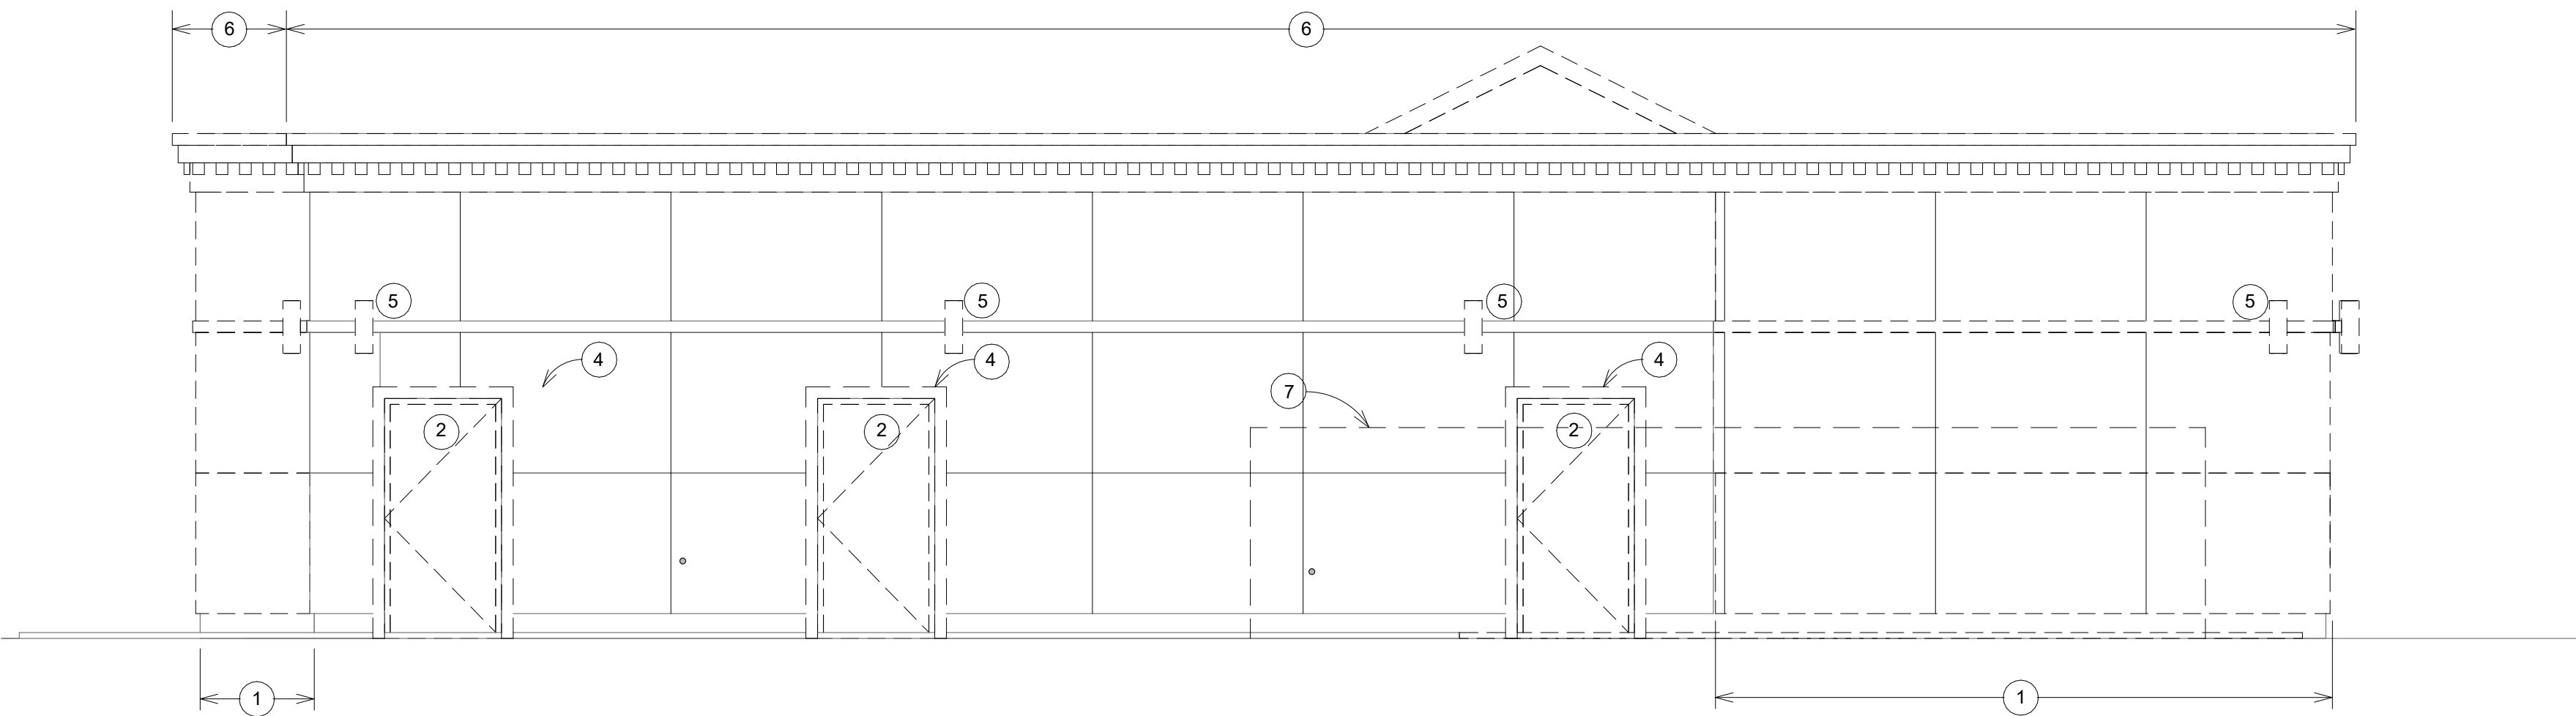

2 SOUTH DEMO ELEVATION
1/4" = 1'-0"

DEMOLITION NOTES:	
1	DEMO STUCCO SYSTEM ALONG THIS LENGTH TO PREPARE FOR NEW FRAMED WALLS (SEE NEW ELEVATIONS)
2	DEMO DOOR SYSTEM IN ITS ENTIRETY
3	DEMO WINDOW SYSTEM IN ITS ENTIRETY
4	DEMO TRIM IN ITS ENTIRETY
5	DEMO LIGHT FIXTURE
6	DEMO ALL DENTAL DETAILING ALONG THIS LENGTH
7	DEMO COURTYARD IN ITS ENTIRETY
8	DEMO ENTIRE FRONT VESTIBULE AND ITS ROOF
9	DEMO COLUMN IN ITS ENTIRETY
10	DEMO FAKE SHUTTER
11	DEMO FLOWER BOX

DATE: 4.19.22


DATE: _____

A REMODEL FOR:
BLUE LAKES URGENT CARE
1309 BLUE LAKES BLVD TWIN FALLS, ID
DEMO EXTERIOR ELEVATIONS


Laughlin Ricks Architecture
architecture/planning
134 3RD AVE. E. * Twin Falls, Idaho 83301
PHONE: (208) 736-8050

DATE: 4.19.22
NM RCR
Drawn Checked


A3-0

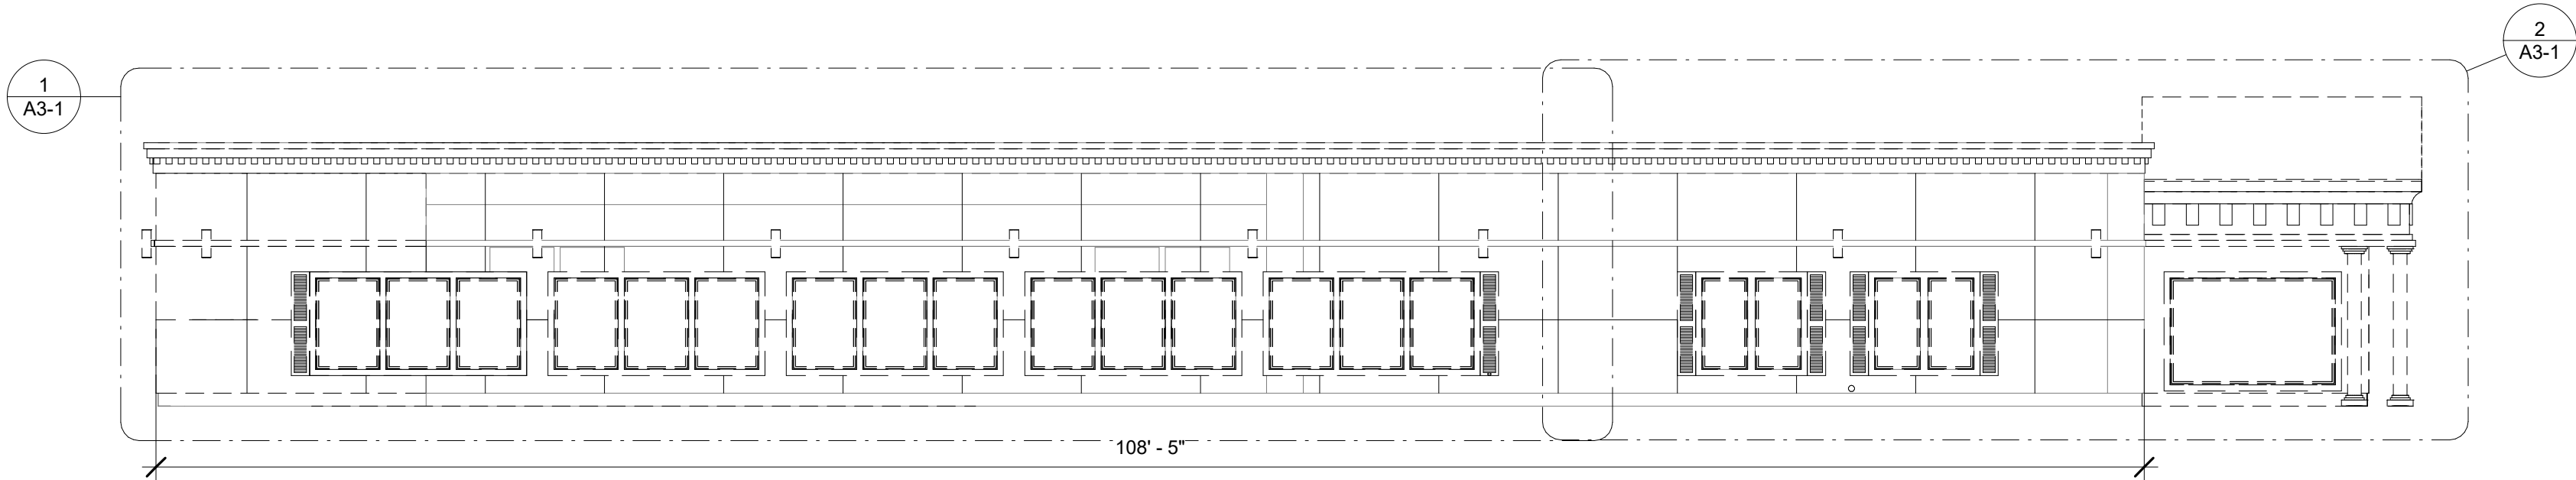

3 EAST DEMO ELEVATION
1/8" = 1'-0"

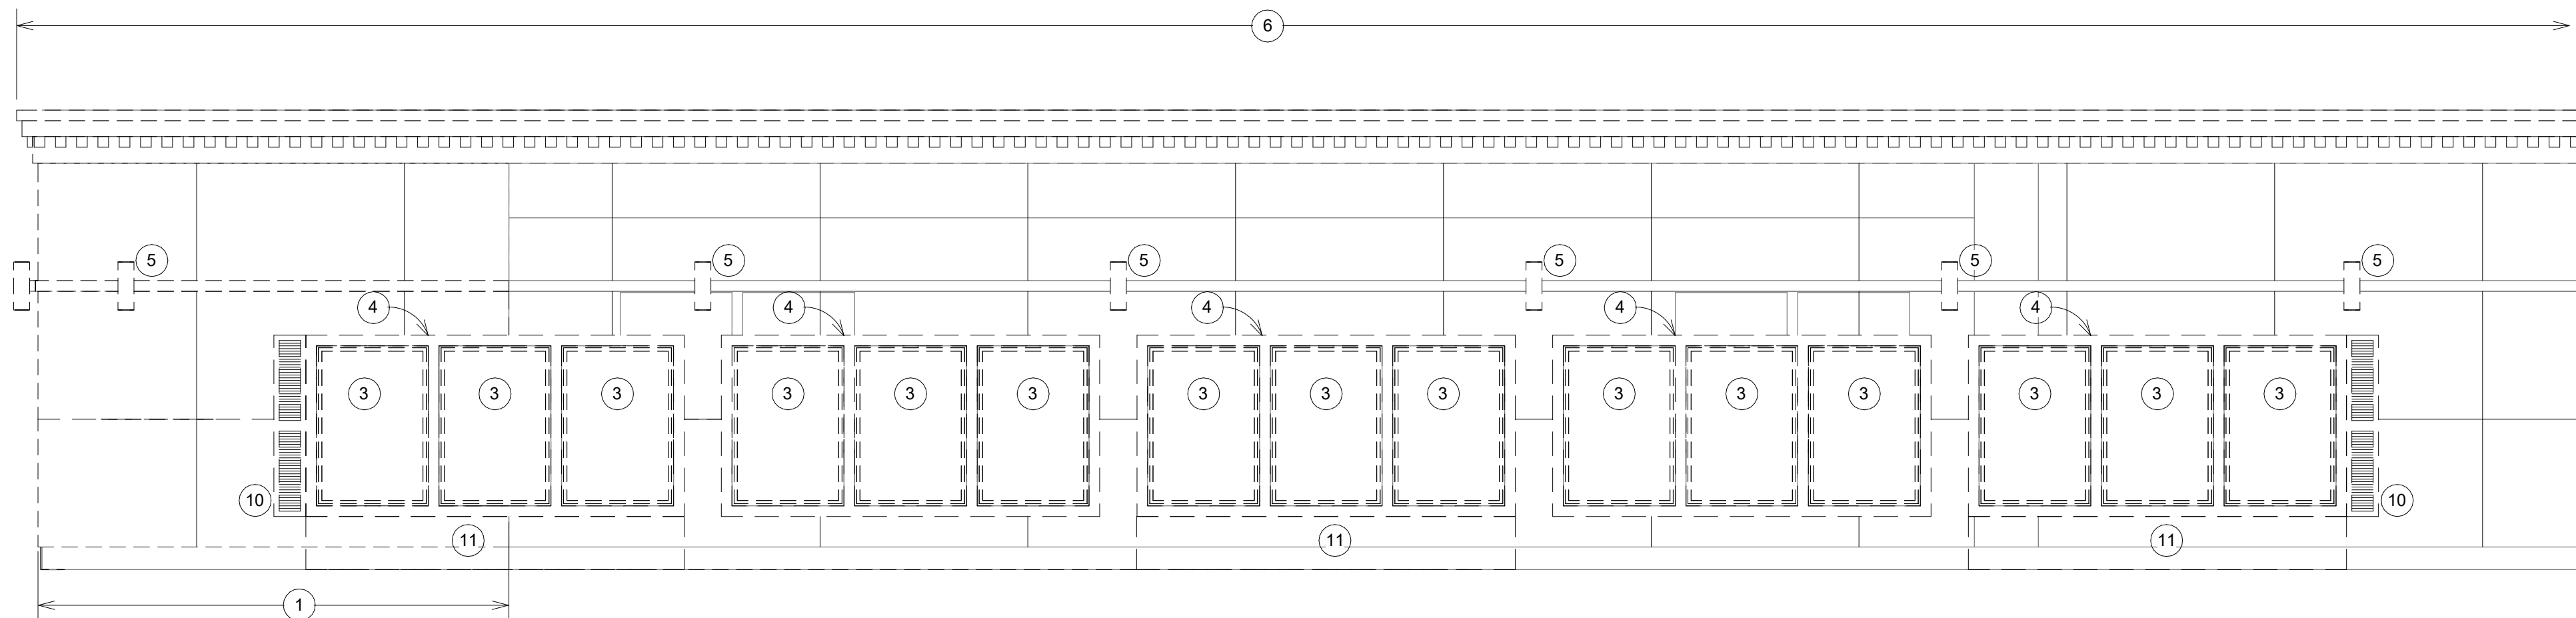

1 EAST DEMO ELEVATION - Callout 1
1/4" = 1'-0"

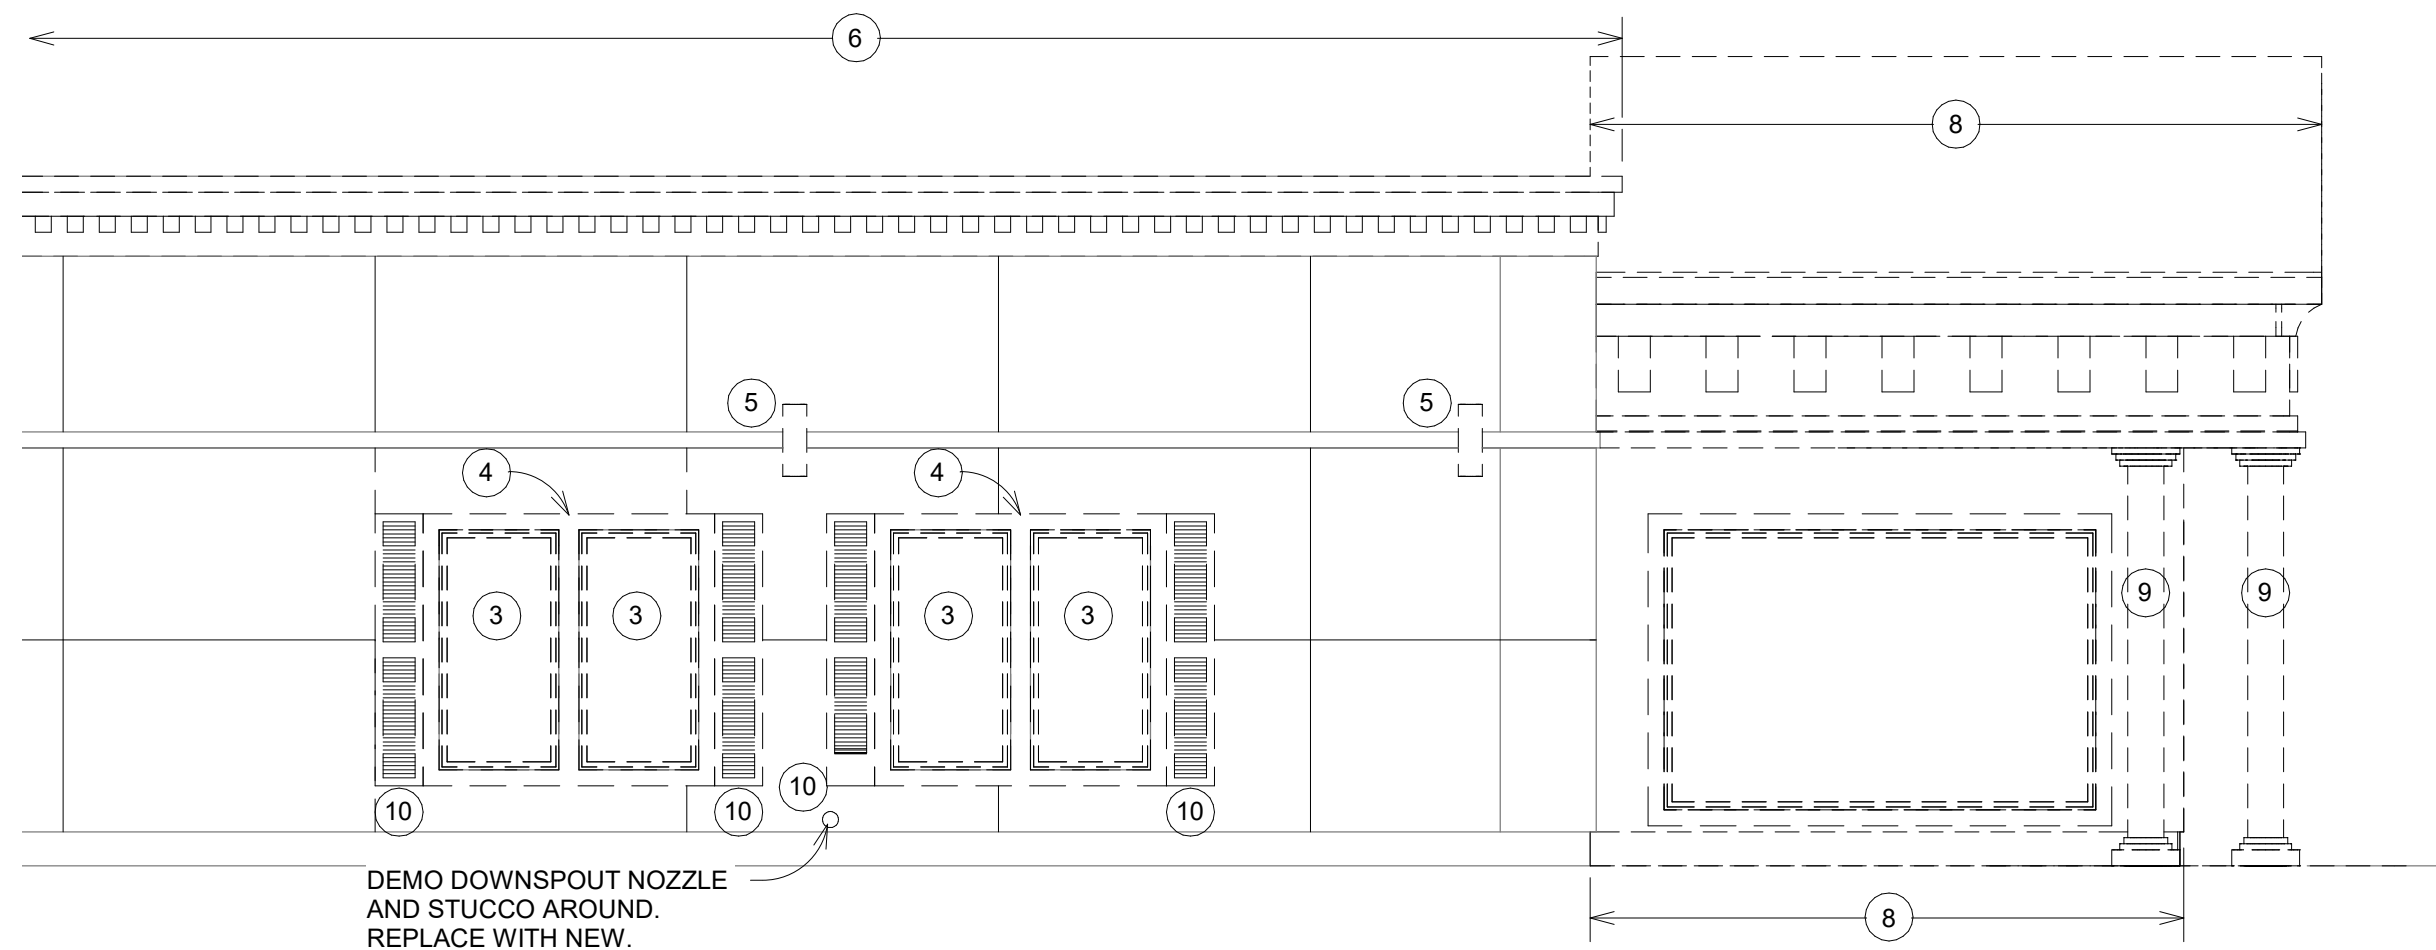

2 EAST DEMO ELEVATION - Callout 2
1/4" = 1'-0"


DEMOLITION NOTES:	
1	DEMO STUCCO SYSTEM ALONG THIS LENGTH TO PREPARE FOR NEW FRAMED WALLS (SEE NEW ELEVATIONS)
2	DEMO DOOR SYSTEM IN ITS ENTIRETY
3	DEMO WINDOW SYSTEM IN ITS ENTIRETY
4	DEMO TRIM IN ITS ENTIRETY
5	DEMO LIGHT FIXTURE
6	DEMO ALL DENTAL DETAILING ALONG THIS LENGTH
7	DEMO COURTYARD IN ITS ENTIRETY
8	DEMO ENTIRE FRONT VESTIBULE AND ITS ROOF
9	DEMO COLUMN IN ITS ENTIRETY
10	DEMO FAKE SHUTTER
11	DEMO FLOWER BOX

A REMODEL FOR:
BLUE LAKES URGENT CARE
1309 BLUE BLAKES BLVD TWIN FALLS, ID
DEMO EXTERIOR ELEVATIONS


Laughlin Ricks Architecture
architecture/planning
134 3RD AVE. E. * Twin Falls, Idaho 83301
PHONE: (208) 736-8050

DATE: 4.19.22
NM RCR
Drawn Checked


A3-1

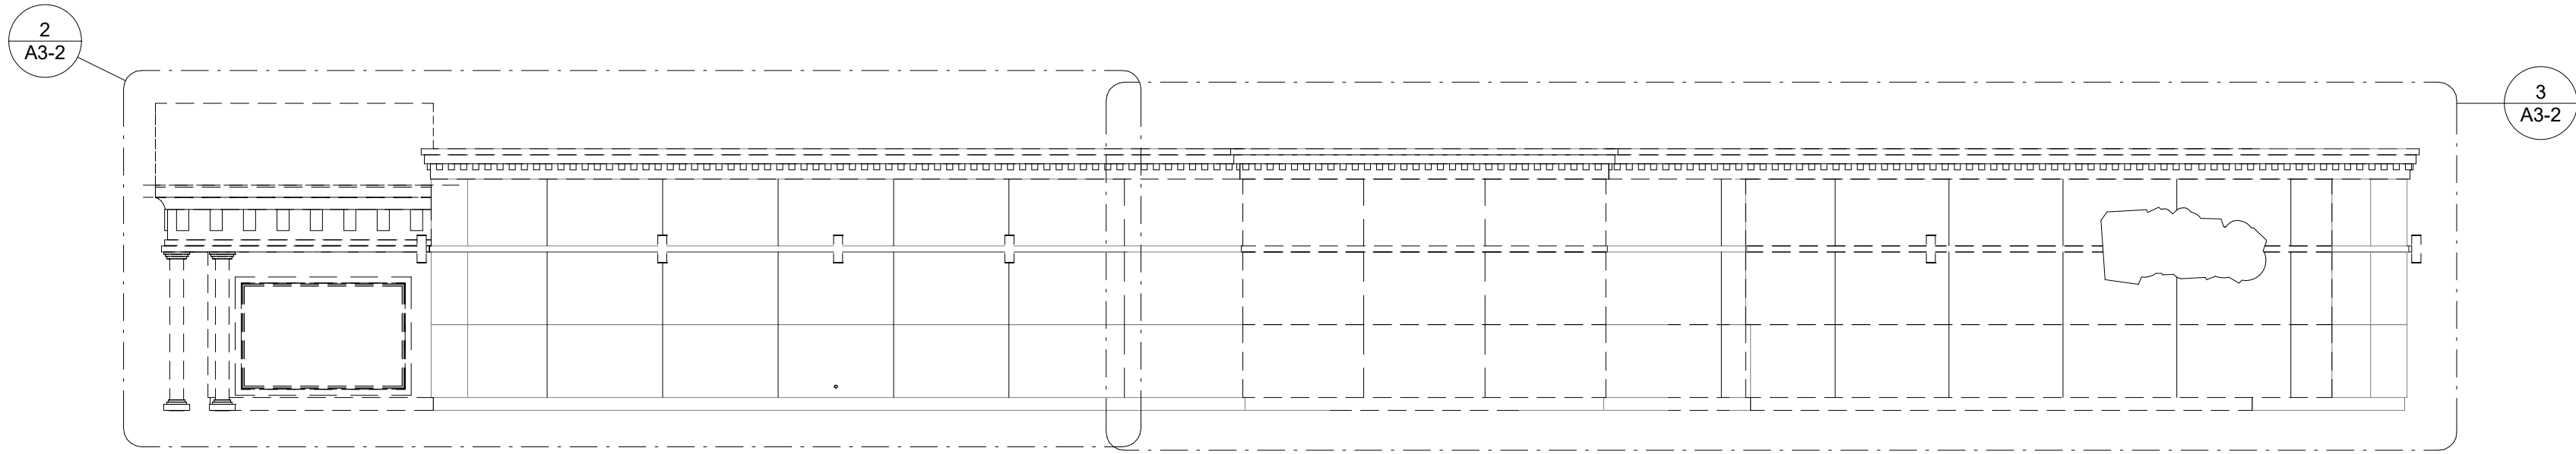

1 WEST DEMO ELEVATION
1/8" = 1'-0"

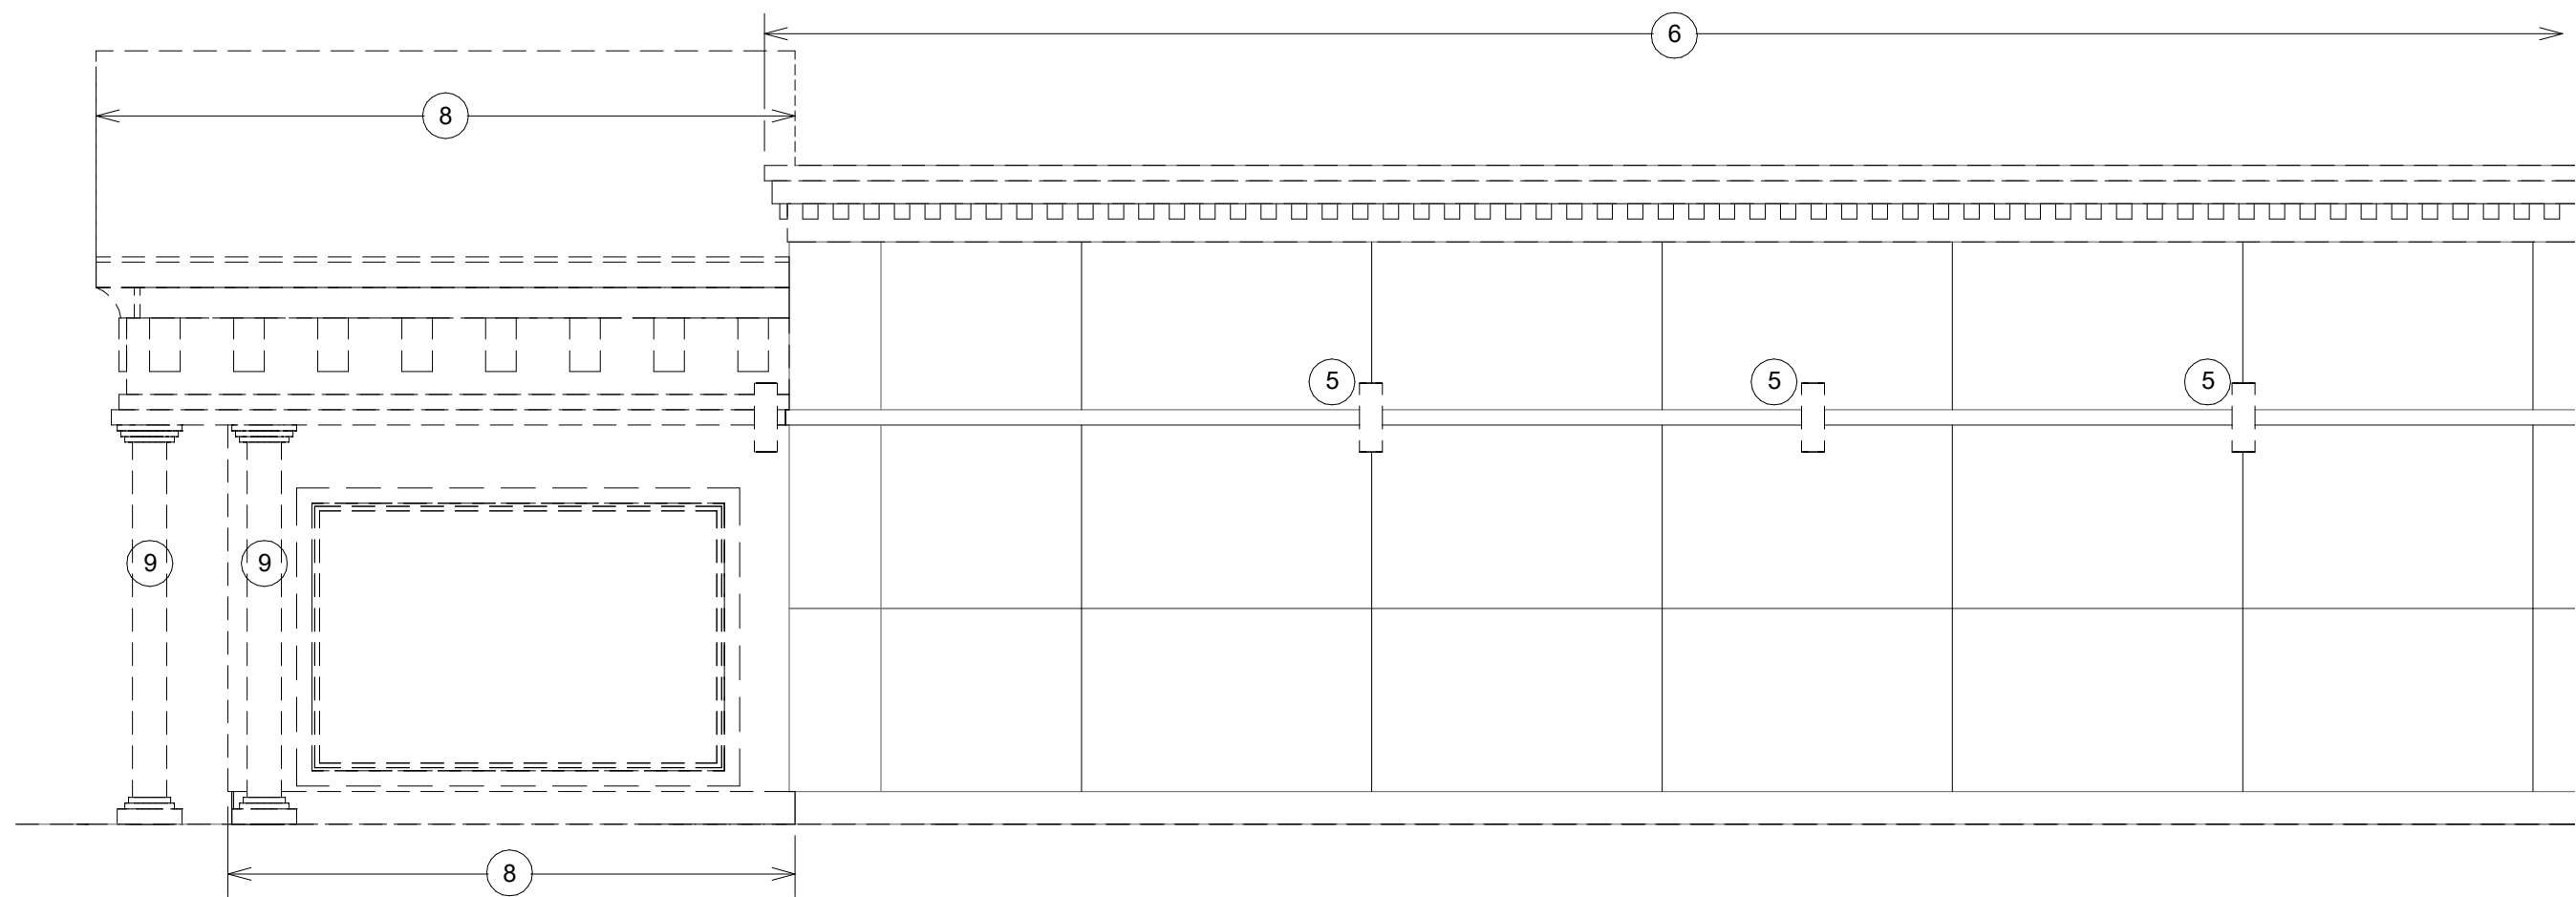

2 WEST DEMO ELEVATION - Callout 1
1/4" = 1'-0"

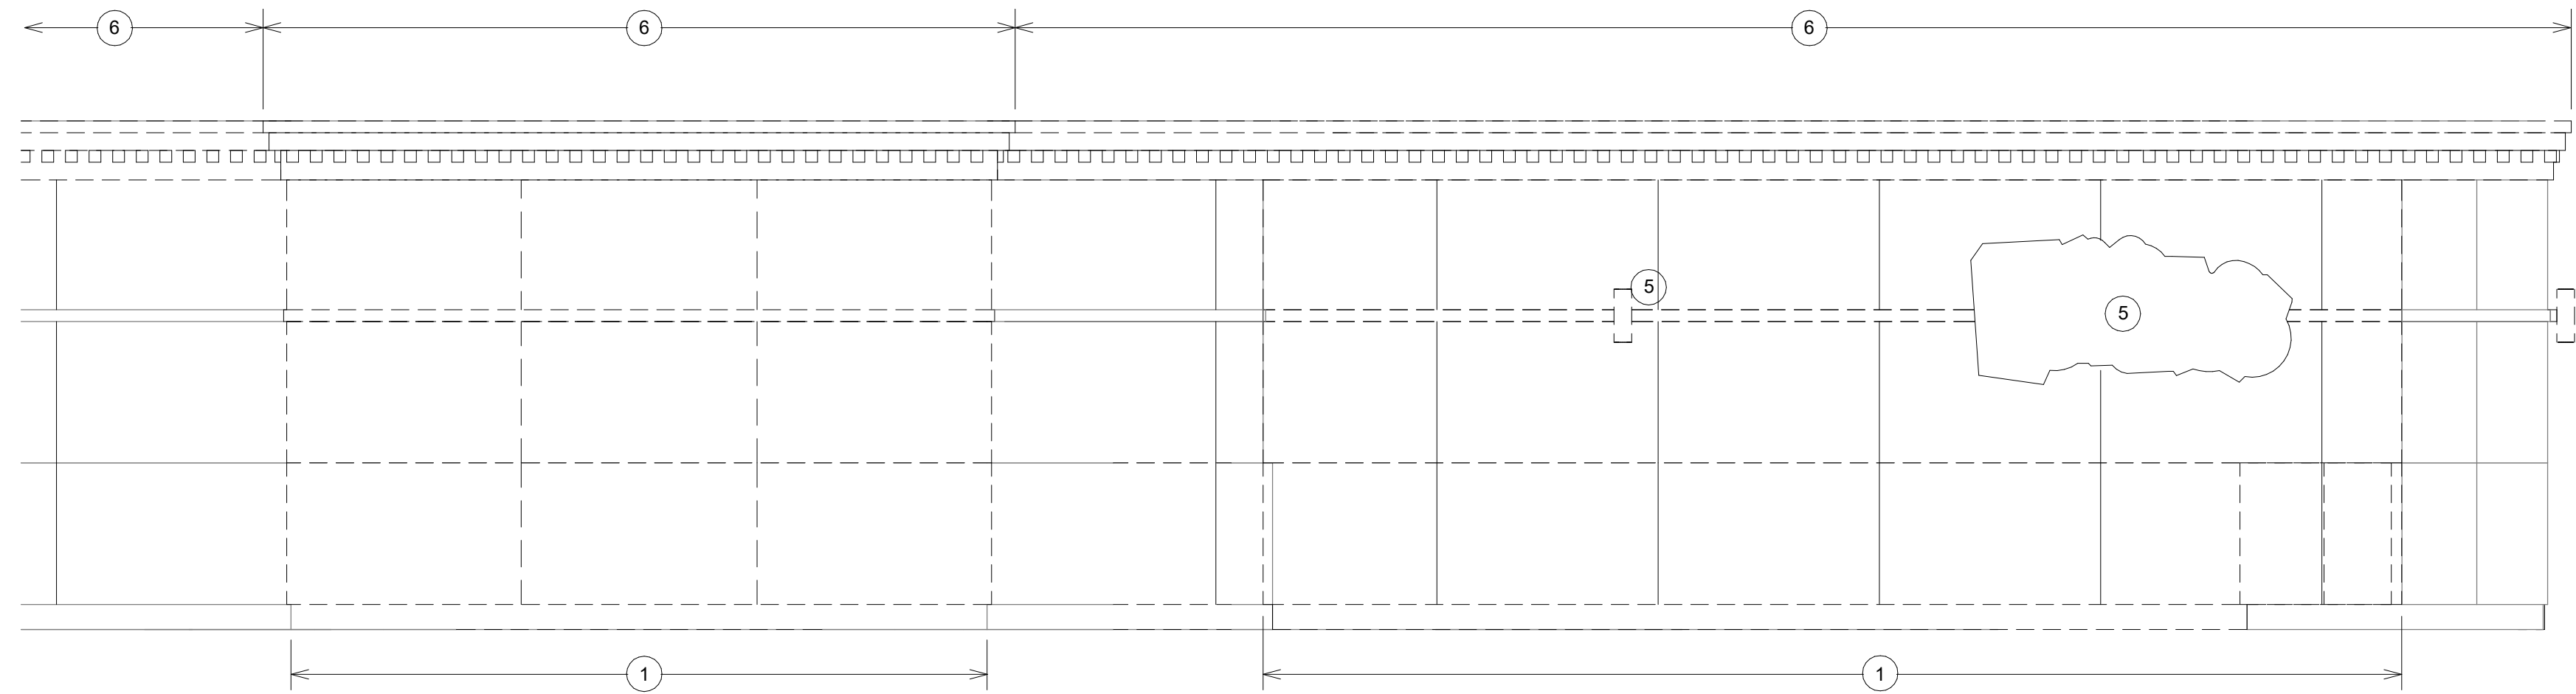

3 WEST DEMO ELEVATION - Callout 2
1/4" = 1'-0"


DEMOLITION NOTES:	
1	DEMO STUCCO SYSTEM ALONG THIS LENGTH TO PREPARE FOR NEW FRAMED WALLS (SEE NEW ELEVATIONS)
2	DEMO DOOR SYSTEM IN ITS ENTIRETY
3	DEMO WINDOW SYSTEM IN ITS ENTIRETY
4	DEMO TRIM IN ITS ENTIRETY
5	DEMO LIGHT FIXTURE
6	DEMO ALL DENTAL DETAILING ALONG THIS LENGTH
7	DEMO COURTYARD IN ITS ENTIRETY
8	DEMO ENTIRE FRONT VESTIBULE AND ITS ROOF
9	DEMO COLUMN IN ITS ENTIRETY
10	DEMO FAKE SHUTTER
11	DEMO FLOWER BOX

A REMODEL FOR:
BLUE LAKES URGENT CARE
1309 BLUE BLAKES BLVD TWIN FALLS, ID
DEMO EXTERIOR ELEVATIONS


Laughlin Ricks Architecture
architecture/planning
134 3RD AVE. E. * Twin Falls, Idaho 83301
PHONE: (208) 736-8050

DATE: 4.19.22
NM RCR
Drawn Checked

A3-2

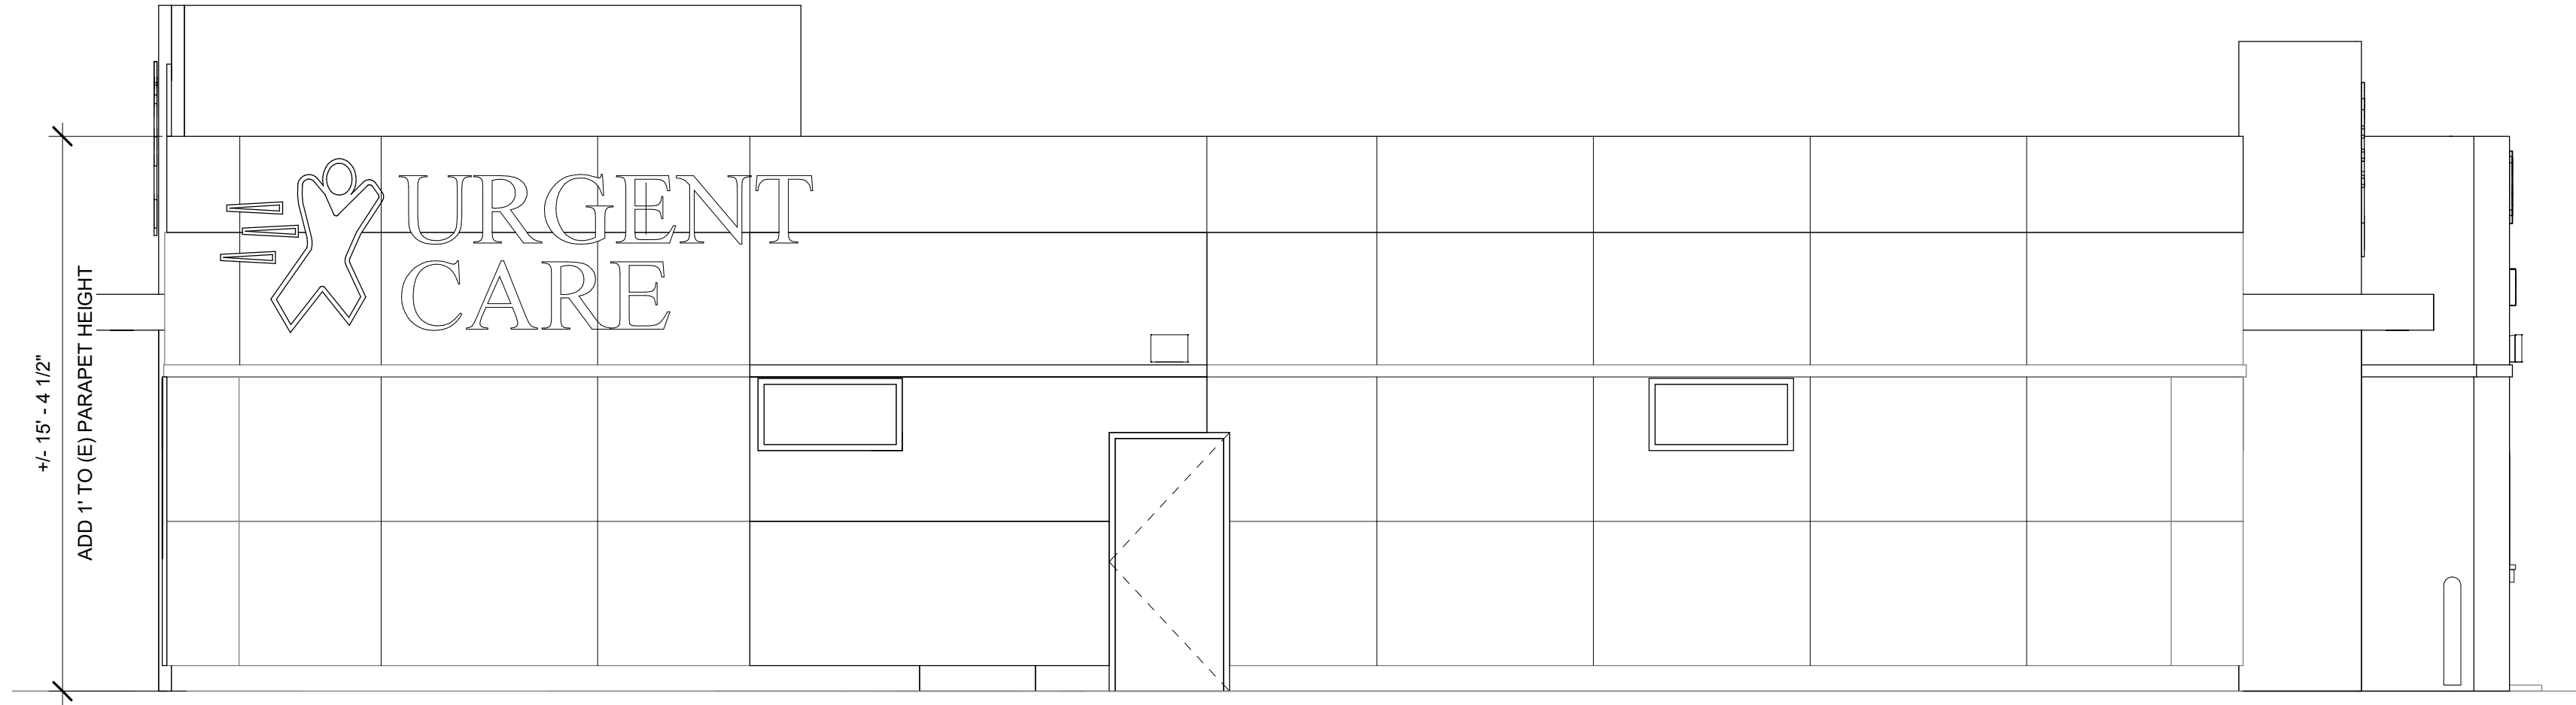

① NEW NORTH
1/4" = 1'-0"

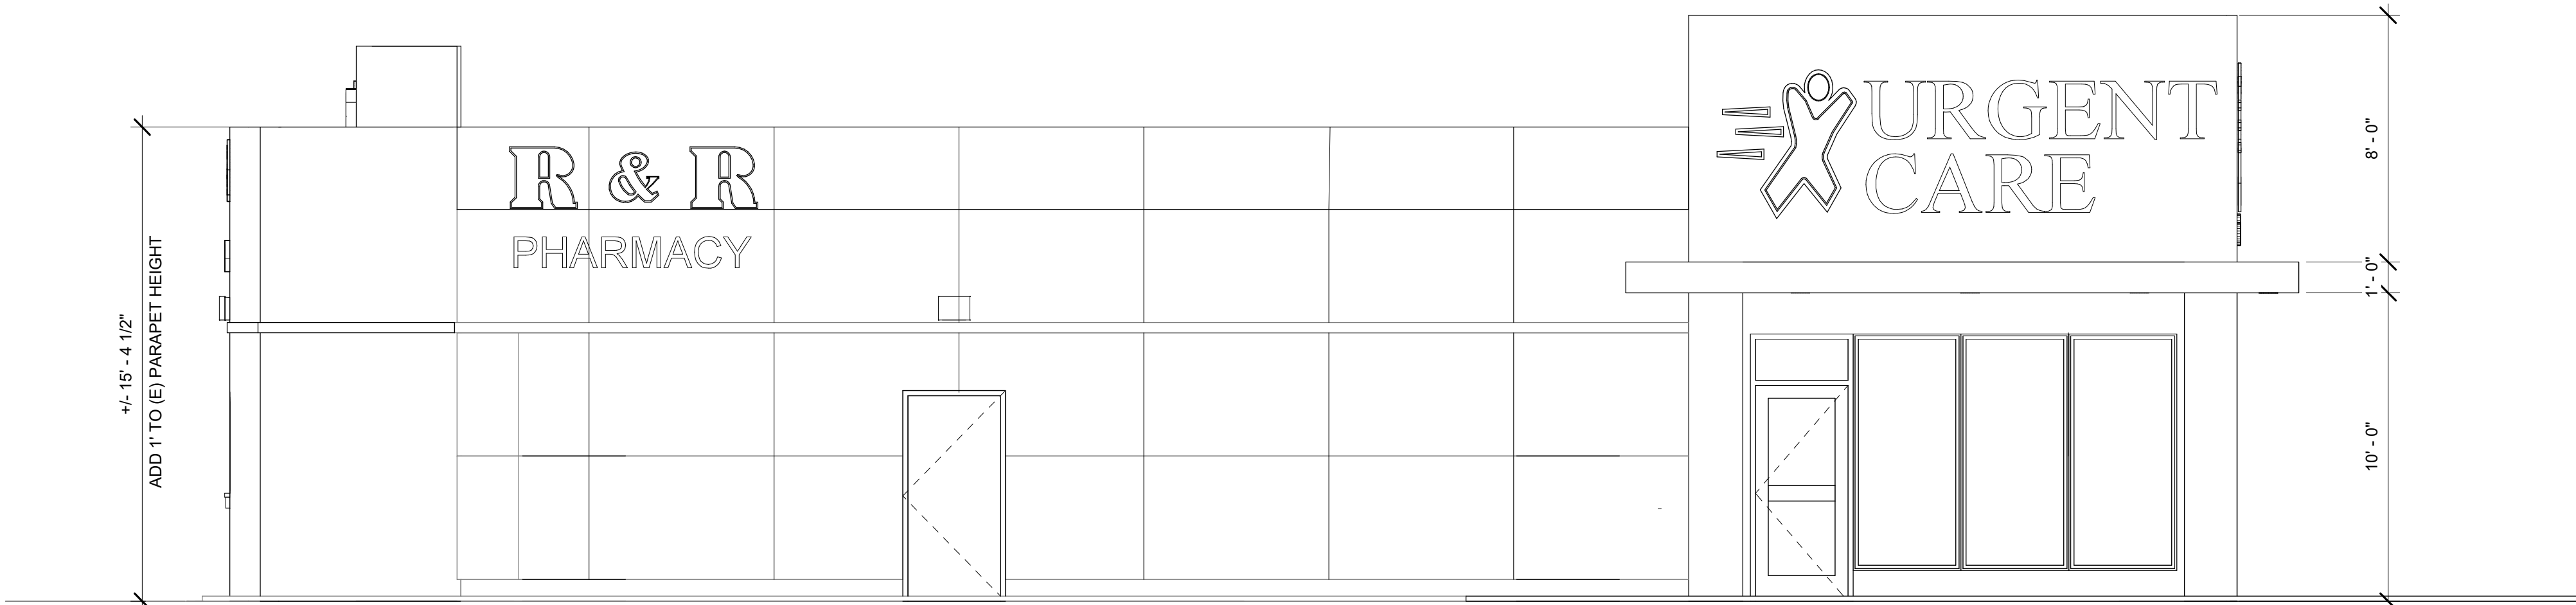

② NEW SOUTH
1/4" = 1'-0"


DATE: 4.19.22
NM RCR
Drawn Checked

A3-3


Laughlin Ricks Architecture
architecture/planning
134 3RD AVE. E. * Twin Falls, Idaho 83301
PHONE: (208) 736-8050

A REMODEL FOR:
BLUE LAKES URGENT CARE
1309 BLUE LAKES BLVD TWIN FALLS, ID
NEW EXTERIOR ELEVATIONS


DATE: 4.19.22
NM RCR
Drawn Checked

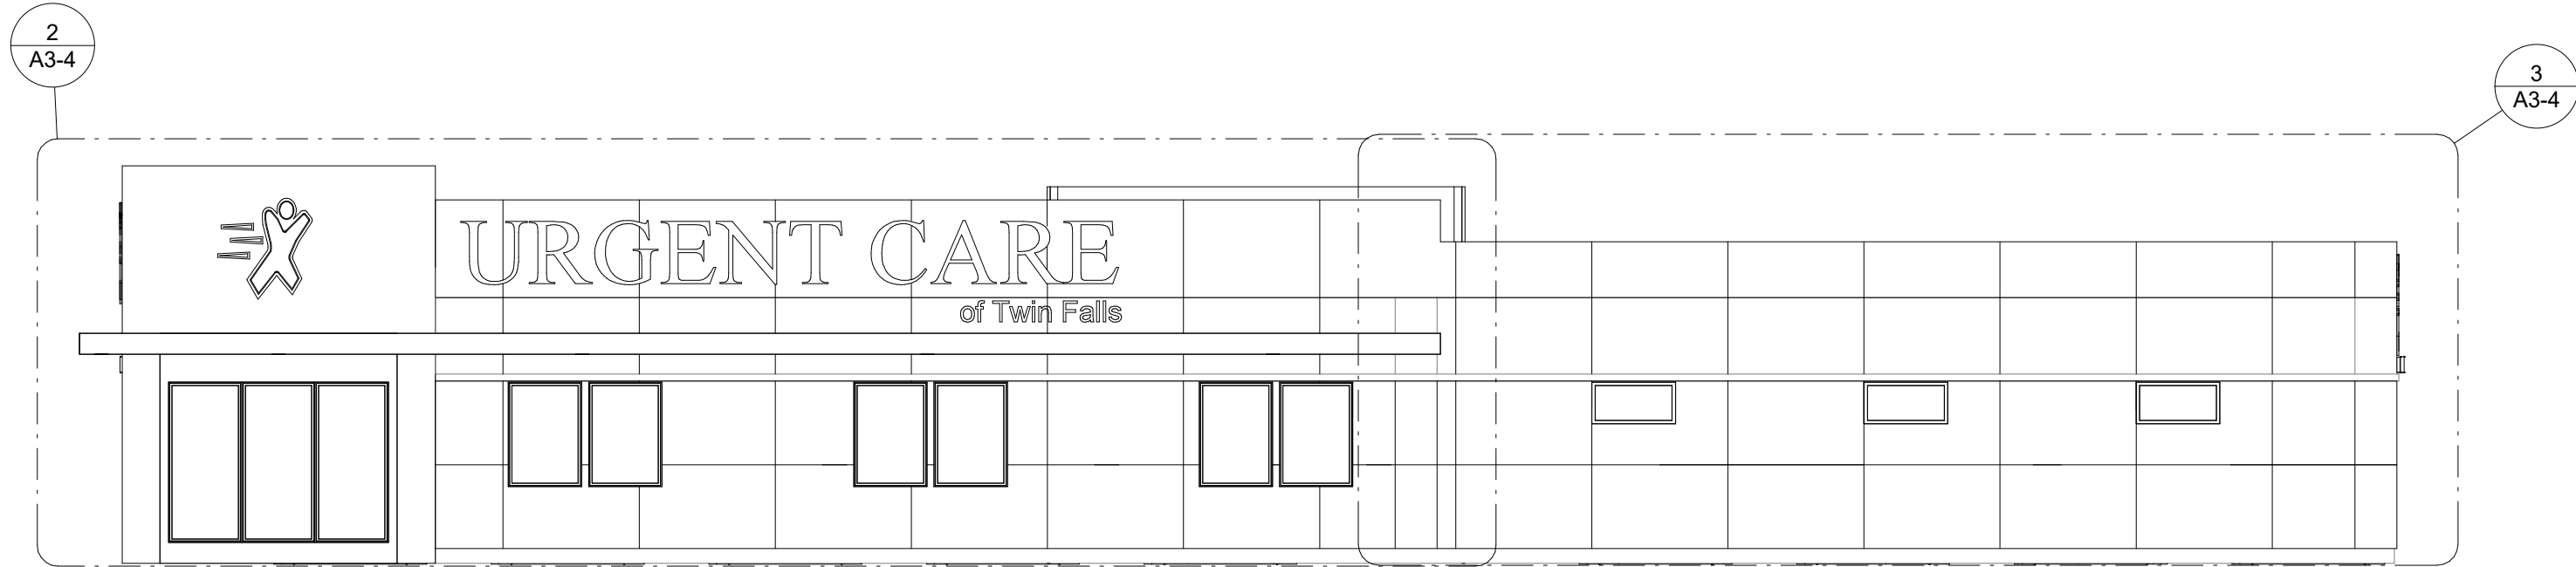

1 NEW EAST
1/8" = 1'-0"

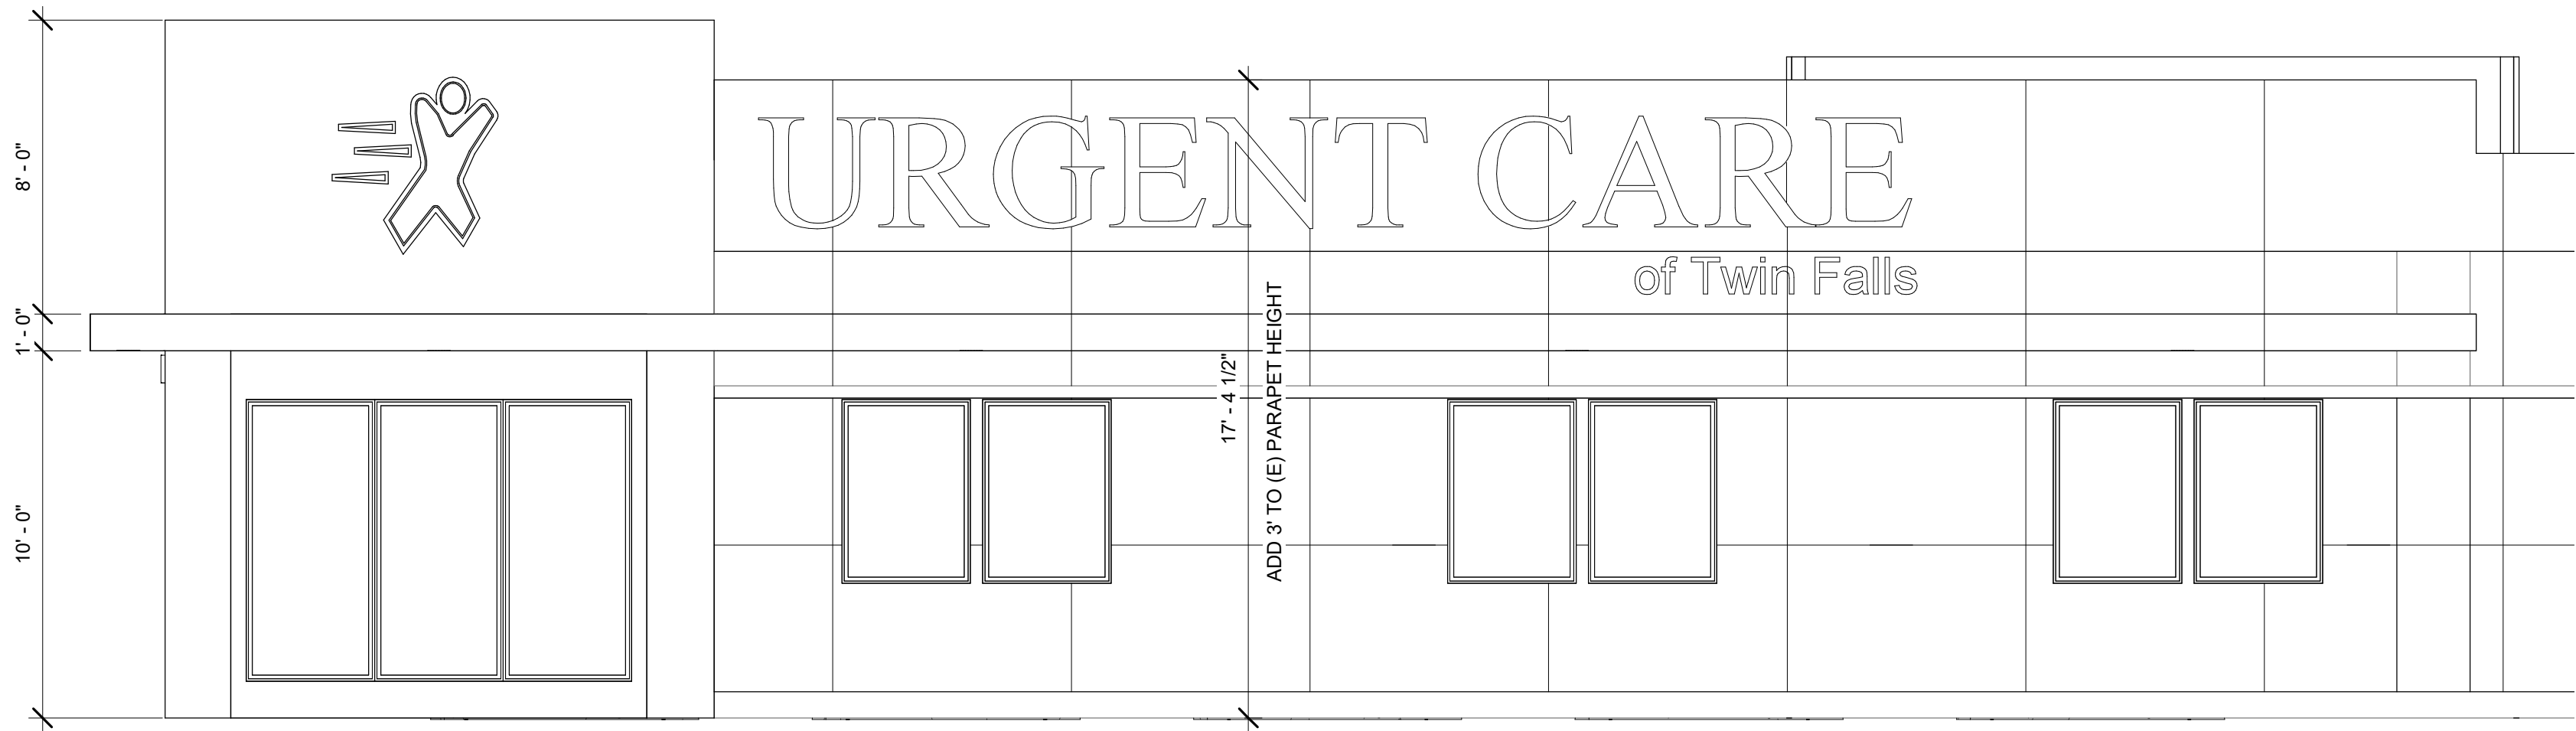

2 NEW EAST - Callout 1
1/4" = 1'-0"

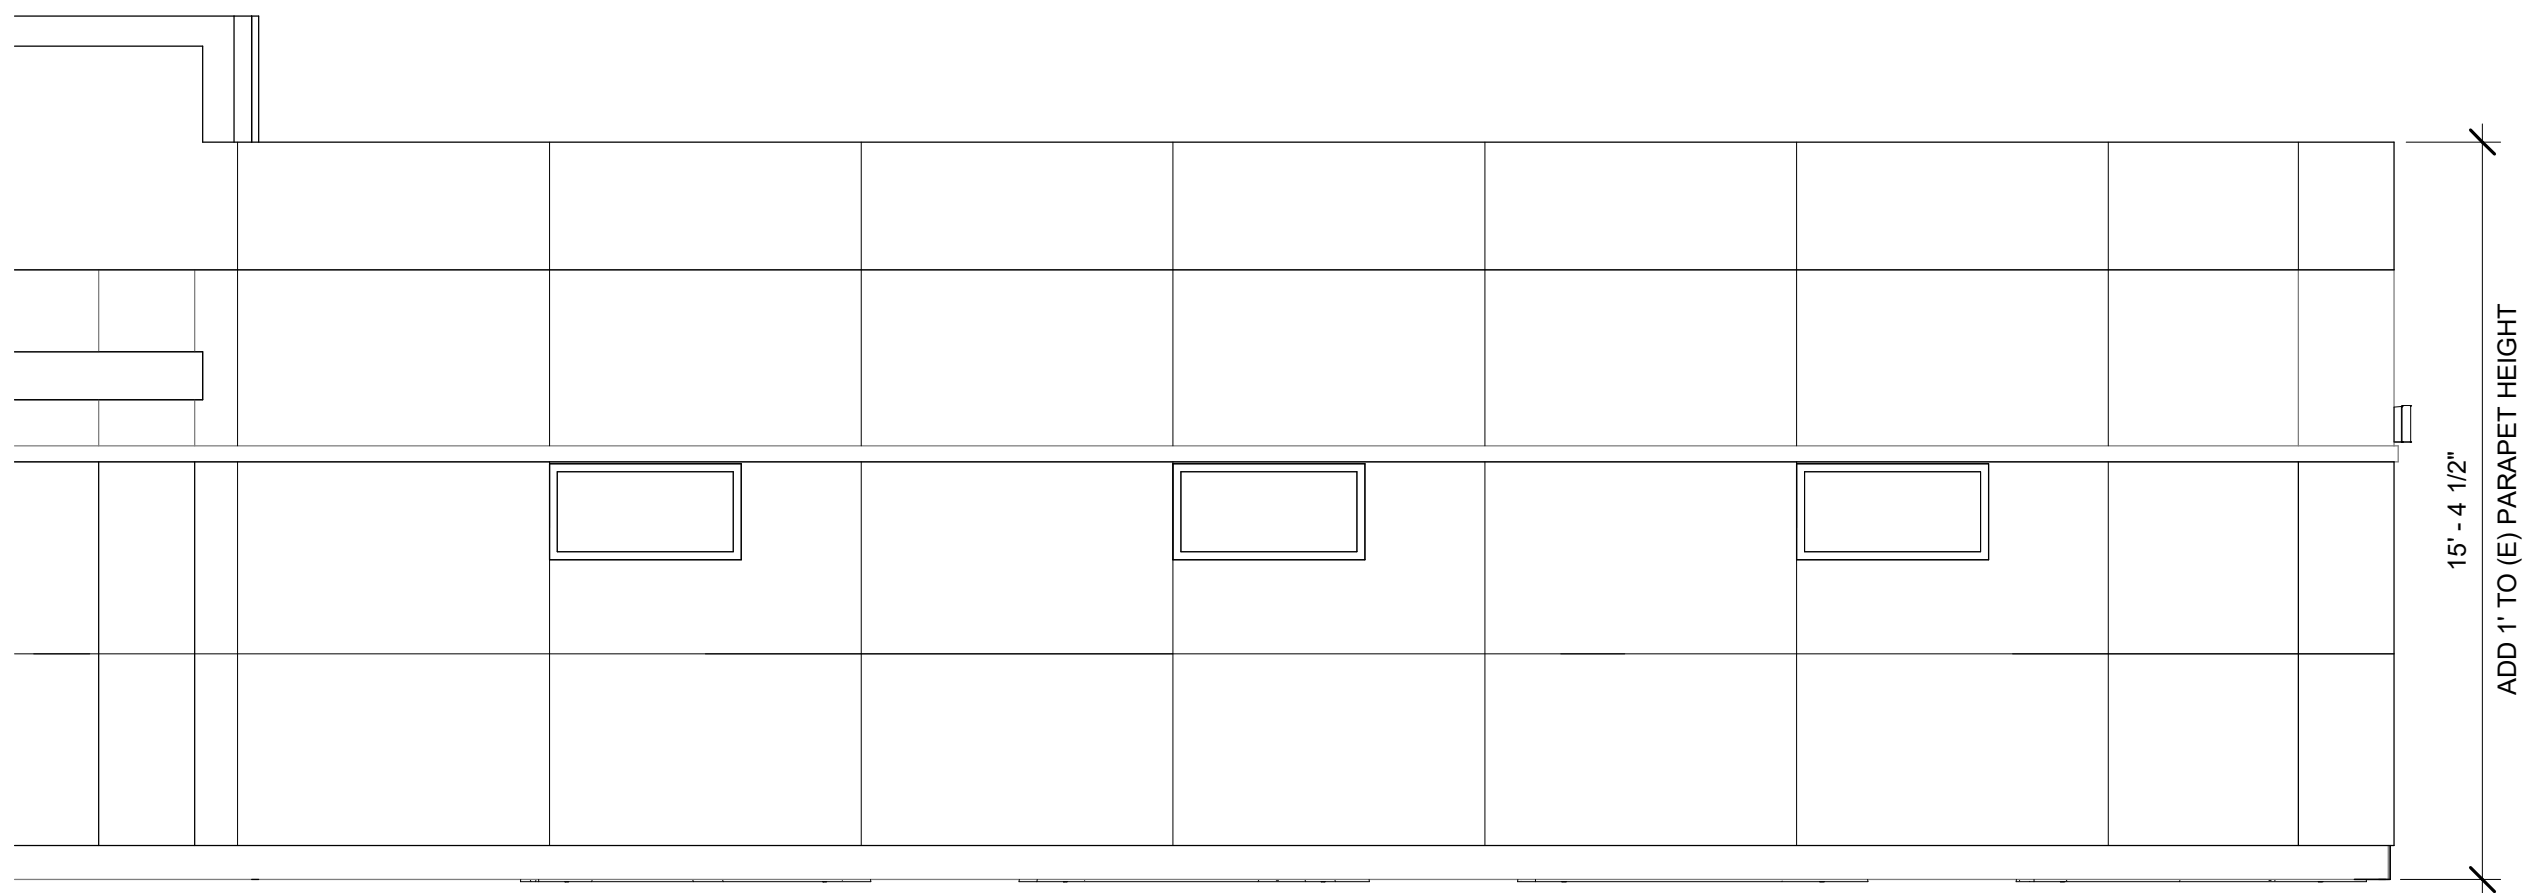

3 NEW EAST - Callout 2
1/4" = 1'-0"

A REMODEL FOR:
BLUE LAKES URGENT CARE
1309 BLUE BLAKES BLVD TWIN FALLS ID
NEW EXTERIOR ELEVATIONS


Laughlin Ricks Architecture
architecture/planning
134 3RD AVE. E. * Twin Falls, Idaho 83301
PHONE: (208) 736-8050

DATE: 4.19.22
NM RCR
Drawn Checked

A3-4



1 NEW WEST
1/8" = 1'-0"

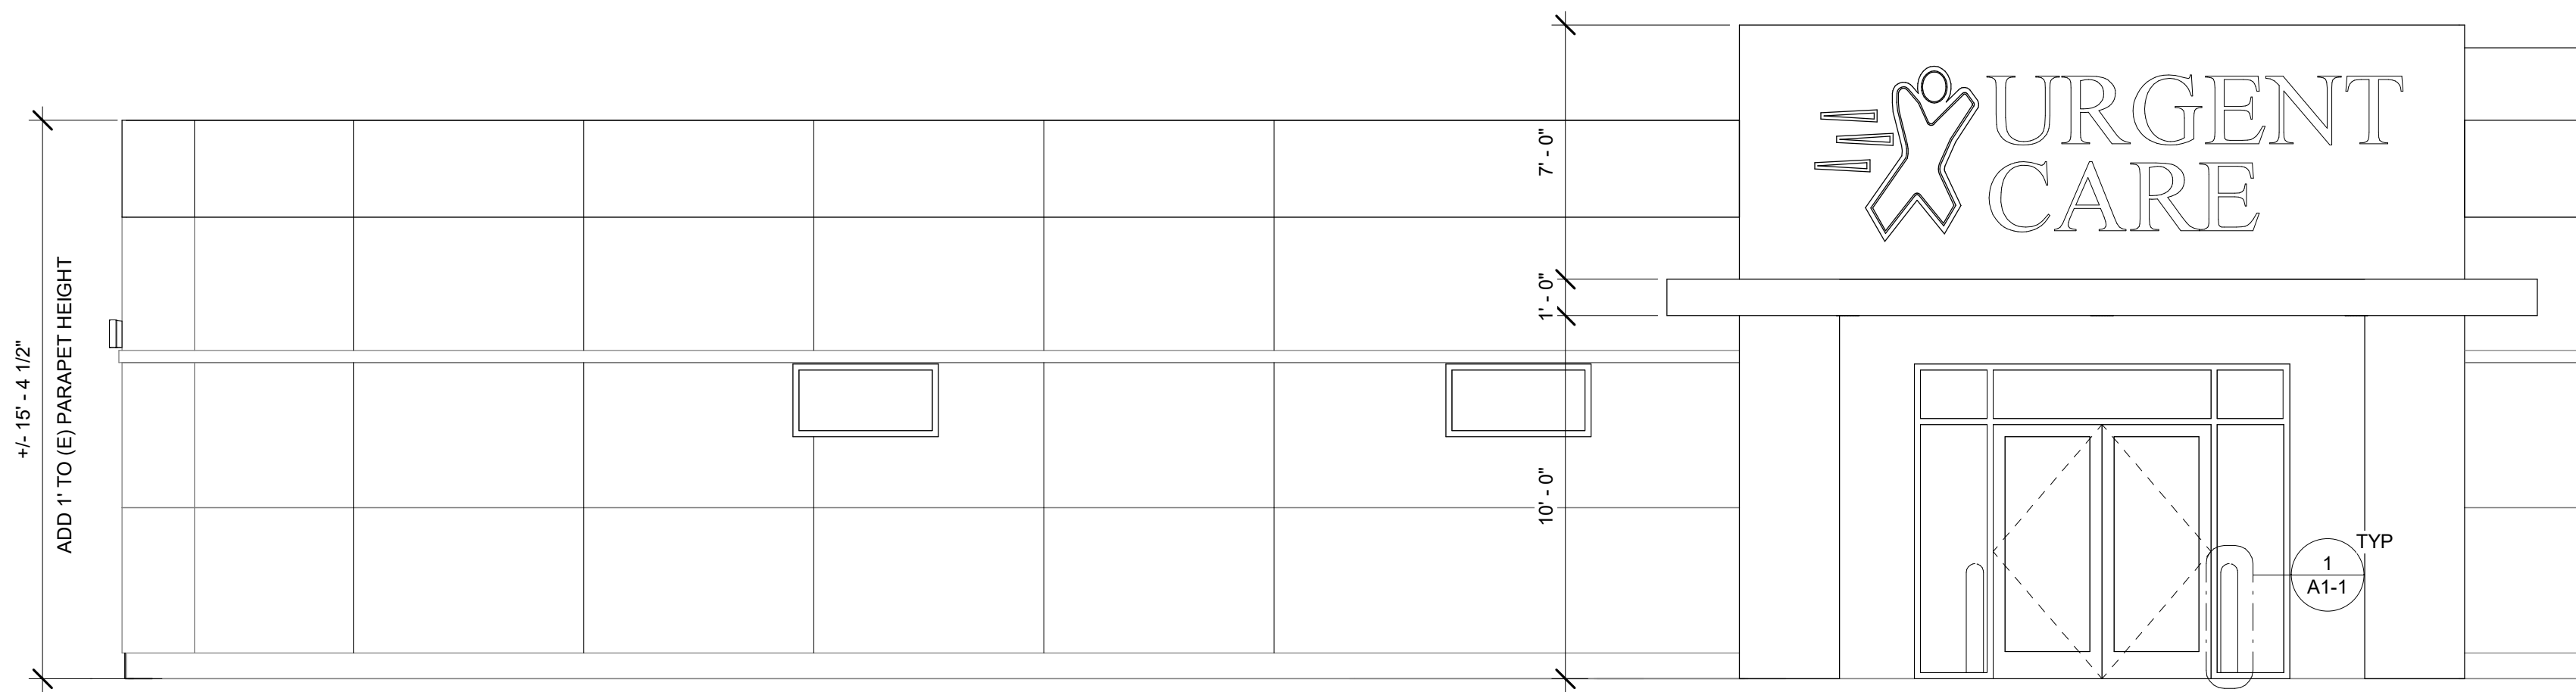

2 NEW WEST - Callout 1
1/4" = 1'-0"



3 NEW WEST - Callout 2
1/4" = 1'-0"

A REMODEL FOR:
BLUE LAKES URGENT CARE
1309 BLUE BLAKES BLVD TWIN FALLS ID
NEW EXTERIOR ELEVATIONS

Laughlin Ricks Architecture
architecture/planning
134 3RD AVE. E. * Twin Falls, Idaho 83301
PHONE: (208) 736-8050

DATE: 4.19.22
NM RCR
Drawn Checked


A3-5

4.19.22

DATE



ALTERNATE BID: PROVIDE RESILIENT CHANNEL @ ALL WALLS OF EXAM 1,2,3,4,5,6, AND PROCEDURE

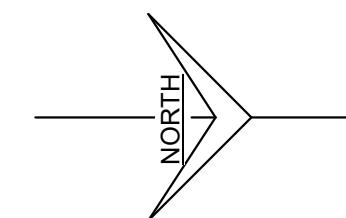

4.19.22

DATE _____


A REMODEL FOR:
BLUE LAKES URGENT CARE
1309 BLUE BLAKES BLVD TWIN FALLS, ID
WALL TYPES PLAN

Laughlin Ricks Architecture
— architecture/planning —
134 3RD AVE. E. * Twin Falls, Idaho 83301
PHONE: (208) 736-8050


DATE: 4.19.22

NM	RCR
Drawn	Checked

A6-0


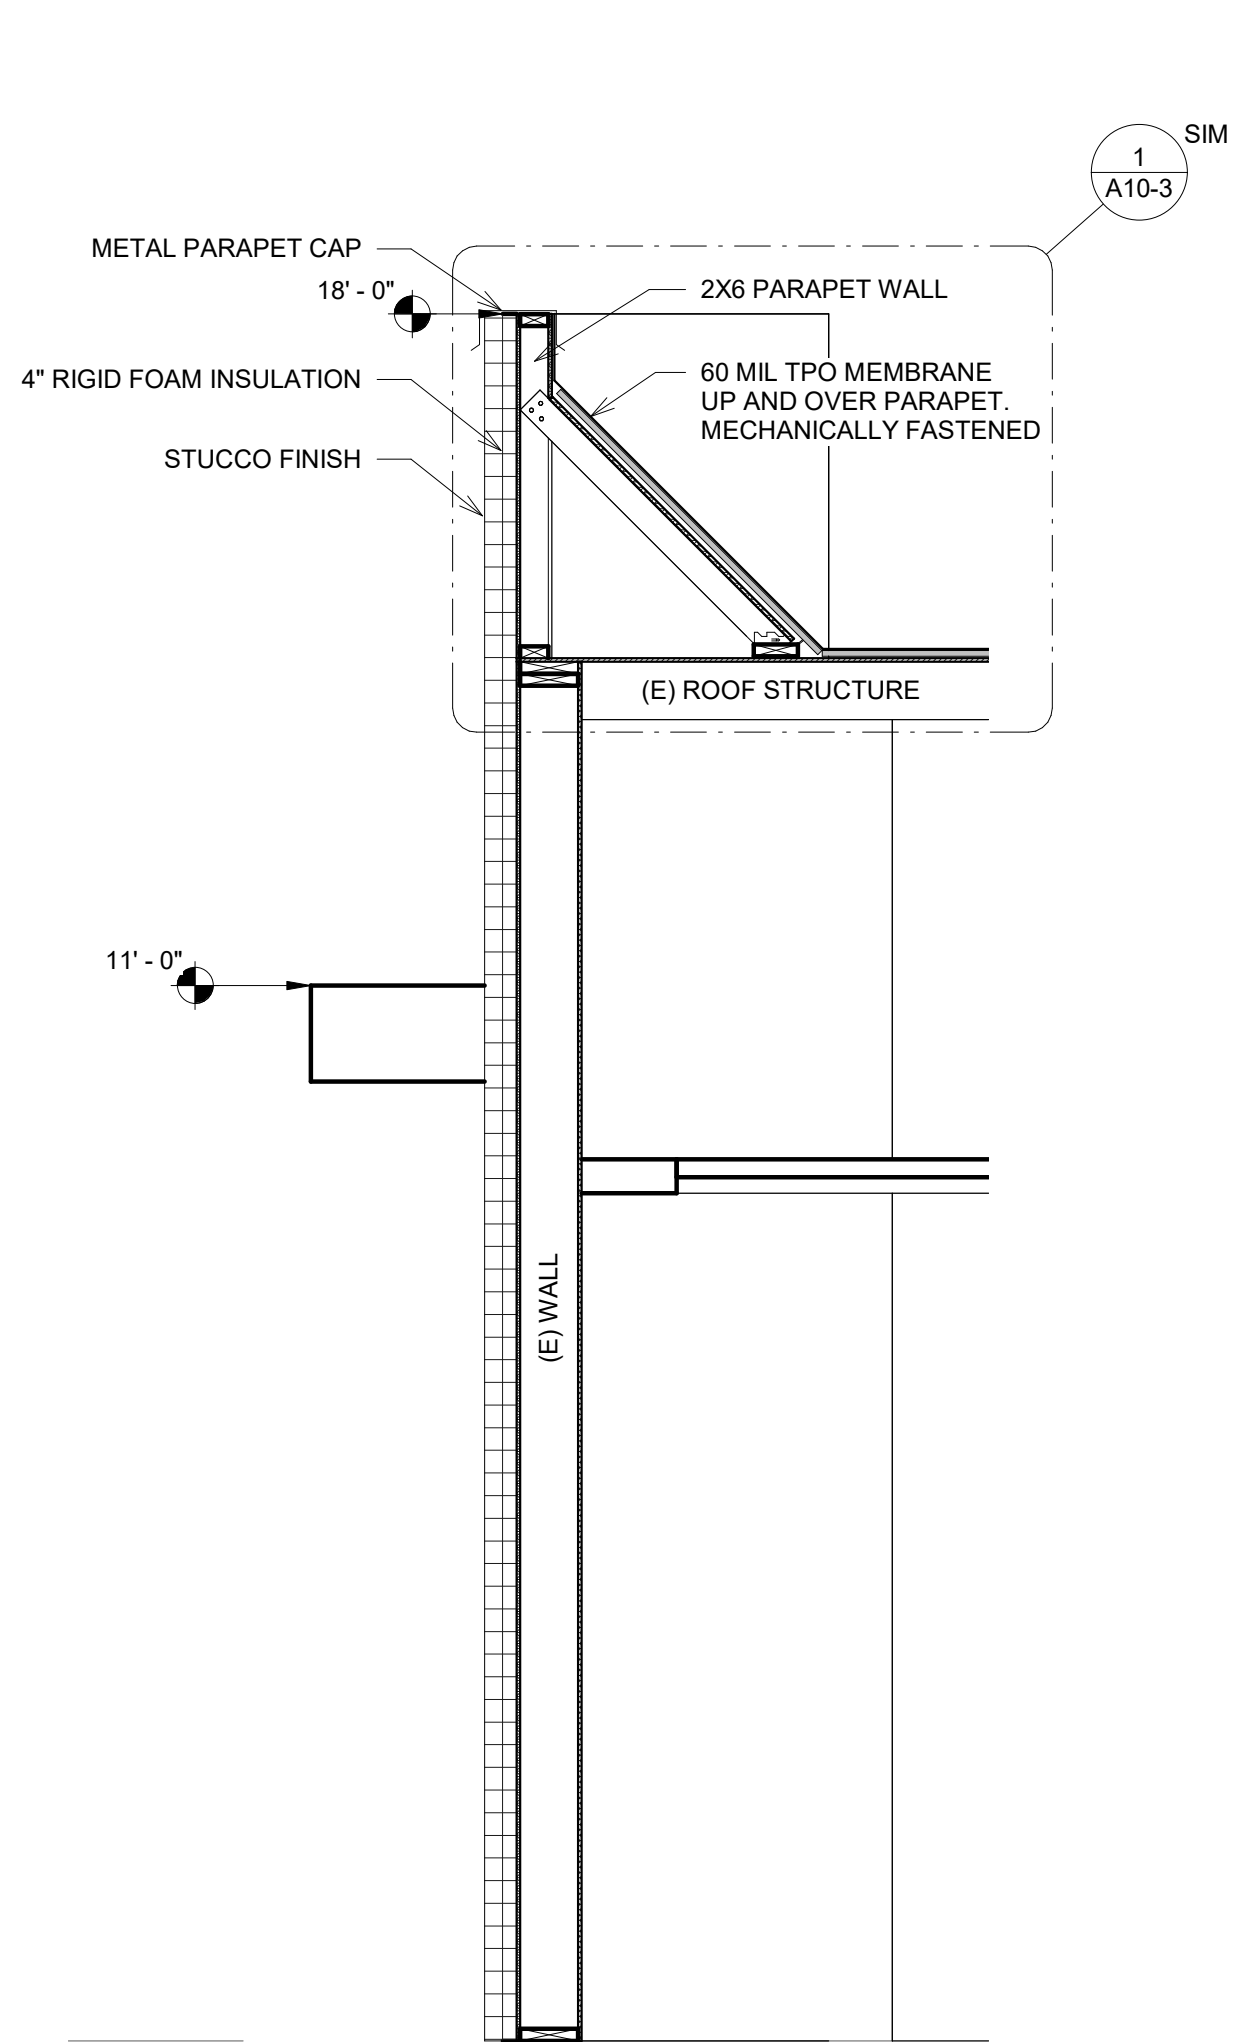


1 Wall Section 1
1/2" = 1'-0"


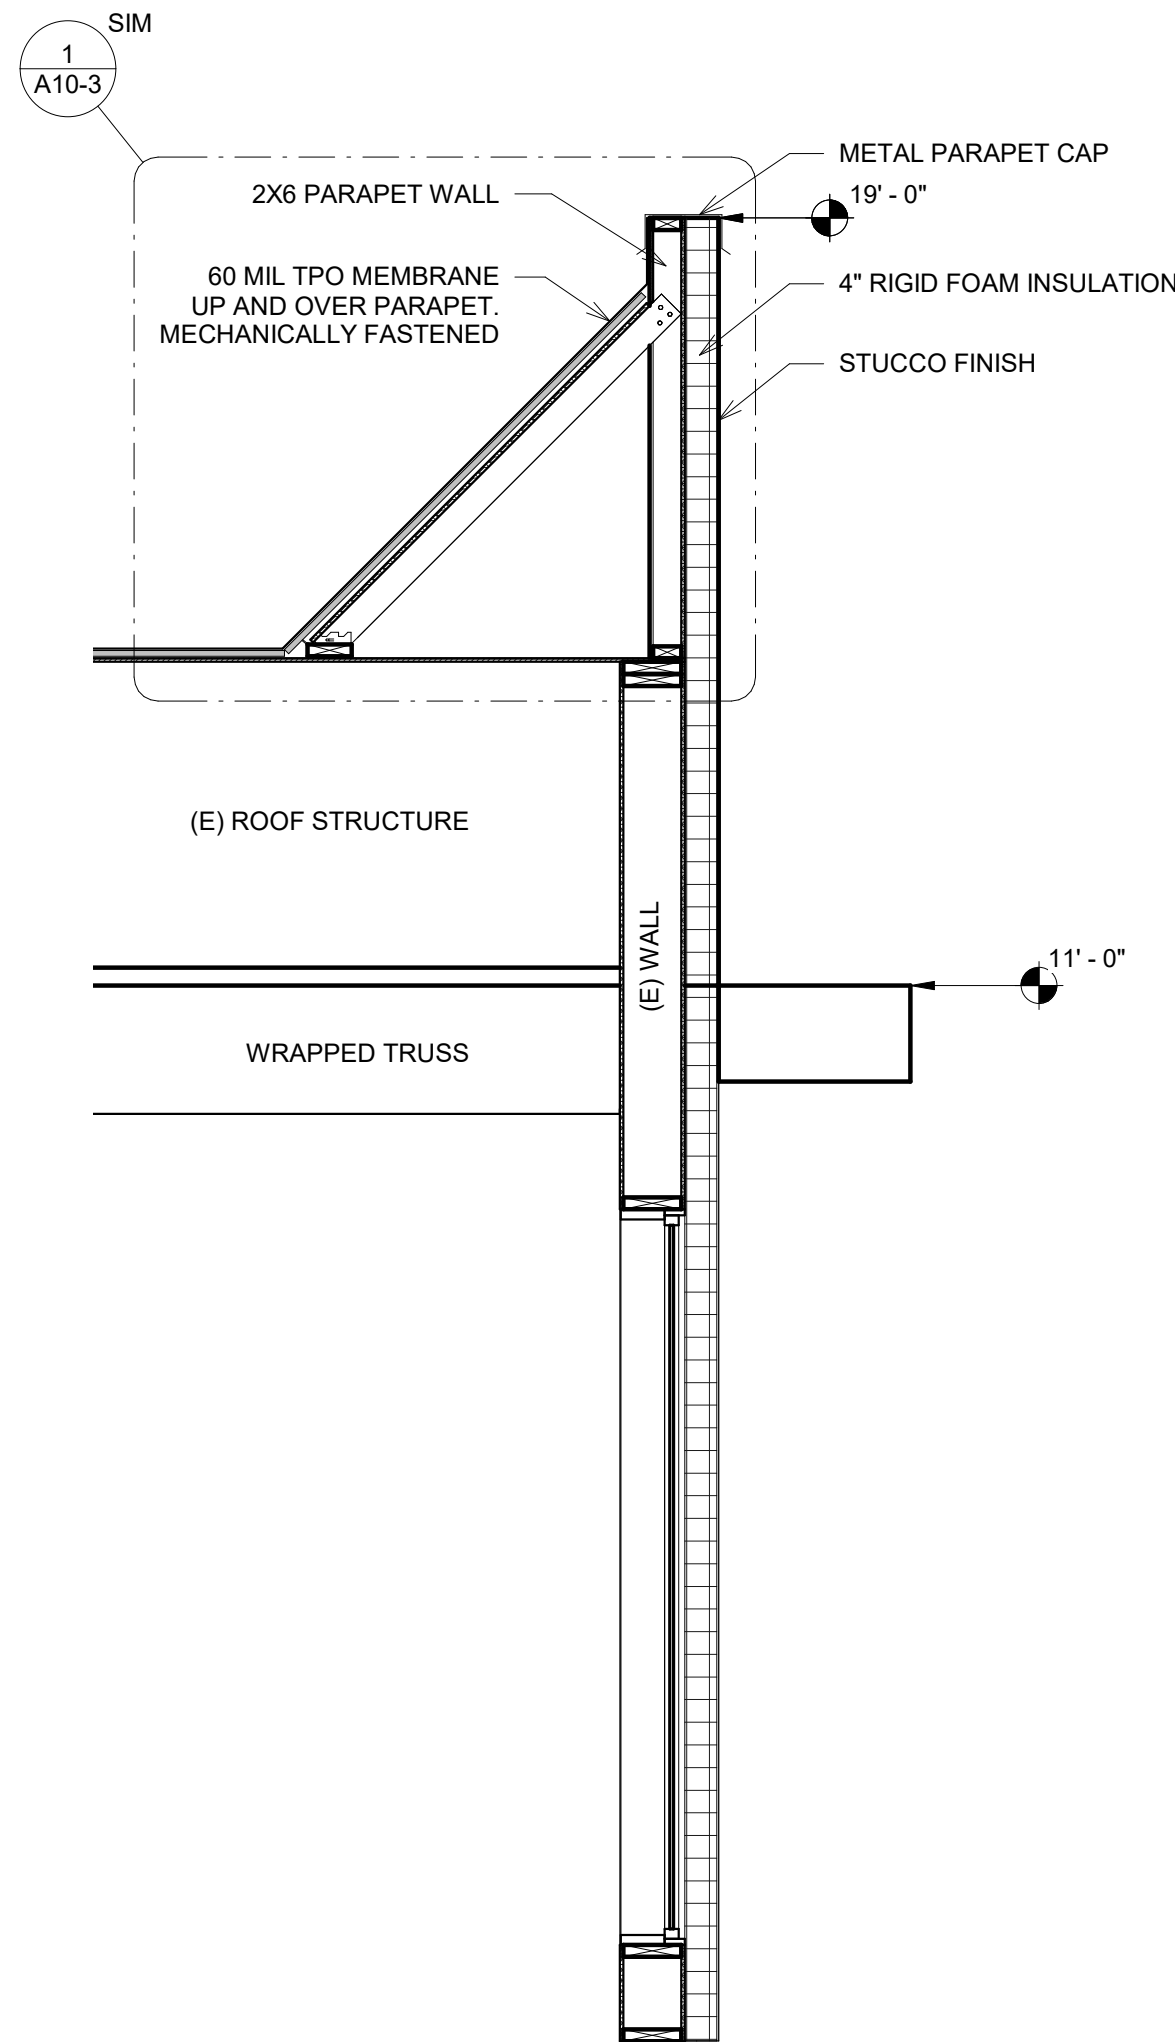


2 Wall Section 2
1/2" = 1'-0"



*REFER TO INTERIOR ELEVATIONS & FINISH SCHEDULE FOR FINISHES

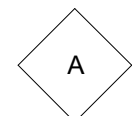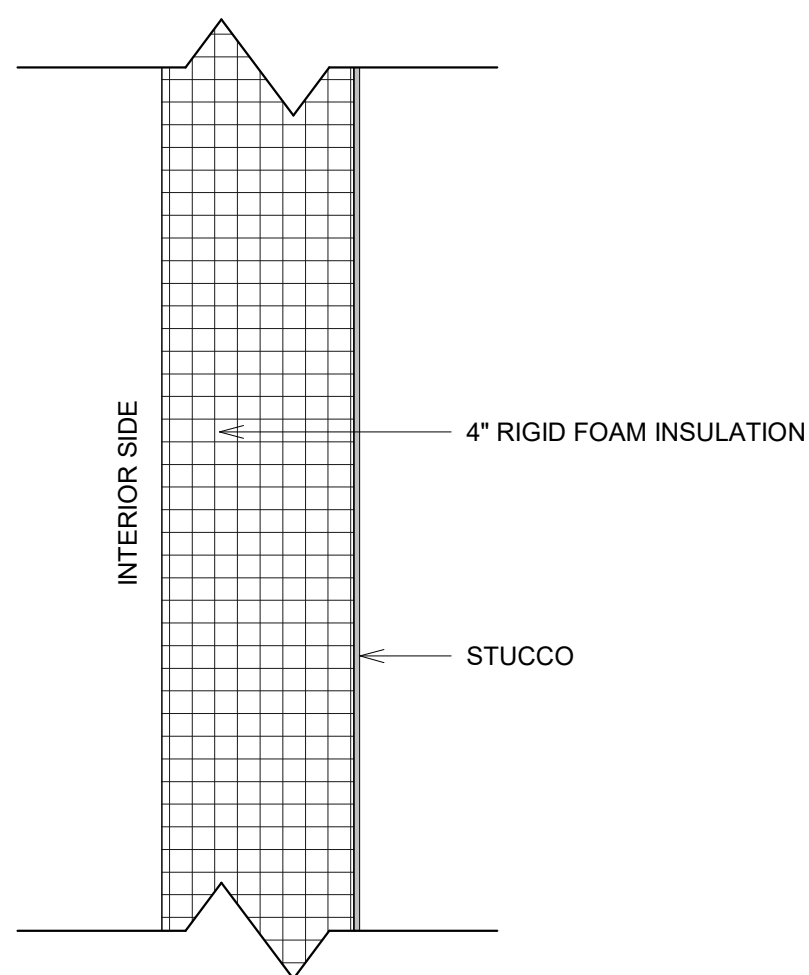



EXTERIOR

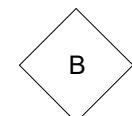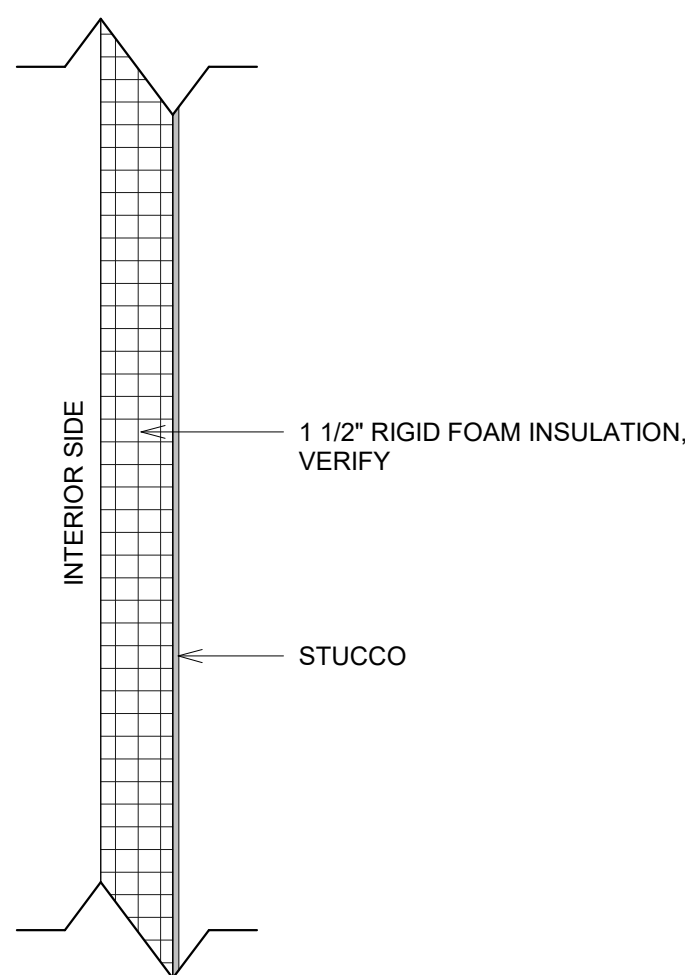



EXTERIOR

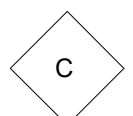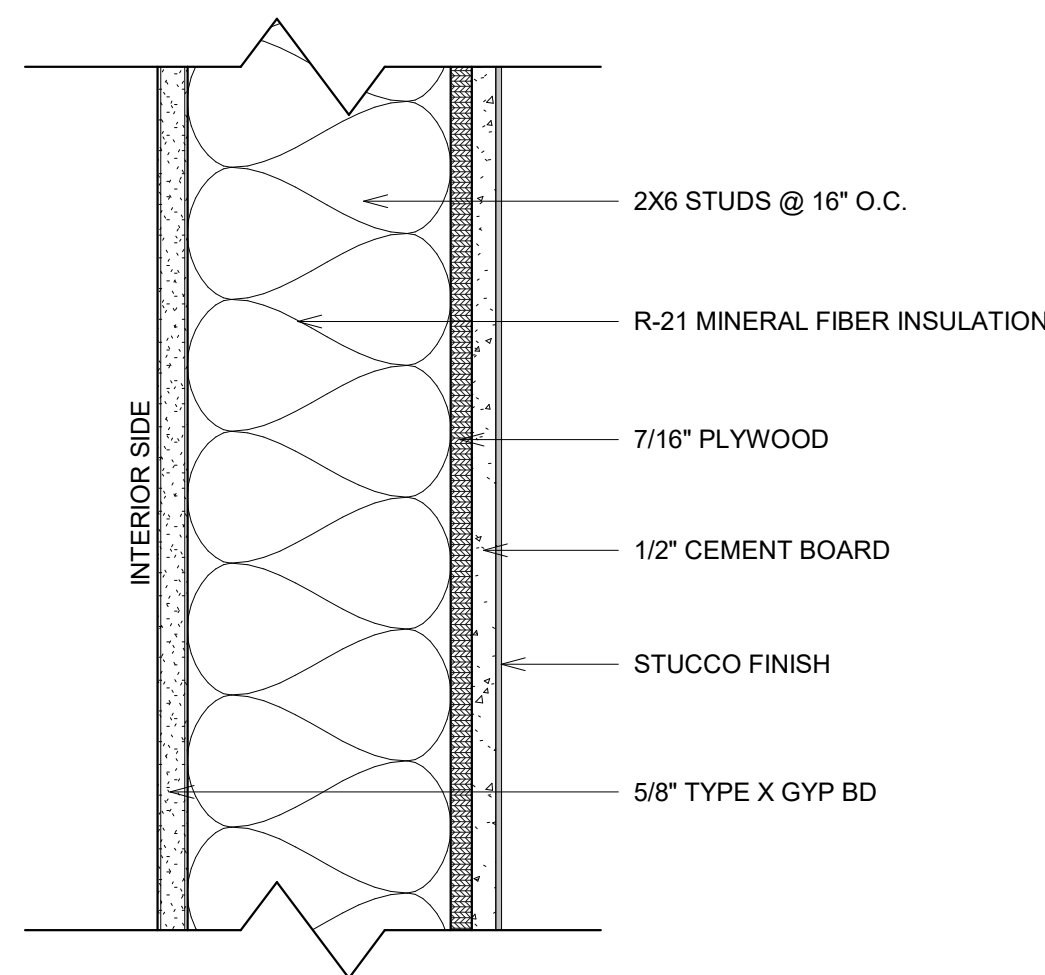



EXTERIOR

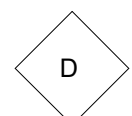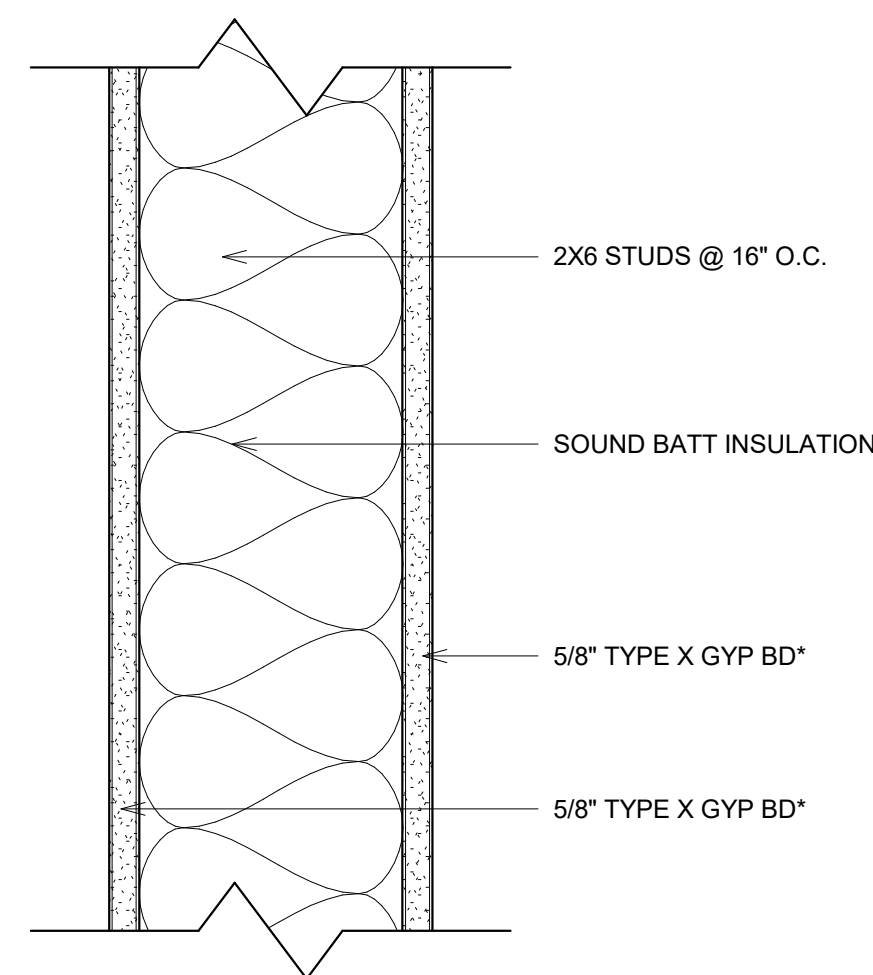

INTERIOR

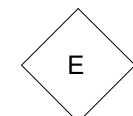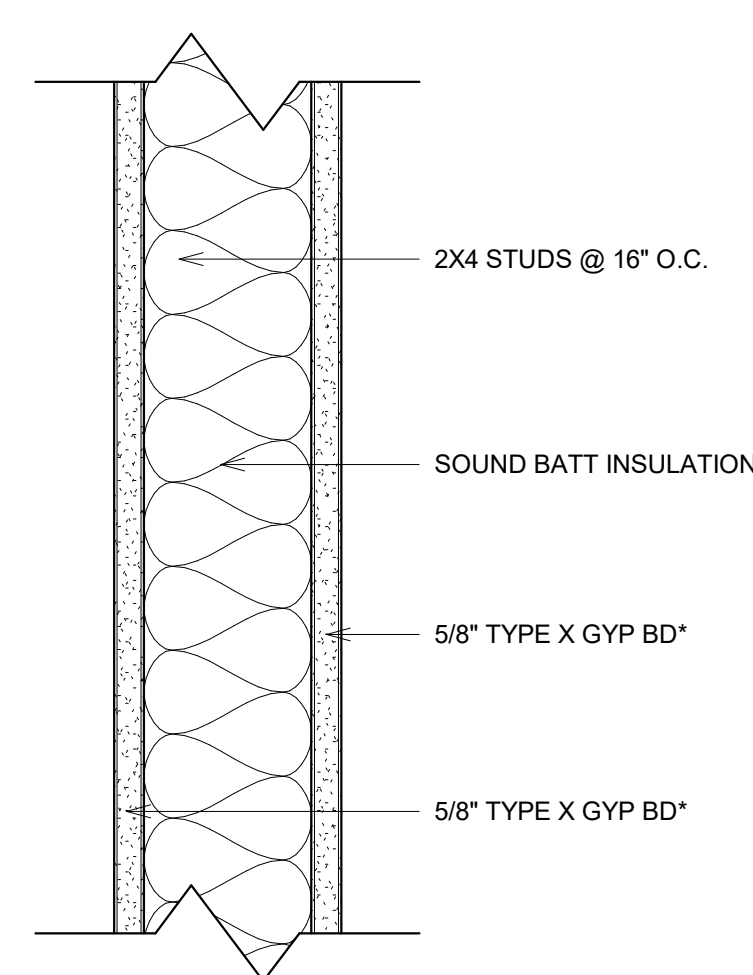

INTERIOR

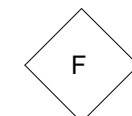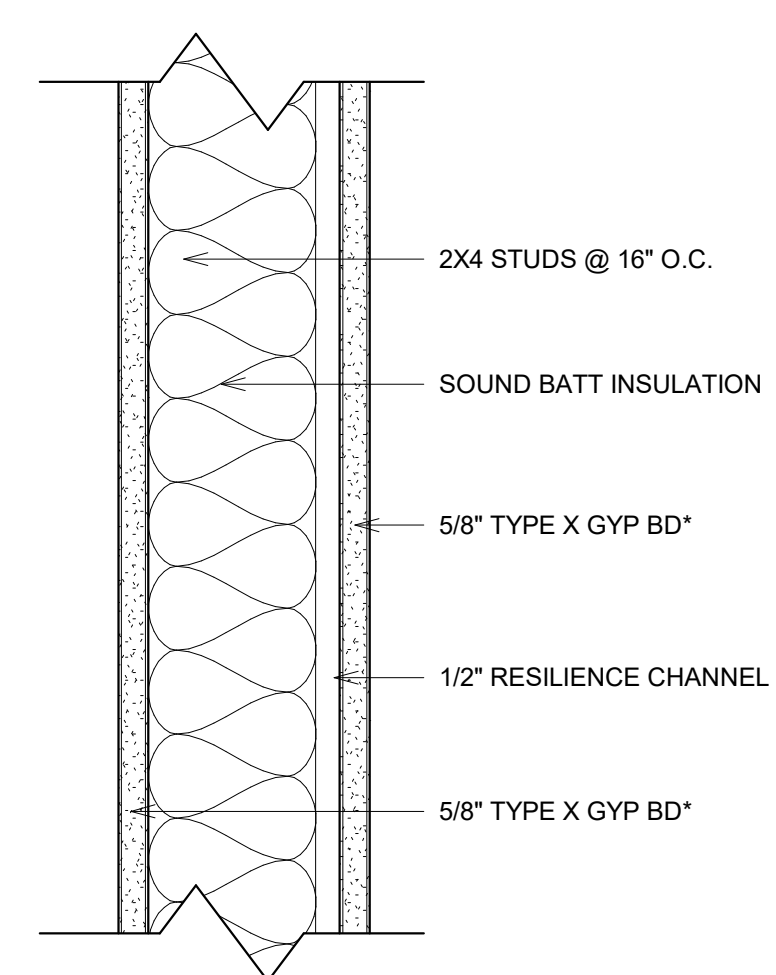

INTERIOR

WALL TYPES
3" = 1'-0"

A REMODEL FOR:

BLUE LAKES URGENT CARE

1309 BLUE BLAKES BLVD TWIN FALLS, ID

WALL SECTIONS & TYPES

Laughlin Ricks Architecture

architecture/planning

134 3RD AVE. E. * Twin Falls, Idaho 83301

PHONE: (208) 736-8050

DATE: 4.19.22

NM RCR
Drawn Checked

A6-1

Lighting Fixture Schedule						
LABEL	DESCRIPTION	MOUNTING	VOLTAGE	WATTAGE	MANUFACTURER	NOTES
F1	4" ROUND RECESSED LED CAN, 0-10V DIMMING, FIELD SELECTABLE LUMENS/CCT	RECESSED	120-277	25	LITHONIA	1
F2	2X2 LED TROFFER	LAY-IN	120	29.4	METALUX	1
F2E	2X2 LED TROFFER (EM)	LAY-IN	120	29.4	METALUX	1
F3	2X4 LED TROFFER	LAY-IN	120	40.4	METALUX	1
F3E	2X4 LED TROFFER (EM)	LAY-IN	120	40.4	METALUX	1
F4	4' X 15/16" T-BAR LED DIFFUSING LENS	LAY-IN	CLASS 2 - 24VDC	32	JLC-TECH	1, PLENTUM RATED CABLE WITH CLASS 2 QUICK CONNECTORS
F5E	LED WALLPACK, WPX2	SURFACE	120	47	LITHONIA	1, EMERGENCY BATTERY BACKUP
F6	RECESSED DOWNLIGHT	RECESSED	120-277	40	LITHONIA	1
F6E	RECESSED DOWNLIGHT	RECESSED	120-277	40	LITHONIA	1, EMERGENCY BATTERY BACKUP

1. DESIGN IS BASED ON FIRST NAMED MANUFACTURER. ALTERNATE MANUFACTURERES ARE ACCEPTABLE, SUBJECT TO COMPLIANCE WITH SPECIFIED REQUIREMENTS, MODEL NUMBER, TYPE, AND OR CATALOG NUMBER.



1 Level 1
1/4" = 1'-0"

4.19.22


DATE _____

A REMODEL FOR:
BLUE LAKES URGENT CARE
1309 BLUE LAKES BLVD TWIN FALLS, ID
CEILING PLAN



























Laughlin Ricks Architecture
architecture/planning
134 3RD AVE. E. * Twin Falls, Idaho 83301
PHONE: (208) 736-8050

DATE: 4.19.22
NM RCR
Drawn Checked

A7-0

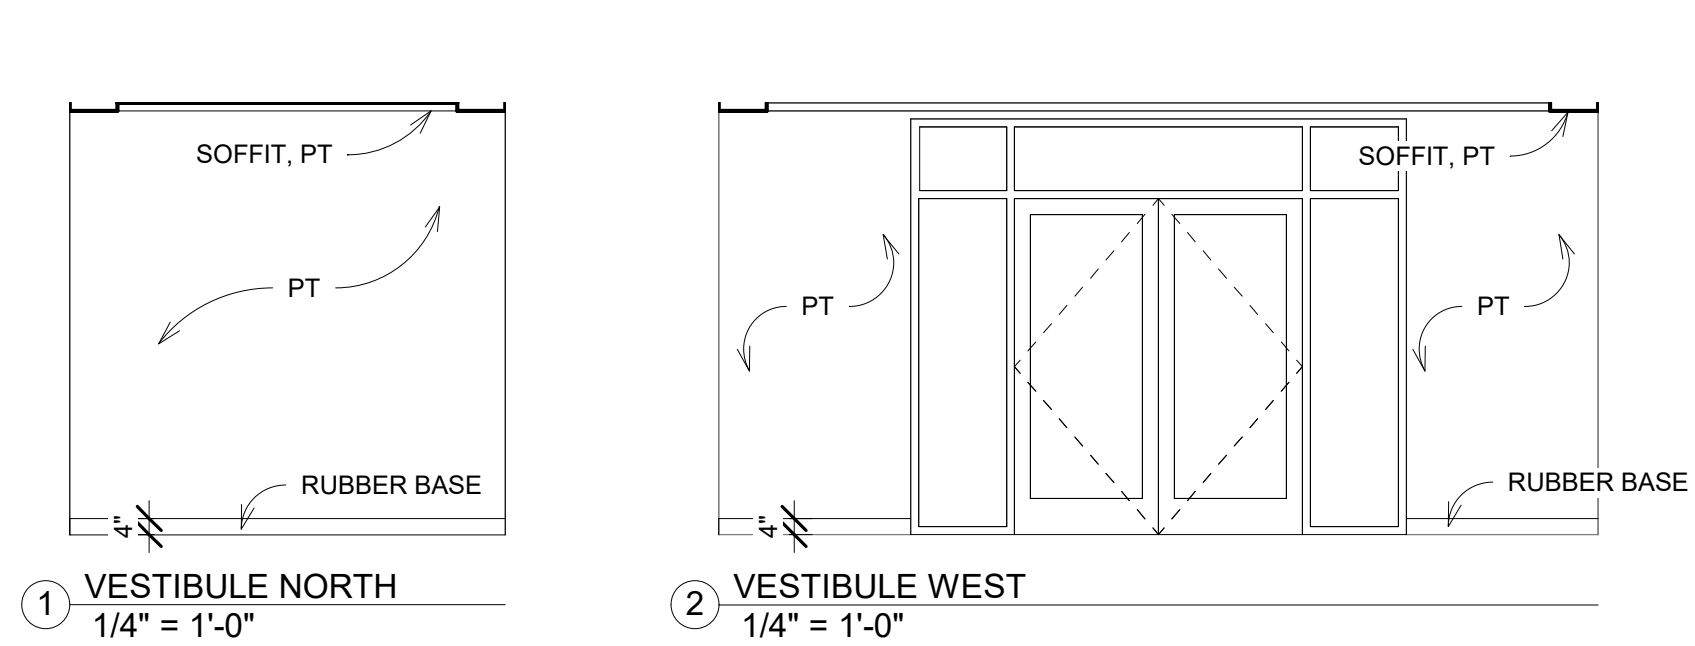

② VESTIBULE WEST
1/4" = 1'-0"

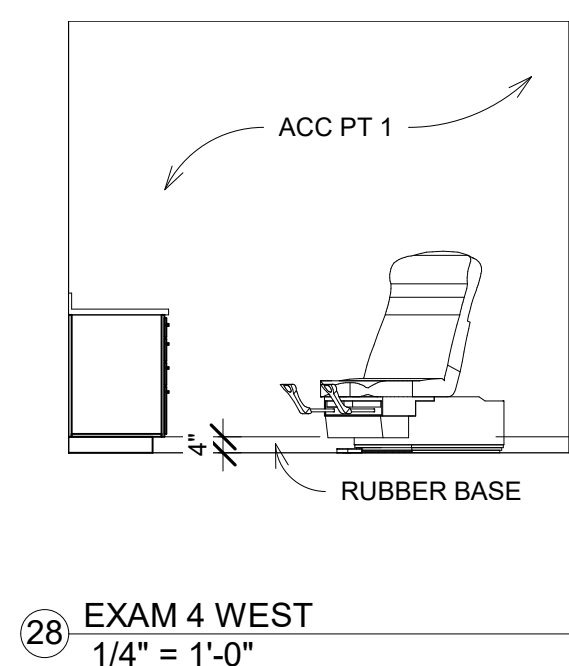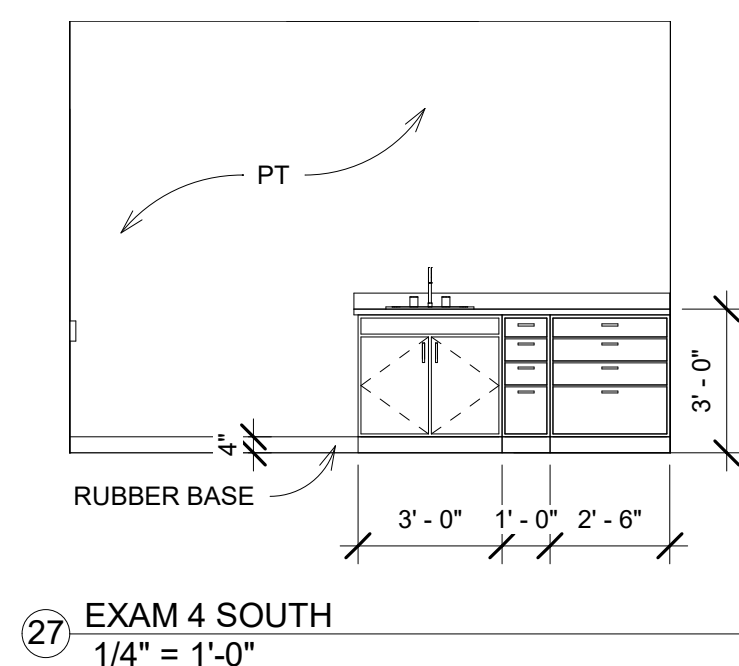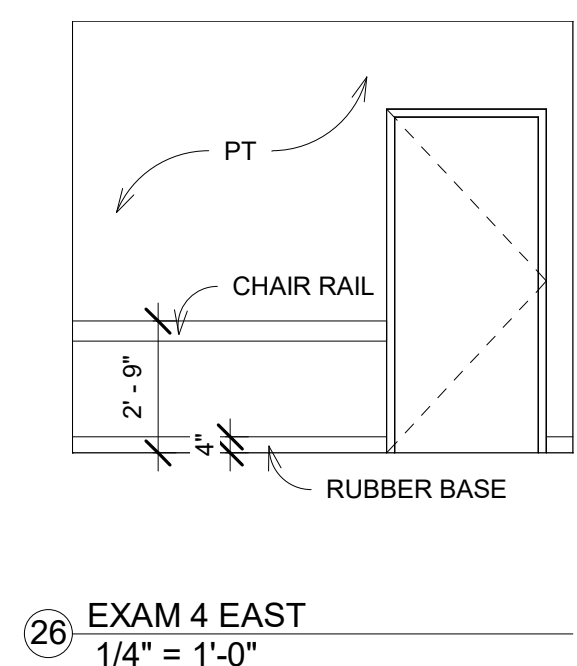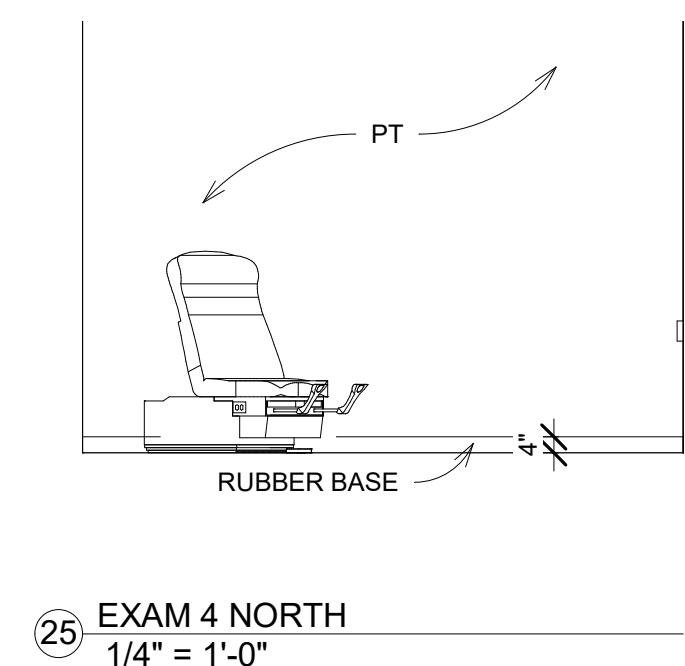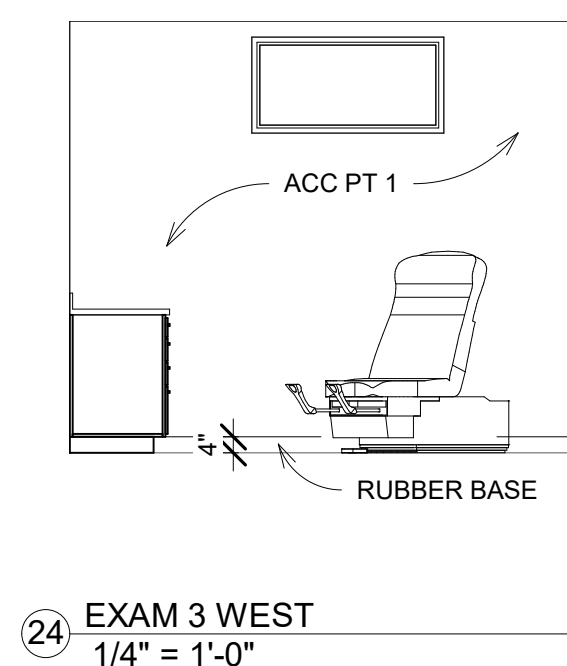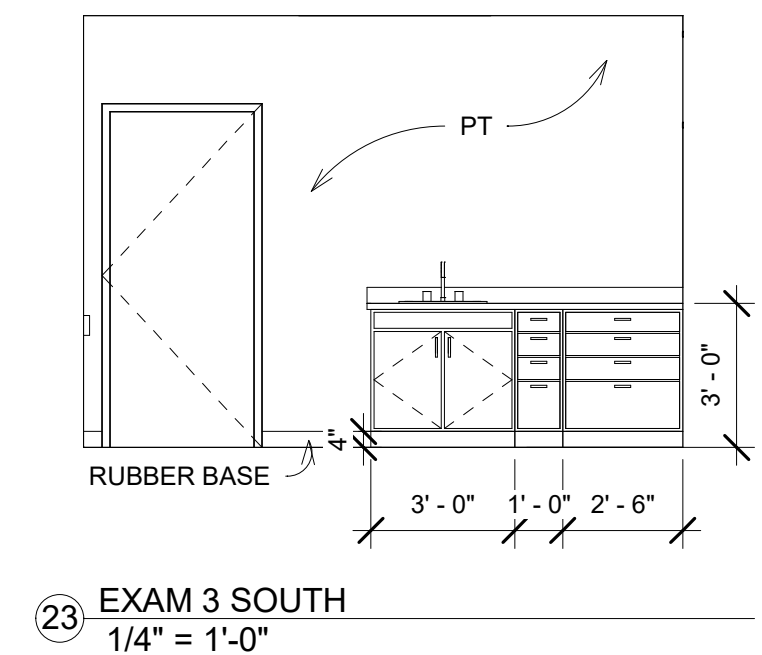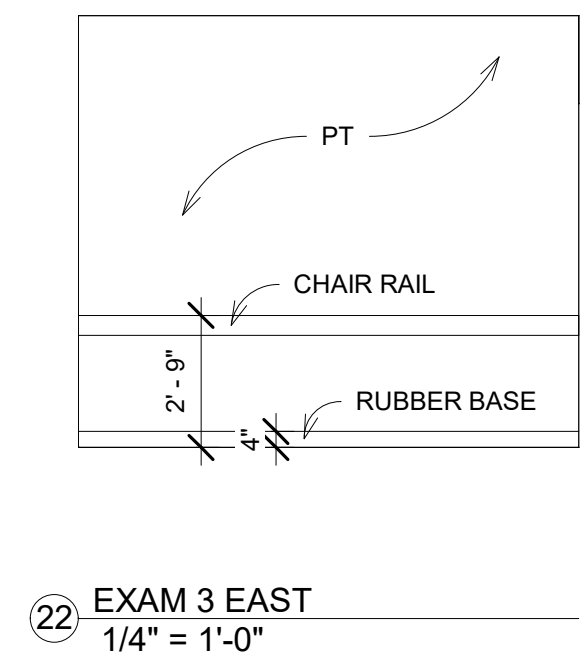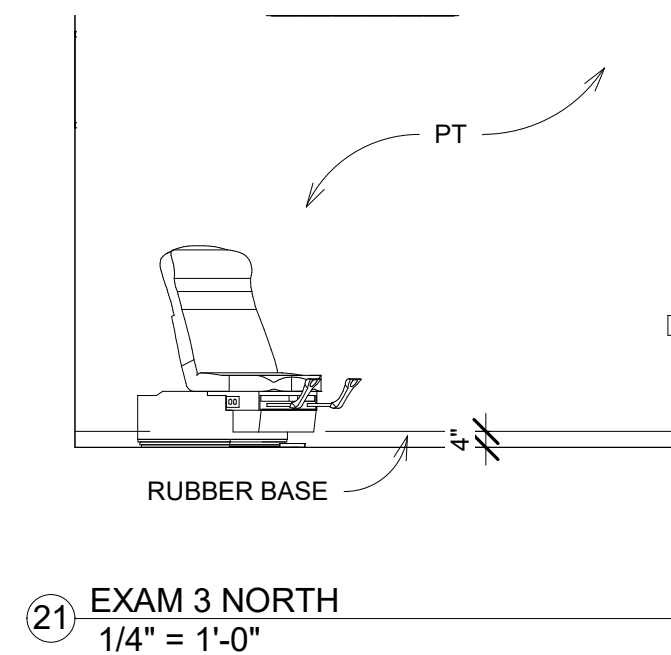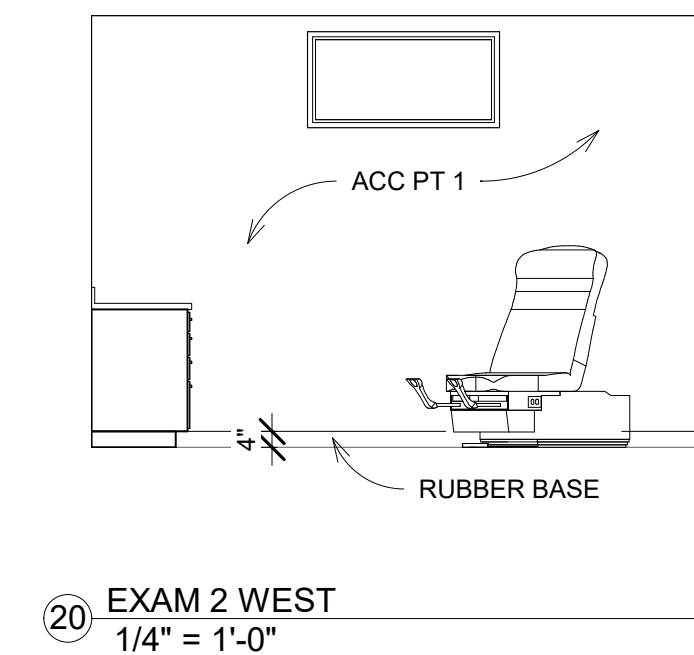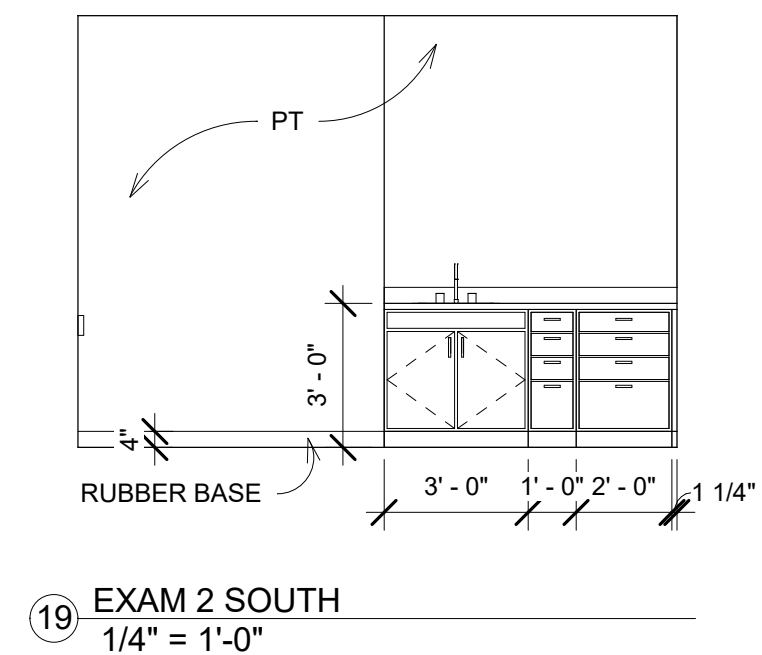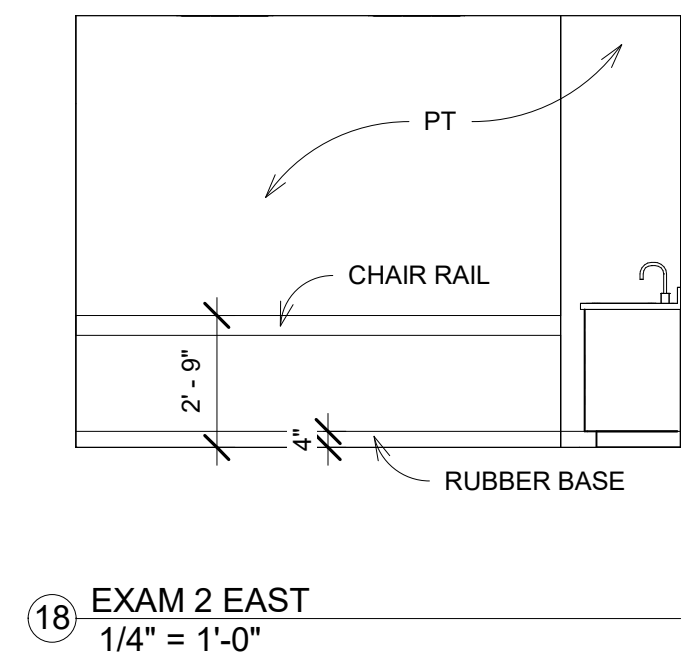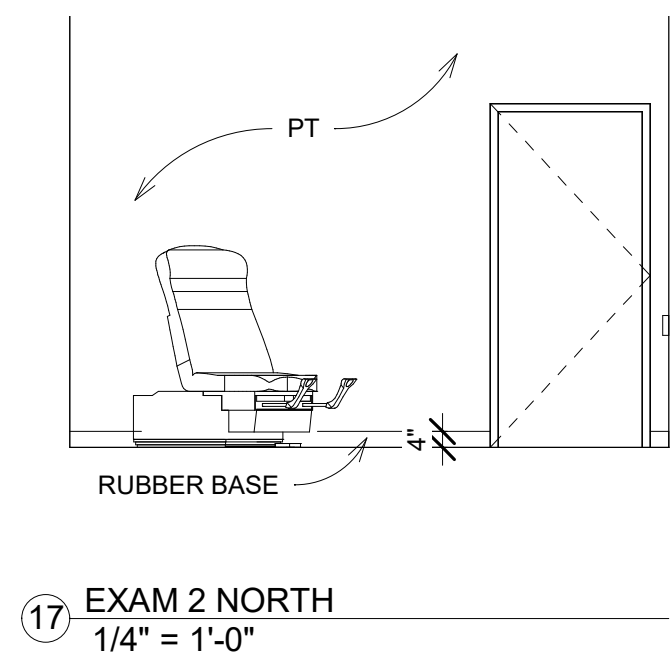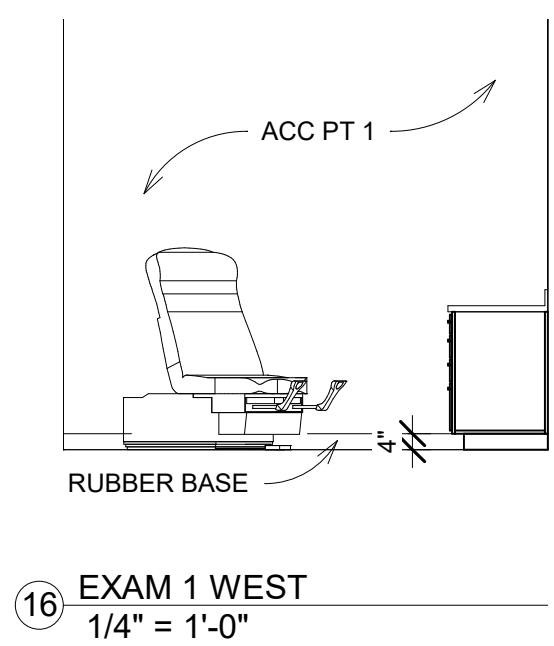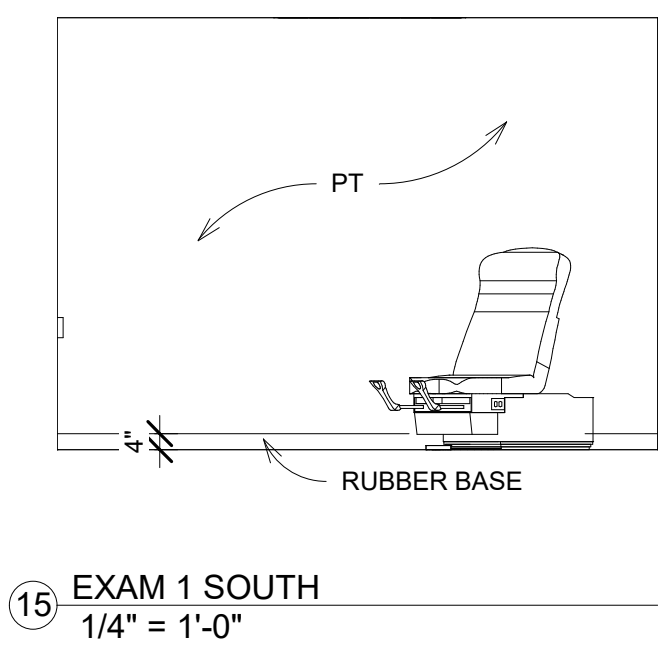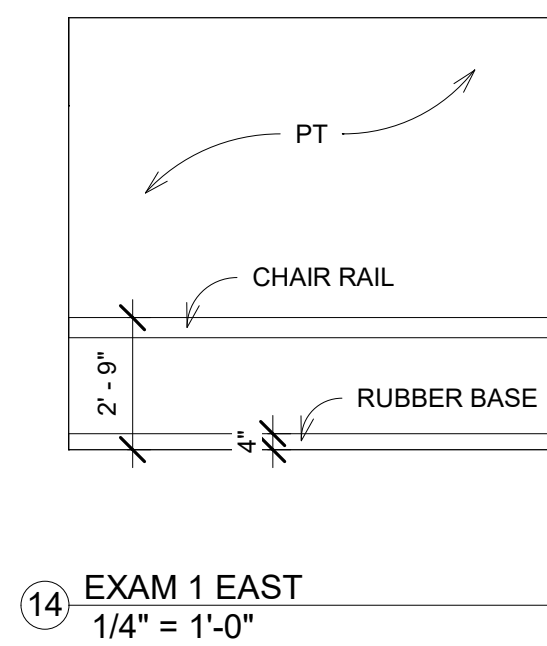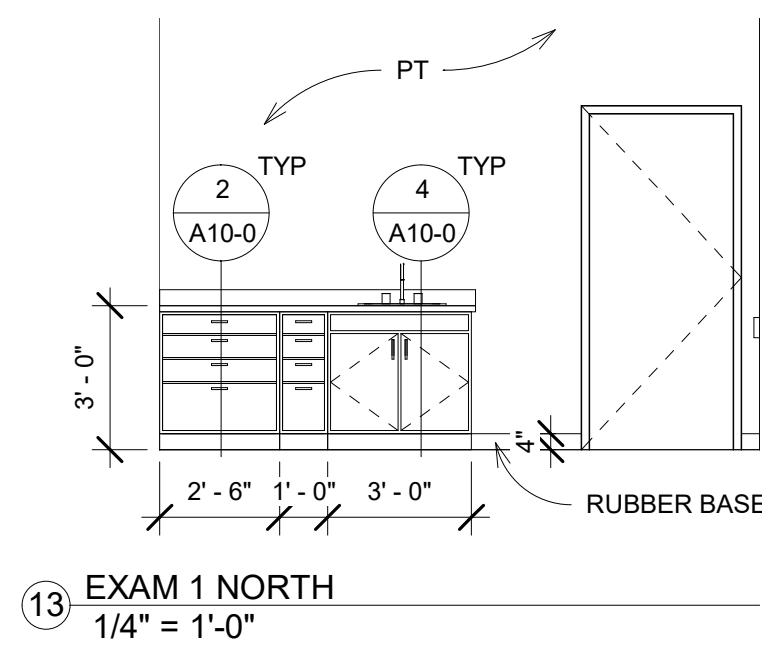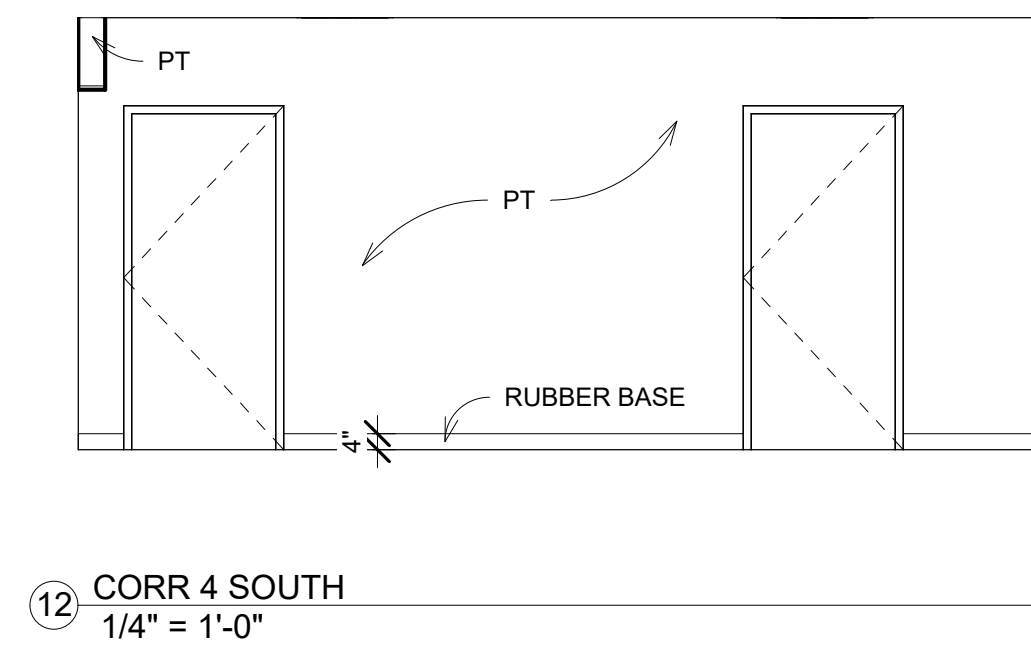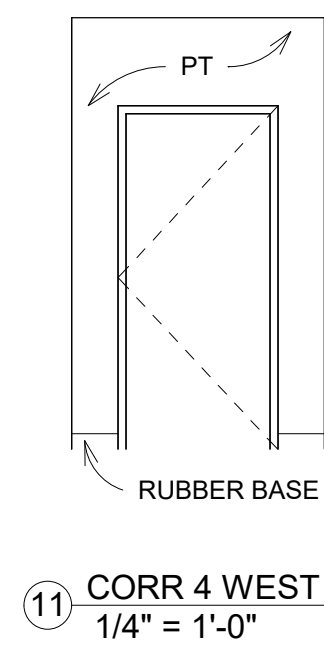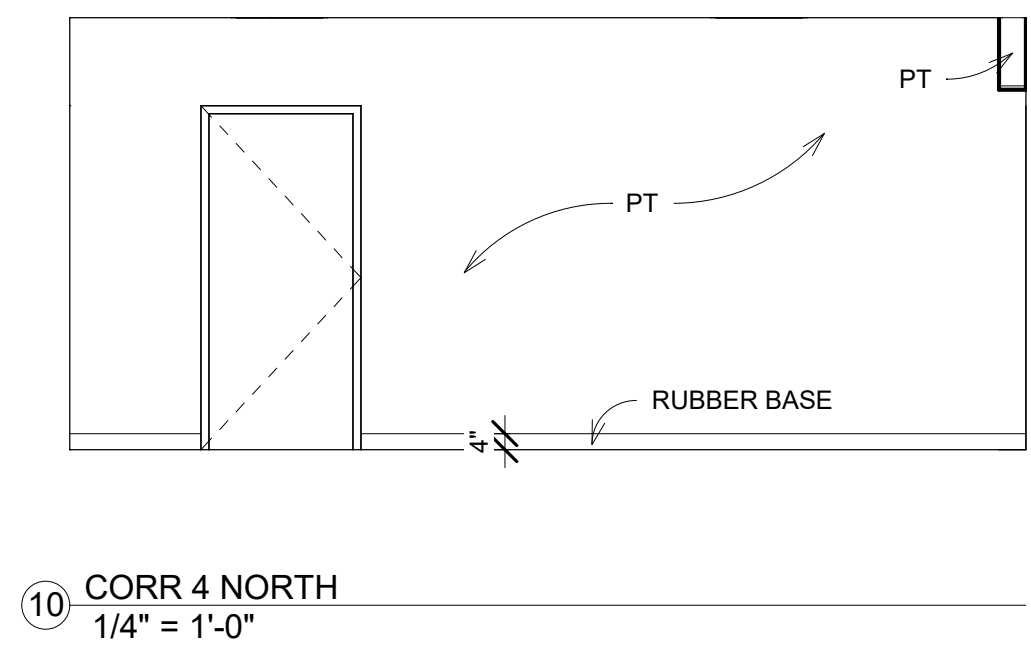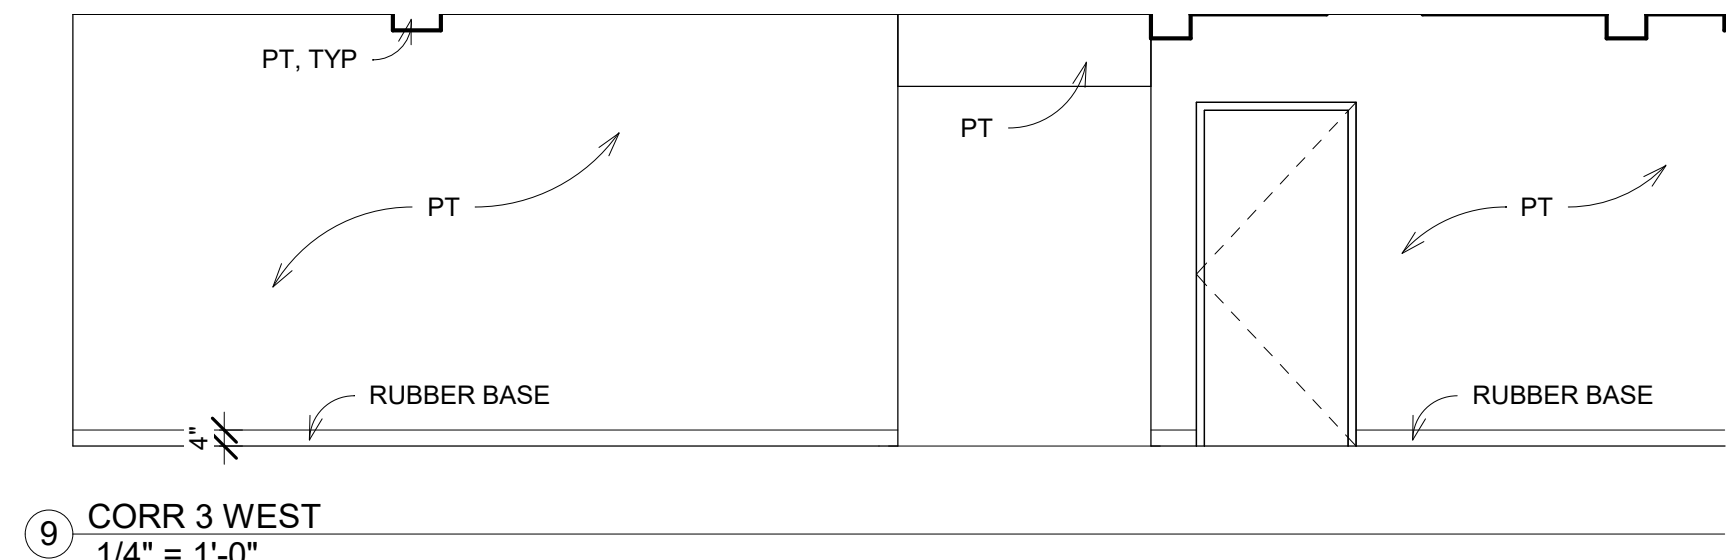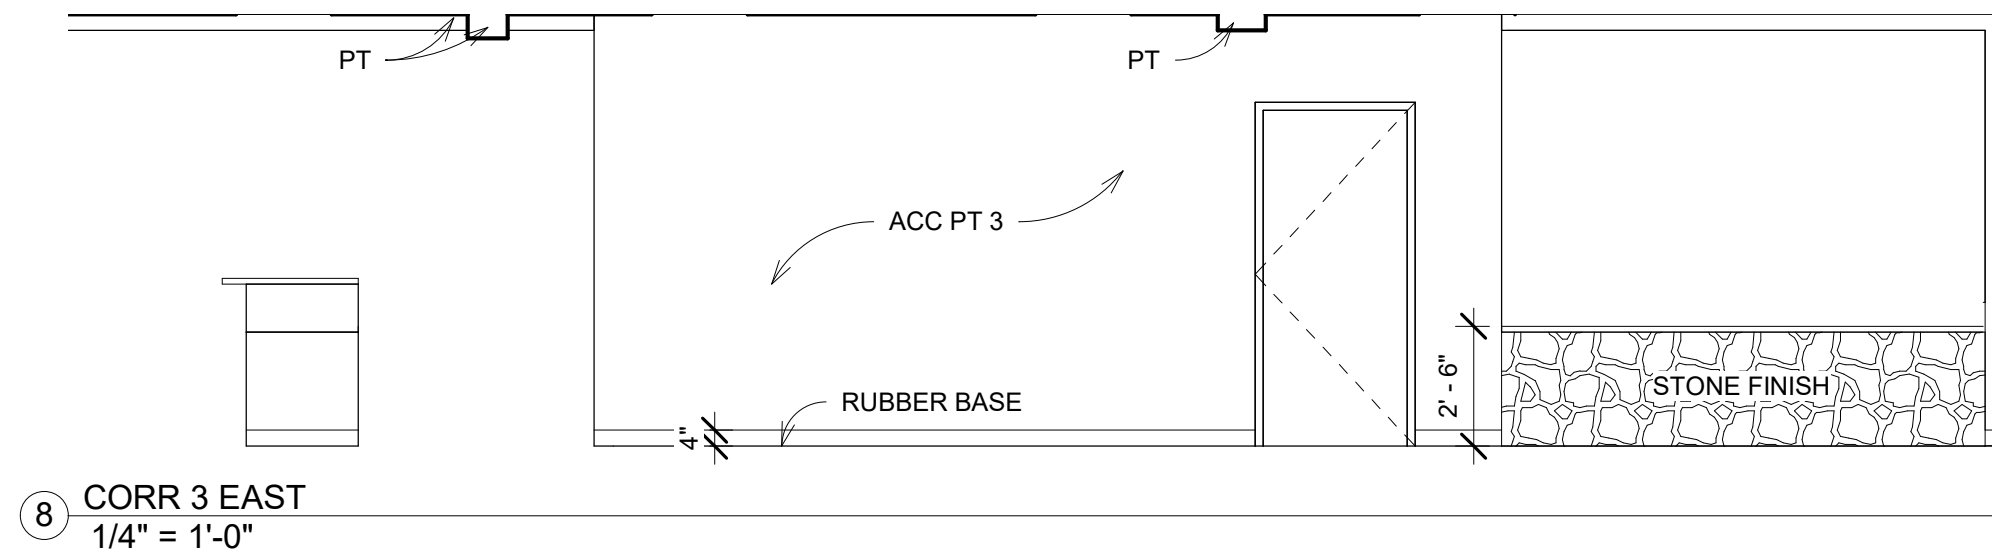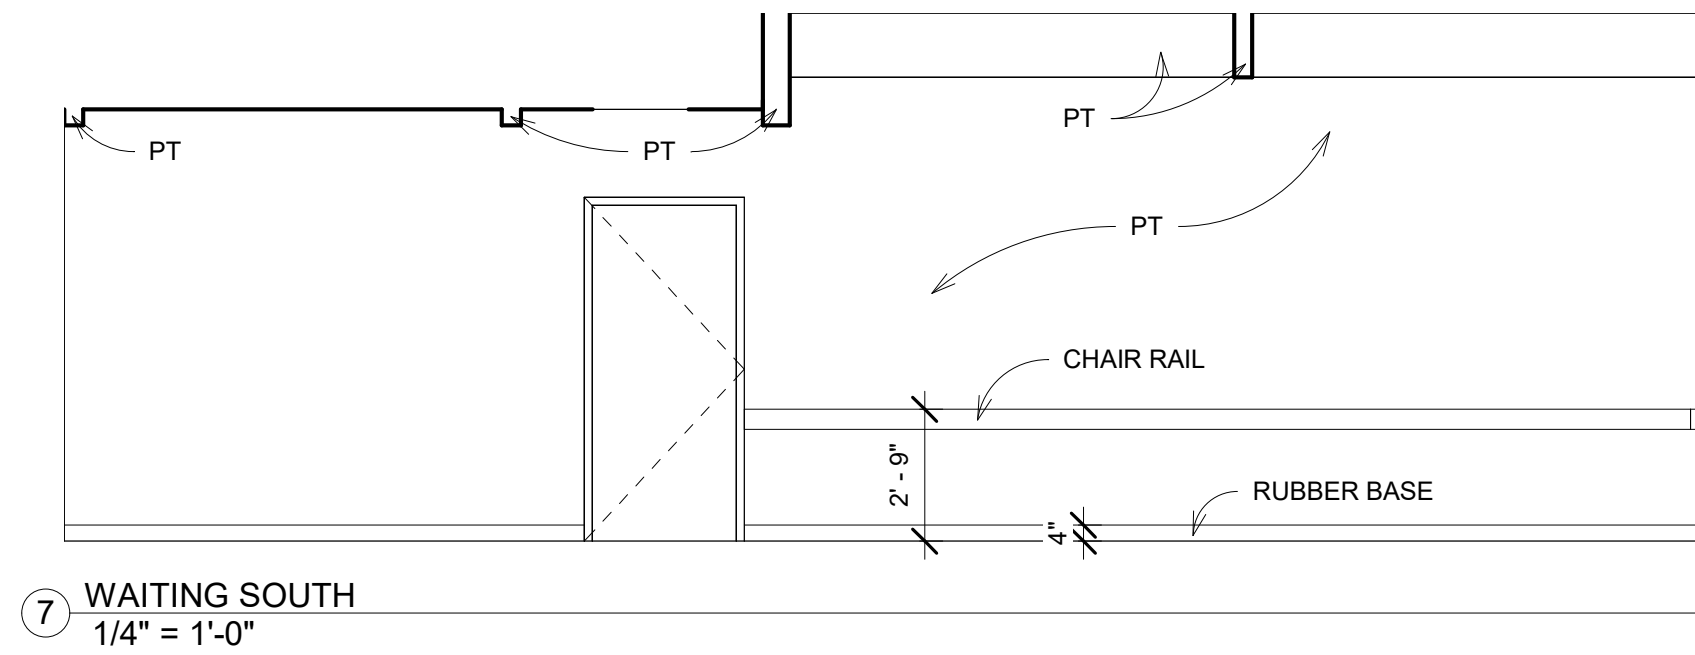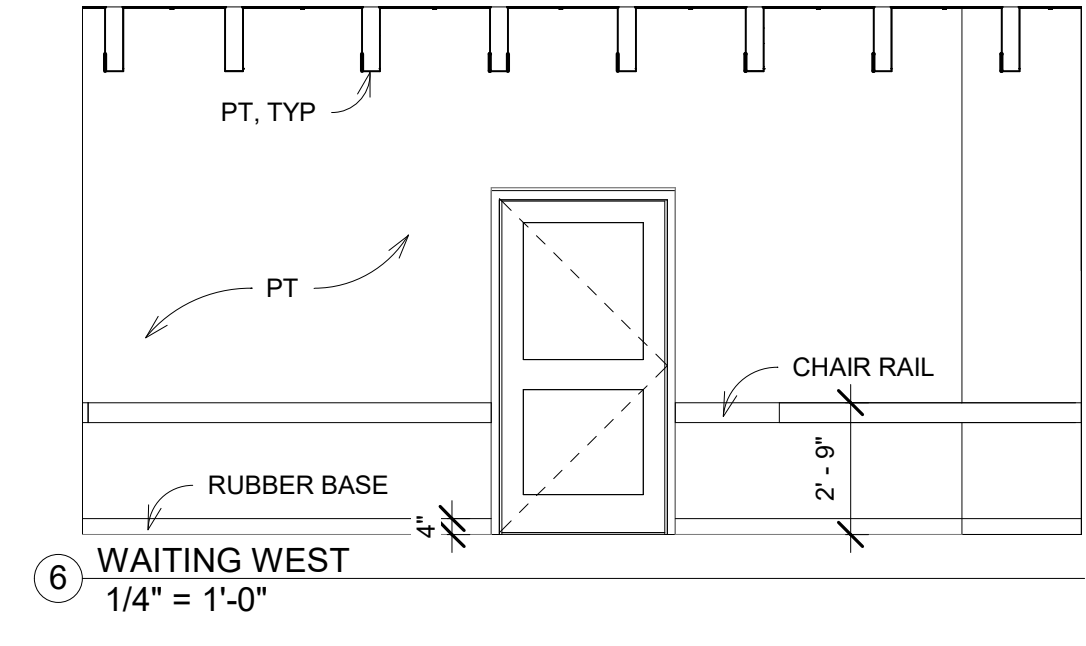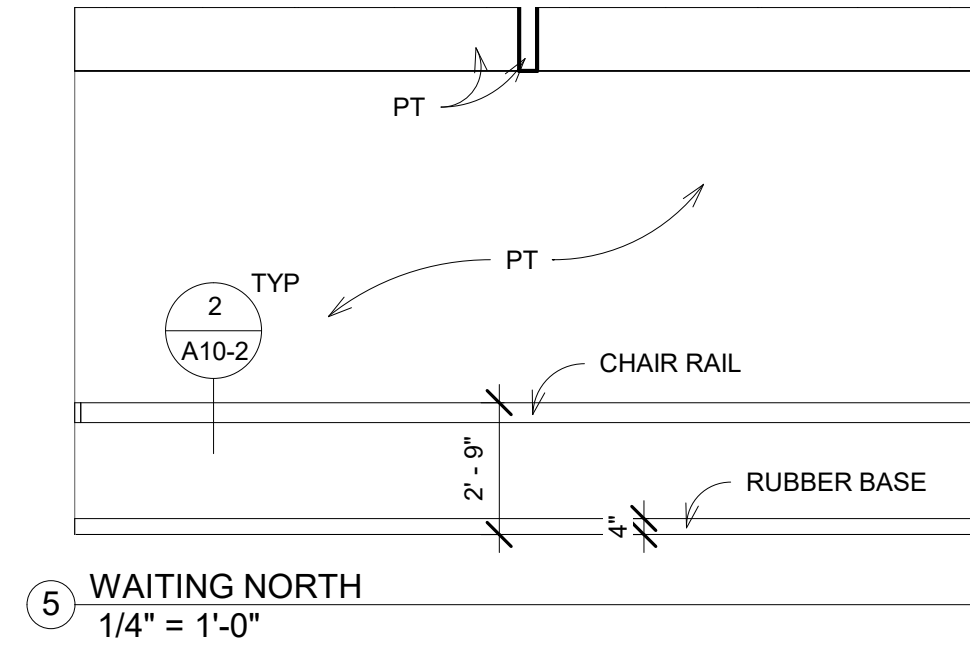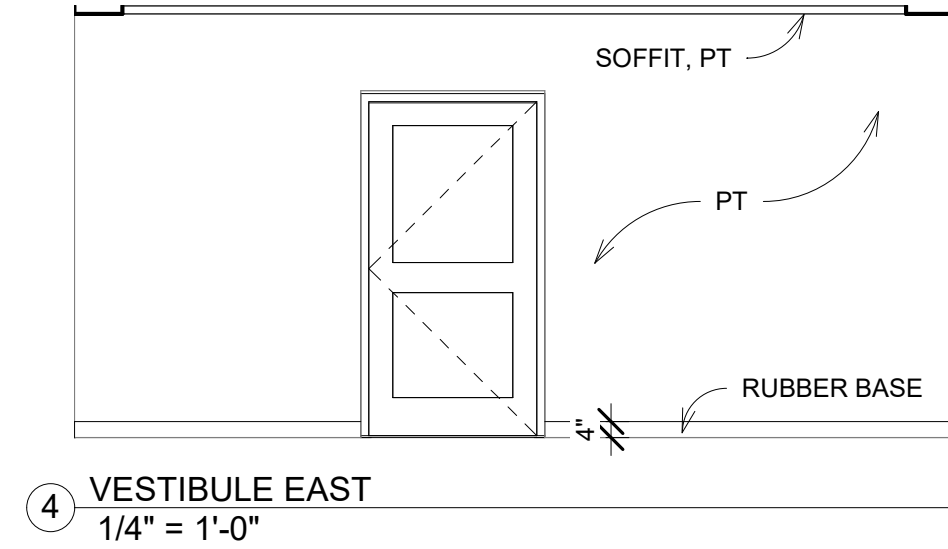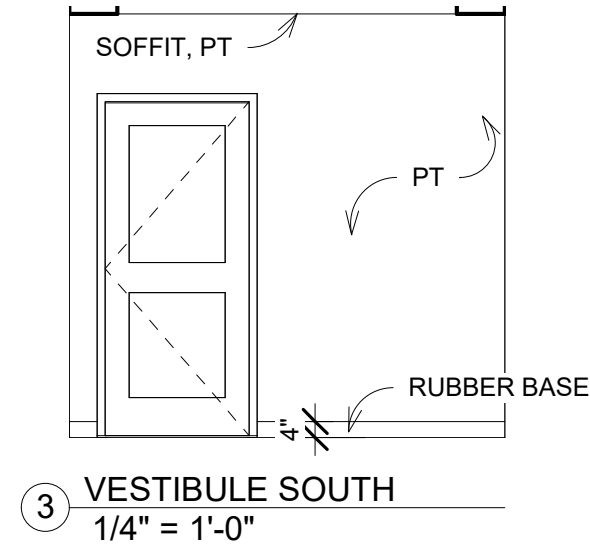

4.19.22

DATE


A REMODEL FOR:
BLUE LAKES URGENT CARE
1309 BLUE LAKES BLVD TWIN FALLS, ID
INTERIOR ELEVATIONS

Laughlin Ricks Architecture
architecture/planning
134 3RD AVE. E. * Twin Falls, Idaho 83301
PHONE: (208) 736-8050


DATE: 4.19.22

NM RCR
Drawn Checked


A8-0

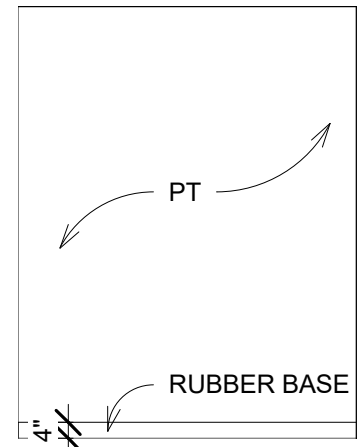


29 STORAGE NORTH
1/4" = 1'-0"

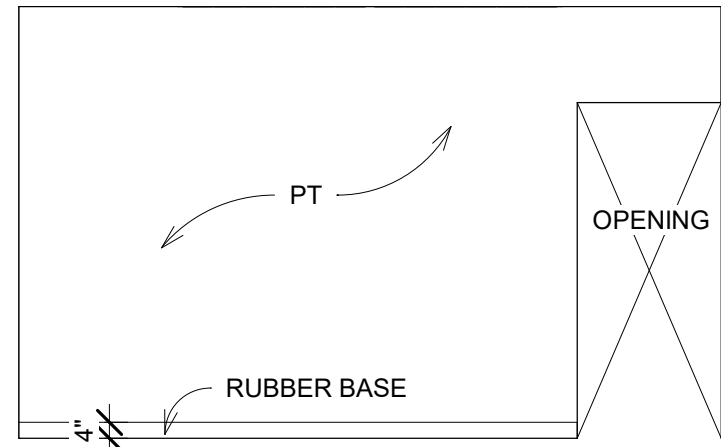


30 STORAGE EAST
1/4" = 1'-0"

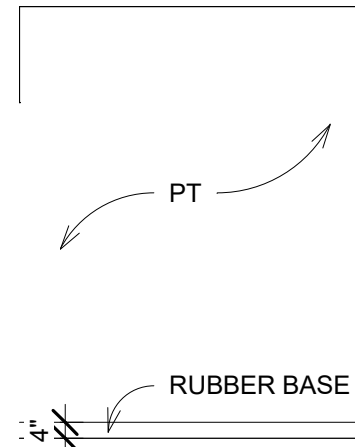


31 STORAGE SOUTH
1/4" = 1'-0"

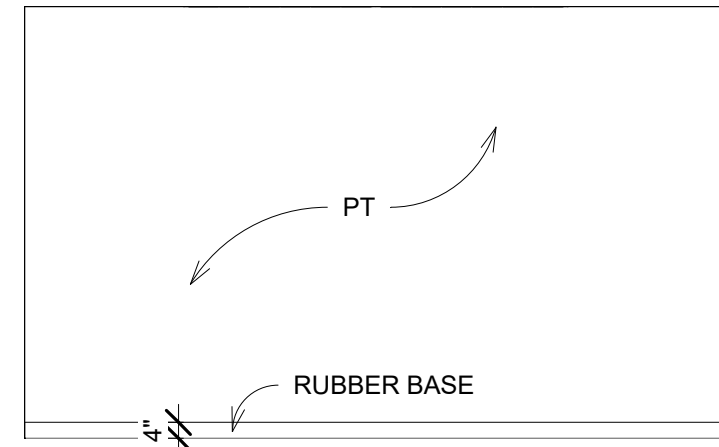


32 STORAGE WEST
1/4" = 1'-0"

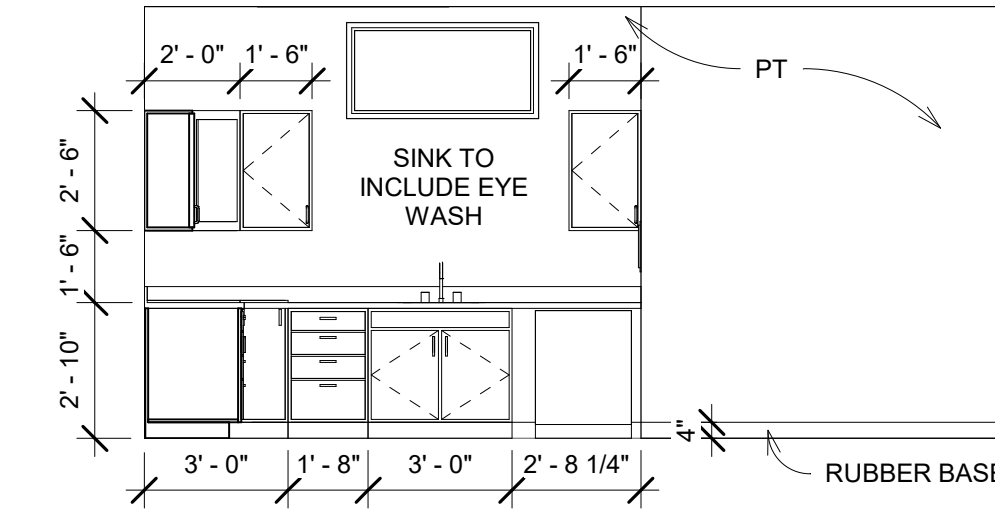


33 LAB NORTH
1/4" = 1'-0"

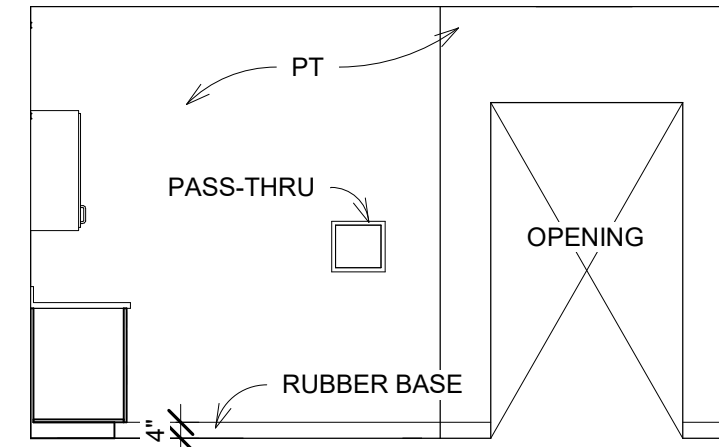


34 LAB EAST
1/4" = 1'-0"

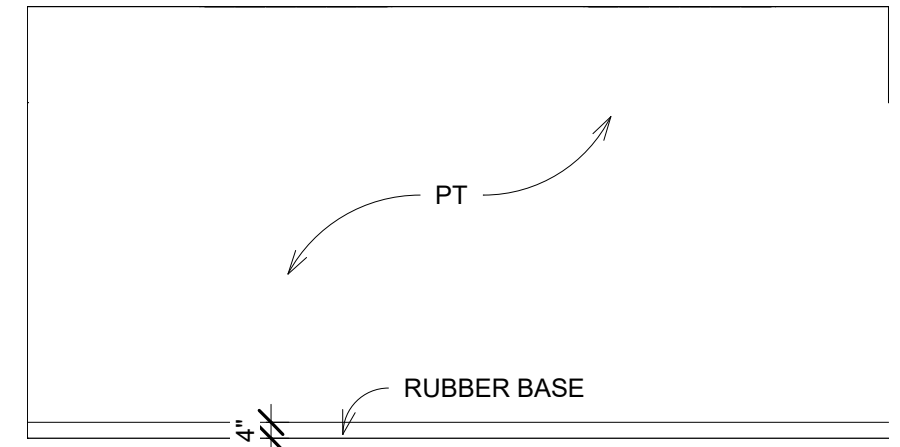


35 LAB SOUTH
1/4" = 1'-0"

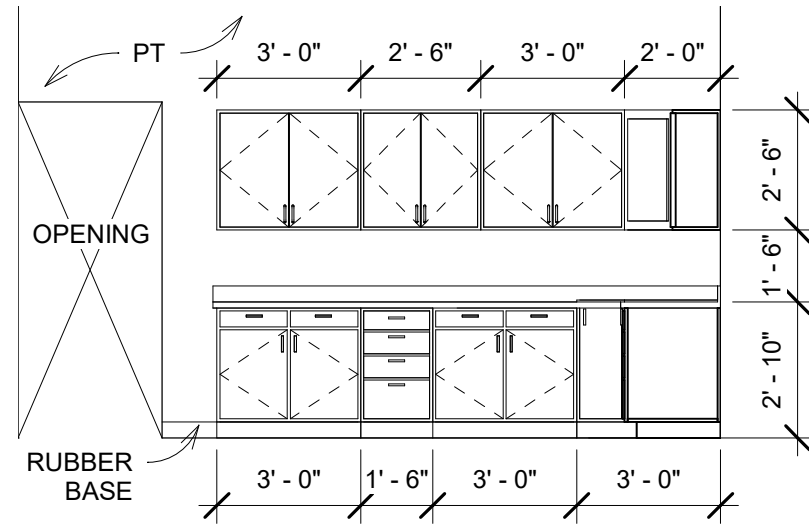


36 LAB WEST
1/4" = 1'-0"

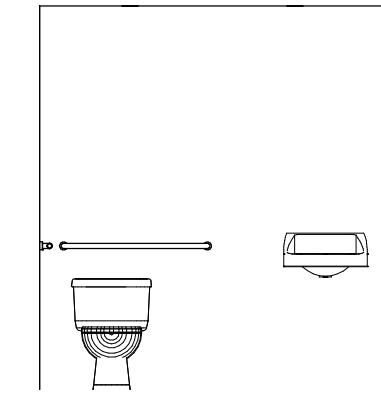


37 RR 1 NORTH
1/4" = 1'-0"

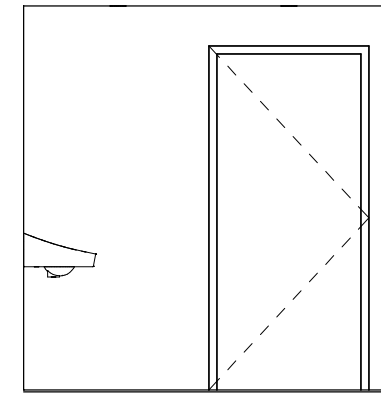


38 RR 1 EAST
1/4" = 1'-0"

 


39 RR 1 SOUTH
1/4" = 1'-0"

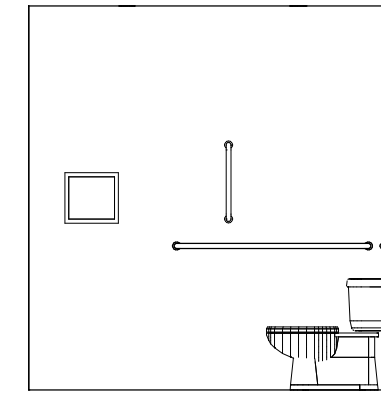


40 RR 1 WEST
1/4" = 1'-0"

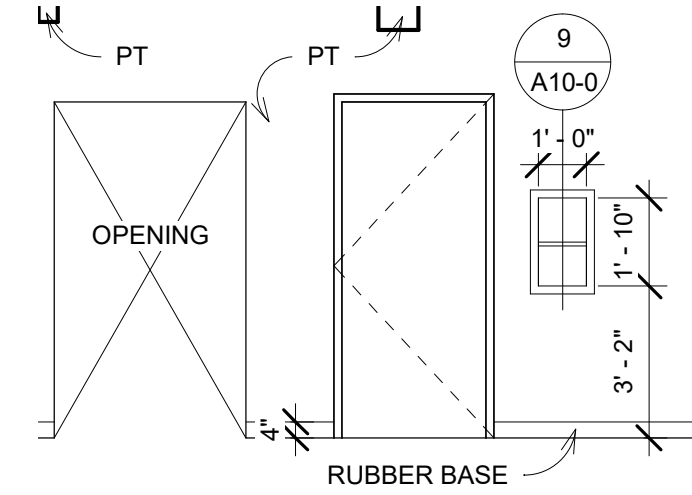


41 CORR 5 WEST
1/4" = 1'-0"

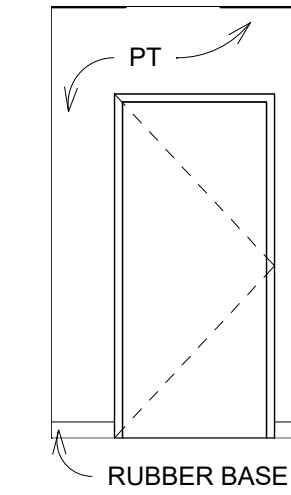


42 CORR 5 NORTH
1/4" = 1'-0"

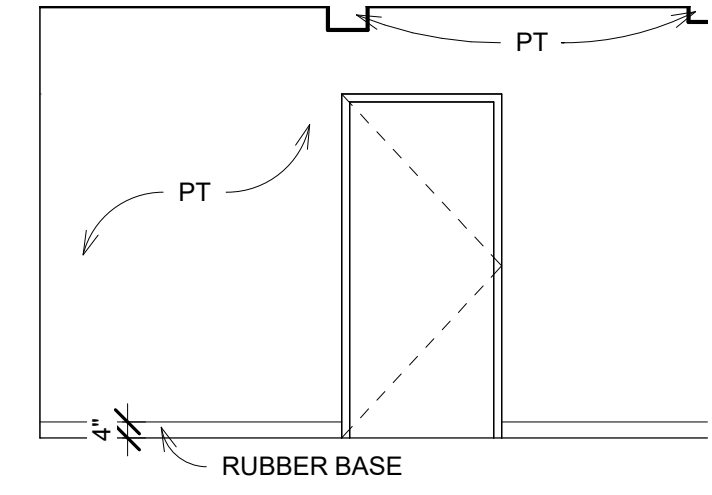


43 CORR 5 EAST
1/4" = 1'-0"

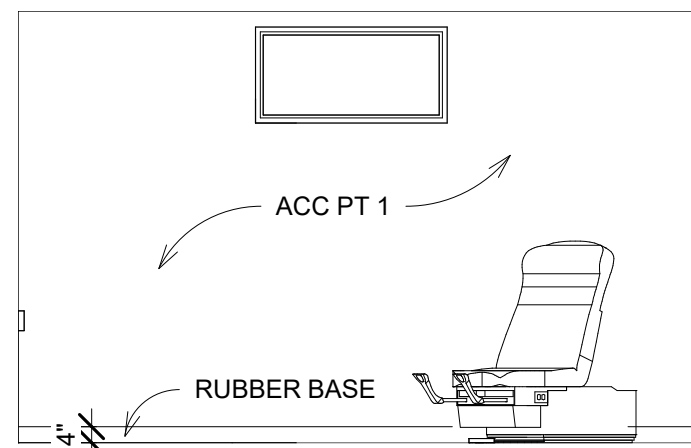


44 EXAM 5 NORTH
1/4" = 1'-0"

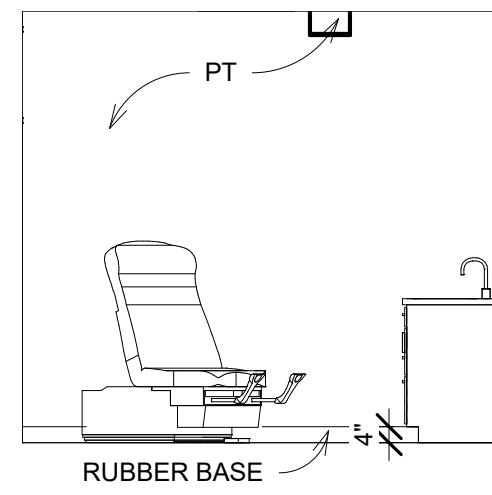


45 EXAM 5 EAST
1/4" = 1'-0"

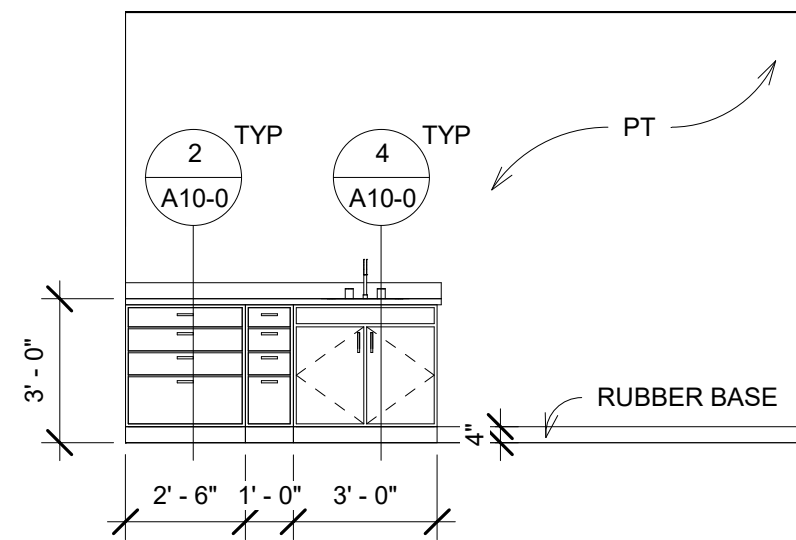


46 EXAM 5 SOUTH
1/4" = 1'-0"

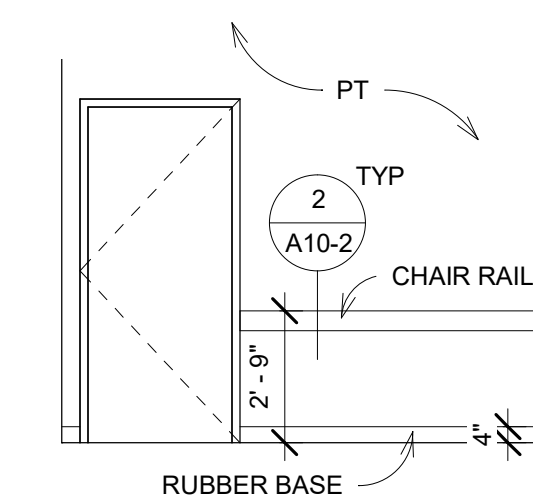


47 EXAM 5 WEST
1/4" = 1'-0"

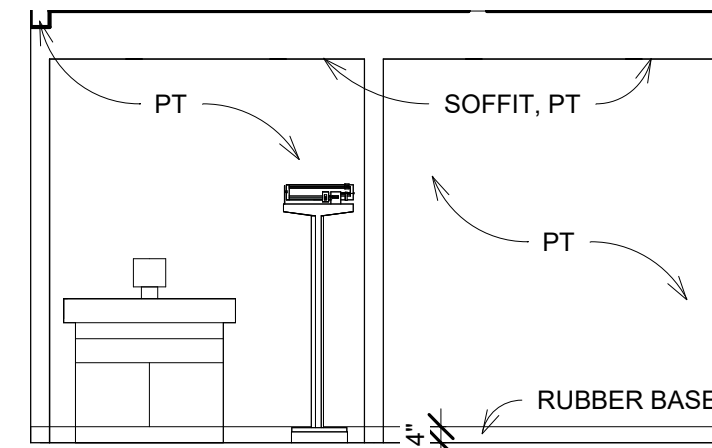


48 CORR 6 NORTH
1/4" = 1'-0"

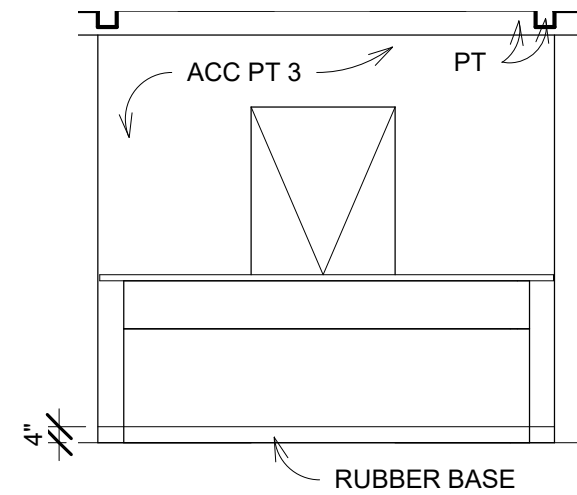


49 CORR 6 SOUTH
1/4" = 1'-0"

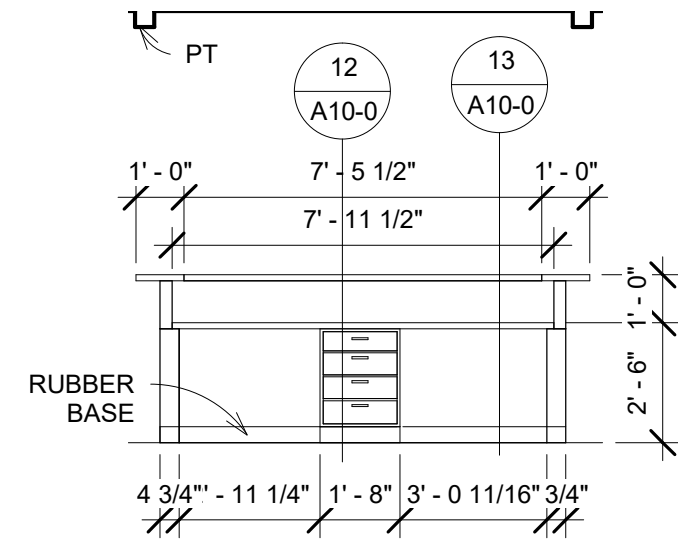


50 MEDICAL ASSISTANT
1/4" = 1'-0"

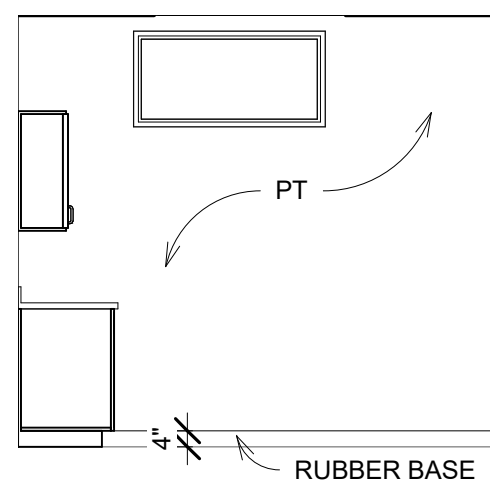


51 PROCEDURE NORTH
1/4" = 1'-0"

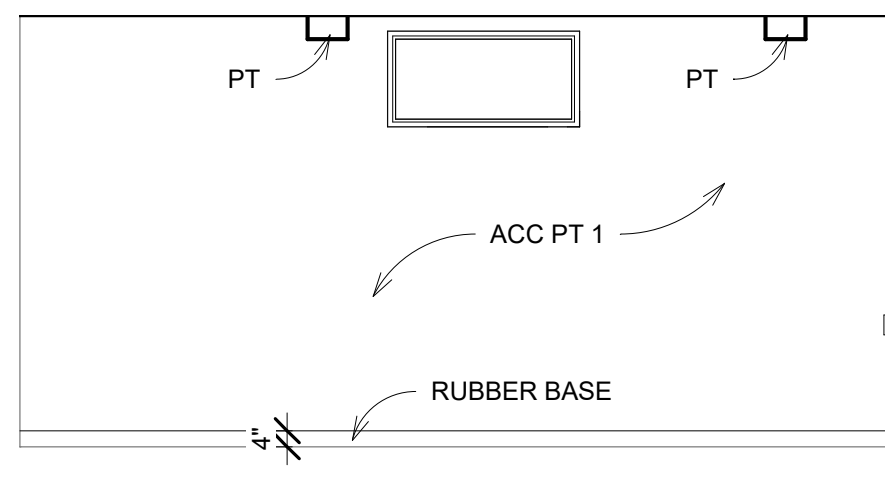


52 PROCEDURE EAST
1/4" = 1'-0"

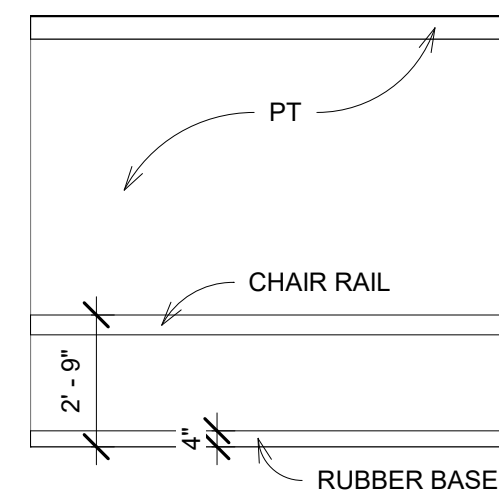


53 PROCEDURE SOUTH
1/4" = 1'-0"

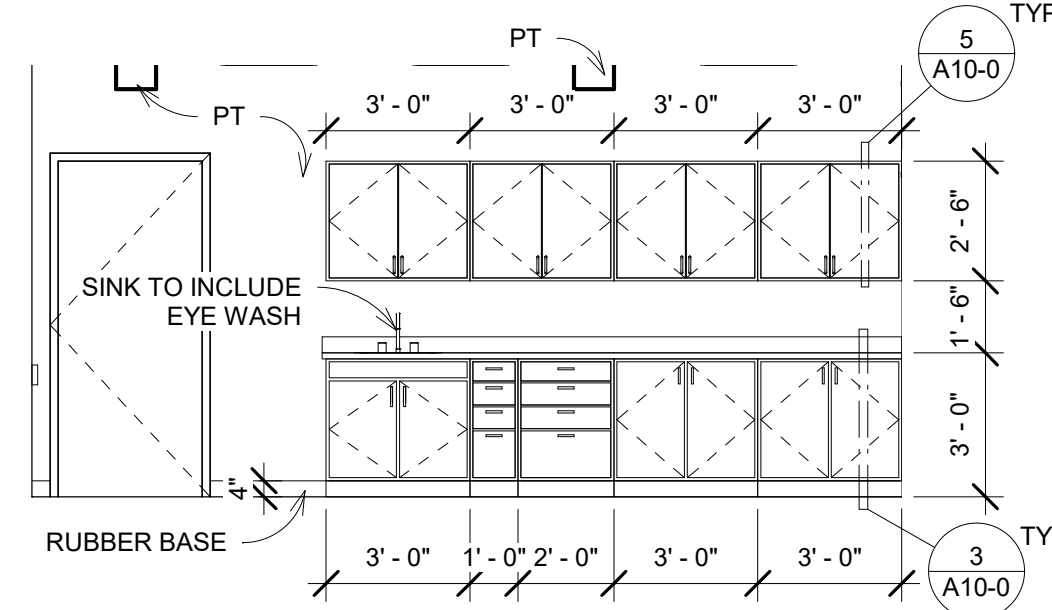


54 PROCEDURE WEST
1/4" = 1'-0"

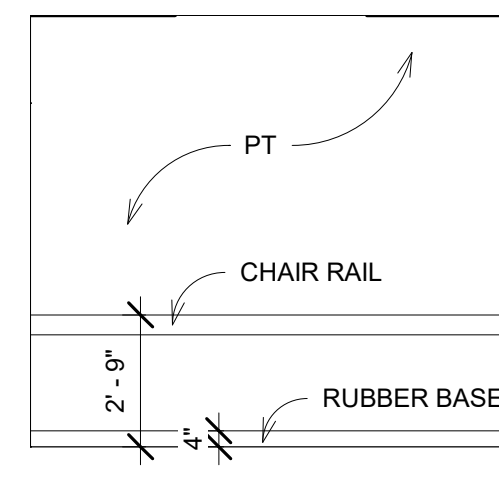


55 EXAM 6 NORTH
1/4" = 1'-0"

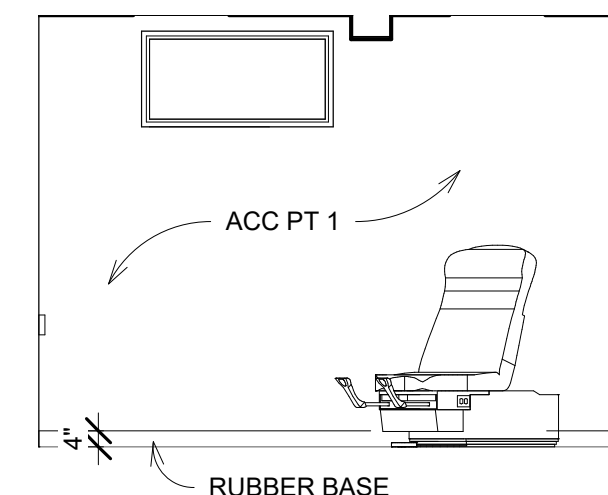


56 EXAM 6 EAST
1/4" = 1'-0"

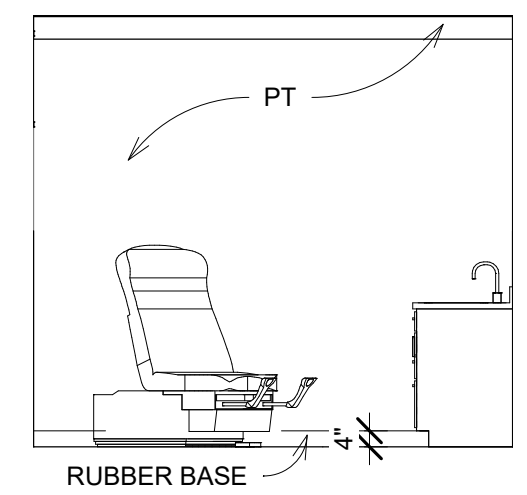


57 EXAM 6 SOUTH
1/4" = 1'-0"

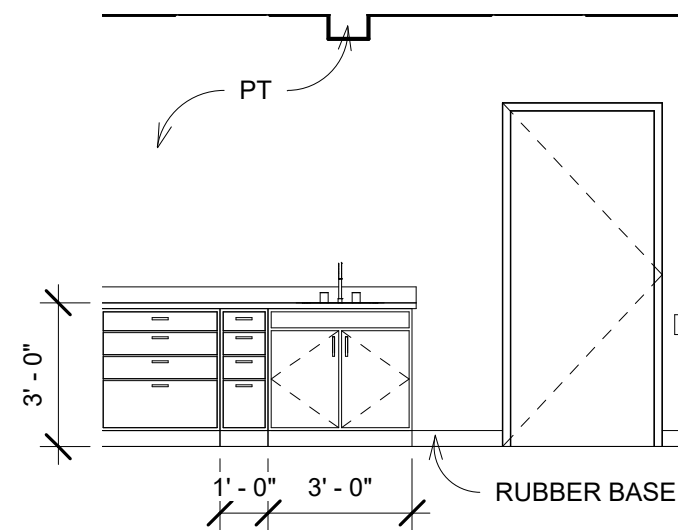


58 EXAM 6 WEST
1/4" = 1'-0"

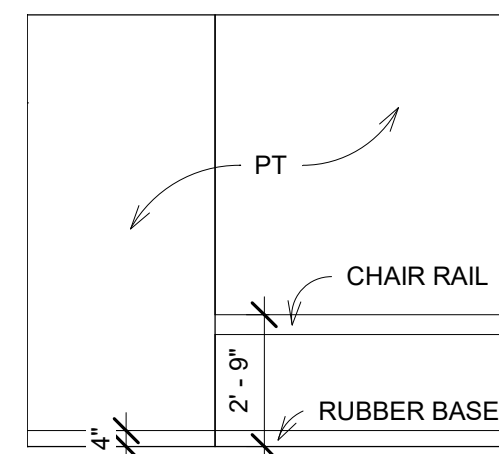


59 EXAM EKG NORTH
1/4" = 1'-0"

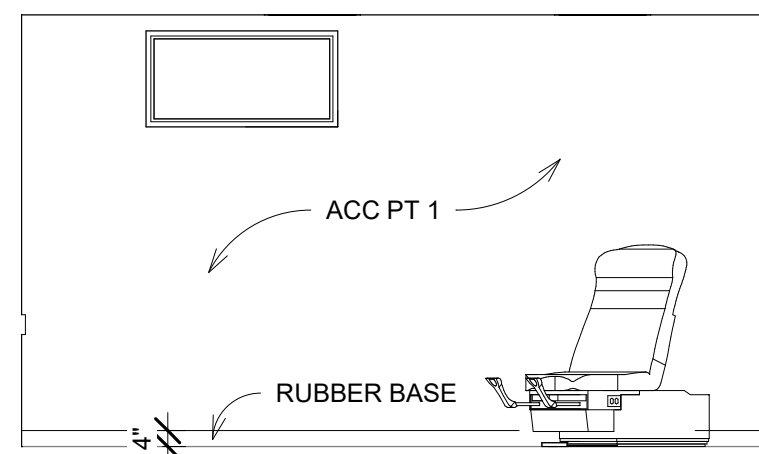

60 EXAM EKG EAST
1/4" = 1'-0"

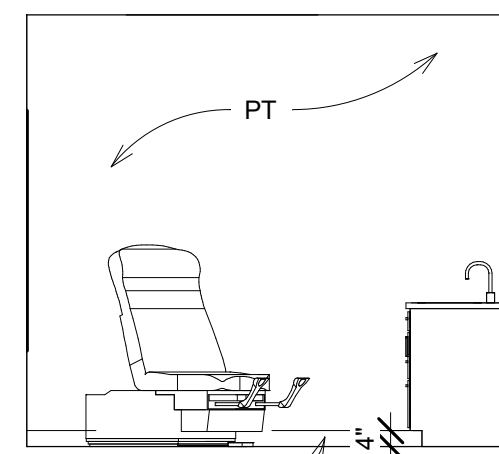

61 EXAM EKG SOUTH
1/4" = 1'-0"

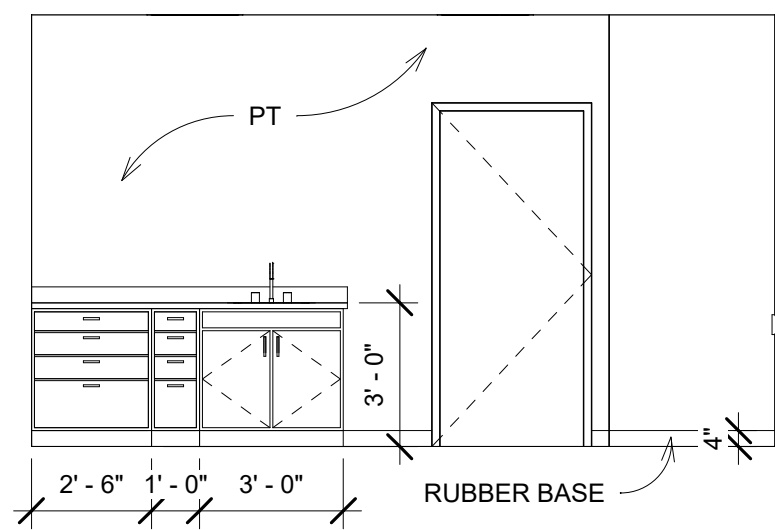

62 EXAM EKG WEST
1/4" = 1'-0"

4.19.22

DATE


A REMODEL FOR:
BLUE LAKES URGENT CARE
1309 BLUE LAKES BLVD TWIN FALLS, ID
INTERIOR ELEVATIONS

Laughlin Ricks Architecture
architecture/planning
134 3RD AVE. E. * Twin Falls, Idaho 83301
PHONE: (208) 736-8050


DATE: 4.19.22

NM RCR
Drawn Checked


A8-1

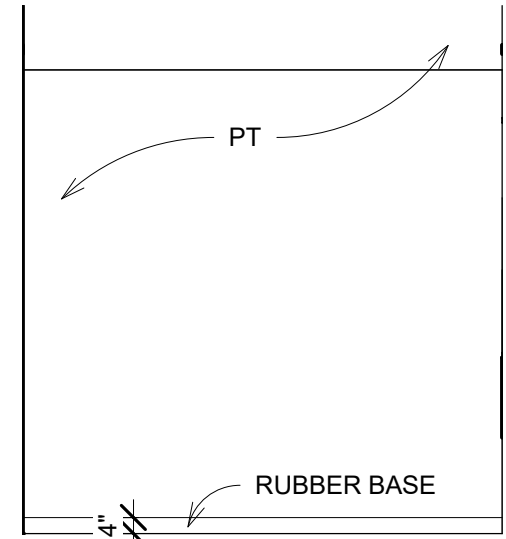


63 OFFICE 1 NORTH
1/4" = 1'-0"

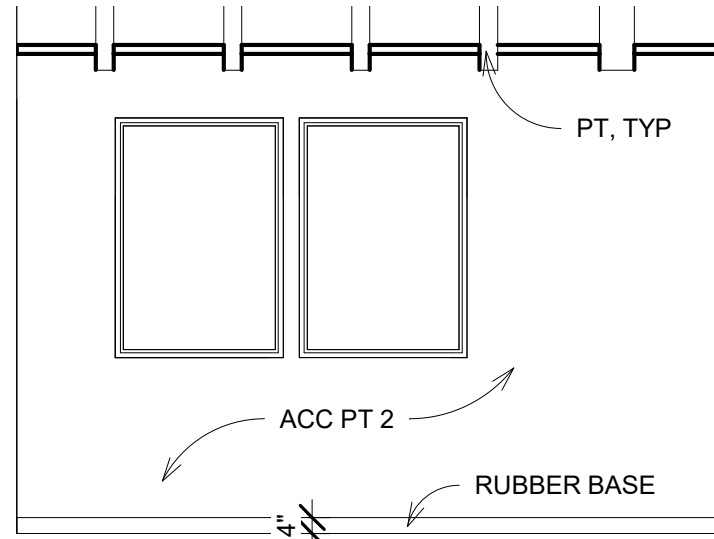


64 OFFICE 1 EAST
1/4" = 1'-0"

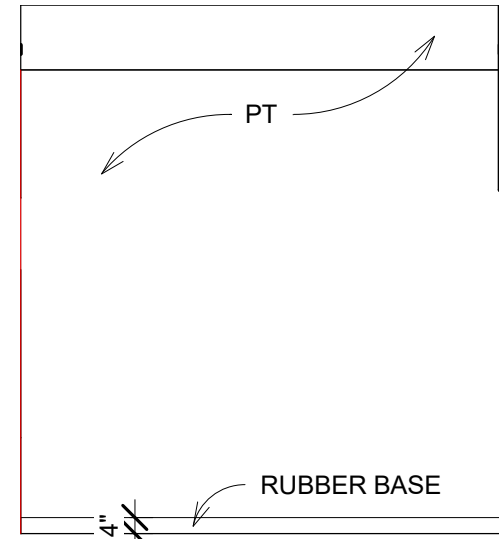


65 OFFICE 1 SOUTH
1/4" = 1'-0"

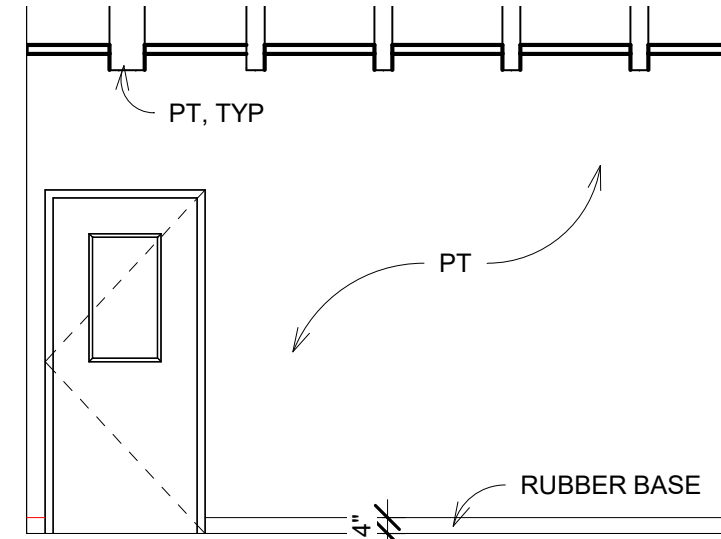


66 OFFICE 1 WEST
1/4" = 1'-0"

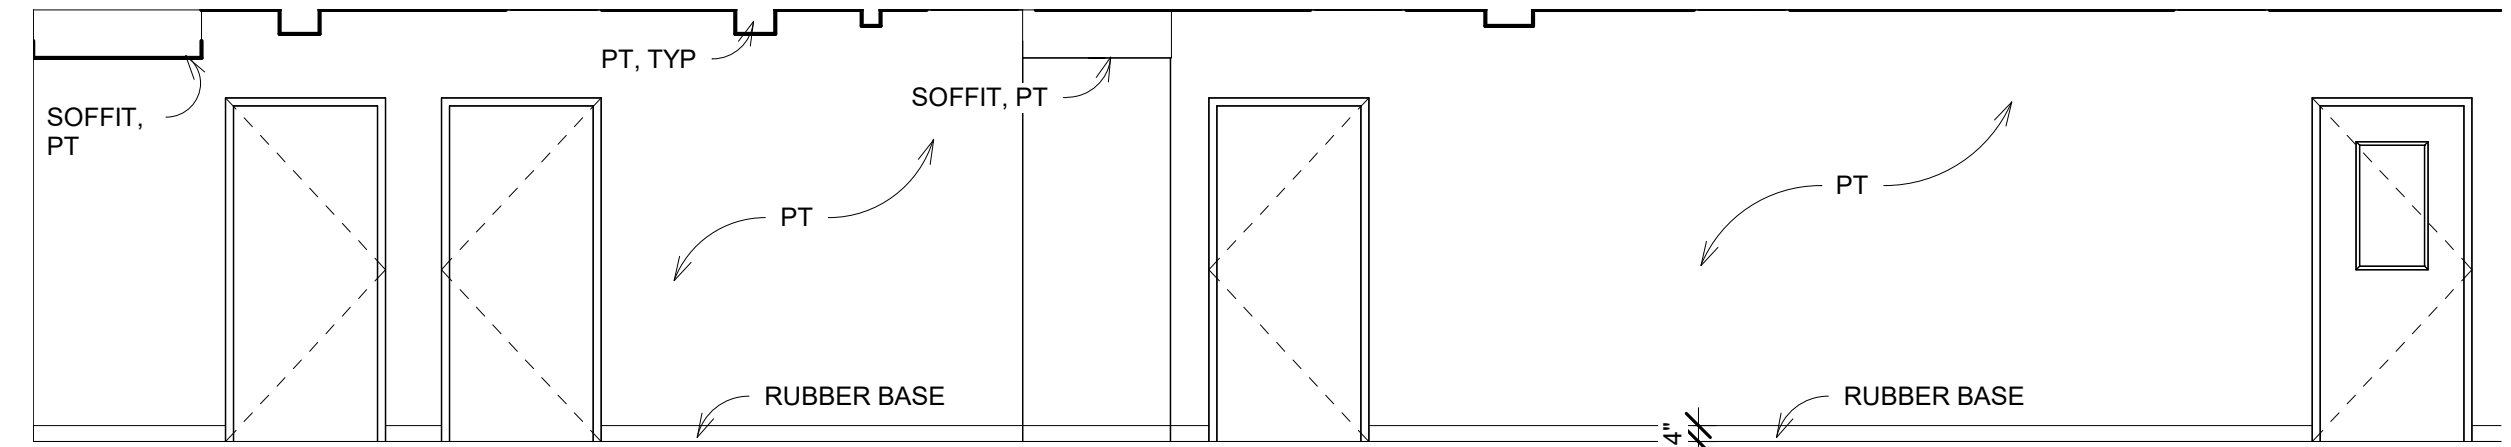


67 CORR 7 EAST
1/4" = 1'-0"

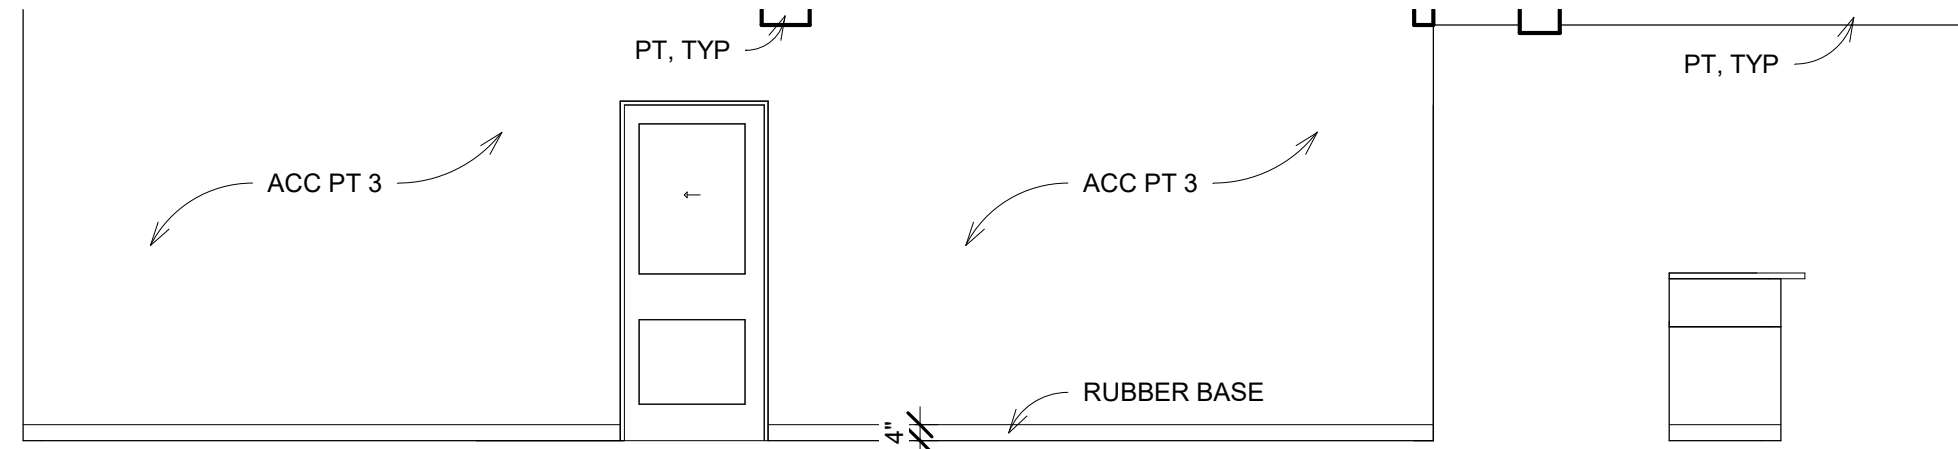


68 CORR 7 WEST
1/4" = 1'-0"

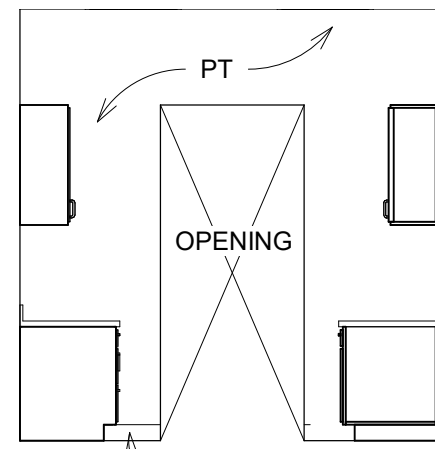


69 PROVIDERS NORTH
1/4" = 1'-0"

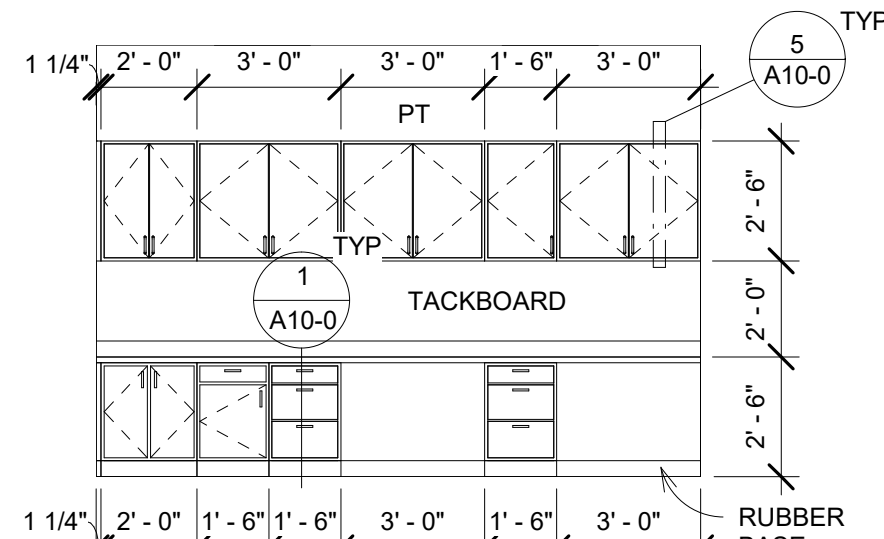


70 PROVIDERS EAST
1/4" = 1'-0"

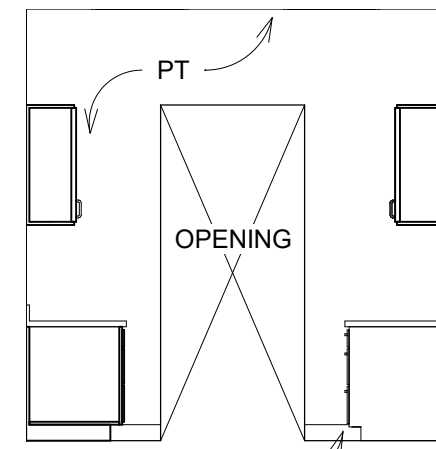


71 PROVIDERS SOUTH
1/4" = 1'-0"

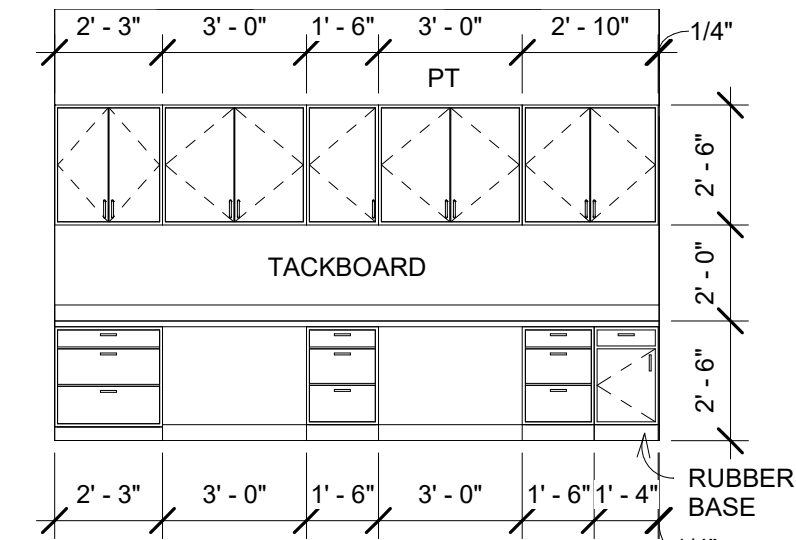


72 PROVIDERS WEST
1/4" = 1'-0"

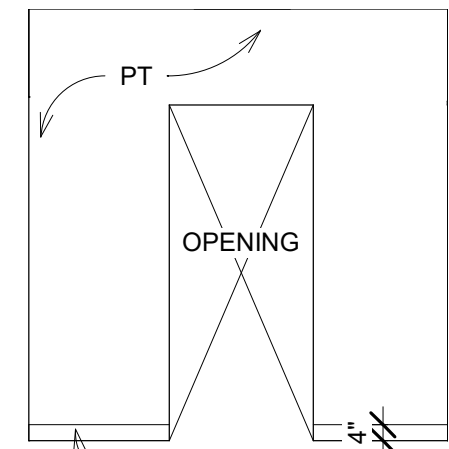


73 RECEPTION NORTH
1/4" = 1'-0"

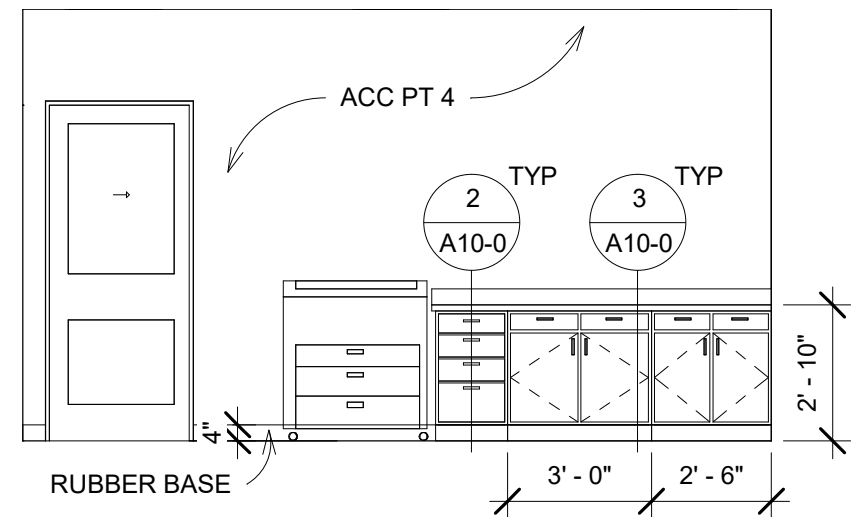


74 RECEPTION EAST
1/4" = 1'-0"

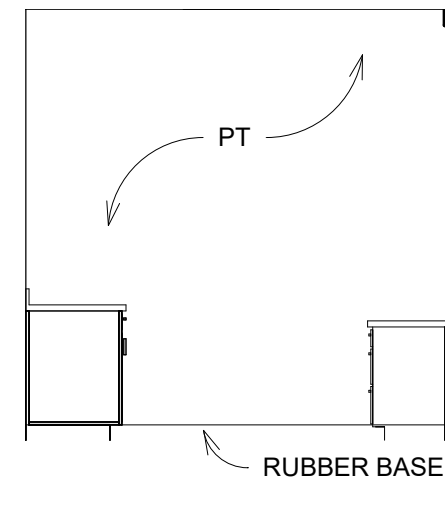


75 RECEPTION SOUTH
1/4" = 1'-0"

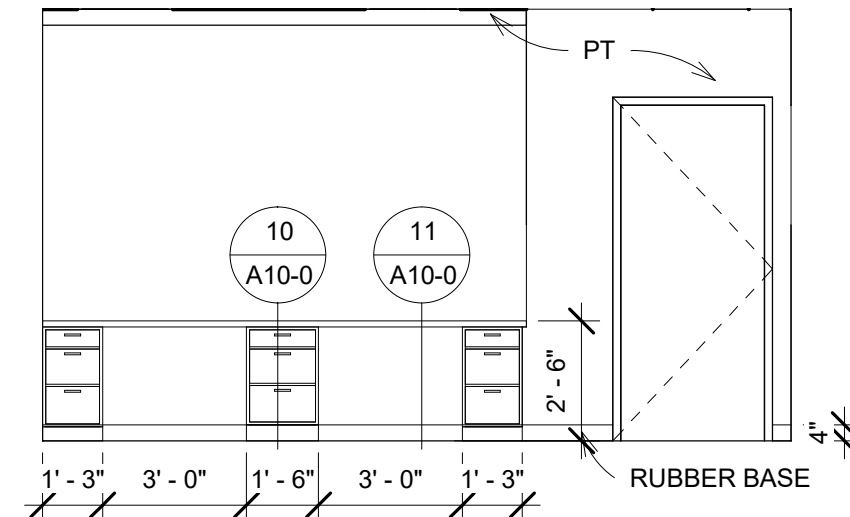


76 RECEPTION WEST
1/4" = 1'-0"

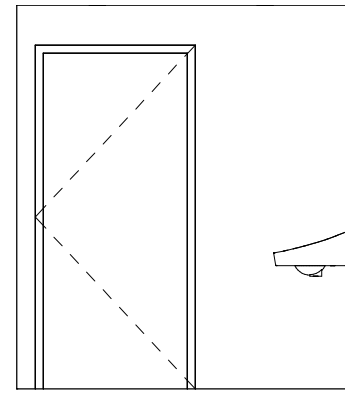


77 RR 2 NORTH
1/4" = 1'-0"

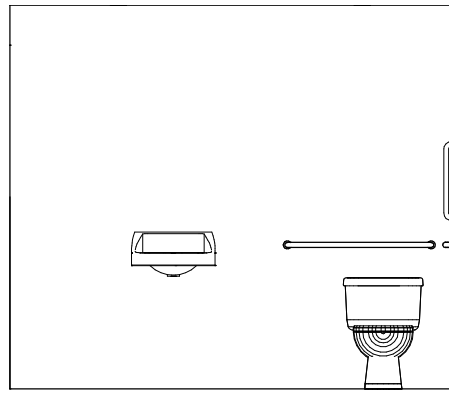


78 RR 2 EAST
1/4" = 1'-0"

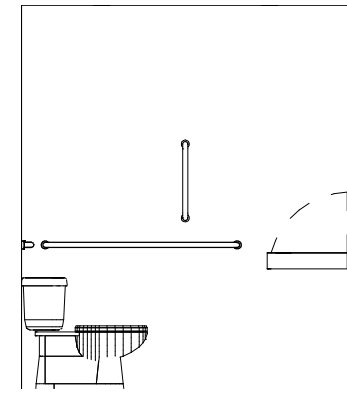


79 RR 2 SOUTH
1/4" = 1'-0"

 


80 RR 2 WEST
1/4" = 1'-0"

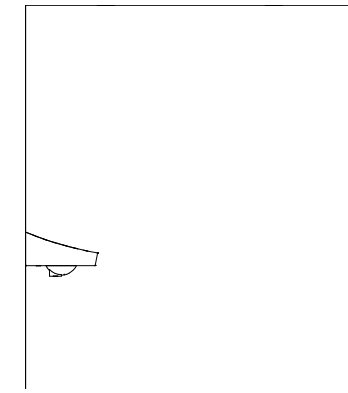


81 RR 3 NORTH
1/4" = 1'-0"

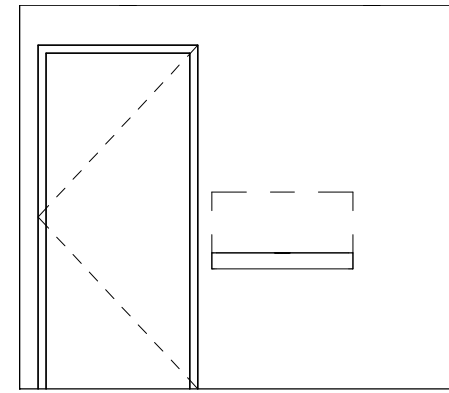


82 RR 3 EAST
1/4" = 1'-0"

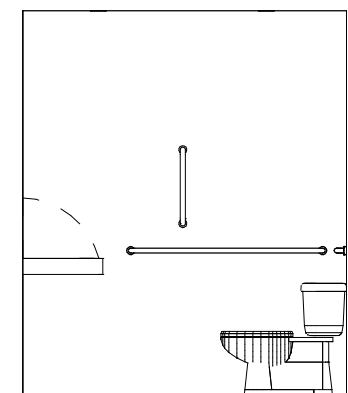


83 RR 3 SOUTH
1/4" = 1'-0"

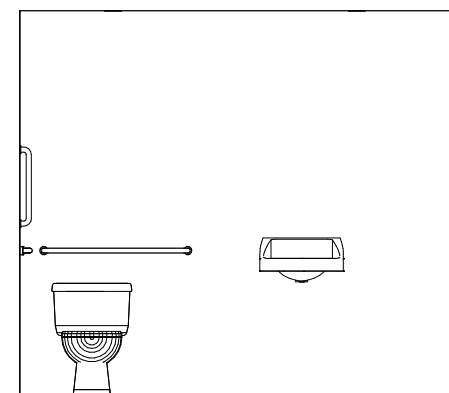


84 RR 3 WEST
1/4" = 1'-0"

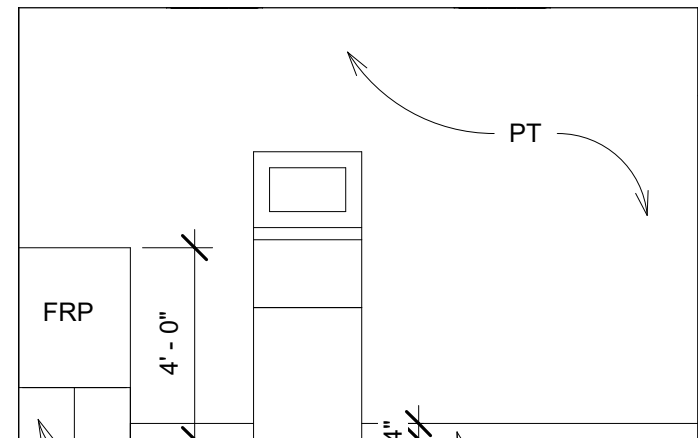


85 UTILITY NORTH
1/4" = 1'-0"

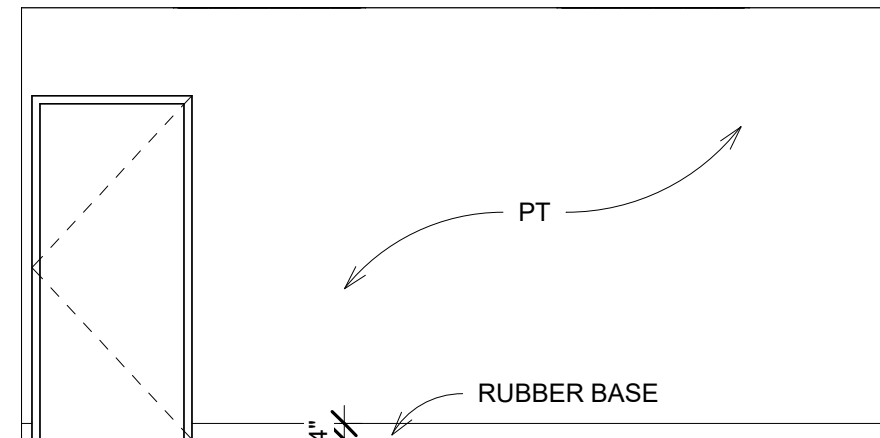


86 UTILITY EAST
1/4" = 1'-0"

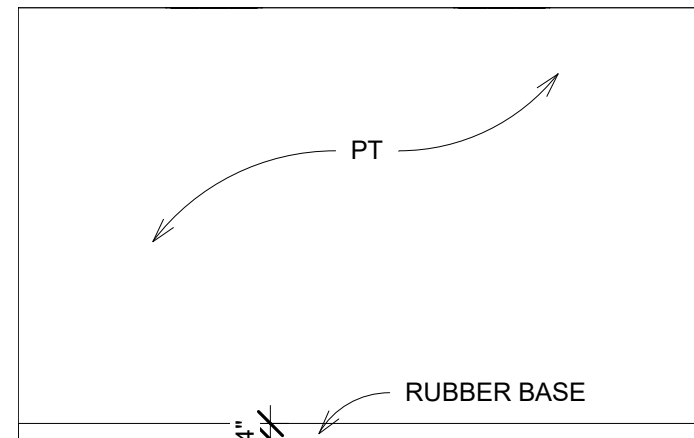


87 UTILITY SOUTH
1/4" = 1'-0"

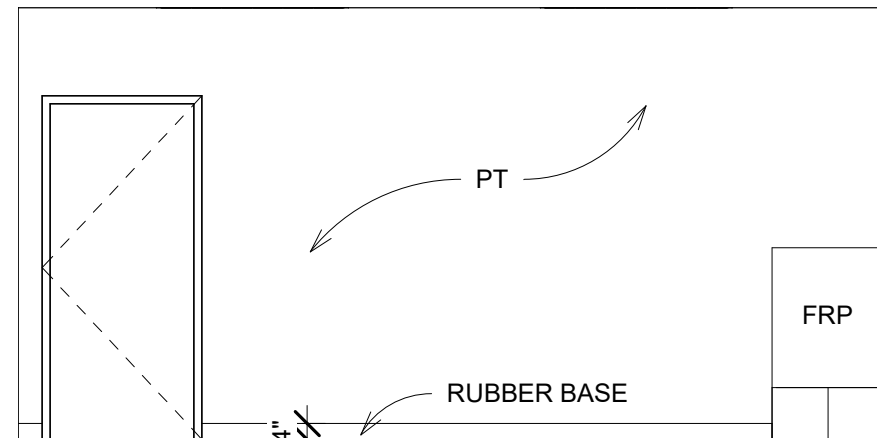


88 UTILITY WEST
1/4" = 1'-0"

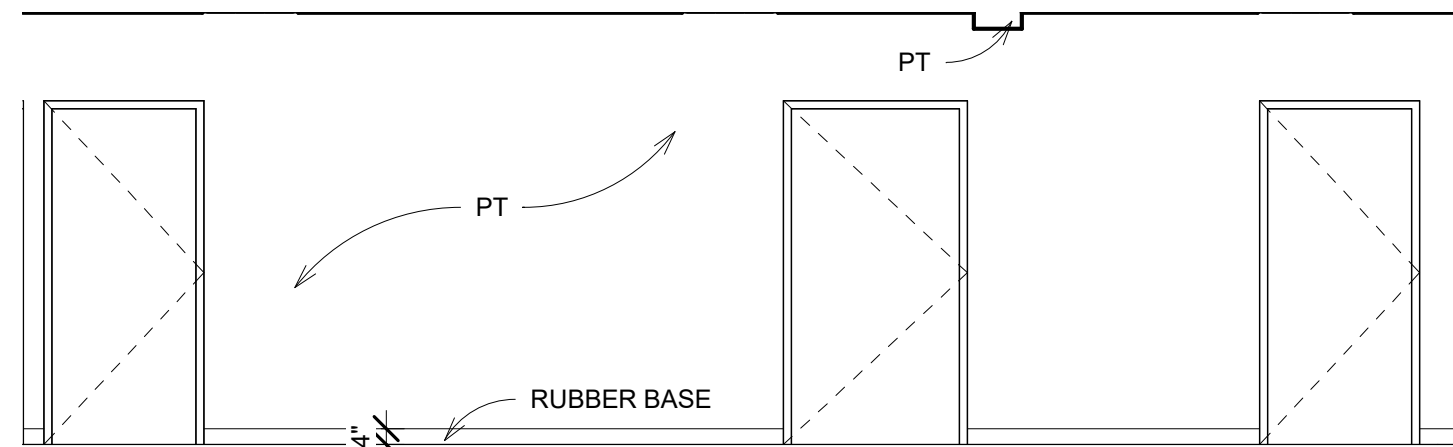

89 CORR 8 WEST
1/4" = 1'-0"

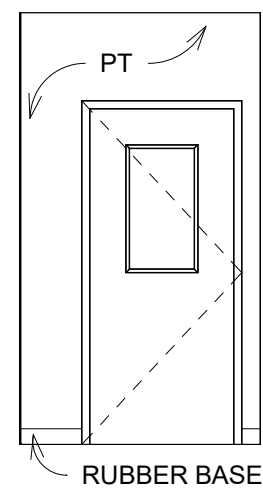

90 CORR 8 SOUTH
1/4" = 1'-0"

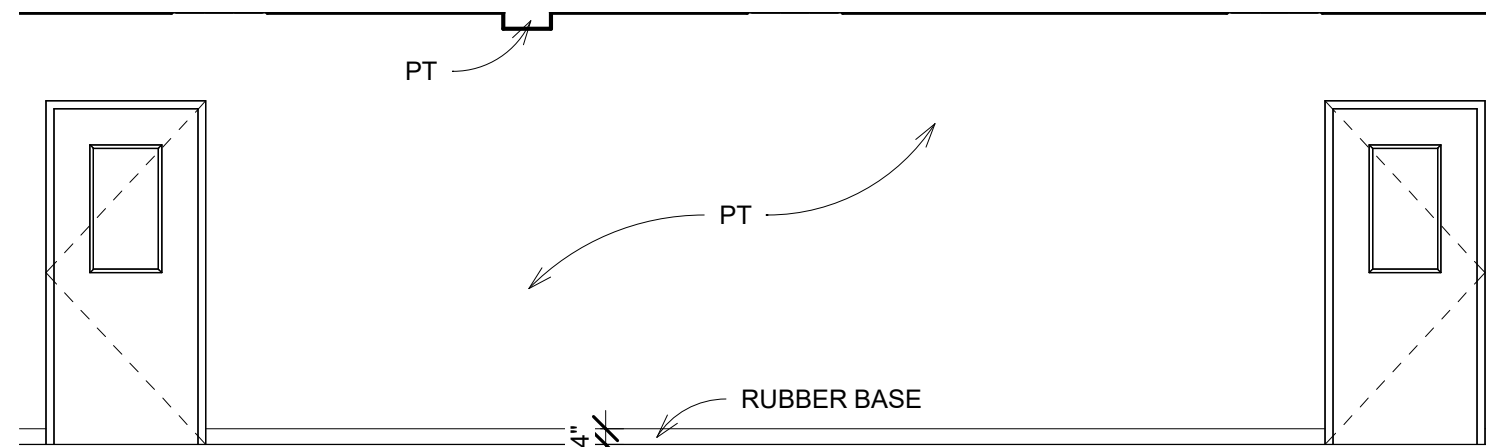

91 CORR 8 EAST
1/4" = 1'-0"

4.19.22

DATE


A REMODEL FOR:
BLUE LAKES URGENT CARE
1309 BLUE LAKES BLVD TWIN FALLS, ID
INTERIOR ELEVATIONS

Laughlin Ricks Architecture
architecture/planning
134 3RD AVE. E. * Twin Falls, Idaho 83301
PHONE: (208) 736-8050


DATE: 4.19.22

NM RCR
Drawn Checked


A8-2

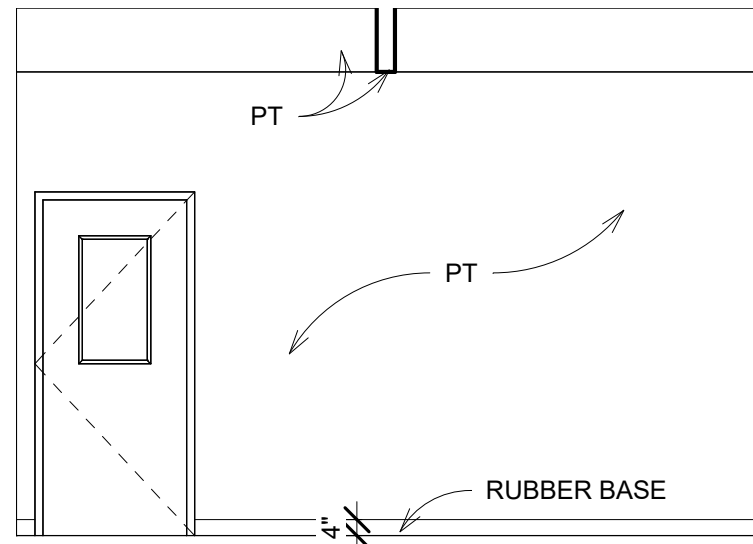


92 CONFERENCE NORTH
1/4" = 1'-0"

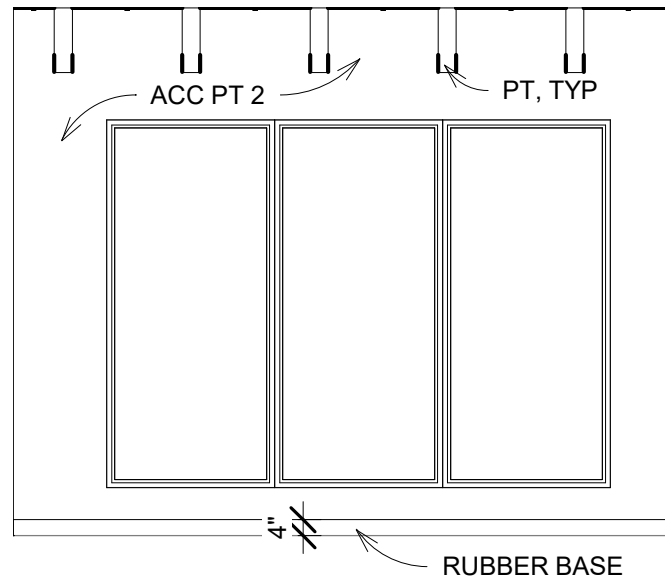


93 CONFERENCE EAST
1/4" = 1'-0"

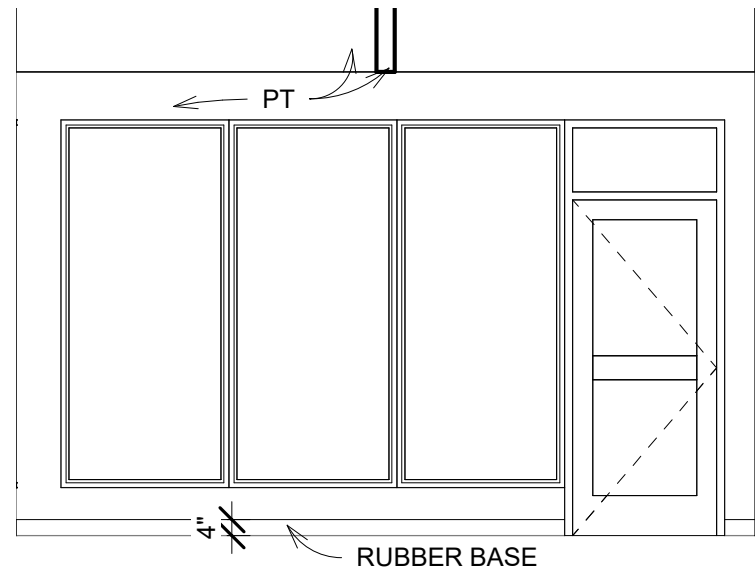


94 CONFERENCE SOUTH
1/4" = 1'-0"

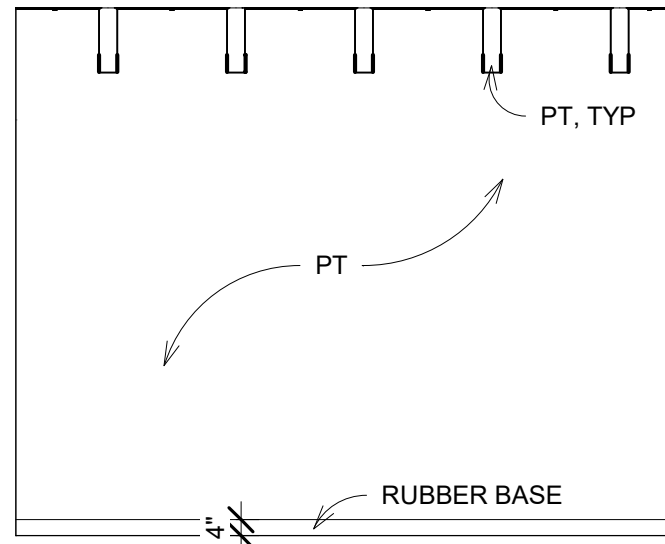


95 CONFERENCE WEST
1/4" = 1'-0"

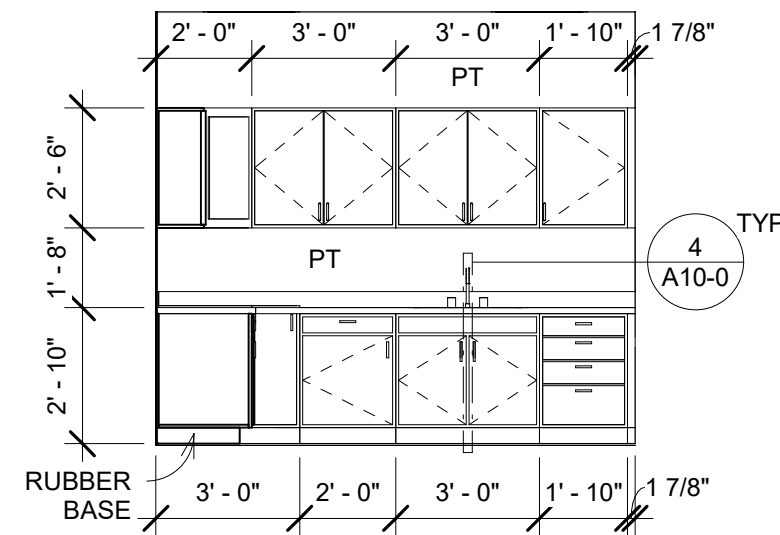


96 BREAKROOM NORTH
1/4" = 1'-0"

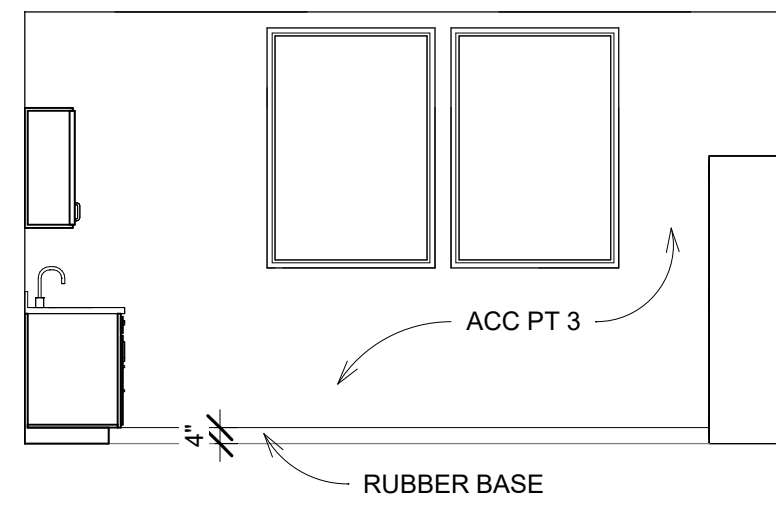


97 BREAKROOM EAST
1/4" = 1'-0"

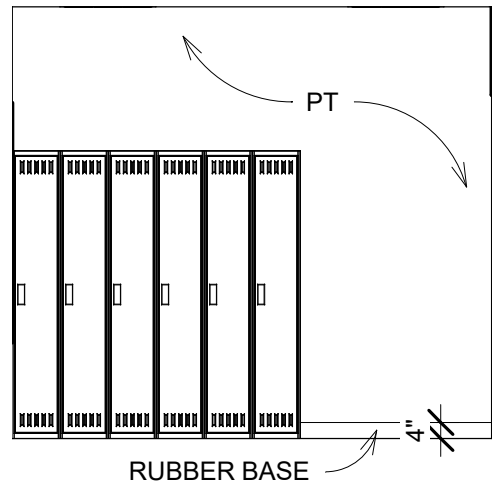


98 BREAKROOM SOUTH
1/4" = 1'-0"

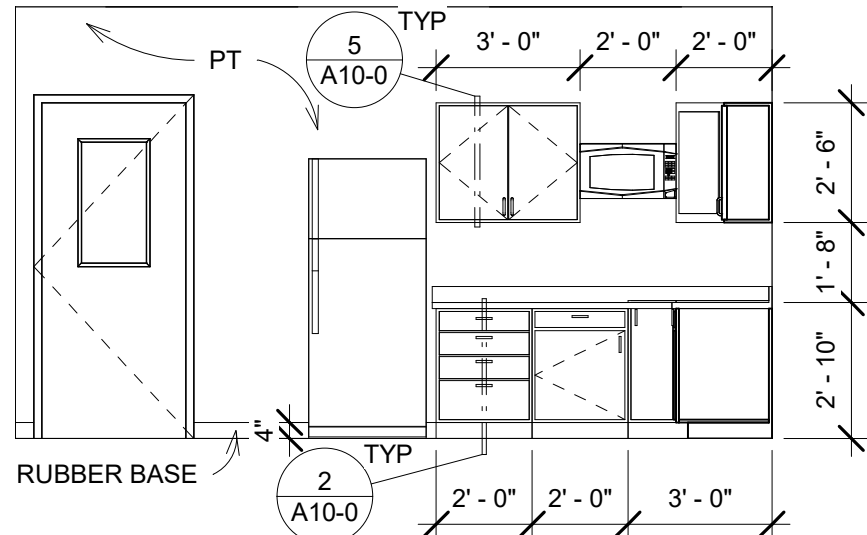


99 BREAKROOM WEST
1/4" = 1'-0"

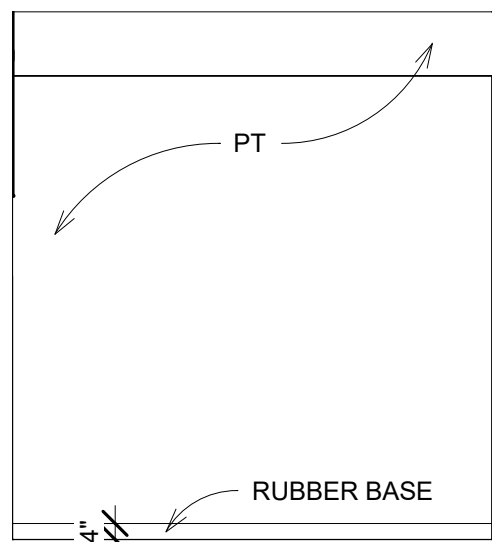


100 OFFICE 2 NORTH
1/4" = 1'-0"

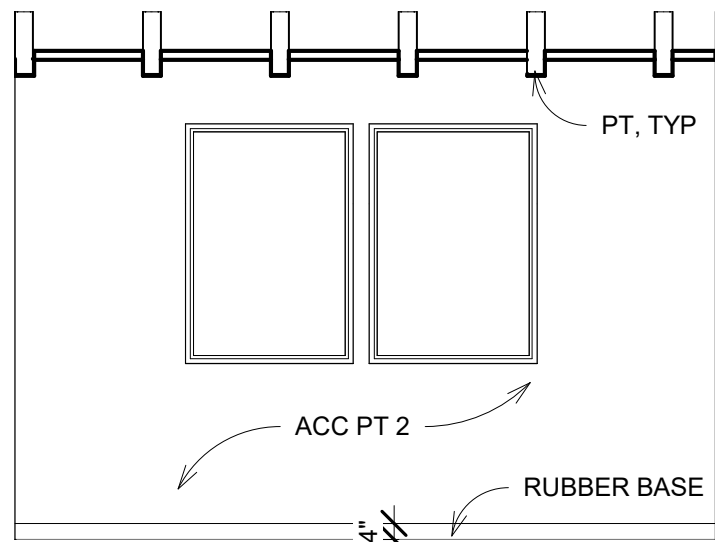


101 OFFICE 2 EAST
1/4" = 1'-0"

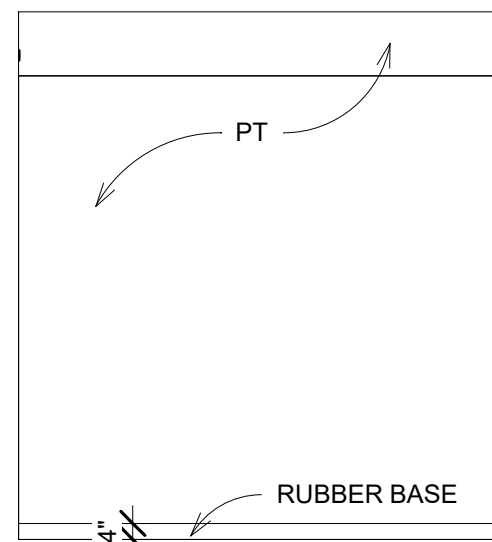


102 OFFICE 2 SOUTH
1/4" = 1'-0"

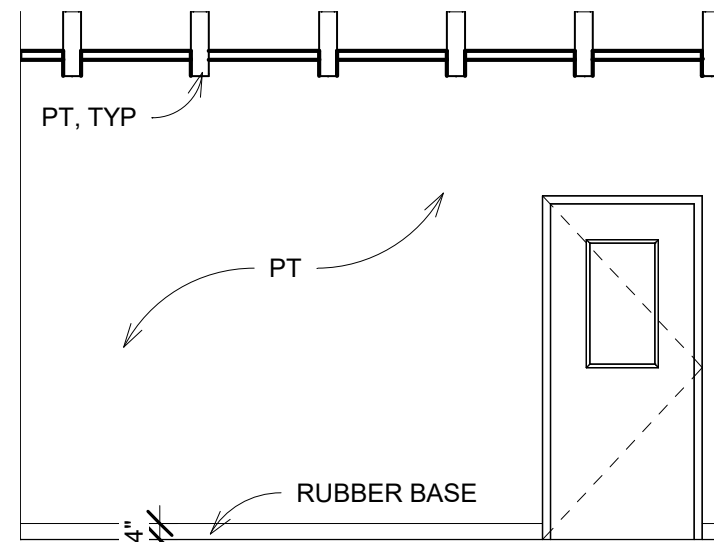


103 OFFICE 2 WEST
1/4" = 1'-0"

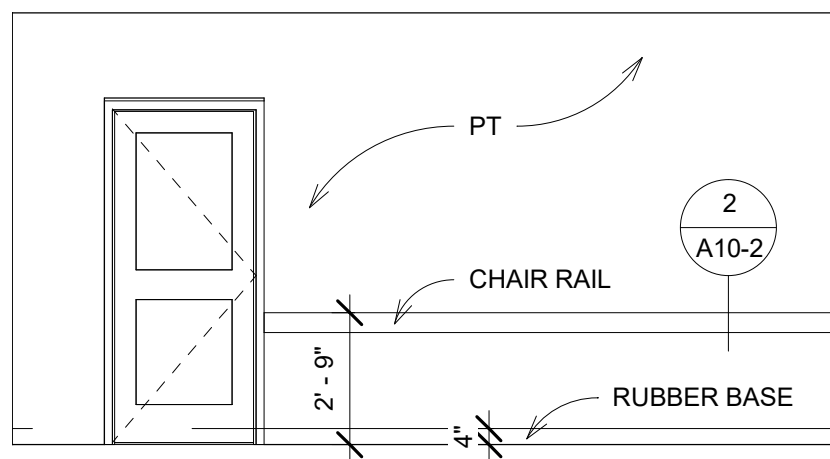


104 PHARMACY WAIT NORTH 1
1/4" = 1'-0"

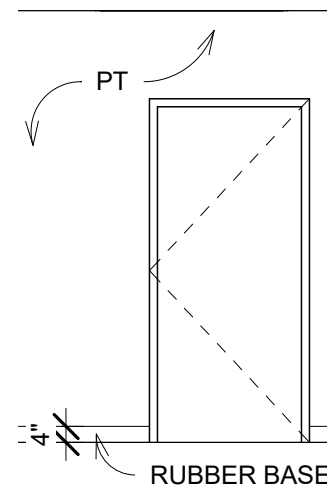


105 PHARMACY WAIT SOUTH 1
1/4" = 1'-0"

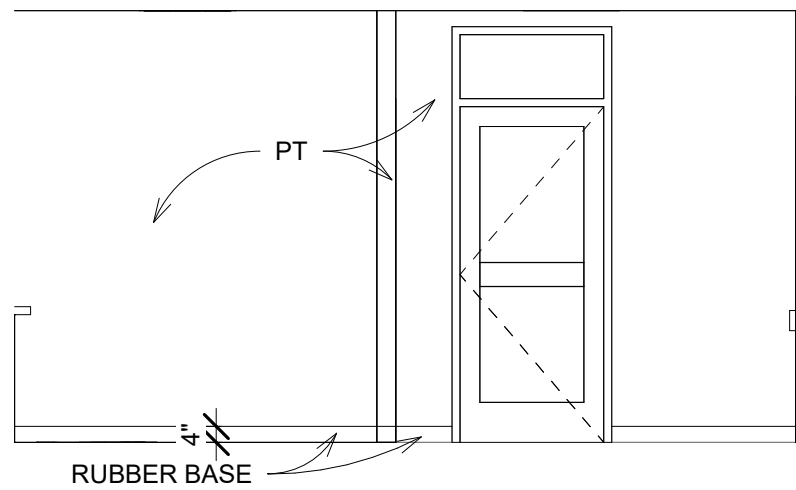


106 PHARMACY WAIT WEST
1/4" = 1'-0"

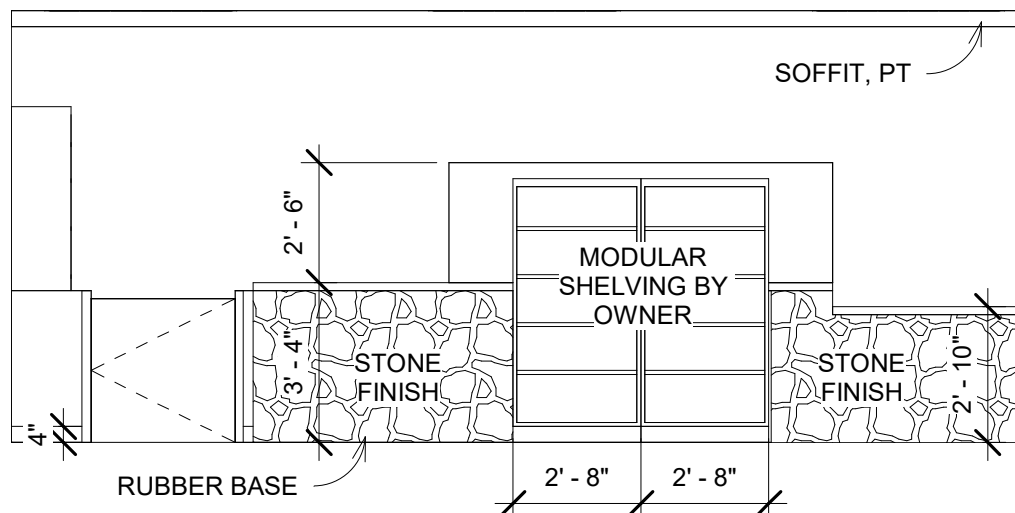


107 PHARMACY WAIT SOUTH 2
1/4" = 1'-0"

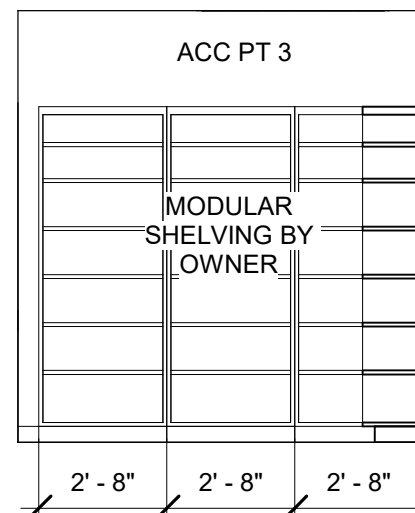


108 PHARMACY WAIT NORTH 2
1/4" = 1'-0"

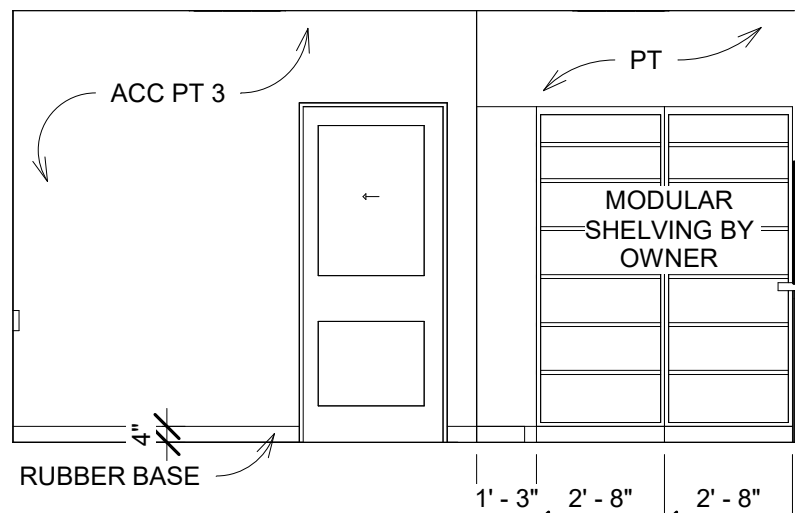


109 PHARMACY WAIT EAST
1/4" = 1'-0"

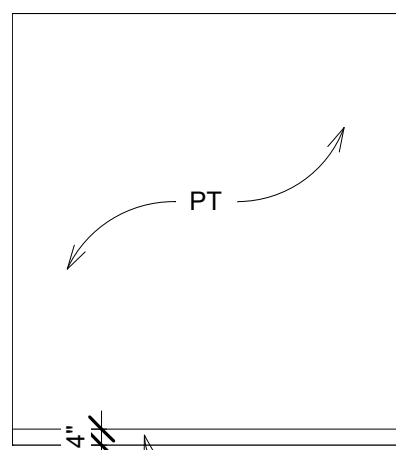


110 OFFICE NORTH
1/4" = 1'-0"

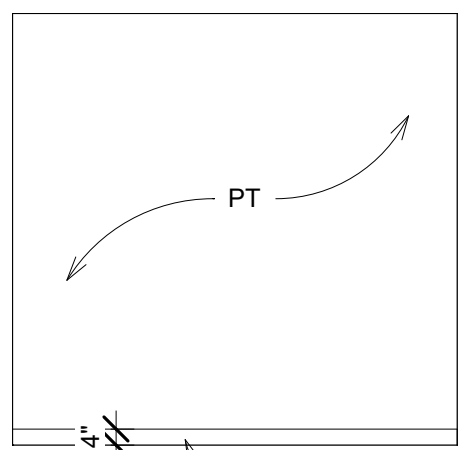


111 OFFICE EAST
1/4" = 1'-0"

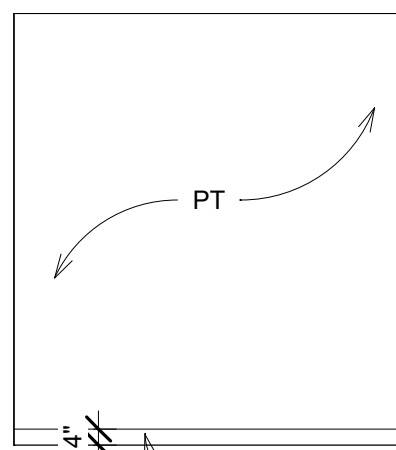


112 OFFICE SOUTH
1/4" = 1'-0"

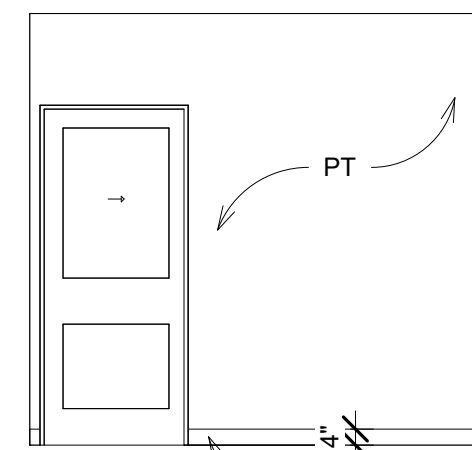


113 OFFICE WEST
1/4" = 1'-0"

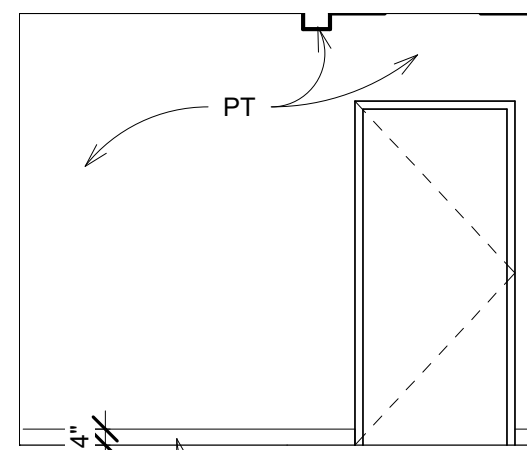


114 CONSULT NORTH
1/4" = 1'-0"

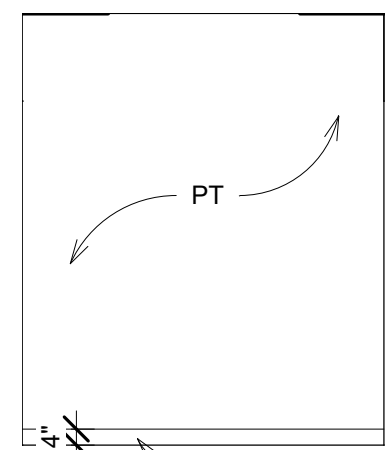


115 CONSULT EAST
1/4" = 1'-0"

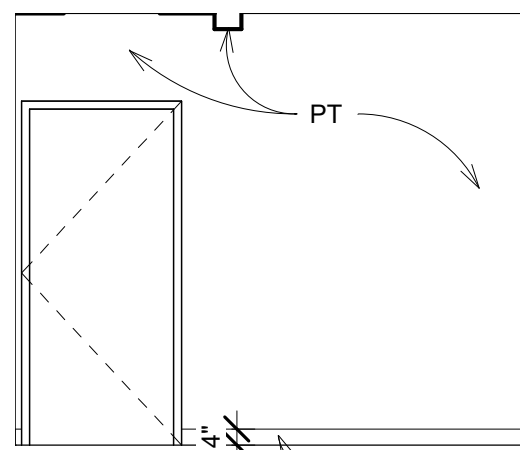


116 CONSULT SOUTH
1/4" = 1'-0"

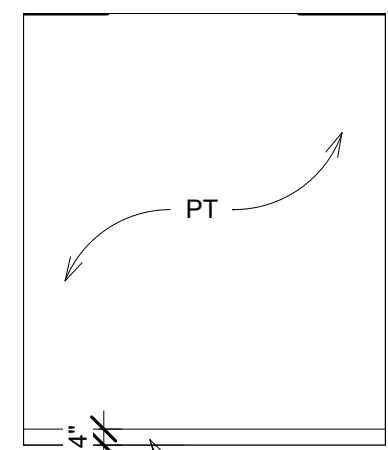


117 CONSULT WEST
1/4" = 1'-0"

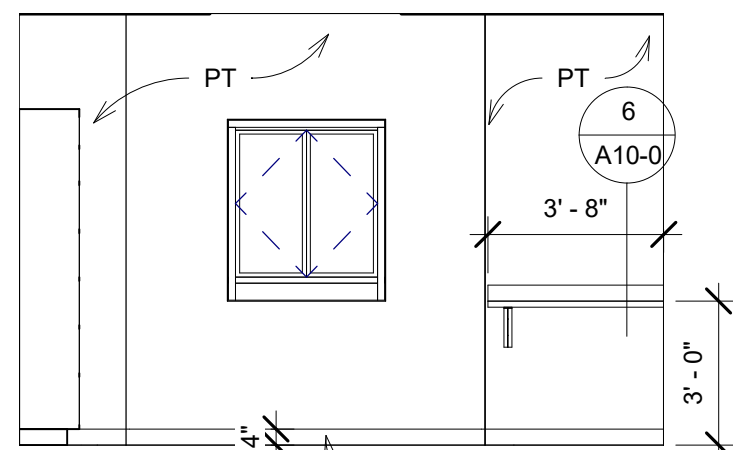


118 DRIVE-THRU WEST
1/4" = 1'-0"

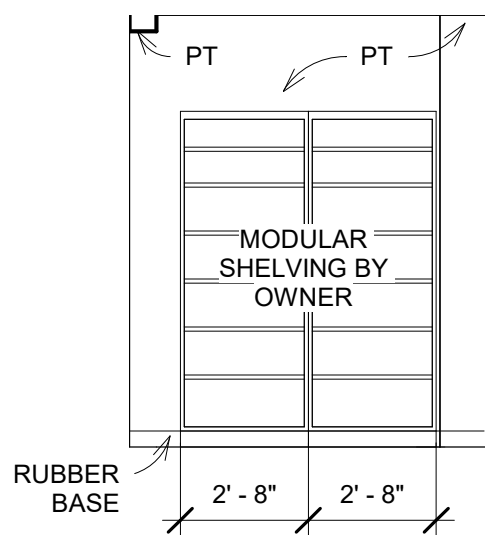


119 DRIVE-THRU SOUTH
1/4" = 1'-0"

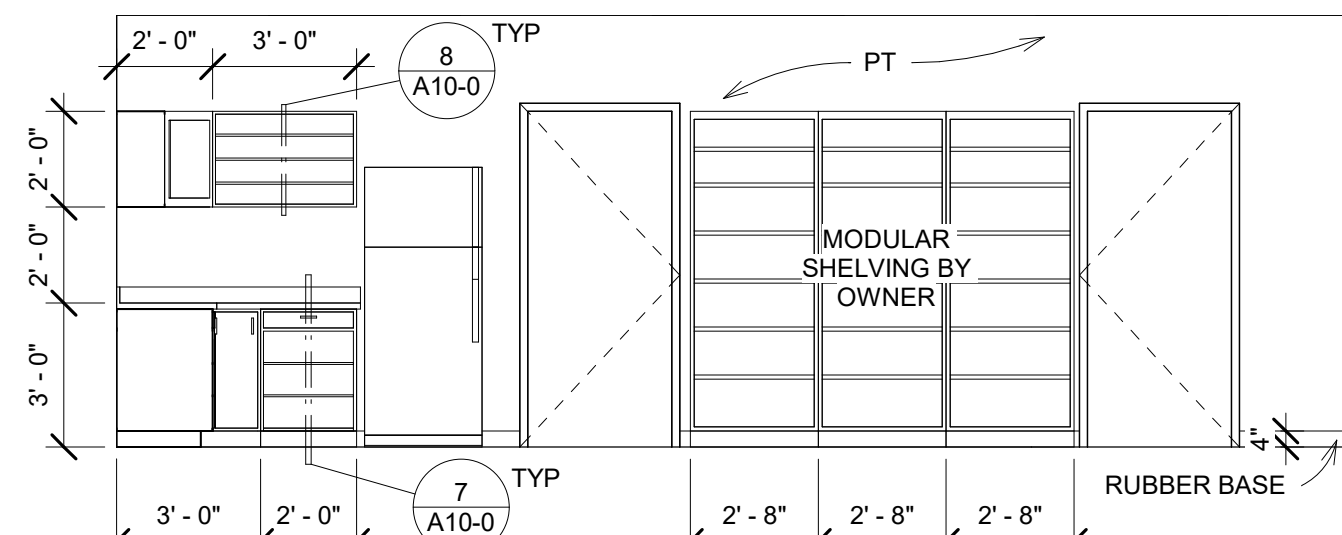

120 PHARMACY SOUTH
1/4" = 1'-0"

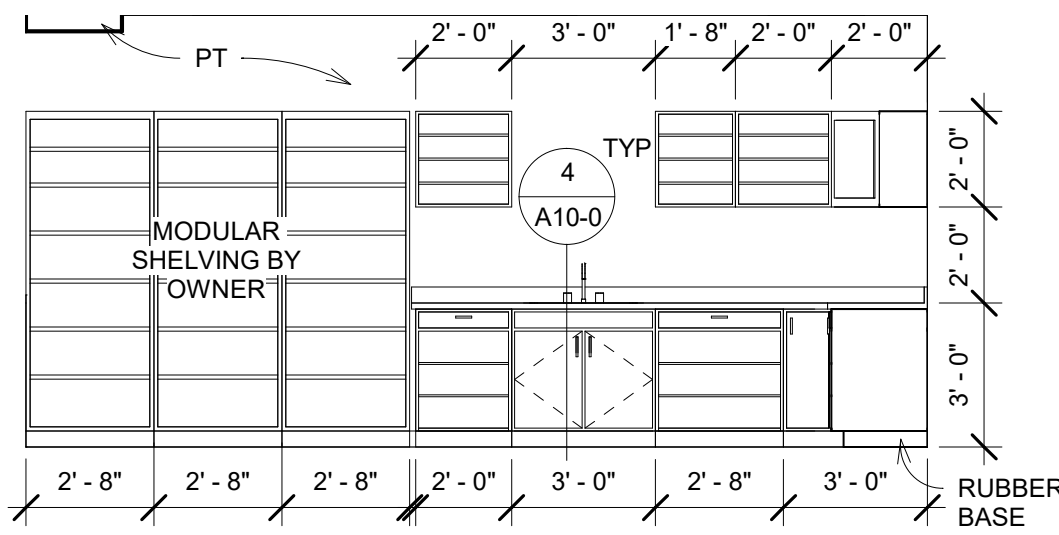

121 PHARMACY EAST
1/4" = 1'-0"

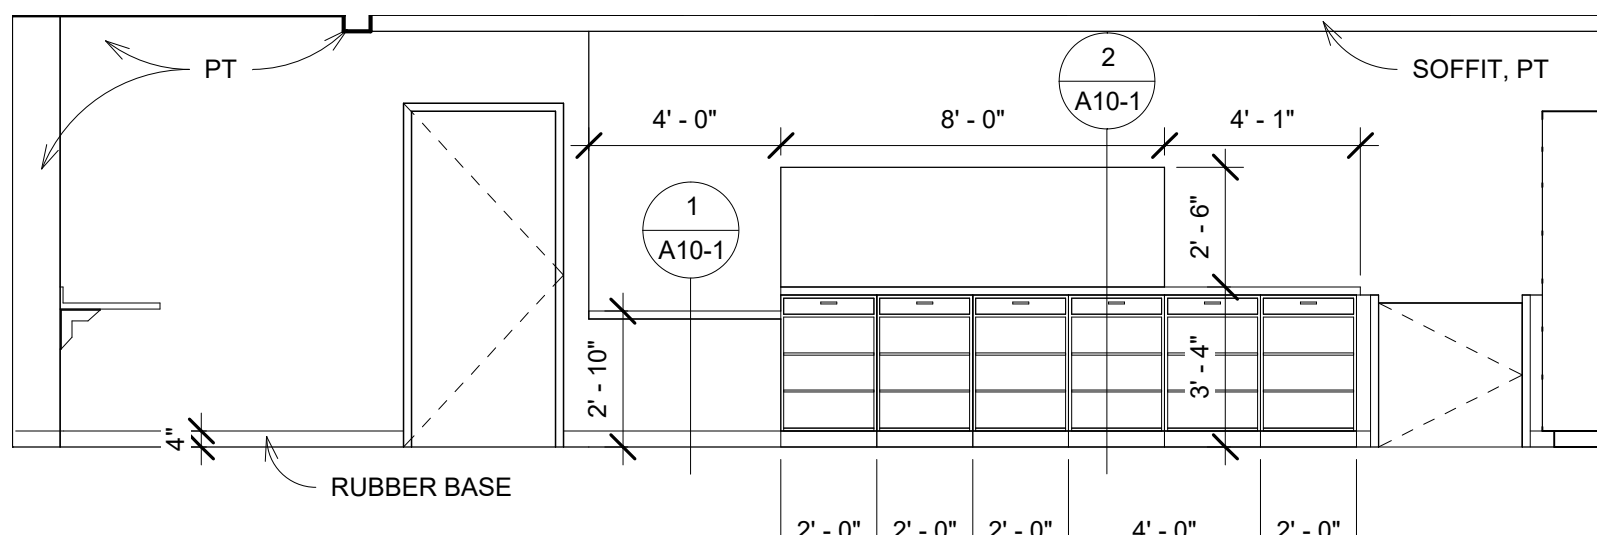

122 PHARMACY NORTH
1/4" = 1'-0"

A REMODEL FOR:


BLUE LAKES URGENT CARE
1309 BLUE LAKES BLVD TWIN FALLS, ID
INTERIOR ELEVATIONS

Laughlin Ricks Architecture
architecture/planning
134 3RD AVE. E. * Twin Falls, Idaho 83301
PHONE: (208) 736-8050


DATE: 4.19.22

NM RCR
Drawn Checked


A8-3

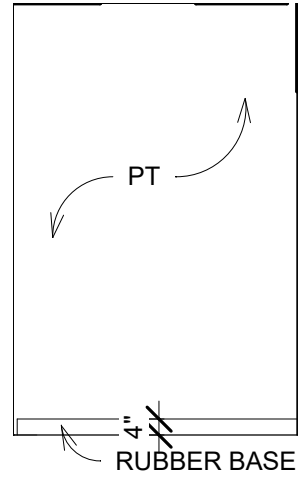


123 STORAGE 2 NORTH
1/4" = 1'-0"

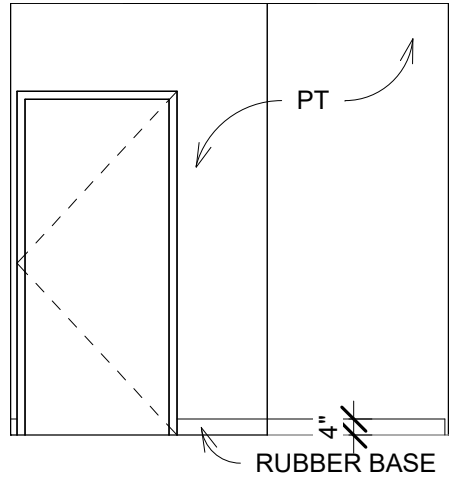


124 STORAGE 2 EAST
1/4" = 1'-0"

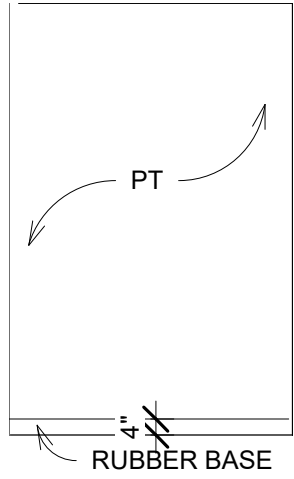


125 STORAGE 2 SOUTH
1/4" = 1'-0"

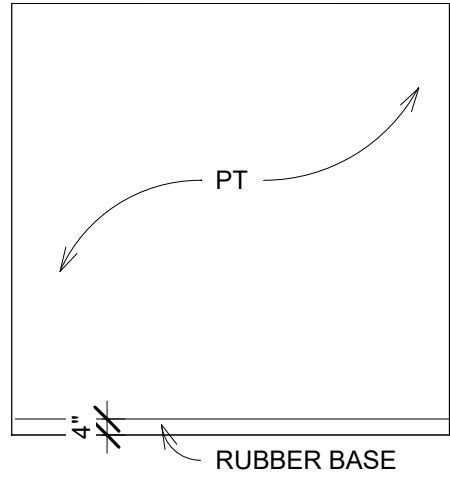


126 STORAGE 2 WEST
1/4" = 1'-0"

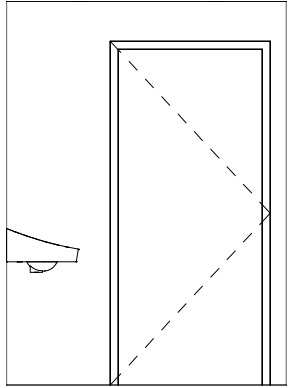


127 RR NORTH
1/4" = 1'-0"

 

128 RR EAST
1/4" = 1'-0"

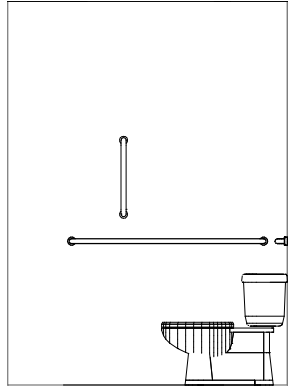

129 RR SOUTH
1/4" = 1'-0"

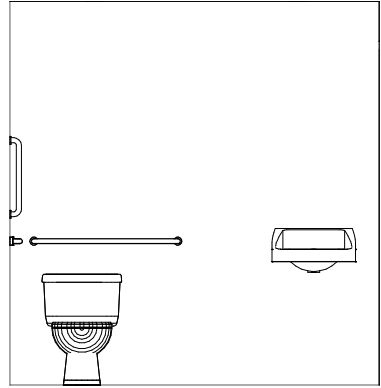

130 RR WEST
1/4" = 1'-0"

A REMODEL FOR:
BLUE LAKES URGENT CARE
1309 BLUE BLAKES BLVD TWIN FALLS, ID
INTERIOR ELEVATIONS

Laughlin Ricks Architecture
architecture/planning
134 3RD AVE. E. * Twin Falls, Idaho 83301
PHONE: (208) 736-8050

DATE: 4.19.22
NM RCR
Drawn Checked

A8-4

4.19.22

DATE

Room Finish Schedule														
Number	Name	Base Finish	Floor Finish	Materials				Finishes				Ceiling Material	Ceiling Finish	Remarks
				North	East	South	West	North	East	South	West			
1	VESTIBULE	RUBBER	WALK-OFF CPT	GYP BD	GYP BD	GYP BD	GYP BD	PT	PT	PT	PT	GYP BD / 2X4 ACT	PT/FF	
2	WAITING	RUBBER	TILE	GYP BD	GYP BD	GYP BD	GYP BD	PT	PT	PT	PT	GYP BD / 2X4 ACT	PT/FF	
3	CORR	RUBBER	TILE/CPT		GYP BD/CBB		GYP BD		ACC PT 3/STONE		PT	GYP BD / 2X4 ACT	PT/FF	
4	CORR	RUBBER	CPT	GYP BD		GYP BD	GYP BD	PT		PT	PT	GYP BD / 2X4 ACT	PT/FF	
5	CORR	RUBBER	WALK-OFF CPT	GYP BD	GYP BD		GYP BD	PT	PT		PT	GYP BD / 2X4 ACT	PT/FF	
6	CORR	RUBBER	CPT	GYP BD	GYP BD		GYP BD	PT	PT		PT	GYP BD / 2X4 ACT	PT/FF	
7	CORR	RUBBER	CPT		GYP BD		GYP BD				ACC PT 3	GYP BD / 2X4 ACT	PT/FF	
8	CORR	RUBBER	CPT		GYP BD	GYP BD	GYP BD		PT	PT	PT	GYP BD / 2X4 ACT	PT/FF	
9	CORR	RUBBER	TILE/CPT	GYP BD	GYP BD	GYP BD	GYP BD	ACC PT 3	PT	PT	PT	GYP BD / 2X4 ACT	PT/FF	
10	EXAM 1	RUBBER	LVP	GYP BD	GYP BD	GYP BD	GYP BD	PT	PT	PT	ACC PT 1	2X4 ACT	FF	
11	EXAM 2	RUBBER	LVP	GYP BD	GYP BD	GYP BD	GYP BD	PT	PT	PT	ACC PT 1	2X4 ACT	FF	
12	CLOSET	RUBBER	CPT	GYP BD	GYP BD	GYP BD	GYP BD	PT	PT	PT	PT	2X4 ACT	FF	
13	EXAM 3	RUBBER	LVP	GYP BD	GYP BD	GYP BD	GYP BD	PT	PT	PT	ACC PT 1	2X4 ACT	FF	
14	EXAM 4	RUBBER	LVP	GYP BD	GYP BD	GYP BD	GYP BD	PT	PT	PT	ACC PT 1	2X4 ACT	FF	
15	LAB	RUBBER	LVP	GYP BD	GYP BD	GYP BD	GYP BD	PT	PT	PT	PT	2X4 ACT	FF	
16	STORAGE	RUBBER	LVP	GYP BD	GYP BD	GYP BD	GYP BD	PT	PT	PT	PT	2X4 ACT	FF	
17	RR 1	TILE	TILE	TBB	TBB	TBB	TBB	TILE/EPOXY PT	TILE/EPOXY PT	TILE/EPOXY PT	TILE/EPOXY PT	GYP BD	PT	
18	EXAM 5	RUBBER	LVP	GYP BD	GYP BD	GYP BD	GYP BD	ACC PT 1	PT	PT	PT	GYP BD / 2X4 ACT	PT/FF	
19	TRIAGE	RUBBER	LVP	GYP BD	GYP BD		GYP BD	PT	PT	PT	PT	GYP BD	PT	
20	CARTS	RUBBER	CPT	GYP BD	GYP BD		GYP BD	PT	PT	PT	PT	GYP BD	PT	
21	PROCEDURE	RUBBER	LVP	GYP BD	GYP BD	GYP BD	GYP BD	PT	ACC PT 1	PT	PT	GYP BD / 2X4 ACT	PT/FF	
22	EXAM 6	RUBBER	LVP	GYP BD	GYP BD	GYP BD	GYP BD	PT	ACC PT 1	PT	PT	GYP BD / 2X4 ACT	PT/FF	
23	EXAM EKG	RUBBER	LVP	GYP BD	GYP BD	GYP BD	GYP BD	PT	ACC PT 1	PT	PT	2X4 ACT	PT/FF	
24	OFFICE 1	RUBBER	CPT	GYP BD	GYP BD	GYP BD	GYP BD	PT	ACC PT 2	PT	PT	GYP BD / 2X4 ACT	PT/FF	
25	OFFICE 2	RUBBER	CPT	GYP BD	GYP BD	GYP BD	GYP BD	PT	ACC PT 2	PT	PT	GYP BD / 2X4 ACT	PT/FF	
26	BREAKROOM	RUBBER	LVP	GYP BD	GYP BD	GYP BD	GYP BD	PT	ACC PT 3	PT	PT	2X4 ACT	FF	
27	CONFERENCE ROOM	RUBBER	CPT	GYP BD	GYP BD	GYP BD	GYP BD	PT	ACC PT 2	PT	PT	GYP BD / 2X4 ACT	PT/FF	
28	UTILITY/STORAGE	RUBBER	LVP	GYP BD	GYP BD	GYP BD	GYP BD	PT/FRP	PT	PT	PT/FRP	2X4 ACT	FF	FRP AROUND MOP SINK TO 4'-0"
29	X-RAY	RUBBER	LVP	GYP BD	GYP BD	GYP BD	GYP BD	PT	PT	PT	PT	2X4 ACT	FF	LEAD LINED GYP BD THROUGHOUT
30	RR 2	TILE	TILE	TBB	TBB	TBB	TBB	TILE/EPOXY PT	TILE/EPOXY PT	TILE/EPOXY PT	TILE/EPOXY PT	GYP BD	PT	
31	RR 3	TILE	TILE	TBB	TBB	TBB	TBB	TILE/EPOXY PT	TILE/EPOXY PT	TILE/EPOXY PT	TILE/EPOXY PT	GYP BD	PT	
32	RECEPTION	RUBBER	CPT	GYP BD	GYP BD	GYP BD	GYP BD	PT	ACC PT 4	PT	PT	2X4 ACT	FF	
33	PROVIDERS	RUBBER	CPT	GYP BD	GYP BD	GYP BD	GYP BD	PT	PT	PT	PT	2X4 ACT	FF	
34	MEDICAL ASSISTANT	RUBBER	CPT			GYP BD				ACC PT 3		GYP BD / 2X4 ACT	PT/FF	
35	HOT WATER	RUBBER	SEALED CONCRETE	GYP BD	GYP BD	GYP BD	GYP BD	PT	PT	PT	PT	2X4 ACT	FF	
36	ELEC	RUBBER	SEALED CONCRETE	GYP BD	GYP BD	GYP BD	GYP BD	PT	PT	PT	PT	2X4 ACT	FF	
37	RR	TILE	TILE	TBB	TBB	TBB	TBB	TILE/EPOXY PT	TILE/EPOXY PT	TILE/EPOXY PT	TILE/EPOXY PT	GYP BD	PT	
38	PHARMACY	RUBBER	CPT/LVP	GYP BD	GYP BD	GYP BD	GYP BD	PT	PT	PT	PT	GYP BD / 2X4 ACT	PT/FF	
39	STORAGE 2	RUBBER	CPT	GYP BD	GYP BD	GYP BD	GYP BD	PT	PT	PT	PT	2X4 ACT	FF	
40	DRIVE-THRU	RUBBER	CPT	GYP BD	GYP BD	GYP BD	GYP BD	PT		PT	PT	GYP BD / 2X4 ACT	PT/FF	
41	CONSULTING	RUBBER	CPT	GYP BD	GYP BD	GYP BD	GYP BD	PT	PT	PT	PT	GYP BD / 2X4 ACT	PT/FF	
42	PHARMACY WAITING	RUBBER	CPT/TILE	GYP BD	GYP BD	GYP BD/CBB	GYP BD	PT/ACC PT 3	PT/ACC PT 3	PT/STONE	PT	GYP BD / 2X4 ACT	PT/FF	
43	OFFICE	RUBBER	CPT	GYP BD	GYP BD	GYP BD	GYP BD	PT	PT	PT	PT	2X4 ACT	FF	

4.19.22

DATE

A REMODEL FOR:

BLUE LAKES URGENT CARE

1309 BLUE BLAKES BLVD TWIN FALLS ID

ROOM FINISH SCHEDULE

Laughlin Ricks Architecture

architecture/planning

134 3RD AVE. E. * Twin Falls, Idaho 83301


PHONE: (208) 736-8050

DATE: 4.19.22


NM RCR

Drawn Checked

A9-0

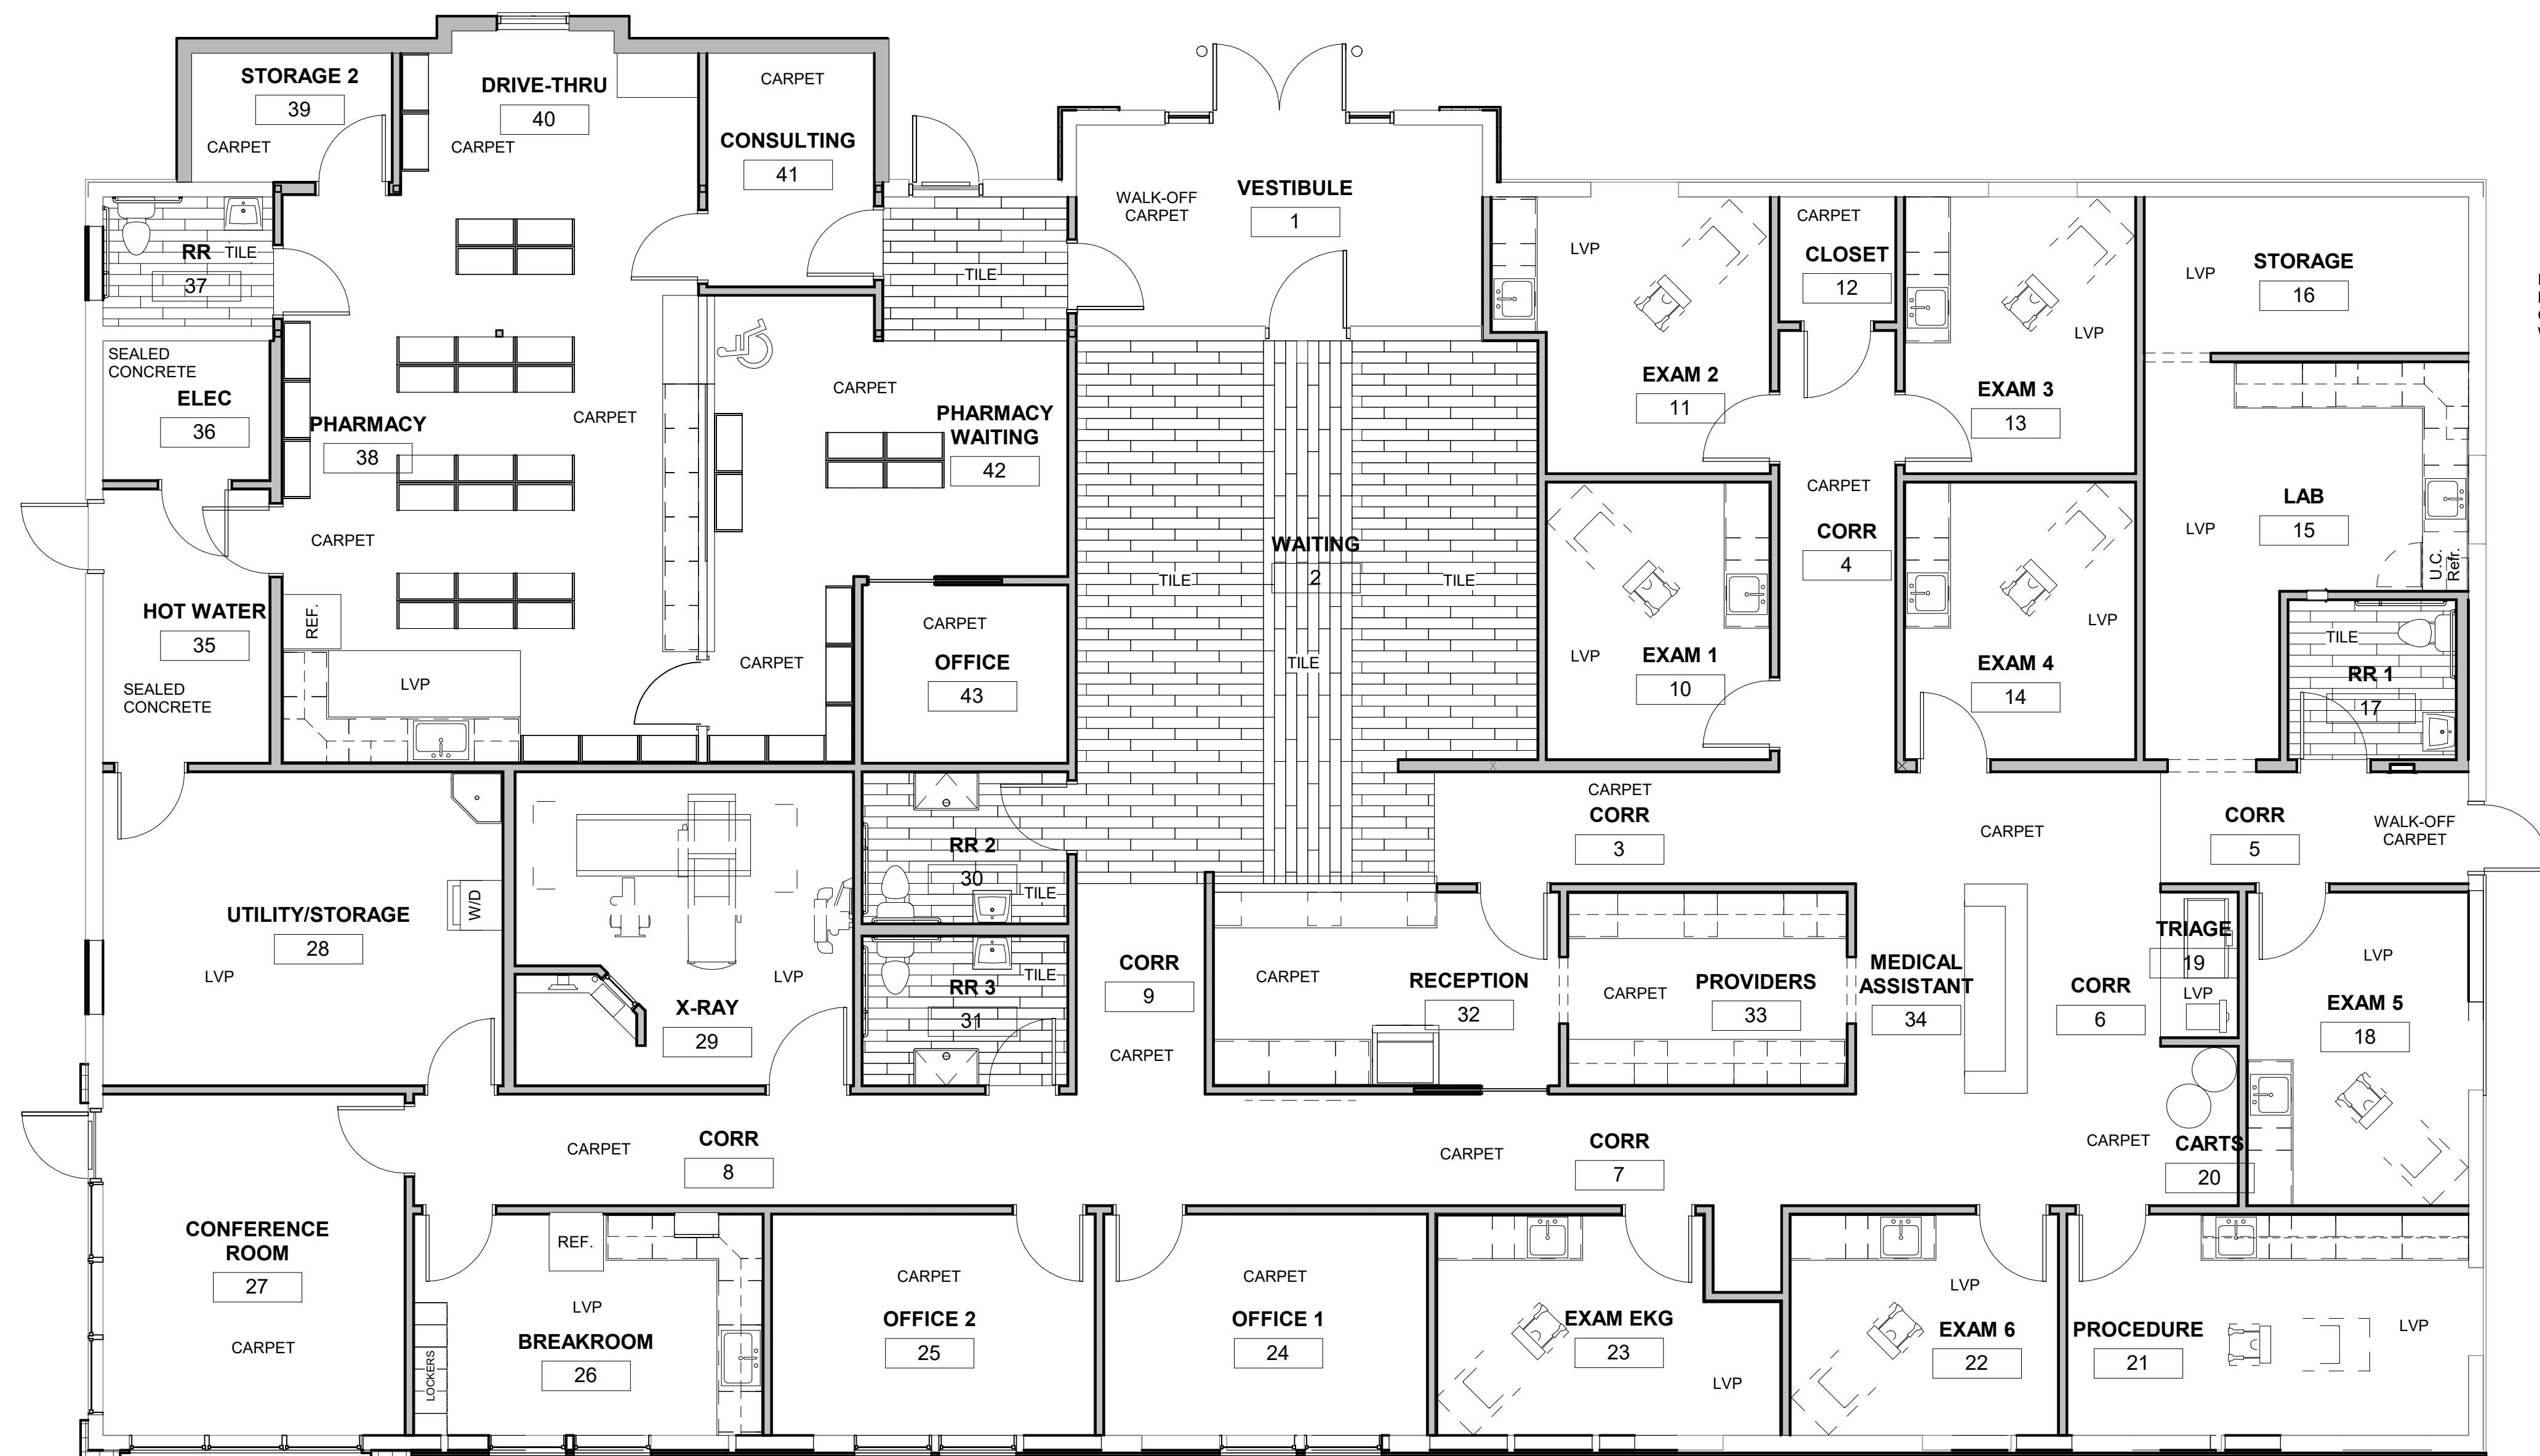

FLOOR TILE: SADDLE BROOK XT, GRAVEL ROAD
LVP: MARMOLEUM - TEXTURA, TRACE OF NATURE?
CARPET:
WALK-OFF CARPET:

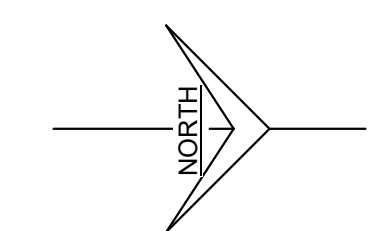

① FINISH FLOOR PLAN
3/16" = 1'-0"

4.19.22

DATE


A REMODEL FOR:
BLUE LAKES URGENT CARE
1309 BLUE BLAKES BLVD TWIN FALLS, ID
FINISH FLOOR PLAN

Laughlin Ricks Architecture
architecture/planning
134 3RD AVE. E. * Twin Falls, Idaho 83301
PHONE: (208) 736-8050


DATE: 4.19.22
NM RCR
Drawn Checked

A9-1

DOOR SCHEDULE											
Door Number	Elevation	Width	Height	Door Material	Door Finish	Frame Material	Frame Finish	Accessories	Door Glass	UL RATING	Comments
1	a	3' - 0"	7' - 0"	ALUMINUM STOREFRONT	FF	ALUMINUM	FF	WEATHER-STRIP/ THRESHOLD / CLOSER / CONTINUOUS HINGES / PANIC HARDWARE	SFGL		
2	c	3' - 6"	7' - 0"	ALUMINUM STOREFRONT	FF	ALUMINUM	FF		SFGL		
3	f	3' - 0"	7' - 0"	P-LAM	FF	TIMELY HM	FF				
4	f	3' - 0"	7' - 0"	P-LAM	FF	TIMELY HM	FF				
5	f	3' - 0"	7' - 0"	P-LAM	FF	TIMELY HM	FF				
6	f	3' - 0"	7' - 0"	P-LAM	FF	TIMELY HM	FF				
7	f	3' - 0"	7' - 0"	P-LAM	FF	TIMELY HM	FF				
8	f	3' - 0"	7' - 0"	P-LAM	FF	TIMELY HM	FF				
9	f	3' - 0"	7' - 0"	P-LAM	FF	TIMELY HM	FF				
10	f	3' - 0"	7' - 0"	FRP	FF	HM	FF				SPECIAL-LITE SL-20
11	f	3' - 0"	7' - 0"	P-LAM	FF	TIMELY HM	FF				
12	f	3' - 0"	7' - 0"	P-LAM	FF	TIMELY HM	FF				
13	f	3' - 0"	7' - 0"	P-LAM	FF	TIMELY HM	FF				
14	f	3' - 0"	7' - 0"	P-LAM	FF	TIMELY HM	FF				
15	h	3' - 0"	7' - 0"	P-LAM	FF	TIMELY HM	FF				
16	g	3' - 0"	7' - 0"	P-LAM	FF	TIMELY HM	FF				
17	g	3' - 0"	7' - 0"	P-LAM	FF	TIMELY HM	FF				
18	f	3' - 0"	7' - 0"	P-LAM	FF	TIMELY HM	FF				
19	f	3' - 0"	7' - 0"	P-LAM	FF	TIMELY HM	FF				
20	e	3' - 6"	7' - 0"	P-LAM, LEAD LINED	FF	TIMELY HM	FF				
21	f	3' - 0"	7' - 0"	P-LAM	FF	TIMELY HM	FF				
23	l	3' - 0"	7' - 0"	ALUMINUM STOREFRONT	FF	ALUMINUM	FF		SFGL		
23	b	3' - 0"	7' - 0"	P-LAM	FF	TIMELY HM	FF				
24	f	3' - 0"	7' - 0"	P-LAM	FF	TIMELY HM	FF				
25	k	3' - 0"	6' - 8"	FRP	FF	HM	FF				SPECIAL-LITE SL-20
26	f	3' - 0"	7' - 0"	P-LAM	FF	TIMELY HM	FF				
27	d	3' - 0"	7' - 0"	ALUMINUM STOREFRONT	FF	HM	FF				
28	b	3' - 0"	7' - 0"	ALUMINUM STOREFRONT	FF	ALUMINUM	FF		SFGL		
29	f	3' - 0"	7' - 0"	P-LAM	FF	TIMELY HM	FF				
30	f	3' - 0"	7' - 0"	P-LAM	FF	TIMELY HM	FF				
31	h	3' - 0"	7' - 0"	P-LAM	FF	TIMELY HM	FF				
32	j	3' - 0"	3' - 0"	P-LAM	FF						
33	f	3' - 0"	7' - 0"	P-LAM	FF	TIMELY HM	FF				
34	f	3' - 0"	7' - 0"	P-LAM	FF	TIMELY HM	FF				
35	f	3' - 0"	7' - 0"	P-LAM	FF	TIMELY HM	FF				

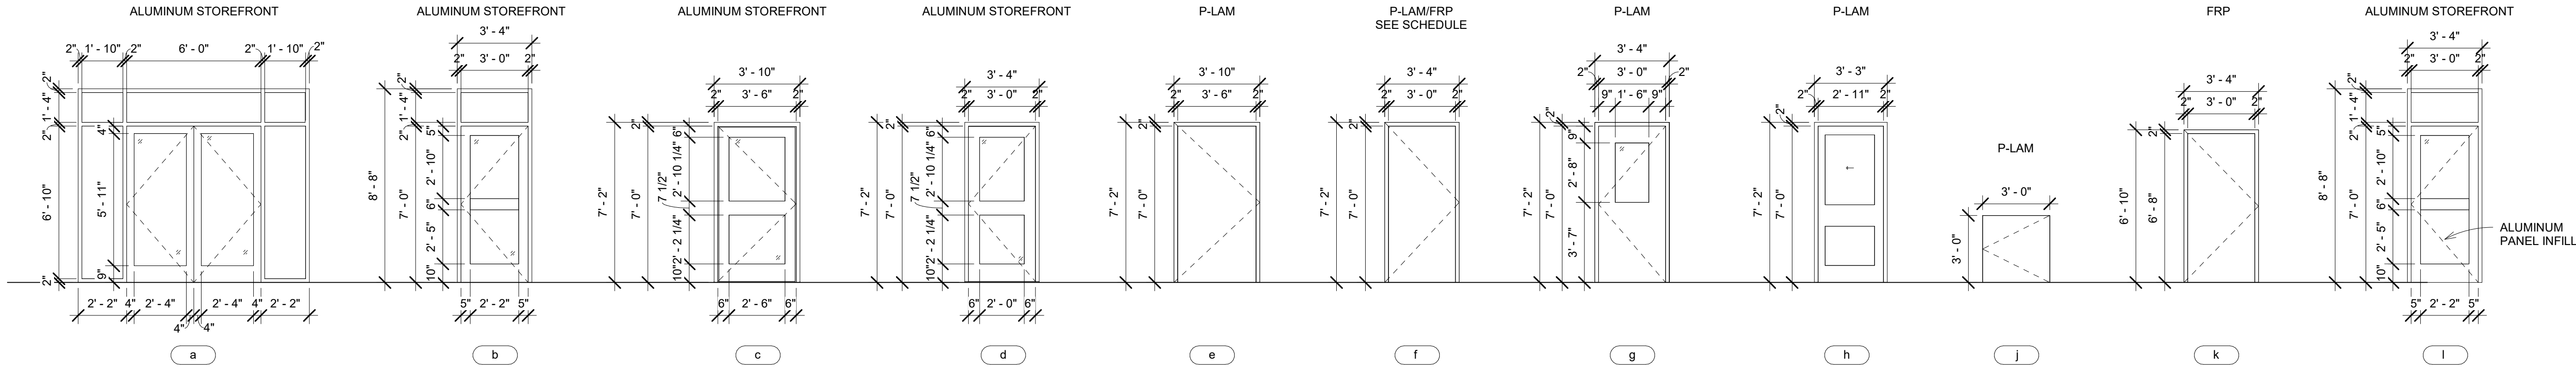

DOOR TYPES
1/4" = 1'-0"

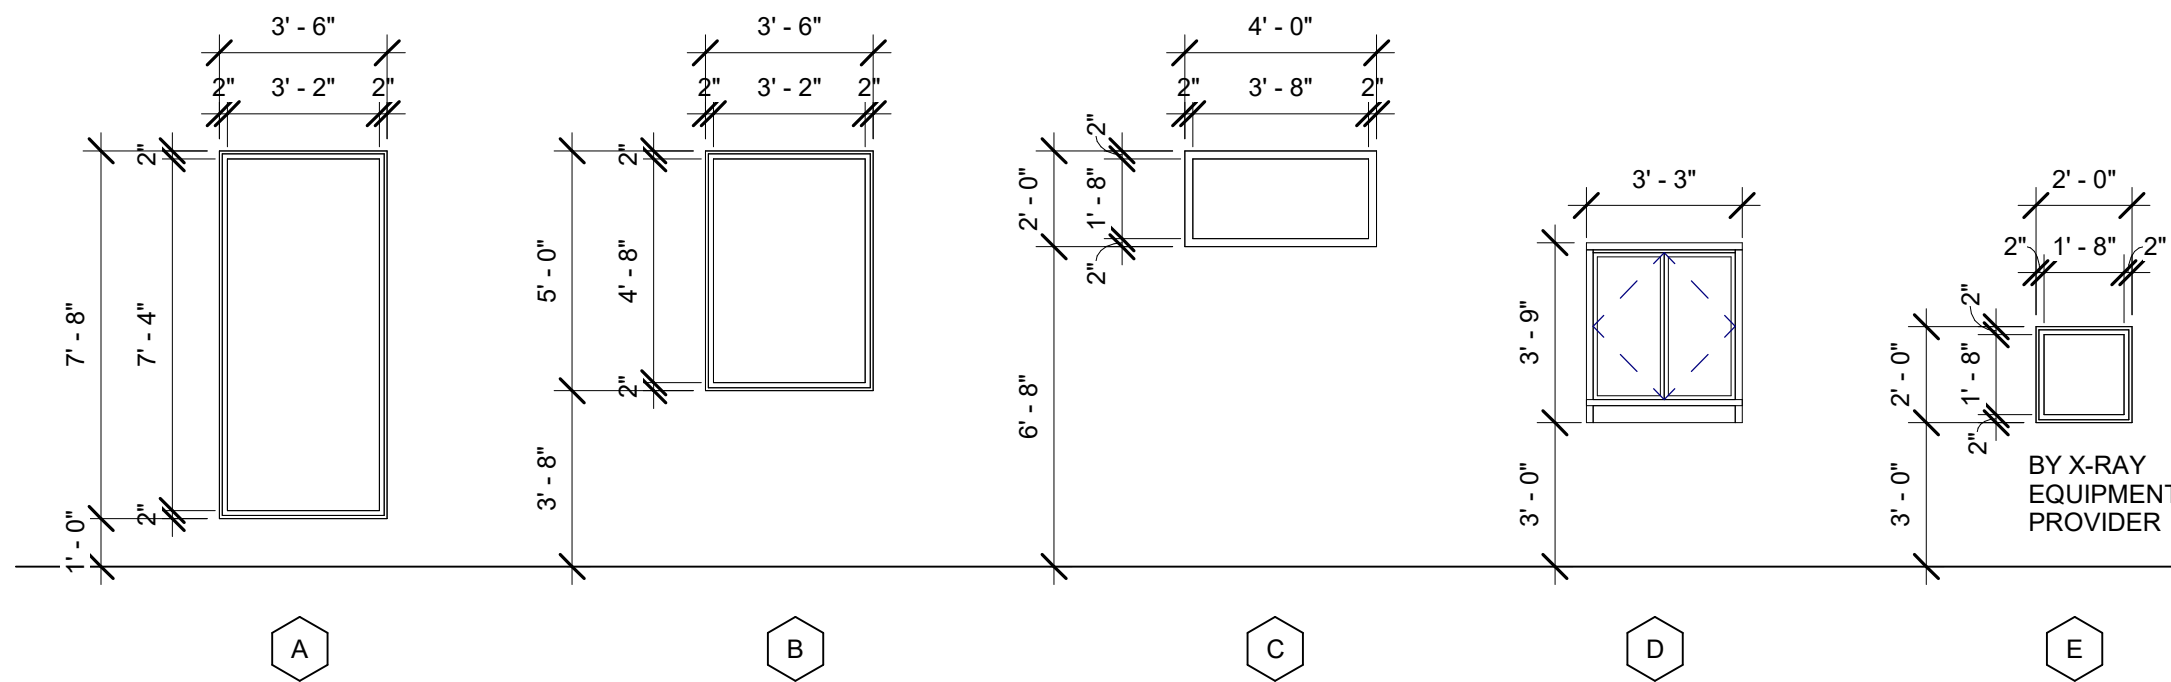

WINDOW TYPES
1/4" = 1'-0"

ALUMINUM STOREFRONT: DARK BRONZE
P-LAM =FORMICA THERMO WALNUT FRAME: TIMELY FINISH BROWNTONE
FRP=

WINDOW FRAMES: DARK BRONZE

A REMODEL FOR:


BLUE LAKES URGENT CARE
1309 BLUE BLAKES BLVD TWIN FALLS, ID
DOOR & WINDOW TYPES


Laughlin Ricks Architecture
architecture/planning
134 3RD AVE. E. * Twin Falls, Idaho 83301
PHONE: (208) 736-8050

DATE: 4.19.22


NM RCR
Drawn Checked

A9-2

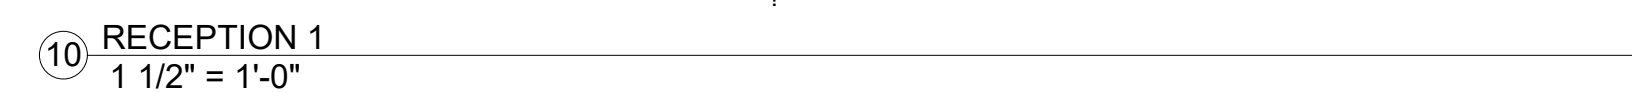

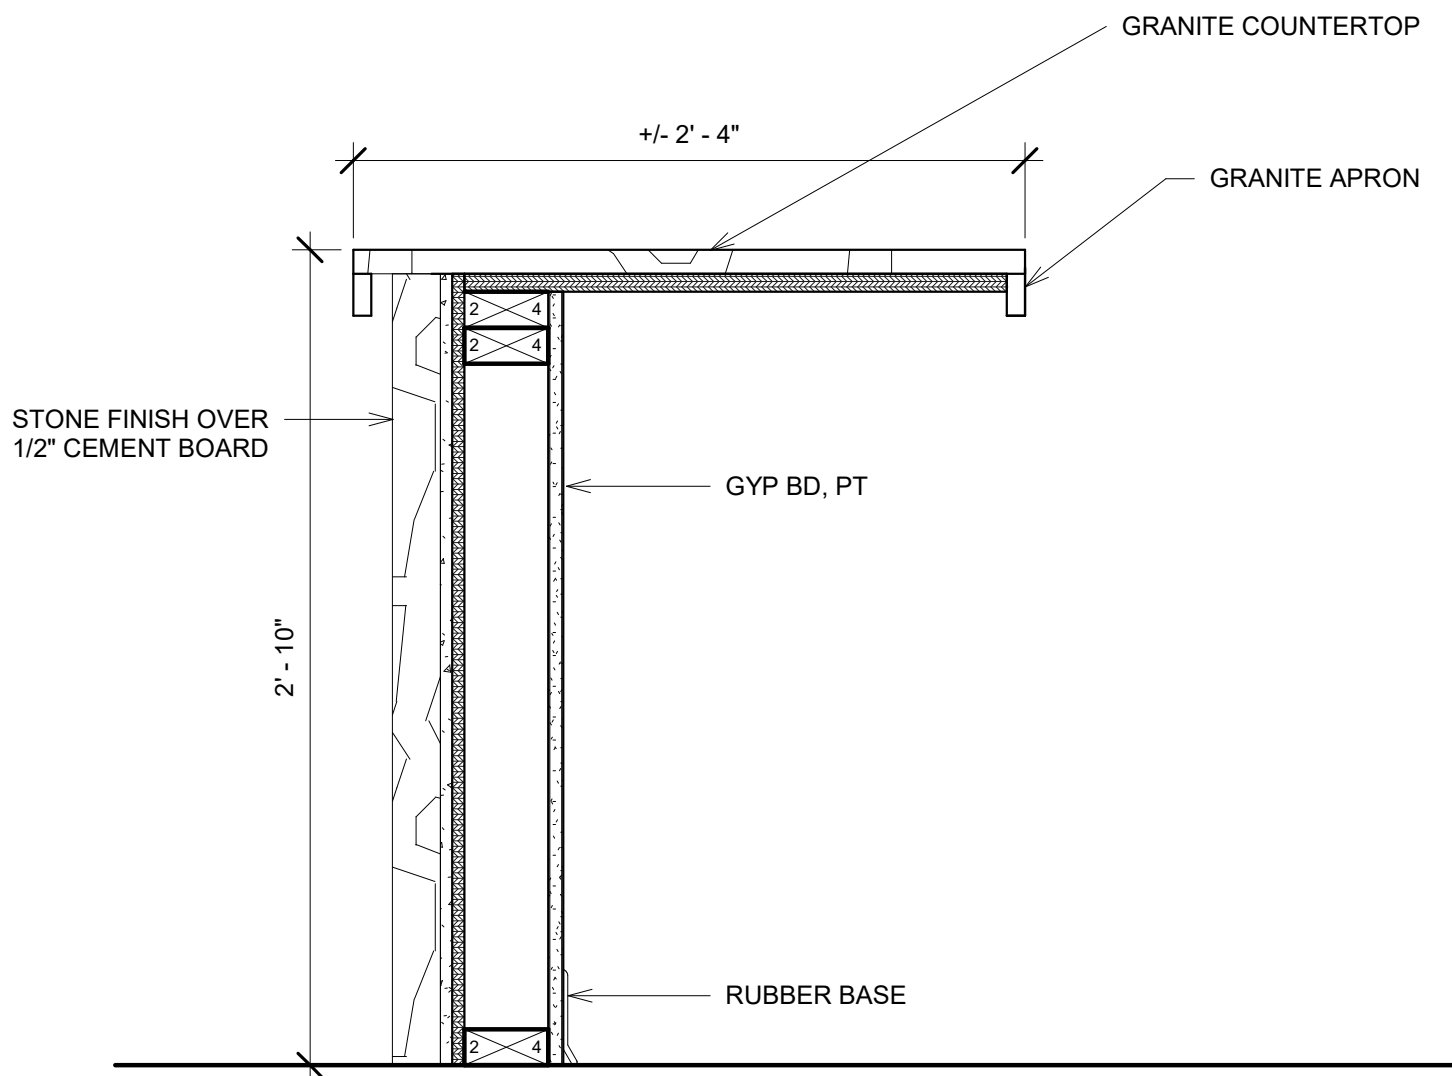

① PHARMACY CASEWORK 1
1 1/2" = 1'-0"

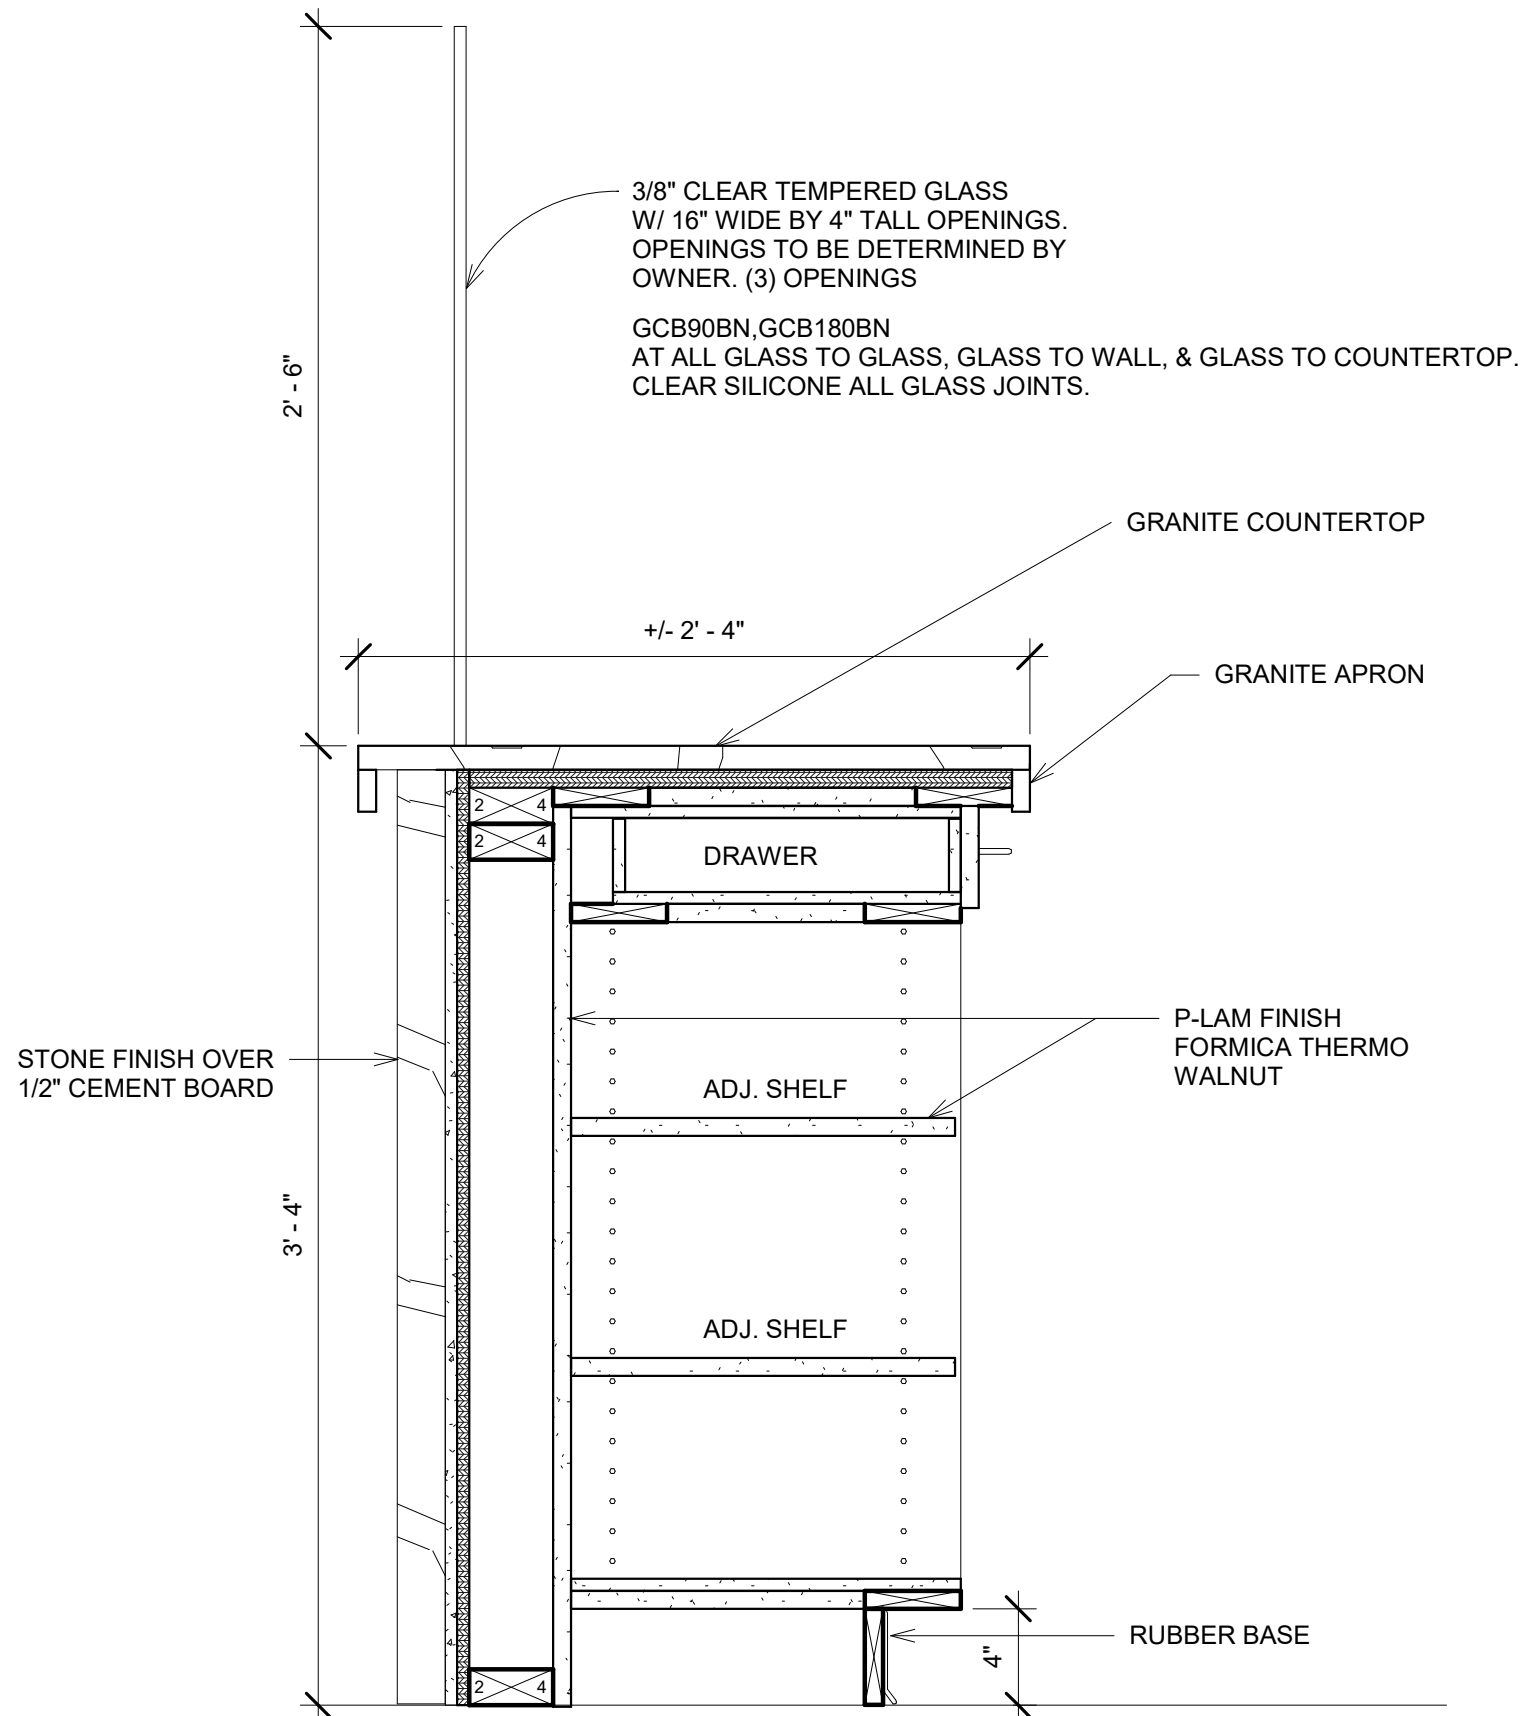

② PHARMACY CASEWORK 2
1 1/2" = 1'-0"

A REMODEL FOR:
BLUE LAKES URGENT CARE
1309 BLUE BLAKES BLVD TWIN FALLS, ID
CASEWORK DETAILS


Laughlin Ricks Architecture
architecture/planning
134 3RD AVE. E. * Twin Falls, Idaho 83301
PHONE: (208) 736-8050

DATE: 4.19.22
NM RCR
Drawn Checked

A10-1

4.19.22

DATE

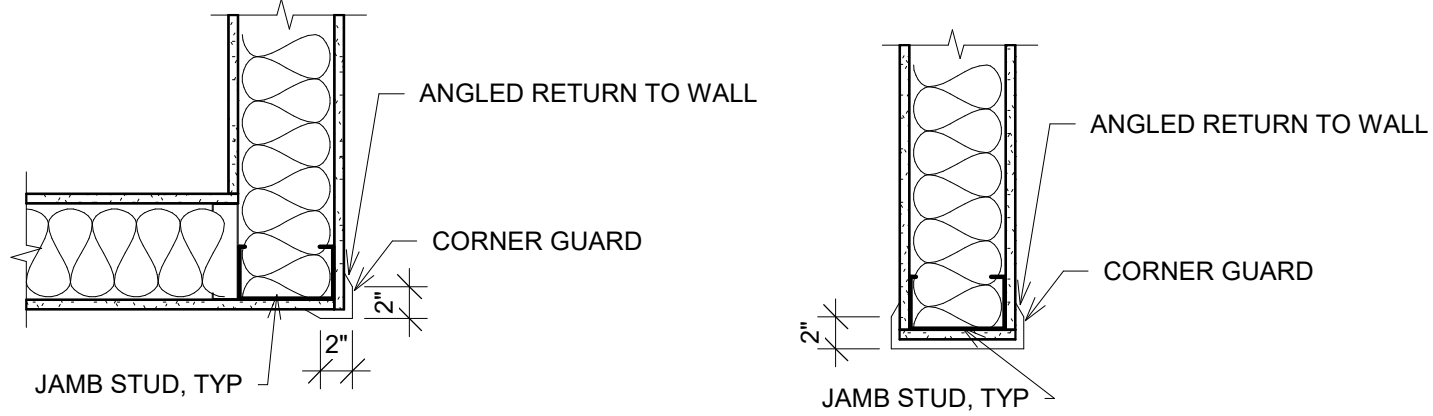


TYPE A

TYPE B

NOTE: CORNER GUARDS @ ALL OUTSIDE CORNERS & ALCOVES. CORNER GUARD HEIGHTS SHALL BE 5'-0" U.N.O.

NOTE: REFER TO PLANS FOR WALL TYPES

1 INTERIOR - CORNER GUARD DETAILS
1" = 1'-0"

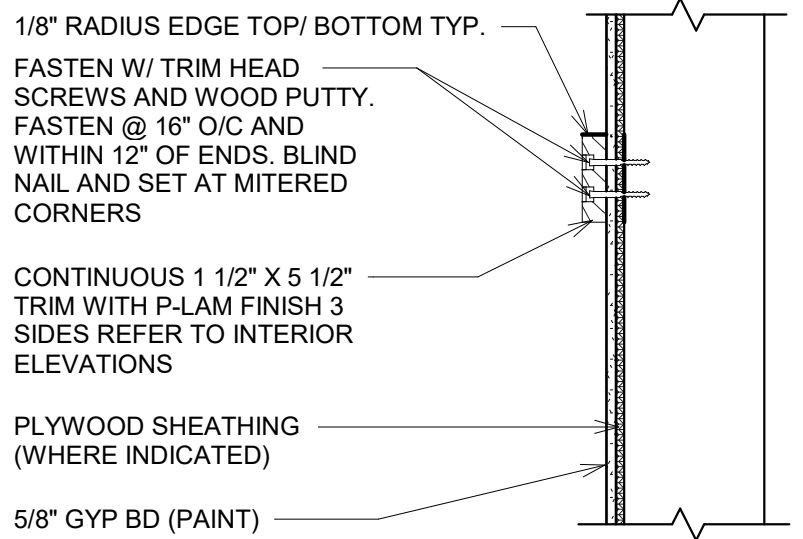

NOTE: CHAMFER EDGES AND RADIUS CORNERS THROUGHOUT

NOTE: VERIFY CHAIR RAIL HEIGHT WITH OWNER.

2 WOOD CHAIR RAIL DETAIL
1" = 1'-0"

A REMODEL FOR:
BLUE LAKES URGENT CARE
1309 BLUE LAKES BLVD TWIN FALLS ID
INTERIOR DETAILS

Laughlin Ricks Architecture
architecture/planning
134 3RD AVE. E. * Twin Falls, Idaho 83301
PHONE: (208) 736-8050

DATE: 4.19.22
NM RCR
Drawn Checked

A10-2

