

LANCE LeBARON HOMES

LOT 21A PRESCOTT ACRES
PARCEL: RP10S18E051211
ZONE: RURAL RESIDENTIAL
LOT SIZE 2.53 ACRES
CODE COMPLIANCE: 2018 IRC
NEW CONSTRUCTION - SHOP
SHOP FLOOR - 4368 SF
BALCONY FLOOR - 1170 SF
CUBIC FOOTAGE FOR FIRE DEPT - 95604 CF

ENERGY:

ENERGY COMPLIANCE
PRESCRIPTIVE ENERGY CODE
R-30 MIN IN FLOORS
R-20 MIN IN WALLS
R-38 MIN IN ATTIC SPACES OVER LIVING AREA
.35 U-VALUE MIN LOW-E WINDOWS

SHEET SCHEDULE


- A1 - SITE PLAN
- A2 - FOUNDATION PLAN
- A3 - SHOP FLOOR PLAN
- A4 - LOFT PLAN
- A5 - ROOF /FRAMING PLAN
- A6 - ELEVATIONS
- A7 - ELEVATIONS

SLOPE GRADE AWAY FROM FOUNDATION
6" IN 10' MIN FINAL GRADING TO BE
MAINTAINED AFTER LANDSCAPING

DO NOT DRAIN STORM WATER ONTO
ADJACENT LOTS BERMS/SWALE TO BE
MAINTAINED AFTER FINAL INSPECTION

SITE PLAN

- NOTES:
1. BUILDER TO VERIFY ALL DIMENSIONS, SPECIFICATIONS AND ELEVATIONS AND REPORT ANY ERRORS AND/OR OMISSIONS PRIOR TO CONSTRUCTION.
 2. PROVIDE STRING LINES OVER PROPERTY PINS AT TIME OF INSPECTIONS.

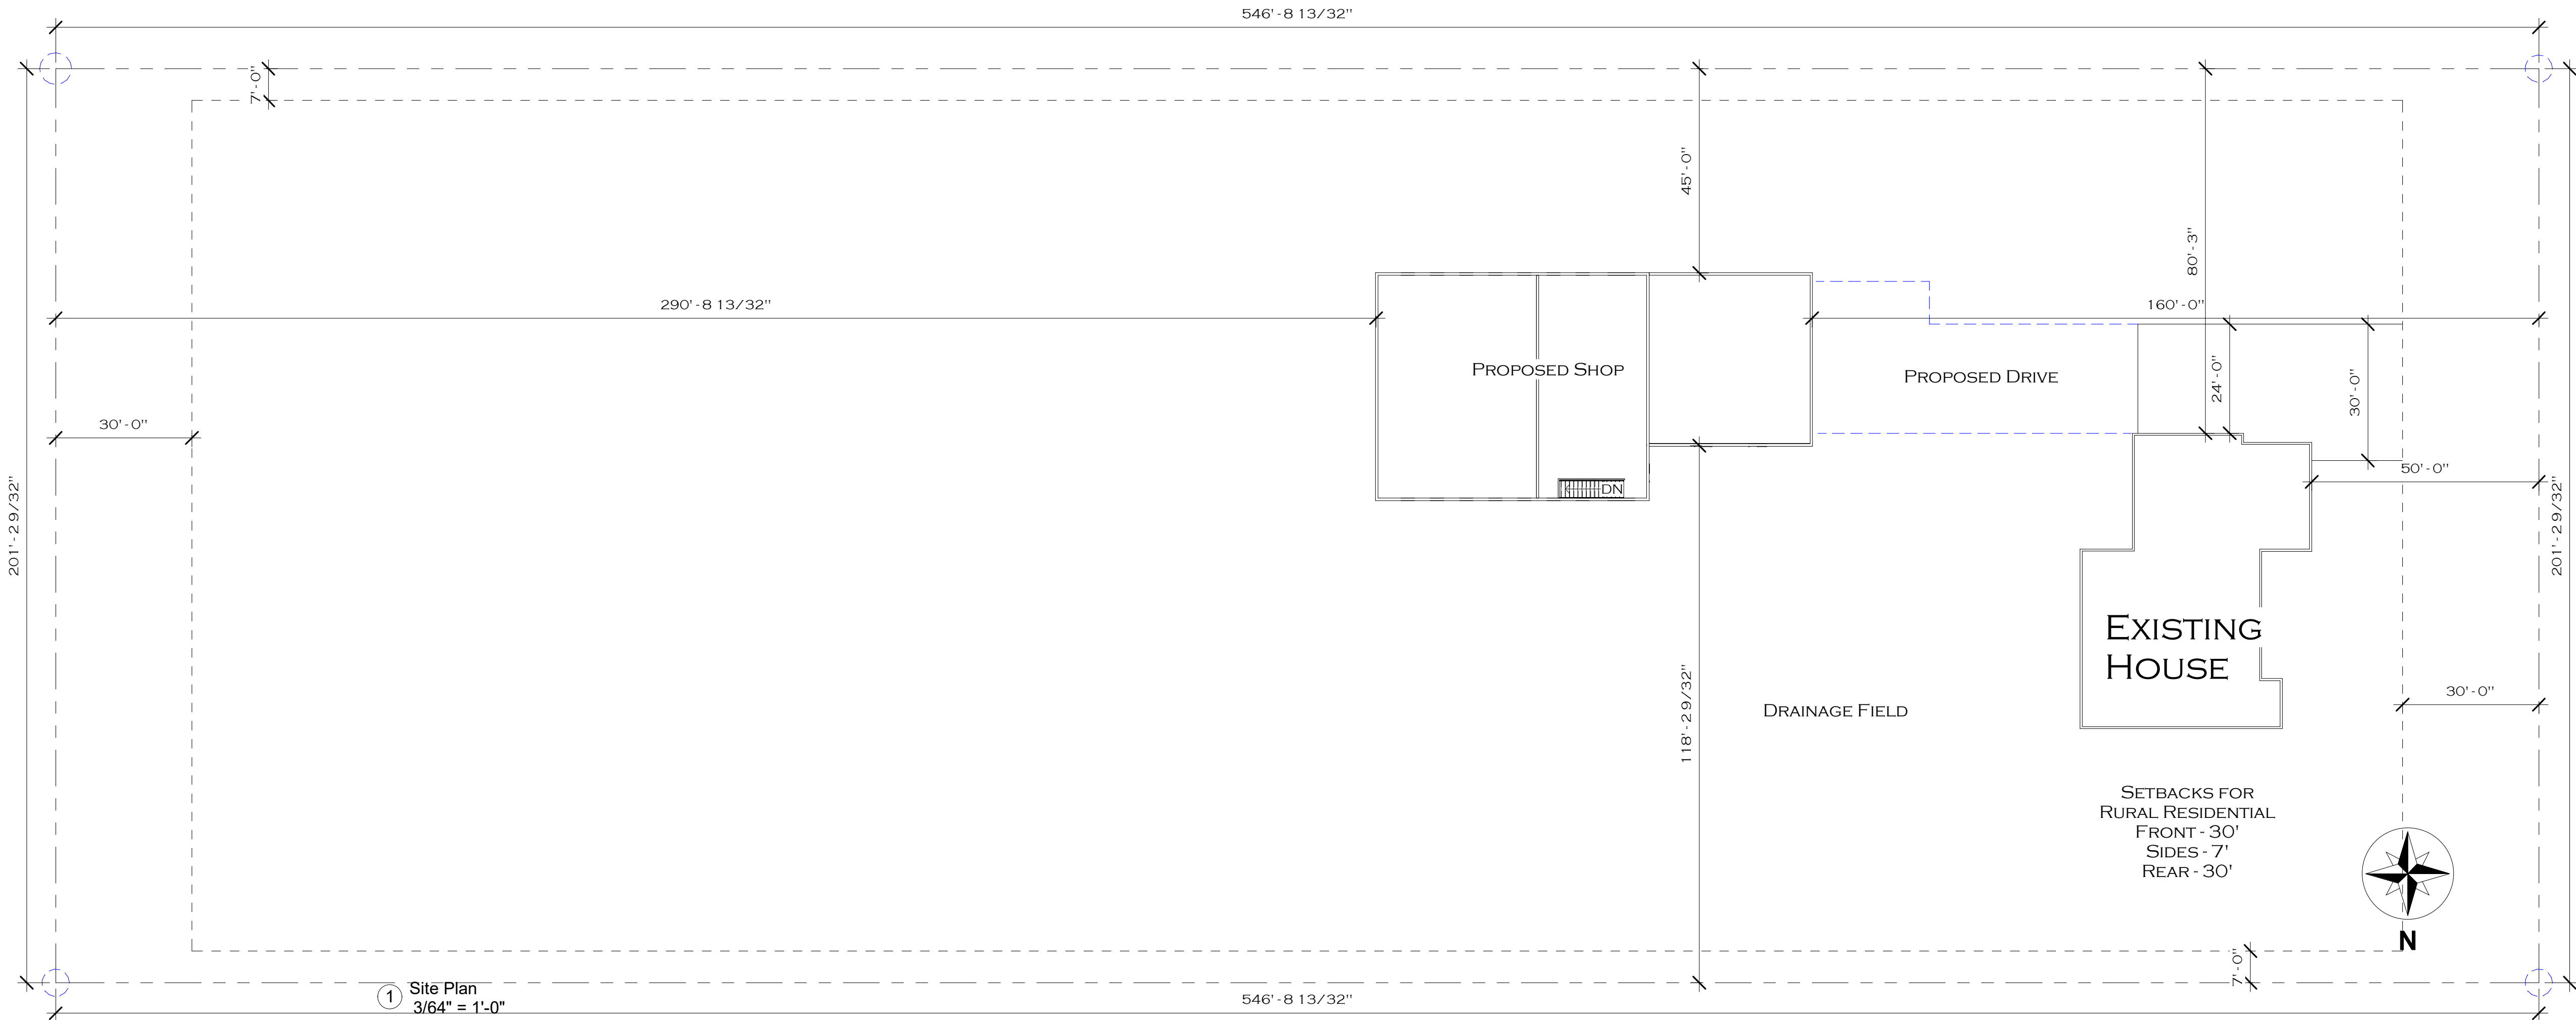

Designer is not a licenced engineer and will claim no responsibility for structural items. The designer's liability regarding errors and/or omissions will be limited to the correction of the original drawings.



SCALE:
3/64" = 1'-0"

DRAWN BY:
James Wallace

DATE DRAWN:
07/04/21


LAST REVISED:

Lance LeBaron Homes
Clark Shop - 4066 N 3462 E
Lot 21A Prescott Acres - Kimberly


SHEET:

A1

PLAN NAME:
Site Plan

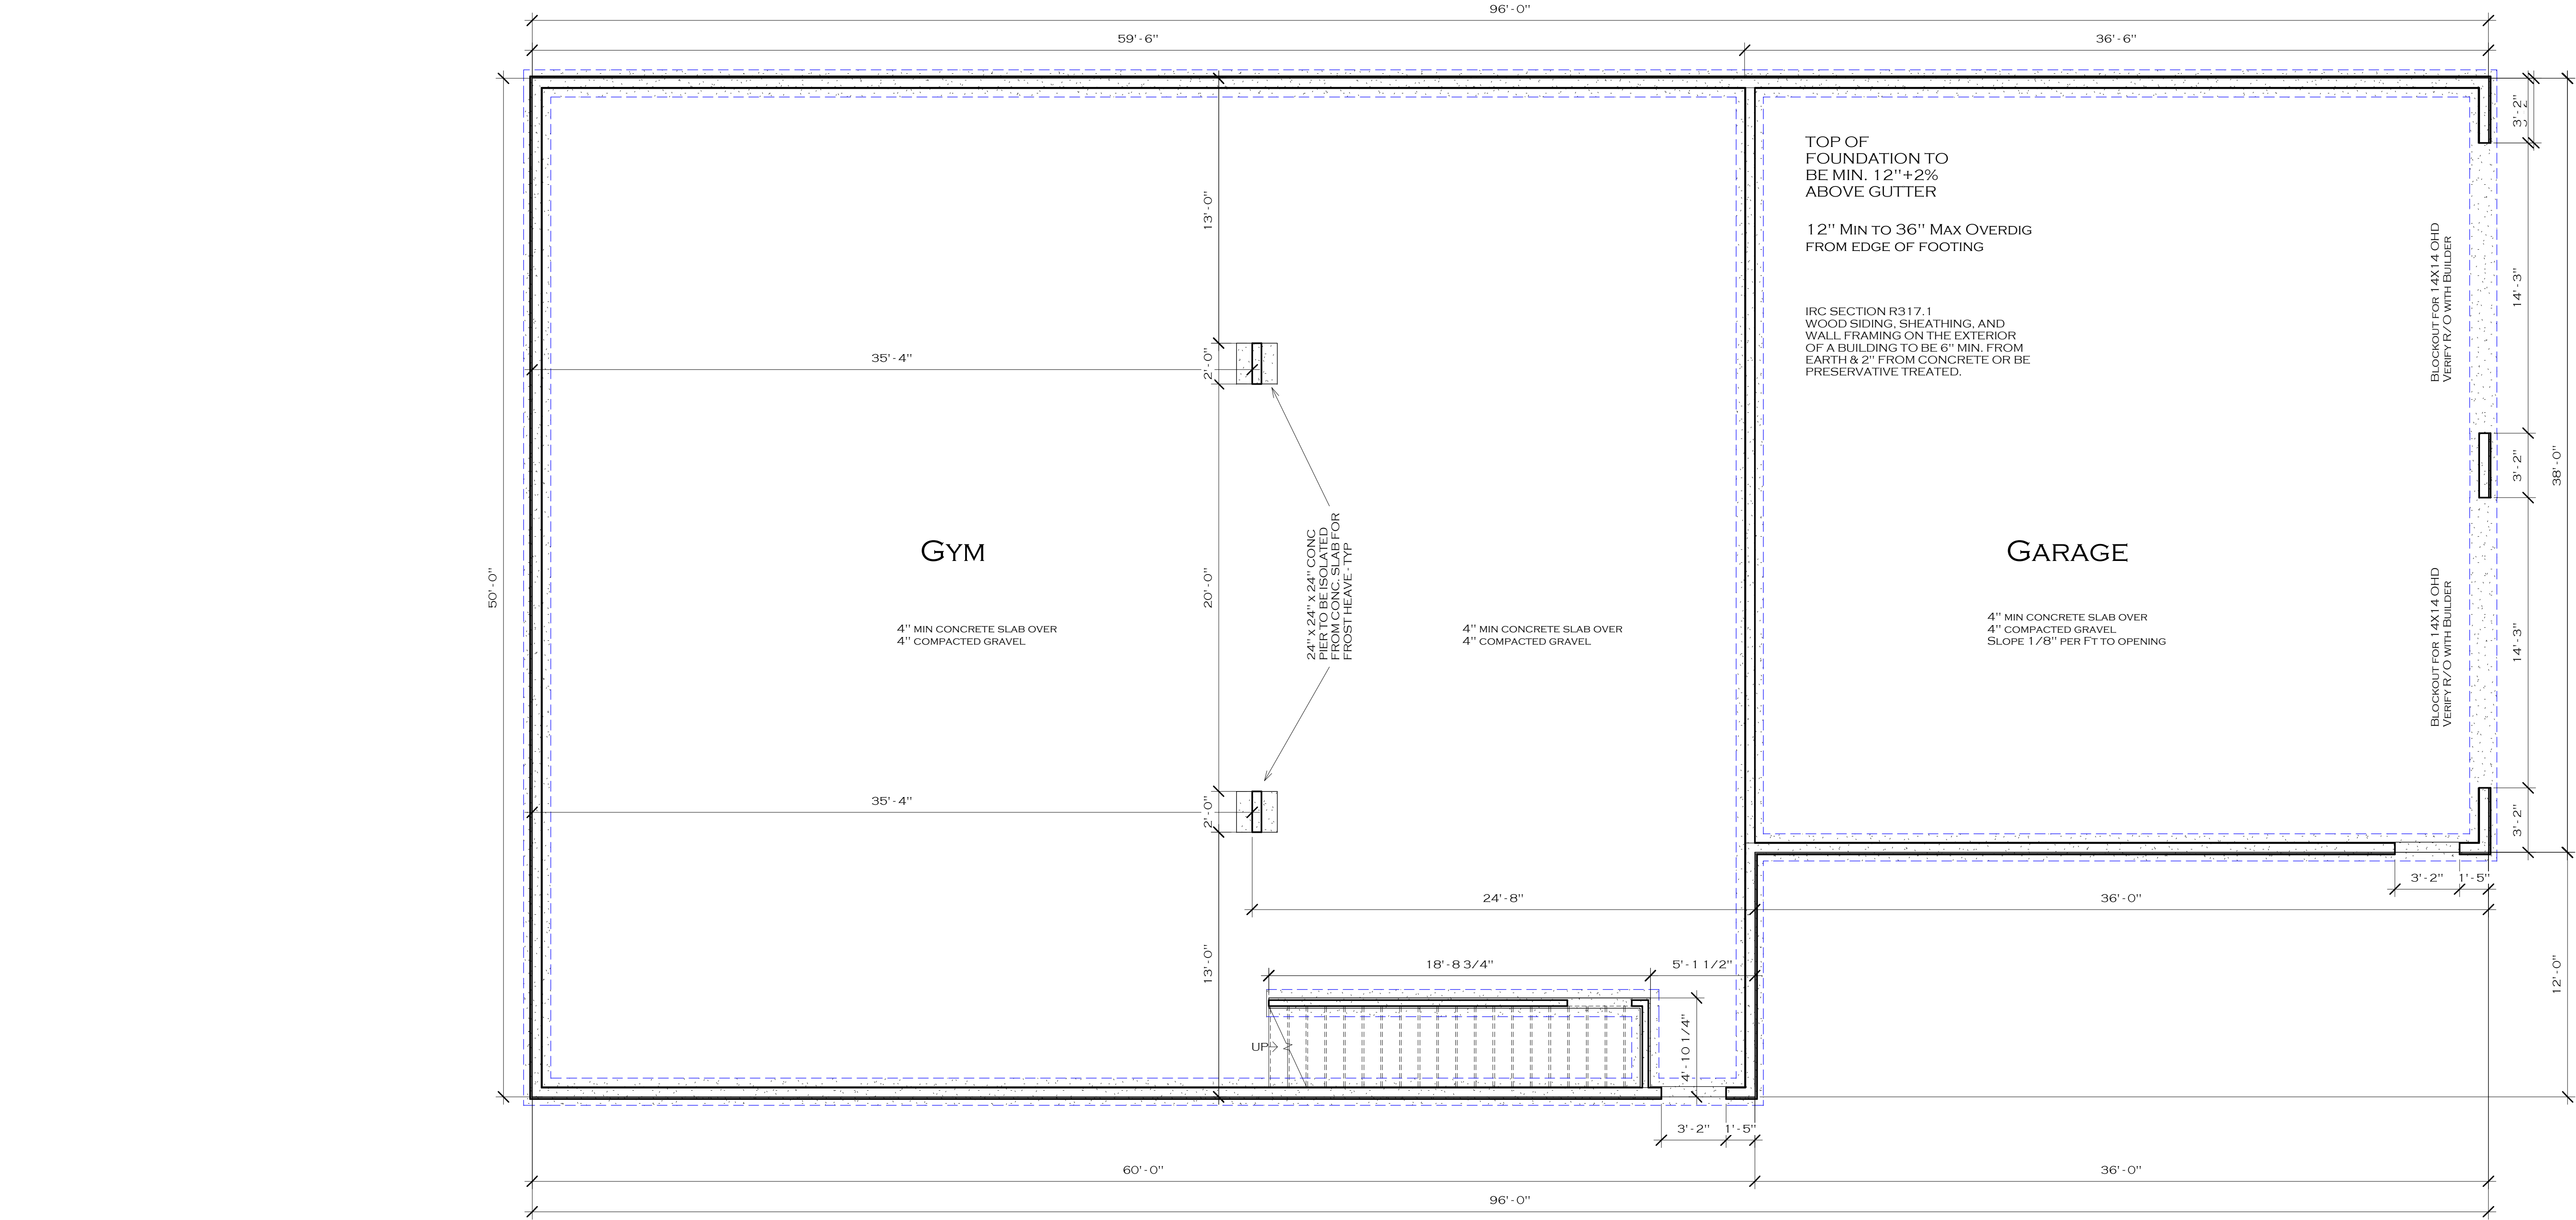

① Foundation
1/4" = 1'-0"

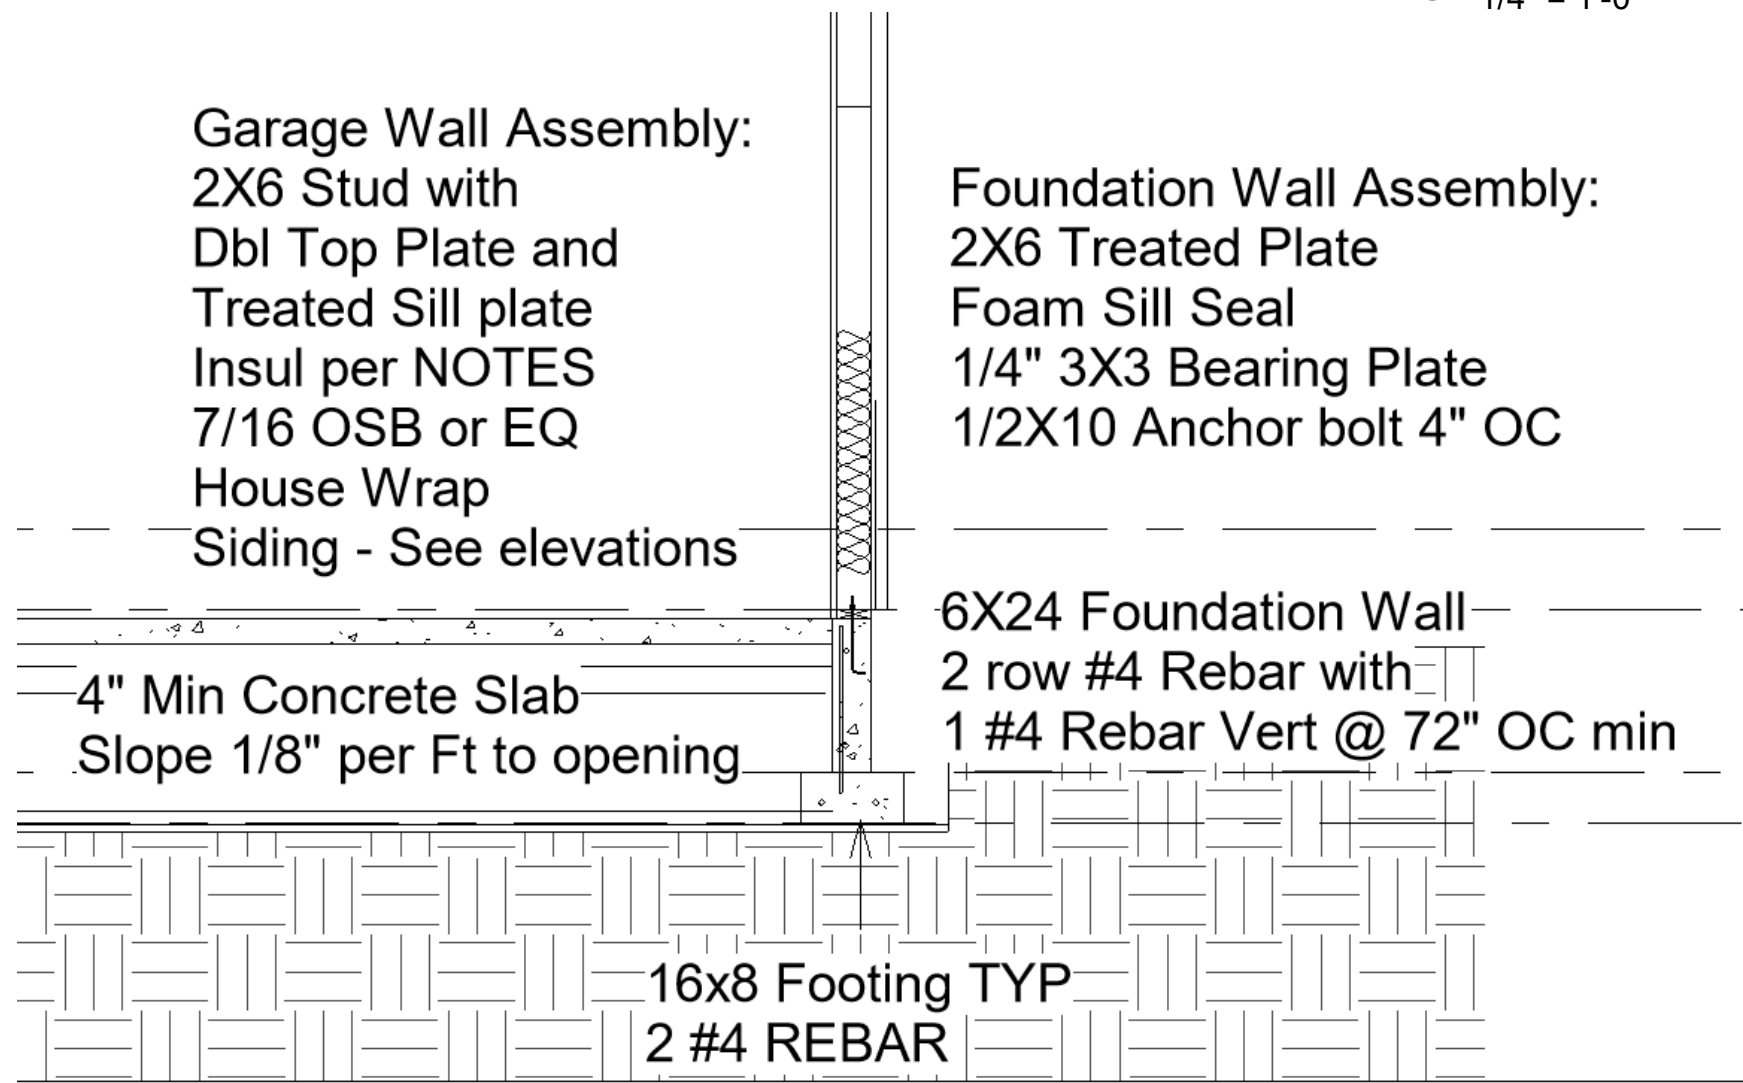

Designer is not a licenced
engineer and will claim no
responsibility for structural
items. The designer's liability
regarding errors and/or
omissions will be limited to
the correction of the original
drawings.



SCALE:
1/4" = 1'-0"

DRAWN BY:
James Wallace

DATE DRAWN:
07/04/21


LAST REVISED:

Lance LeBaron Homes
Clark Shop - 4066 N 3462 E
Lot 21A Prescott Acres - Kimberly

SHEET:

A2

PLAN NAME:
Foundation

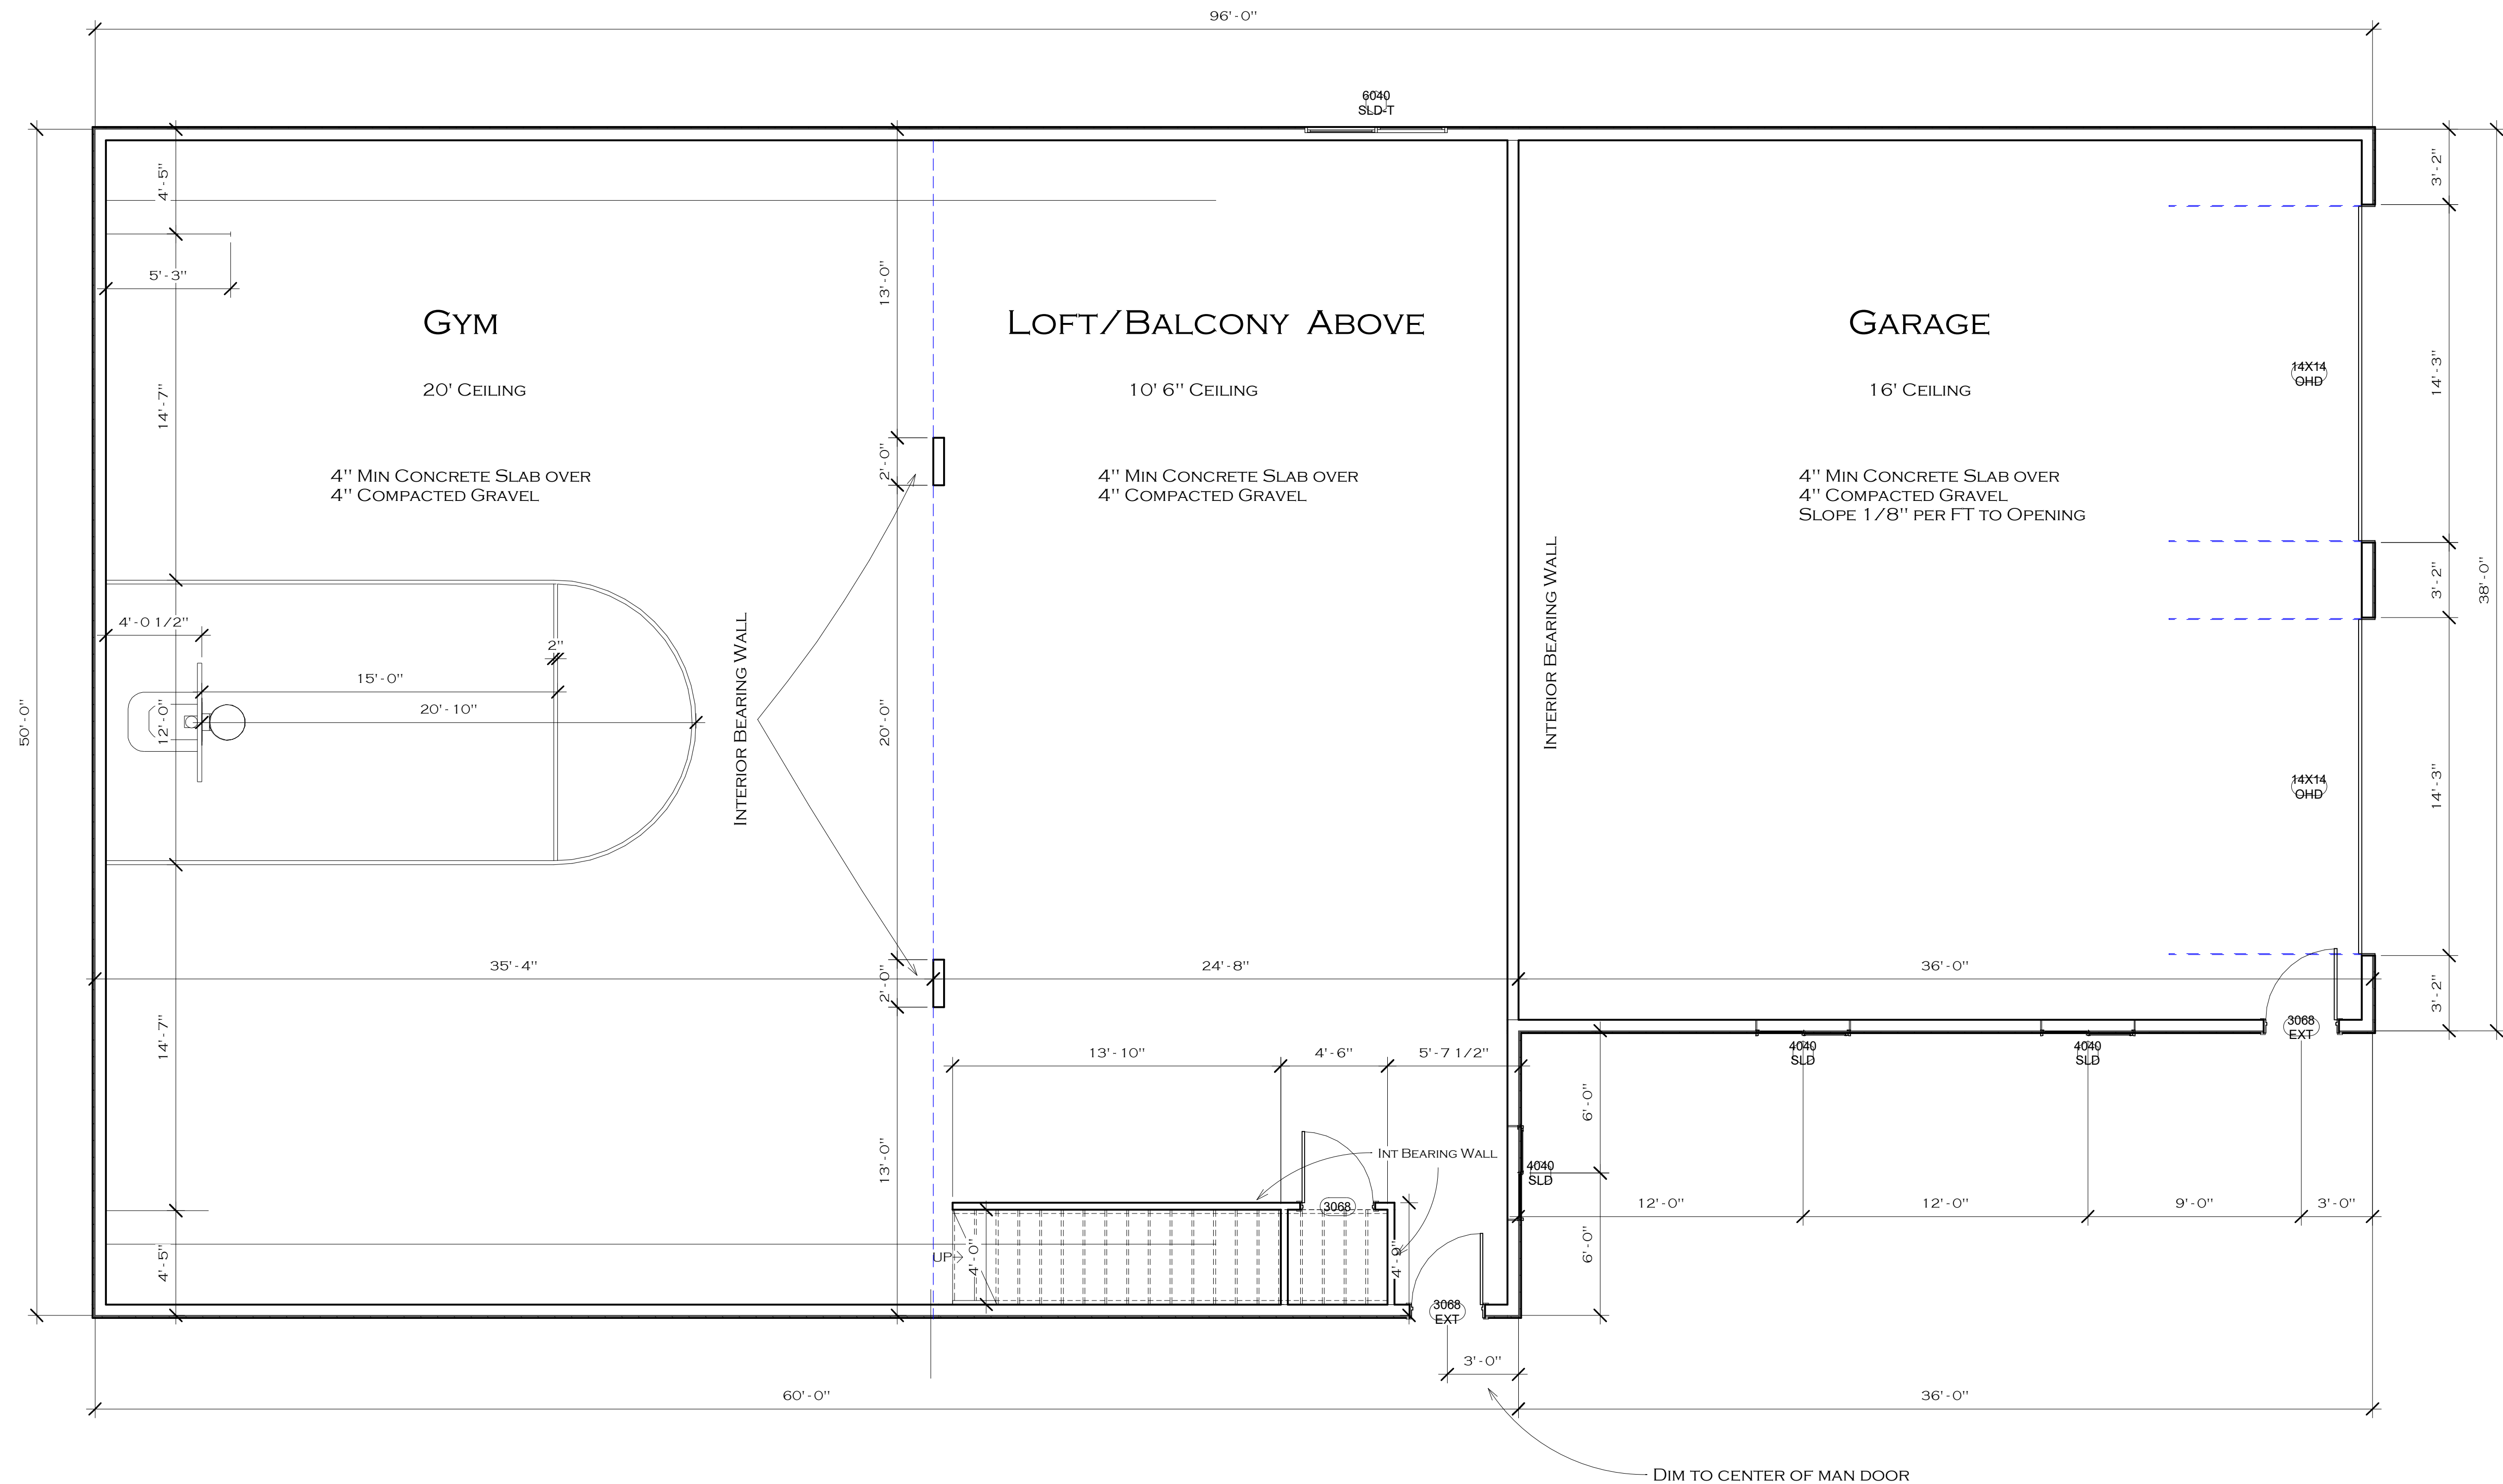

① First Floor
1/4" = 1'-0"

ENERGY COMPLIANCE
PRESCRIPTIVE ENERGY CODE
R-30 MIN IN FLOORS
R-20 MIN IN WALLS
R-38 MIN IN ATTIC SPACES OVER LIVING AREA
.35 U-VALUE MIN LOW-E WINDOWS

ALL HEADERS (2) 2X10 UNO

Designer is not a licensed engineer and will claim no responsibility for structural items. The designer's liability regarding errors and/or omissions will be limited to the correction of the original drawings.



SCALE:
1/4" = 1'-0"

DRAWN BY:
James Wallace

DATE DRAWN:
07/04/21

LAST REVISED:

Lance LeBaron Homes
Clark Shop - 4066 N 3462 E
Lot 21A Prescott Acres - Kimberly


SHEET:

A3

PLAN NAME:
Main Floor

ENERGY COMPLIANCE
PRESCRIPTIVE ENERGY CODE
R-30 MIN IN FLOORS
R-20 MIN IN WALLS
R-38 MIN IN ATTIC SPACES OVER LIVING AREA
.35 U-VALUE MIN LOW-E WINDOWS

ALL HEADERS (2) 2x10 UNO

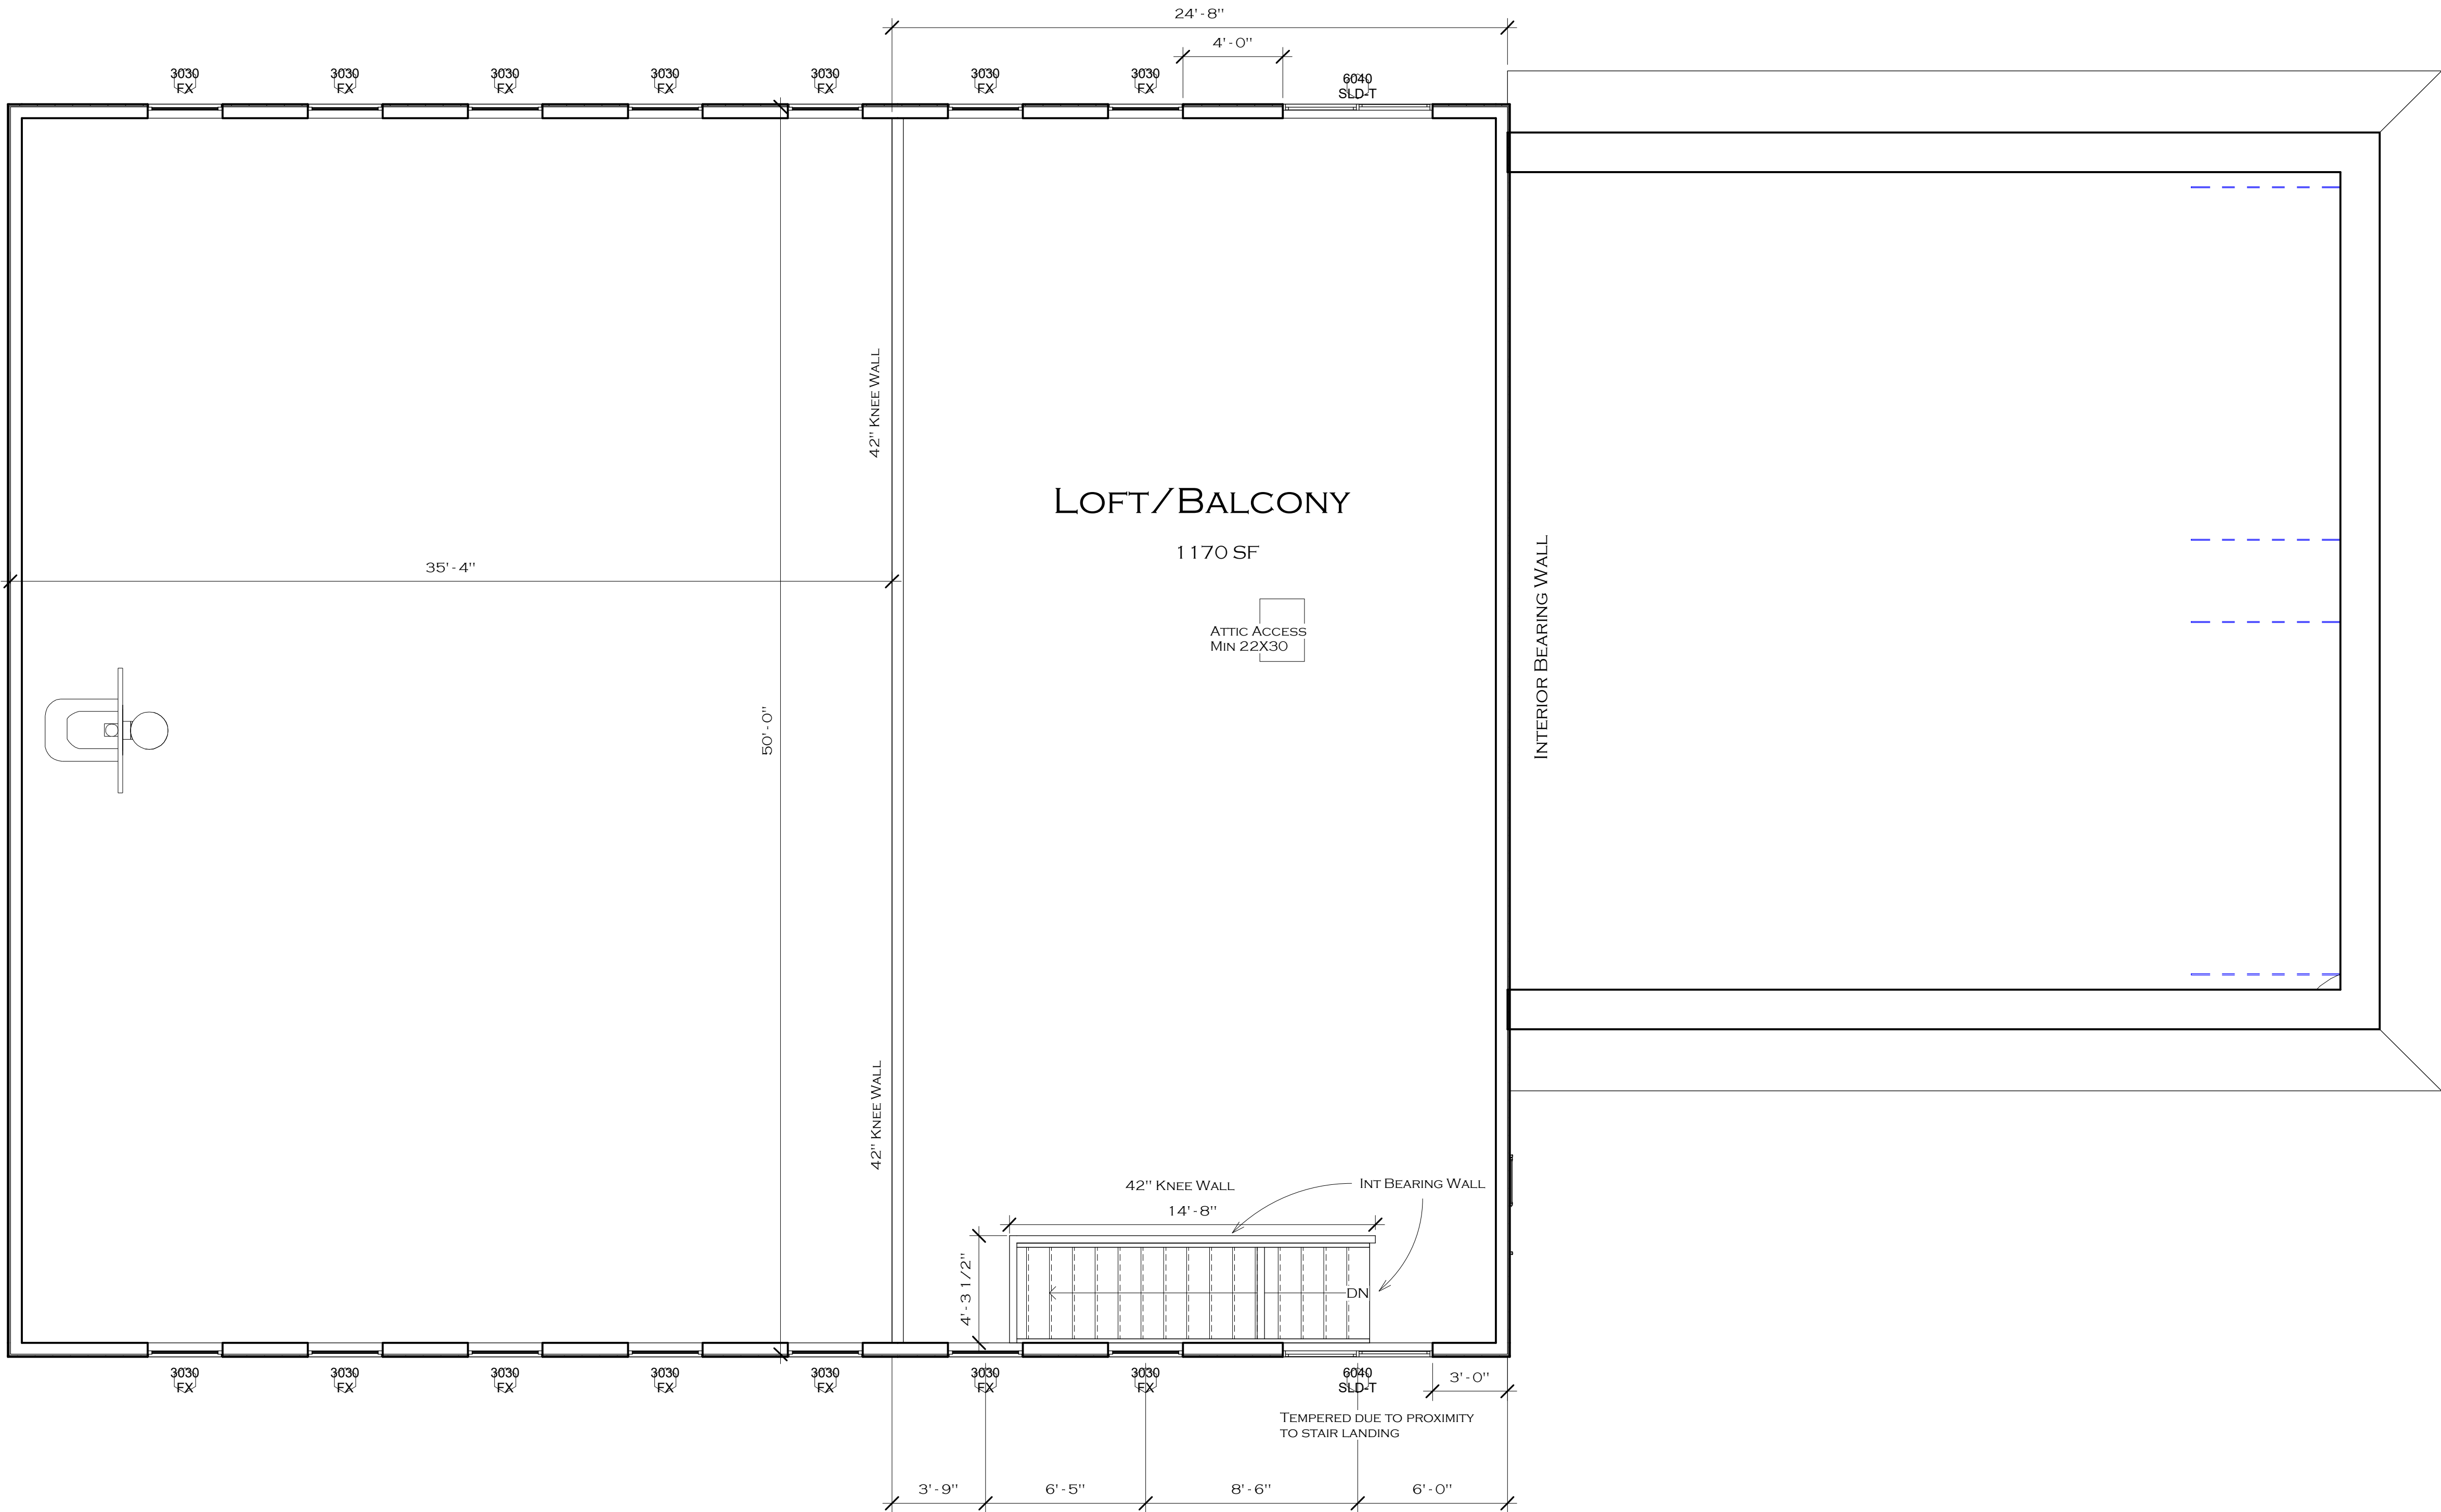

① Balcony Floor
1/4" = 1'-0"

Designer is not a licenced engineer and will claim no responsibility for structural items. The designer's liability regarding errors and/or omissions will be limited to the correction of the original drawings.



SCALE:
1/4" = 1'-0"

DRAWN BY:
James Wallace

DATE DRAWN:
07/04/21


LAST REVISED:

Lance LeBaron Homes
Clark Shop - 4066 N 3462 E
Lot 21A Prescott Acres - Kimberly

SHEET:

A4

PLAN NAME:
Balcony Plan

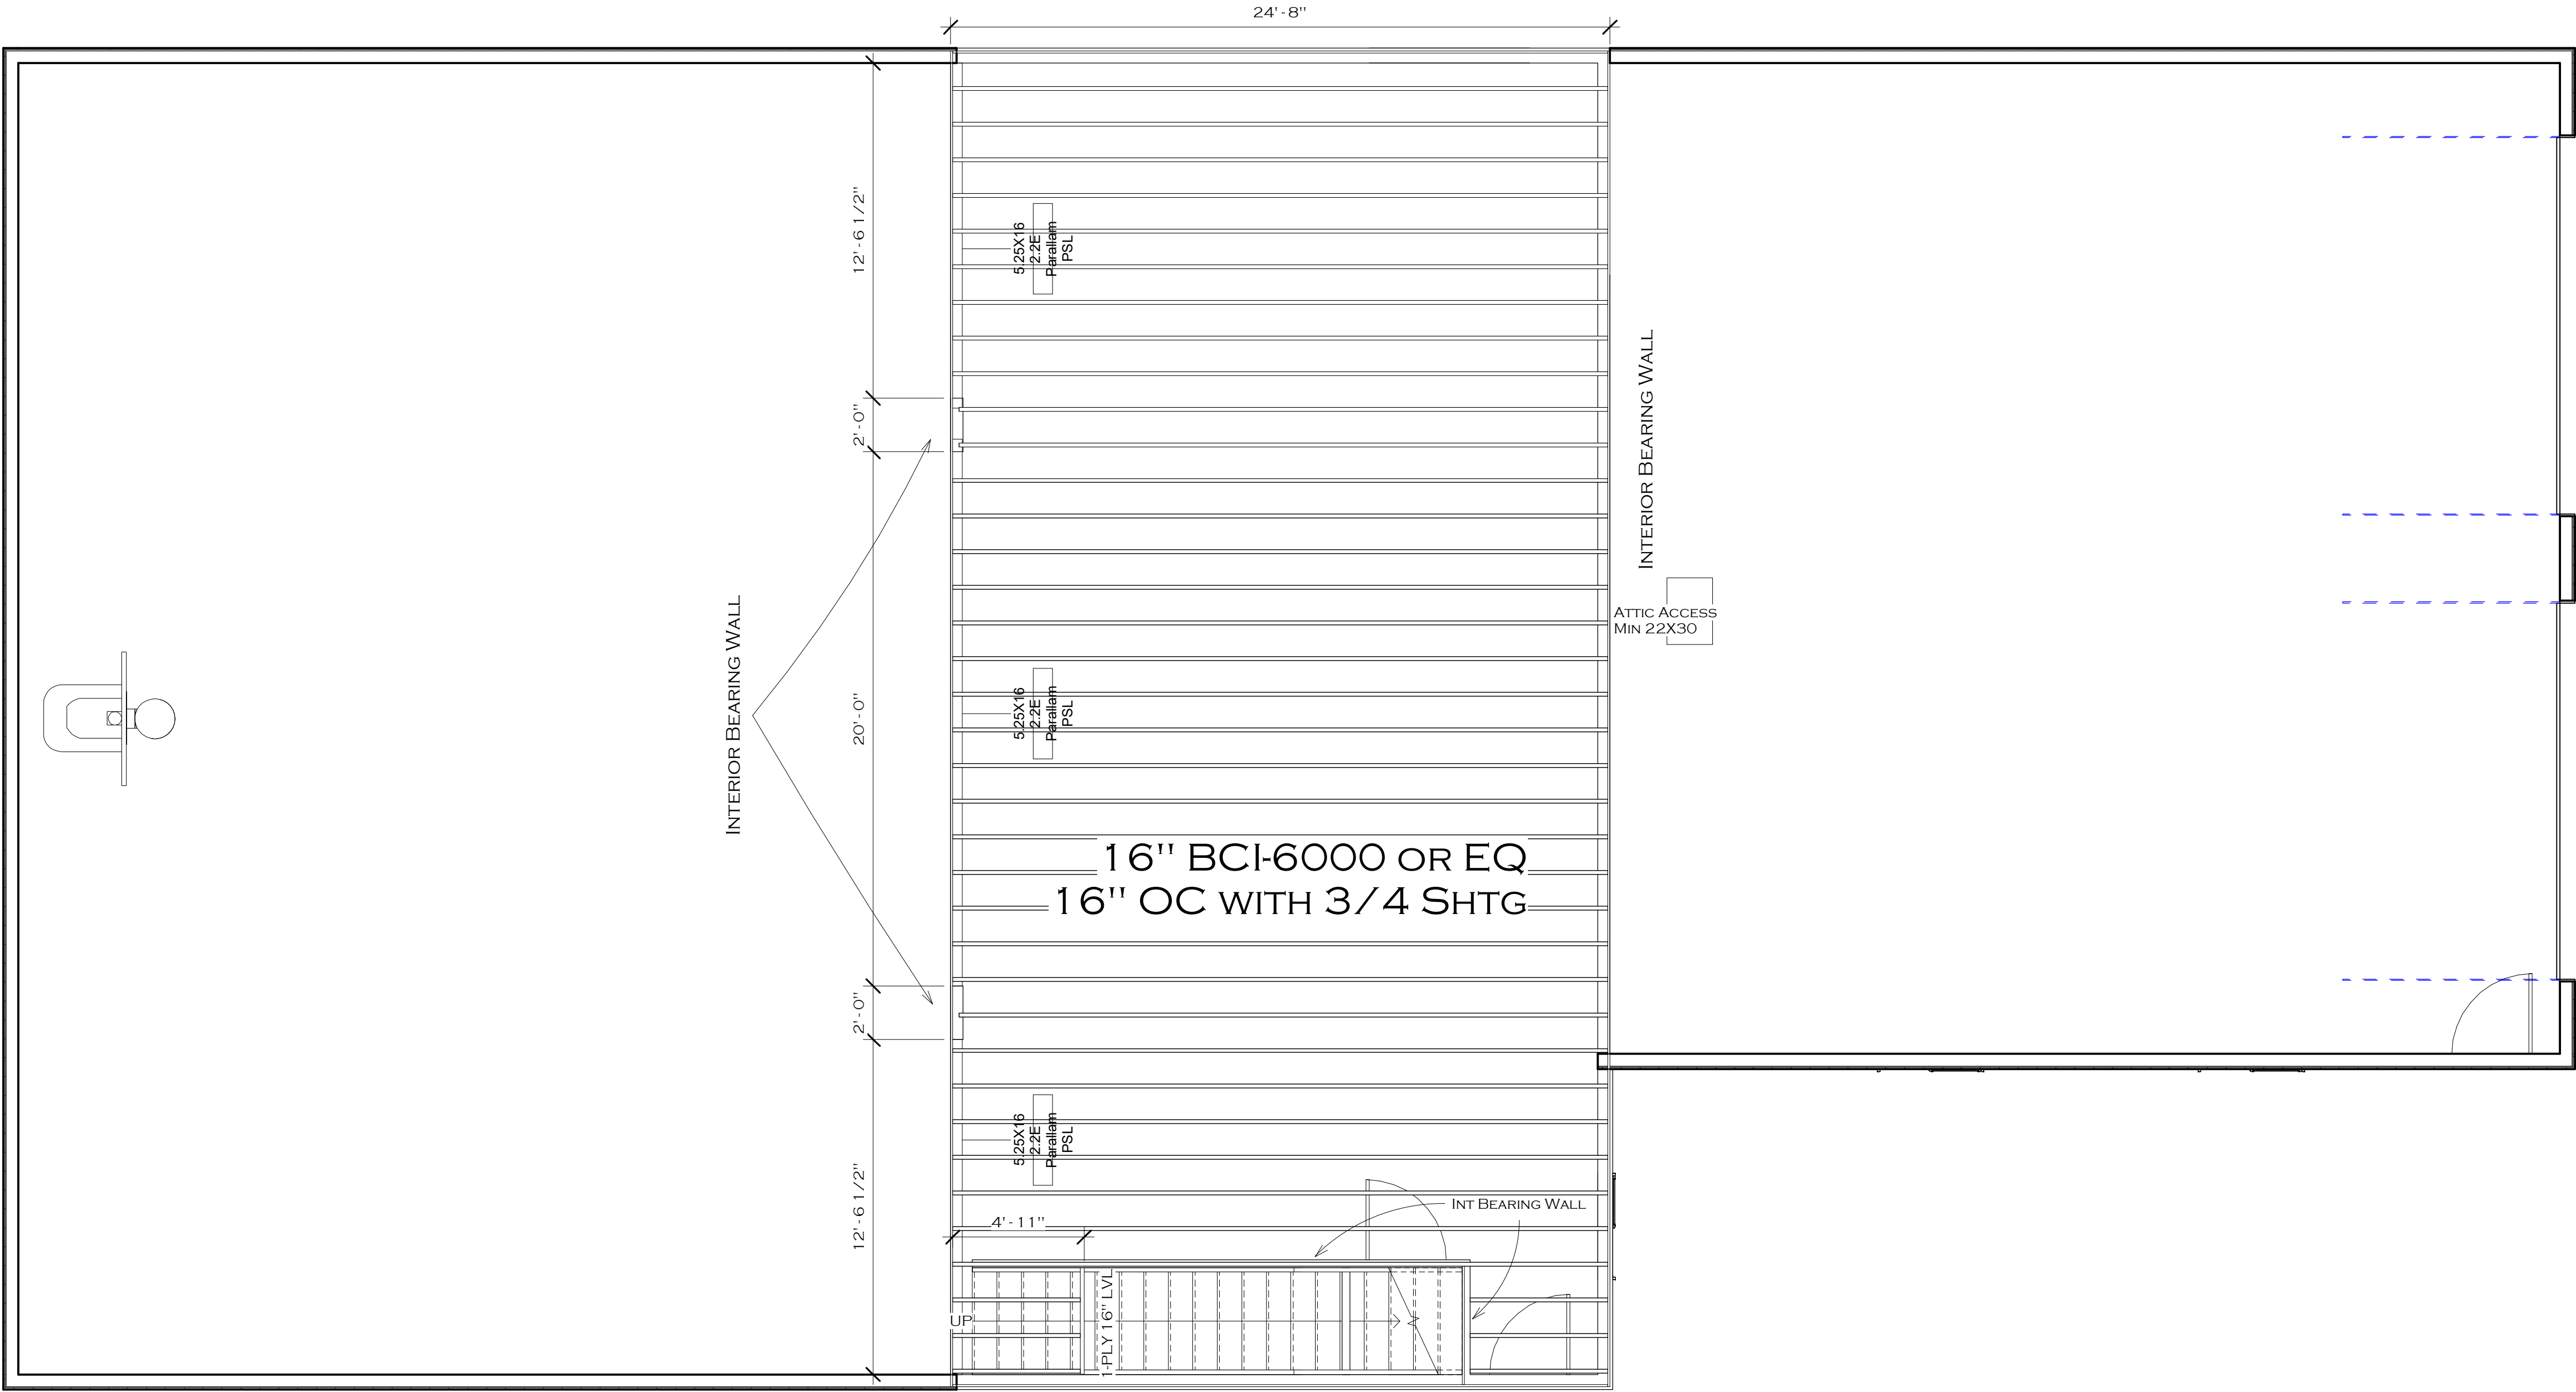

1 Balcony Framing
1/4" = 1'-0"

ENERGY COMPLIANCE
PRESCRIPTIVE ENERGY CODE
R-30 MIN IN FLOORS
R-20 MIN IN WALLS
R-38 MIN IN ATTIC SPACES OVER LIVING AREA
.35 U-VALUE MIN LOW-E WINDOWS

ALL HEADERS (2) 2X10 UNO

Designer is not a licenced engineer and will claim no responsibility for structural items. The designer's liability regarding errors and/or omissions will be limited to the correction of the original drawings.



SCALE:
1/4" = 1'-0"

DRAWN BY:
James Wallace

DATE DRAWN:
07/04/21


LAST REVISED:

Lance LeBaron Homes
Clark Shop - 4066 N 3462 E
Lot 21A Prescott Acres - Kimberly

SHEET:

A5

PLAN NAME:
Blacony Framing

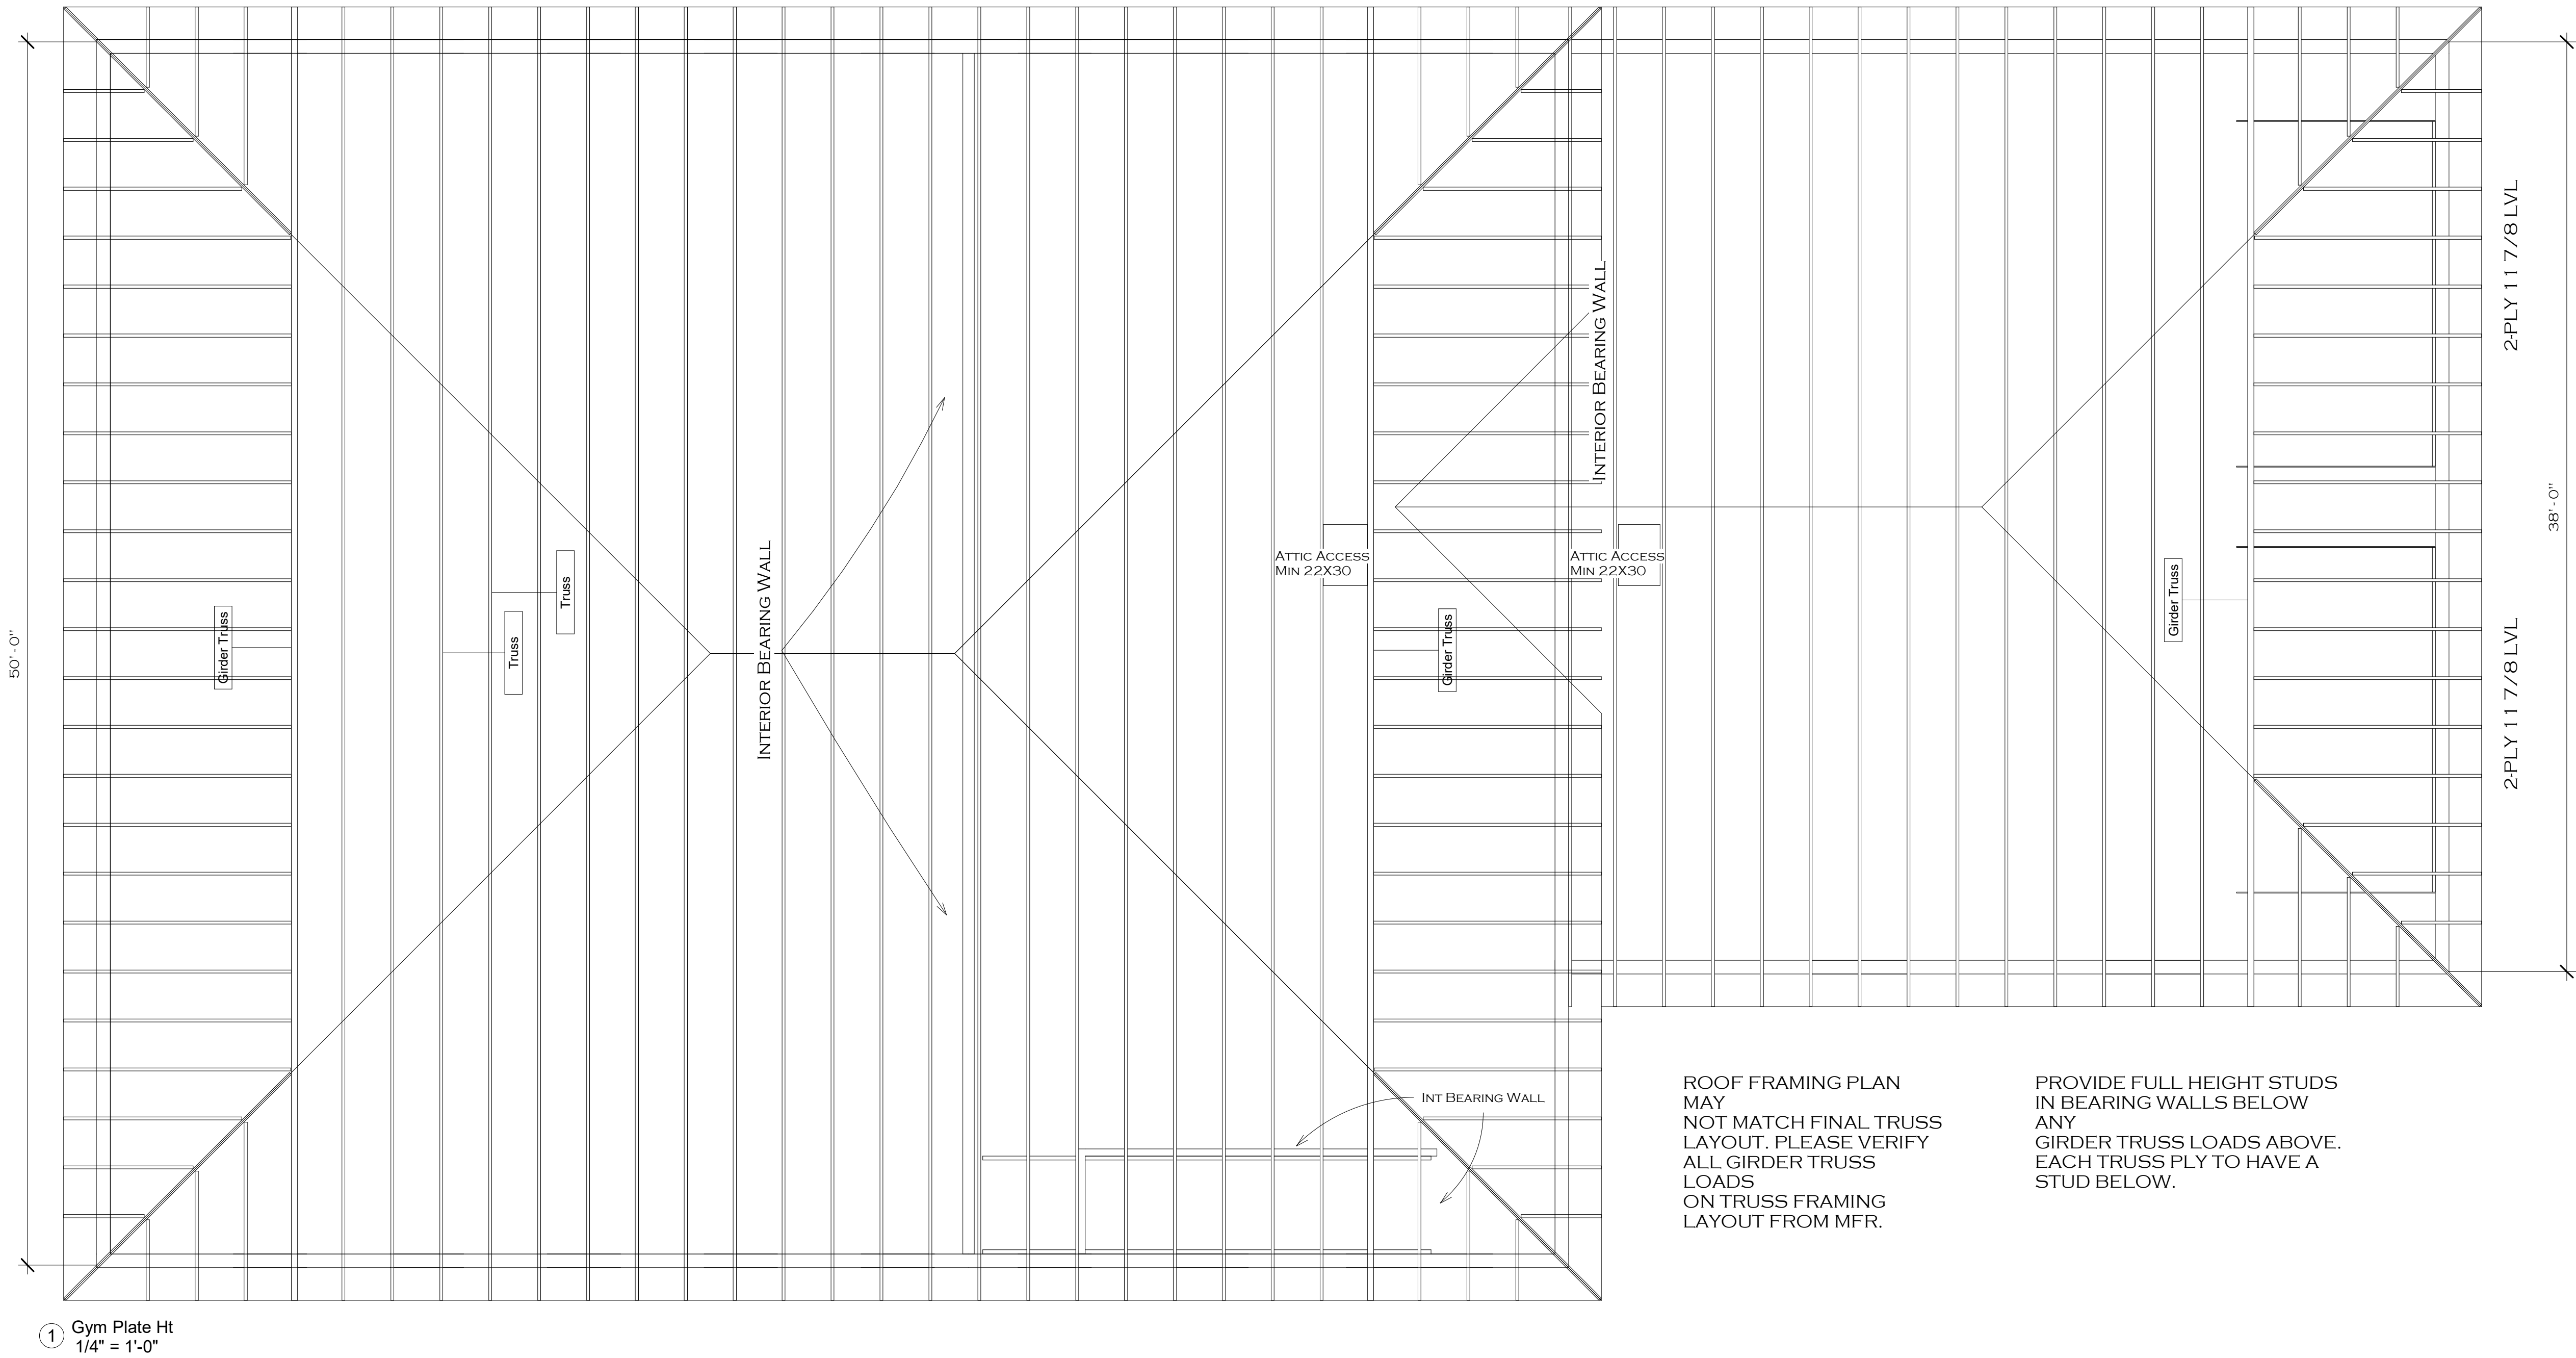

ENERGY COMPLIANCE
PRESCRIPTIVE ENERGY CODE
R-30 MIN IN FLOORS
R-20 MIN IN WALLS
R-38 MIN IN ATTIC SPACES OVER LIVING AREA
.35 U-VALUE MIN LOW-E WINDOWS

ALL HEADERS (2) 2x10 UNO

Designer is not a licenced engineer and will claim no responsibility for structural items. The designer's liability regarding errors and/or omissions will be limited to the correction of the original drawings.



WALLACE
BUILDING DESIGN

Twin Falls, ID 83301, ph: 208-404-3498
Email: Wallacebuildingdesign@gmail.com

SCALE:
1/4" = 1'-0"
DRAWN BY:
James Wallace
DATE DRAWN:
07/04/21
LAST REVISED:


Lance LeBaron Homes
Clark Shop - 4066 N 3462 E
Lot 21A Prescott Acres - Kimberly

SHEET:


A6

PLAN NAME:

Roof Framing

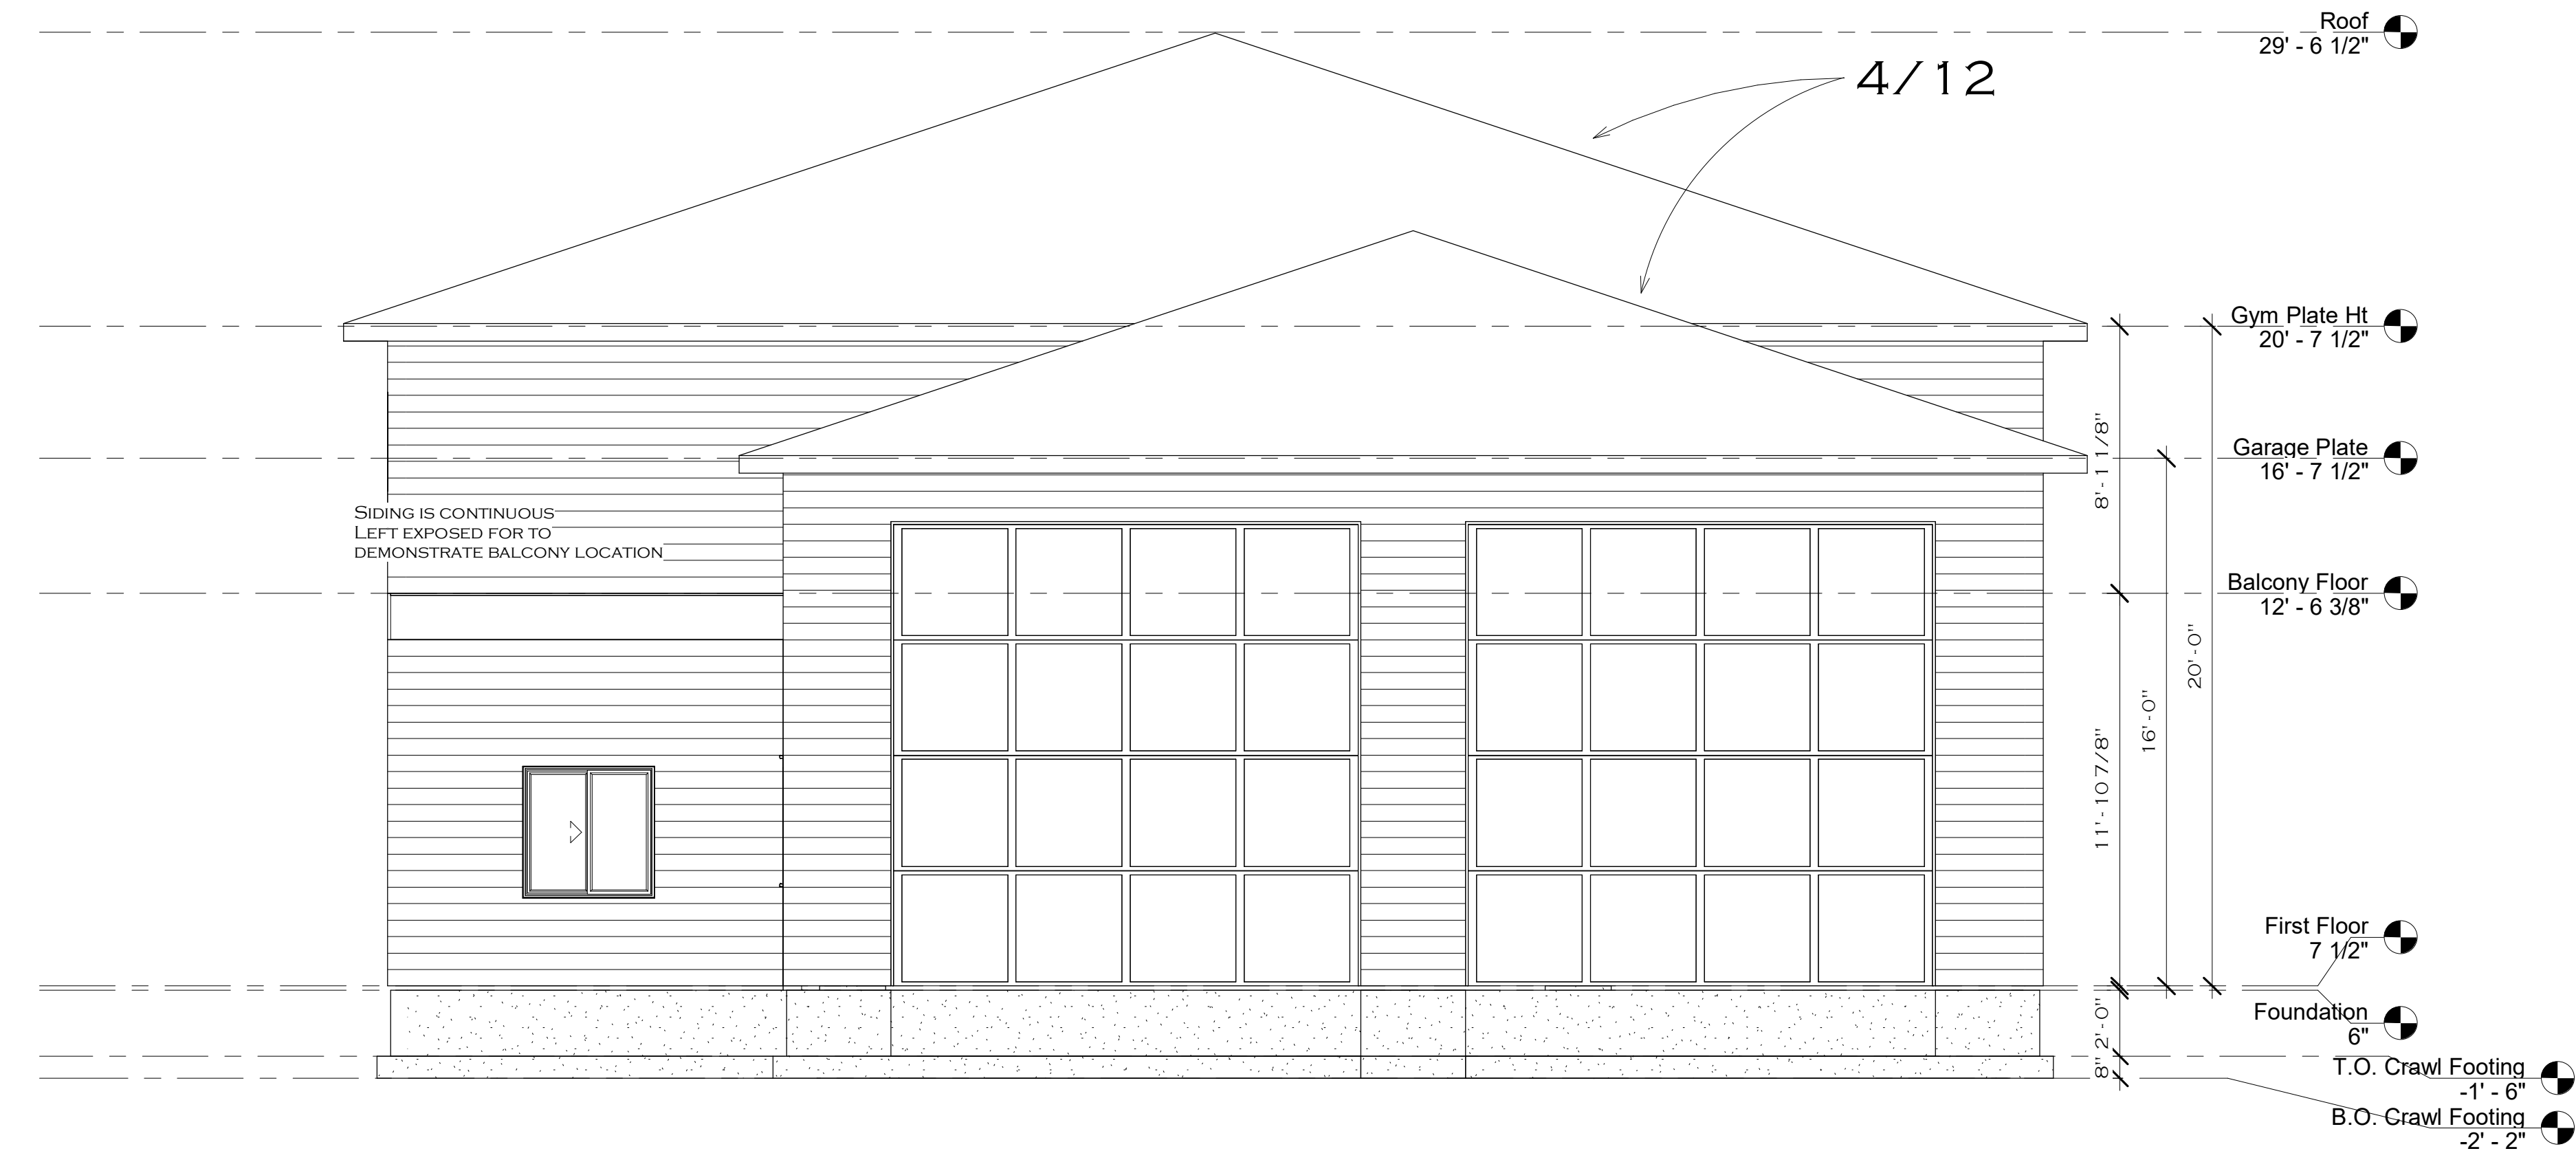

① Front
1/4" = 1'-0"

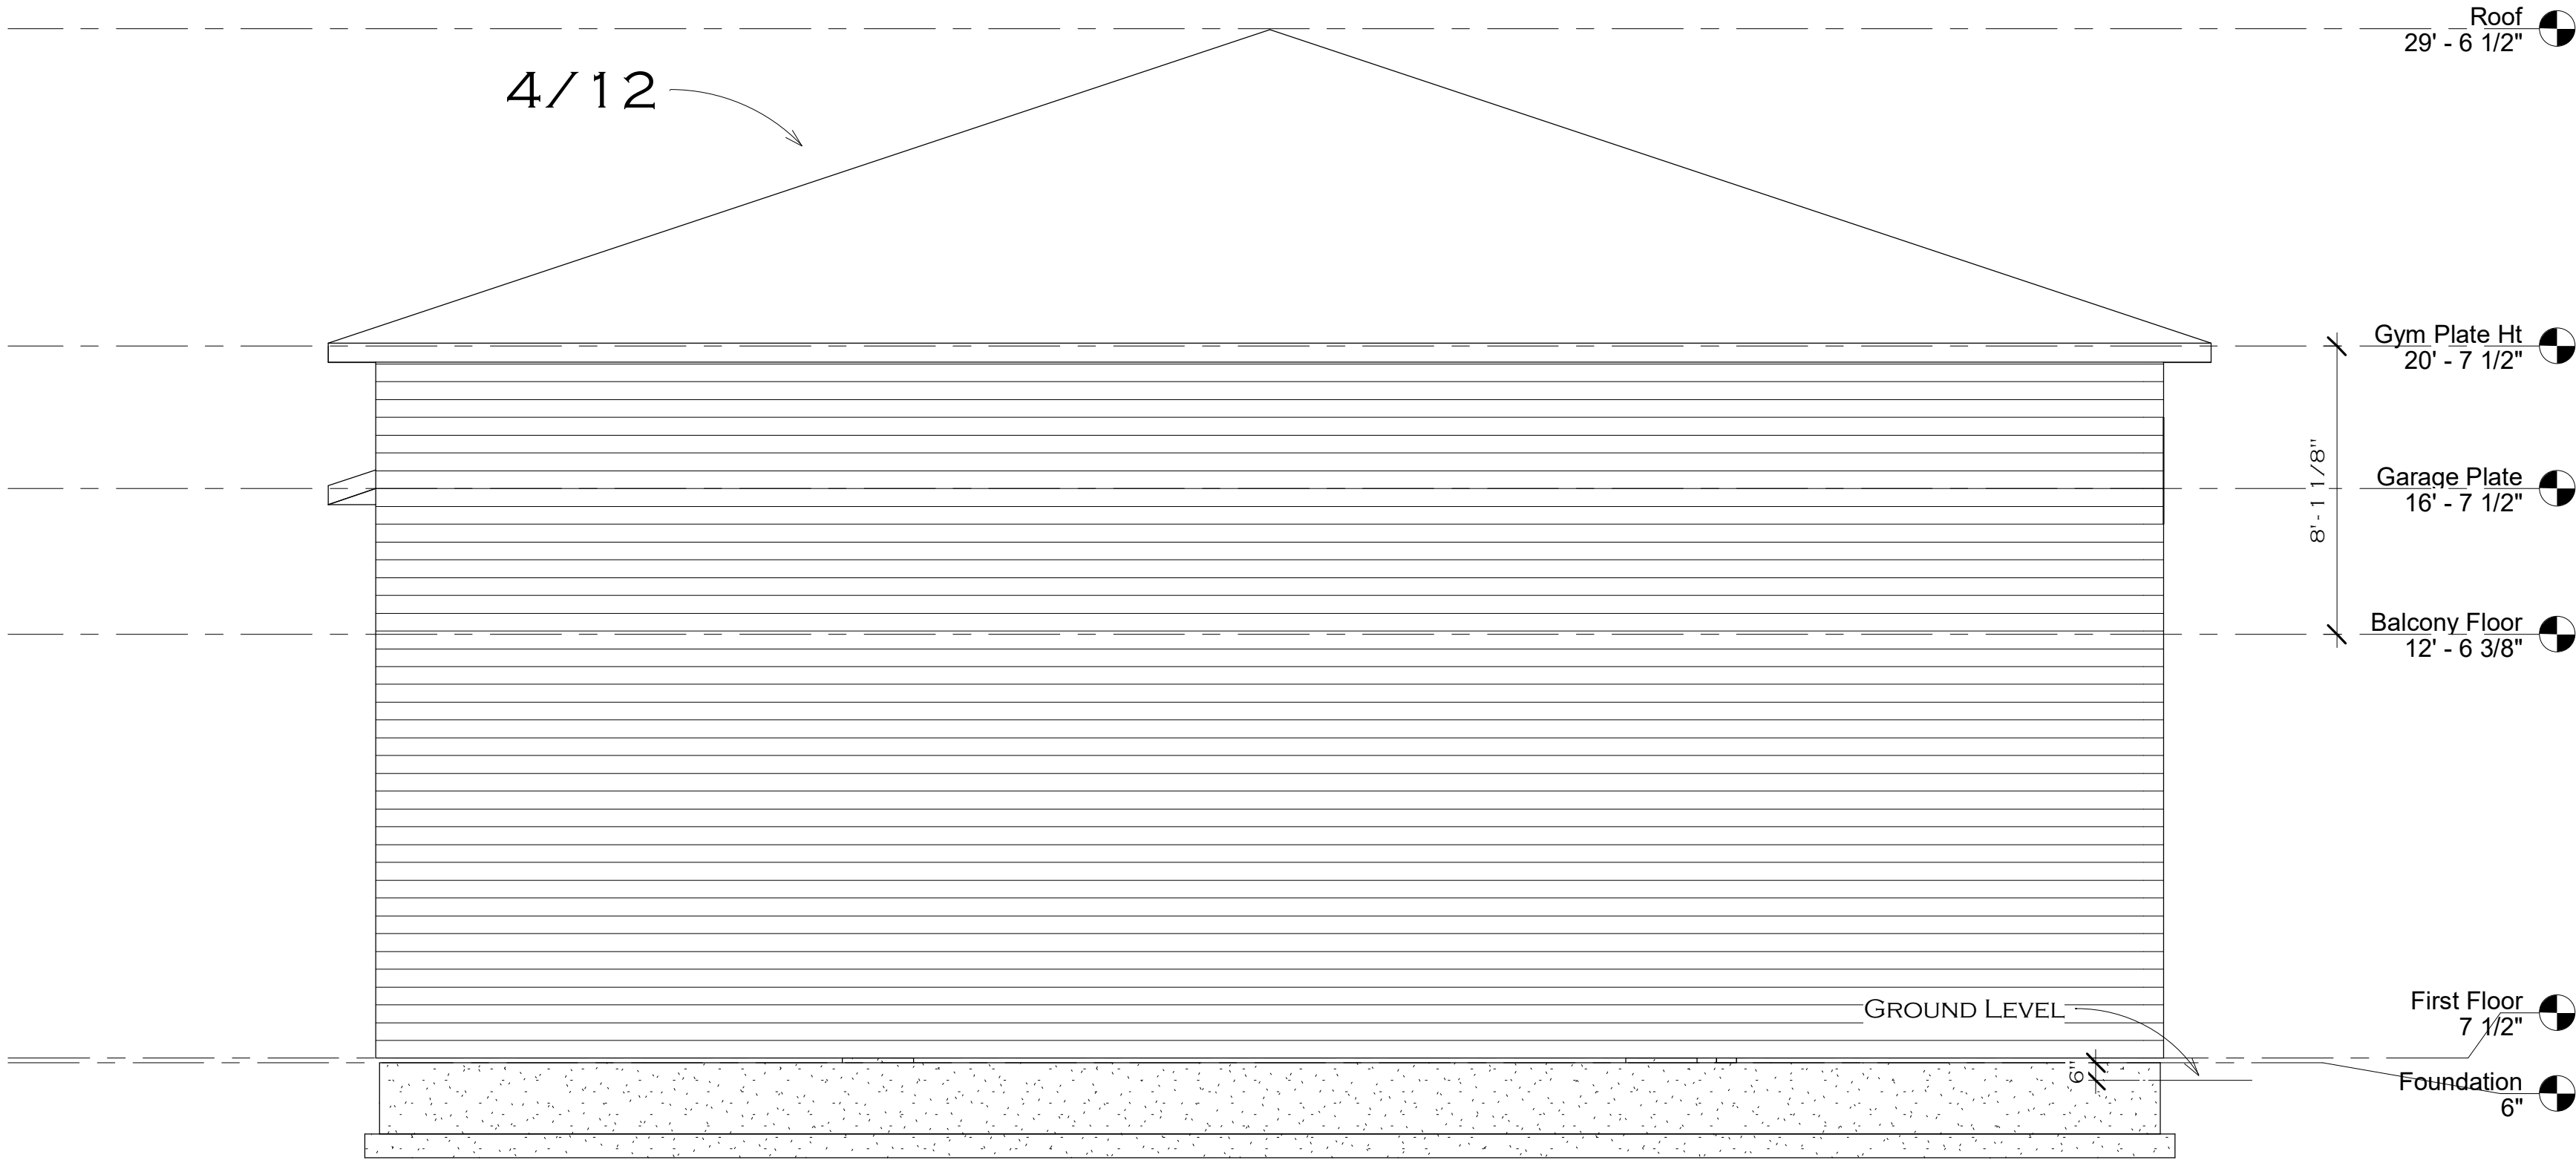

② Rear
1/4" = 1'-0"

Designer is not a licenced engineer and will claim no responsibility for structural items. The designer's liability regarding errors and/or omissions will be limited to the correction of the original drawings.



SCALE:
1/4" = 1'-0"

DRAWN BY:
James Wallace

DATE DRAWN:
07/04/21


LAST REVISED:

Lance LeBaron Homes
Clark Shop - 4066 N 3462 E
Lot 21A Prescott Acres - Kimberly


SHEET:

A7

PLAN NAME:
Elevations

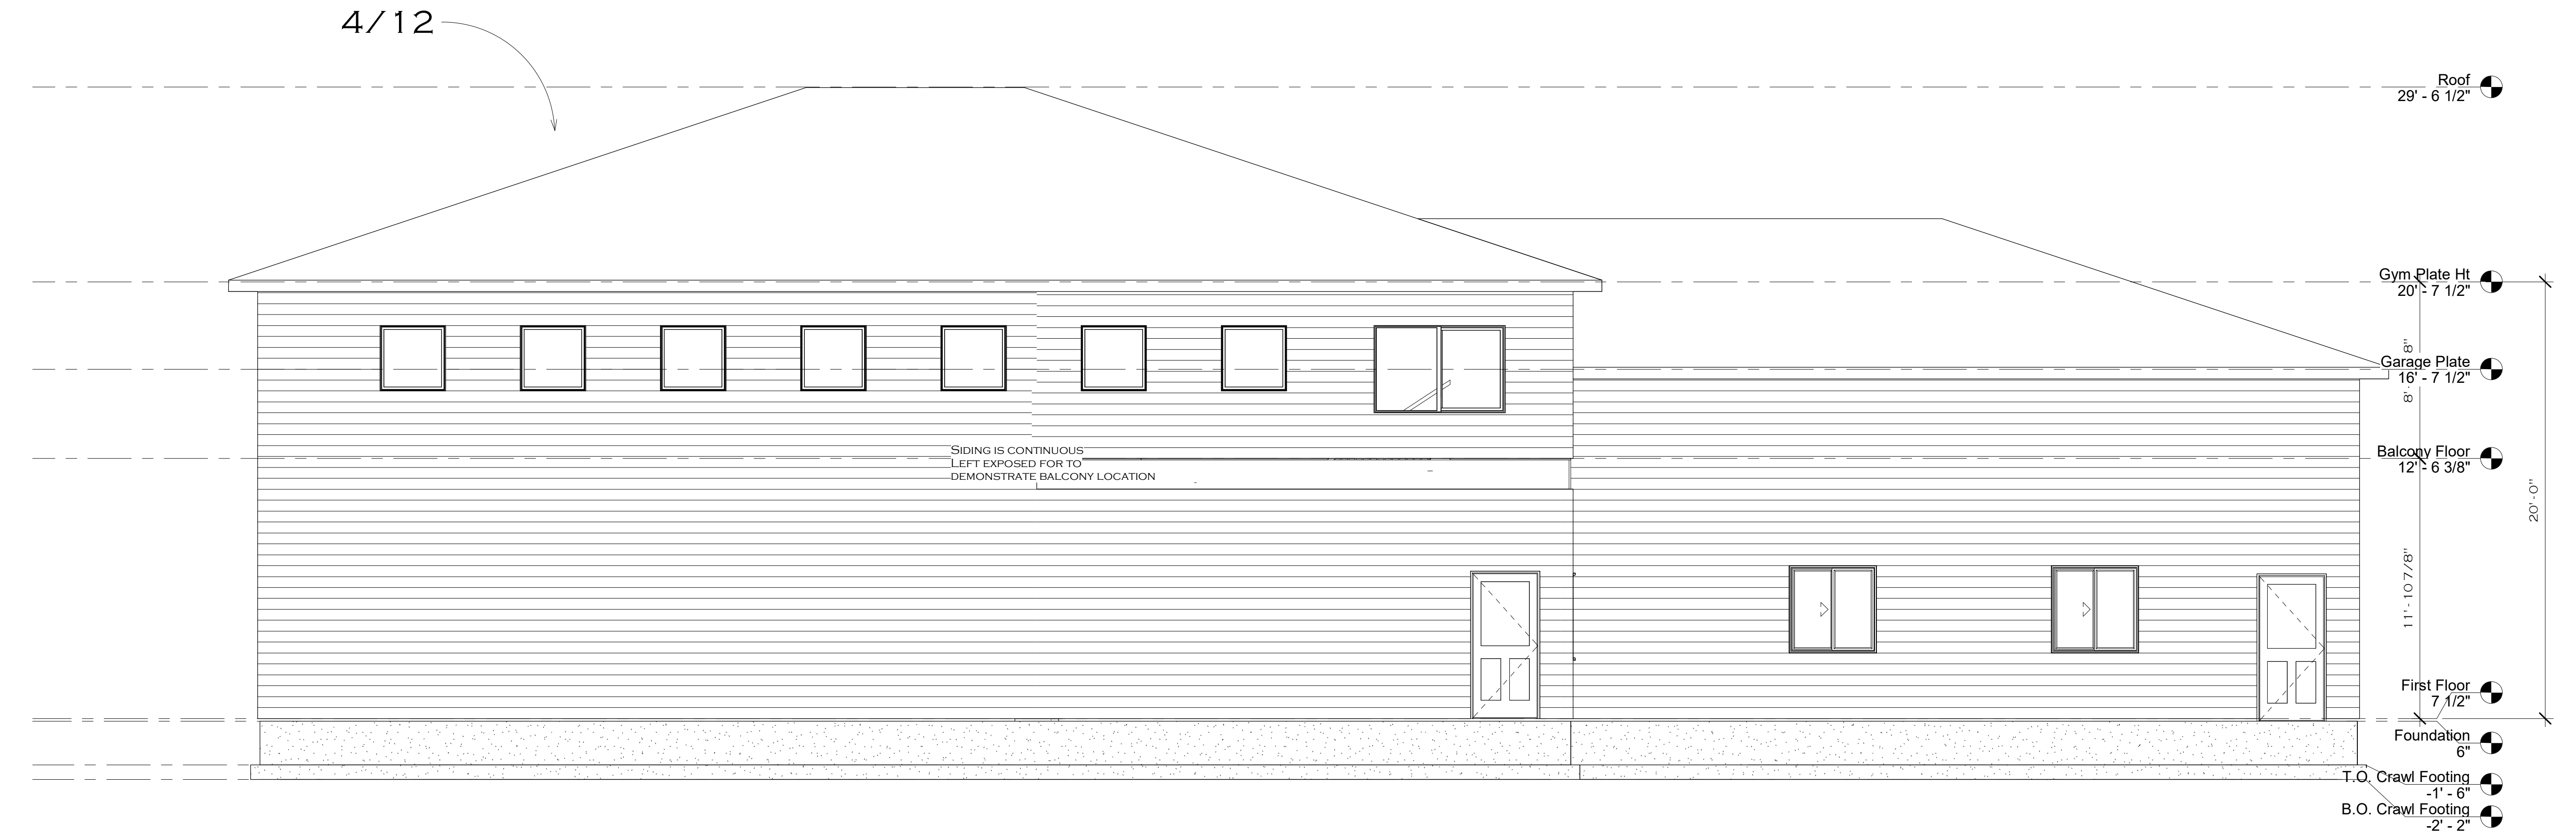

① Left
1/4" = 1'-0"

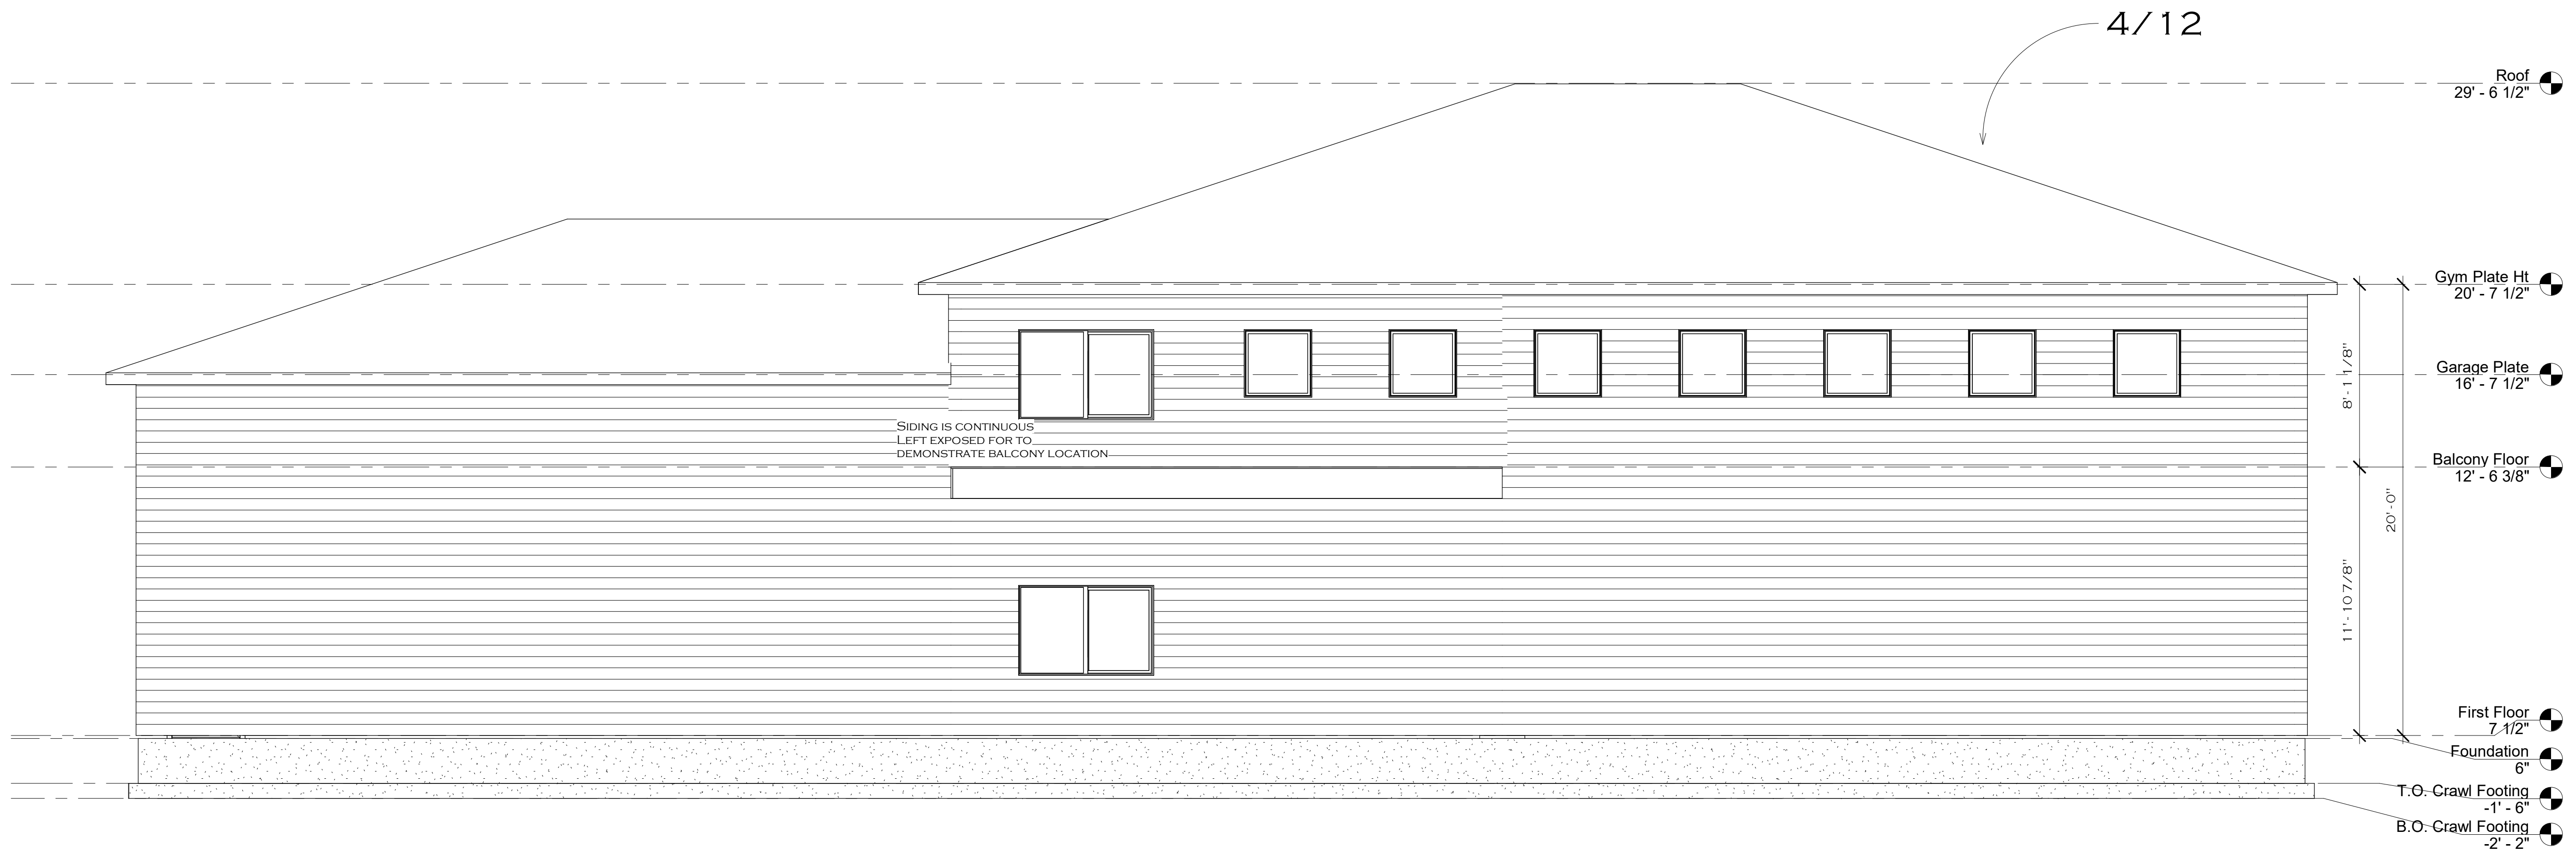

Designer is not a licenced engineer and will claim no responsibility for structural items. The designer's liability regarding errors and/or omissions will be limited to the correction of the original drawings.



Twin Falls, ID 83301, ph: 208-404-3498
Email: Wallacebuildingdesign@gmail.com

SCALE:
1/4" = 1'-0"

DRAWN BY:
James Wallace

DATE DRAWN:
07/04/21


LAST REVISED:

Lance LeBaron Homes
Clark Shop - 4066 N 3462 E
Lot 21A Prescott Acres - Kimberly

SHEET:

A8

PLAN NAME:
Elevations

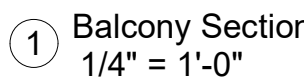

Sections/Details