

GENERAL NOTES:

SITE NOTES:
* DO NOT DRAIN STORM WATER ONTO ADJACENT LOTS.
* SLOPE GRADE AWAY FROM FOUNDATION 6" IN 10' MIN.
WATER RUNOFF TO BE CONTAINED TO LOT.
* FINISH FLOOR ELEVATION TO BE 15' ABOVE TOP OF CURB



FOUNDATION/CONC NOTES:
* PROVIDE EXPANSION JOINTS IN ALL FLATWORK AND ISOLATED POST FOOTINGS FOR ALL POSTS
* ALL FOUNDATION WALLS SHALL BE MIN OF 3000#/SQ IN COMPRESSIVE STRENGTH @ 28 DAYS
* ALL FLATWORK SHALL BE MIN OF 3500#/SQ IN COMPRESSIVE STRENGTH @ 28 DAYS
* DESIGNER ASSUMES NO RESPONSIBILITY FROR STRUCTURAL INTEGRITY. VERIFY ALL STRUCTURAL SPECS W/ MANUF., TRUSS VENDOR, OR ENG
* ALL PONY WALLS PARALLEL TO JOISTS FRAMED TO BOTTOM OF FLOOR SHEATHING OR SOLID BLOCK ABOVE
* FRAME ALL BEARING WALLS IN CRAWL SPACE TO BOTTOM OF FLOOR SHEATHING OR SOLID BLOCK ABOVE
* PROVIDE DAMP PROOFING ON ALL EXTERIOR FOUNDATION WALLS BELOW GRADE
* ANY NAILS THAT PENITRATE CONCRETE OR P.T. LUMBER TO BE HOT DIPPED GALVINIZED OR EQUAL
* FOUNDATION VENTING 1 SQ FT/150 SQ FT OF CRAWL SPACE W/O VAPOR BARRIER OR 1 SQ FT/1500 SQ FT OF CRAWL SPACE WITH VAPOR BARRIER-MAX 36" FROM EACH CORNER

JOIST NOTES:
* INSTALL RIM JOISTS & SQUASH BLOCKS AS PER MANUFACTURE SPECIFICATIONS.
* USE 5000s 1.7 BCI FLOOR JOISTS OR EQUAL. INSTALL AS PER MANUFACTURE SPECIFICATIONS
USE RIM BOARD AND INSTALL AS PER MANUFACTURE SPECS.
* BLOCK OR HEADER ANY CUT/DAMAGED I-JOIST AS REQUIRED

FRAMING NOTES:
* 18"x24" CRAWL SPACE ACCESS REQUIRED WITHIN 20' OF ALL UNDER FLOOR CLEANOUTS
* DOOR FROM GARAGE TO HOUSE TO BE 20 MIN SELF CLOSING FIRE DOOR
* CABINET BACKING HGTS. 32", 56" & 82" O.C.
* ROUGH IN WATER SOFTENER PER CODE
* 5/8" TYP "X" GYP BOARD IS REQ'D @ ALL GARAGE-TO-HOUSE WALLS AND CEILING
* EXTERIOR AND GARAGE WALLS TO BE 2X6 @ 24" O.C. AND INTERIOR WALLS TO BE 2X4 @ 16" O.C. UNLESS OTHERWISE SHOWN/NOTED ON FRAMING PLAN
* FRAMING PLAN SHOWS STRUCTURAL LUMBER AND DIMENSIONED TO EDGE OF LUMBER.
* PROVIDE SMOKE DETECTORS AS SHOWN ON FRAMING PLAN. SHALL SOUND AN AUDIBLE ALARM IN ALL SLEEPING AREAS AND HARD WIRED WITH BATTER BACKUP
* BATH AND RANGE HOOD FANS SHALL VENT TO OUTSIDE PER CODE
* ALL HEADERS TO BE (2) 2X8 UNLESS OTHERWISE NOTED ON PLANS OR CALLED OUT BY TRUSS ENGINEERING PACK
* CRAWL SPACE ACCESS REQ'D WITHIN 20' OF ALL UNDER FLOOR CLEANOUTS

ROOF NOTES
* TRUSS ENGINEERING DESIGN TO BE SUPPLIED BY VENDOR. TRUSS DESIGN IN THIS SET OF PLANS FOR REFERENCE ONLY.
* ATTIC ACCESS WITH 30" OF HEADROOM REQ'D
* ROOF TO BE PRE ENGINEERED TRUSSES INSTALLED AS PER MANUF. SPECS
* USE HURRICANE TIES AS REQ'D AND H-CLIPS BETWEEN ALL TRUSSES
* ROOF SHEETING IS TO BE 7/16" OSB, NAILED PER CODE
* EAVE OVERHANGS TO BE 16"
* 2X6 FASCIA
* THE ROOF PITCH IS TO BE 6:12 U.N.O.

INSULATE PER THE PERSCRIPTIVE METHOD:
* R-38 IN CEILING
* R-21 IN WALLS
* R-30 IN FLOORS
* .35 U VALUE LO-E WINDOWS

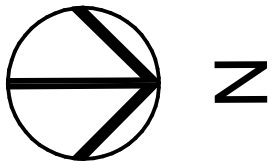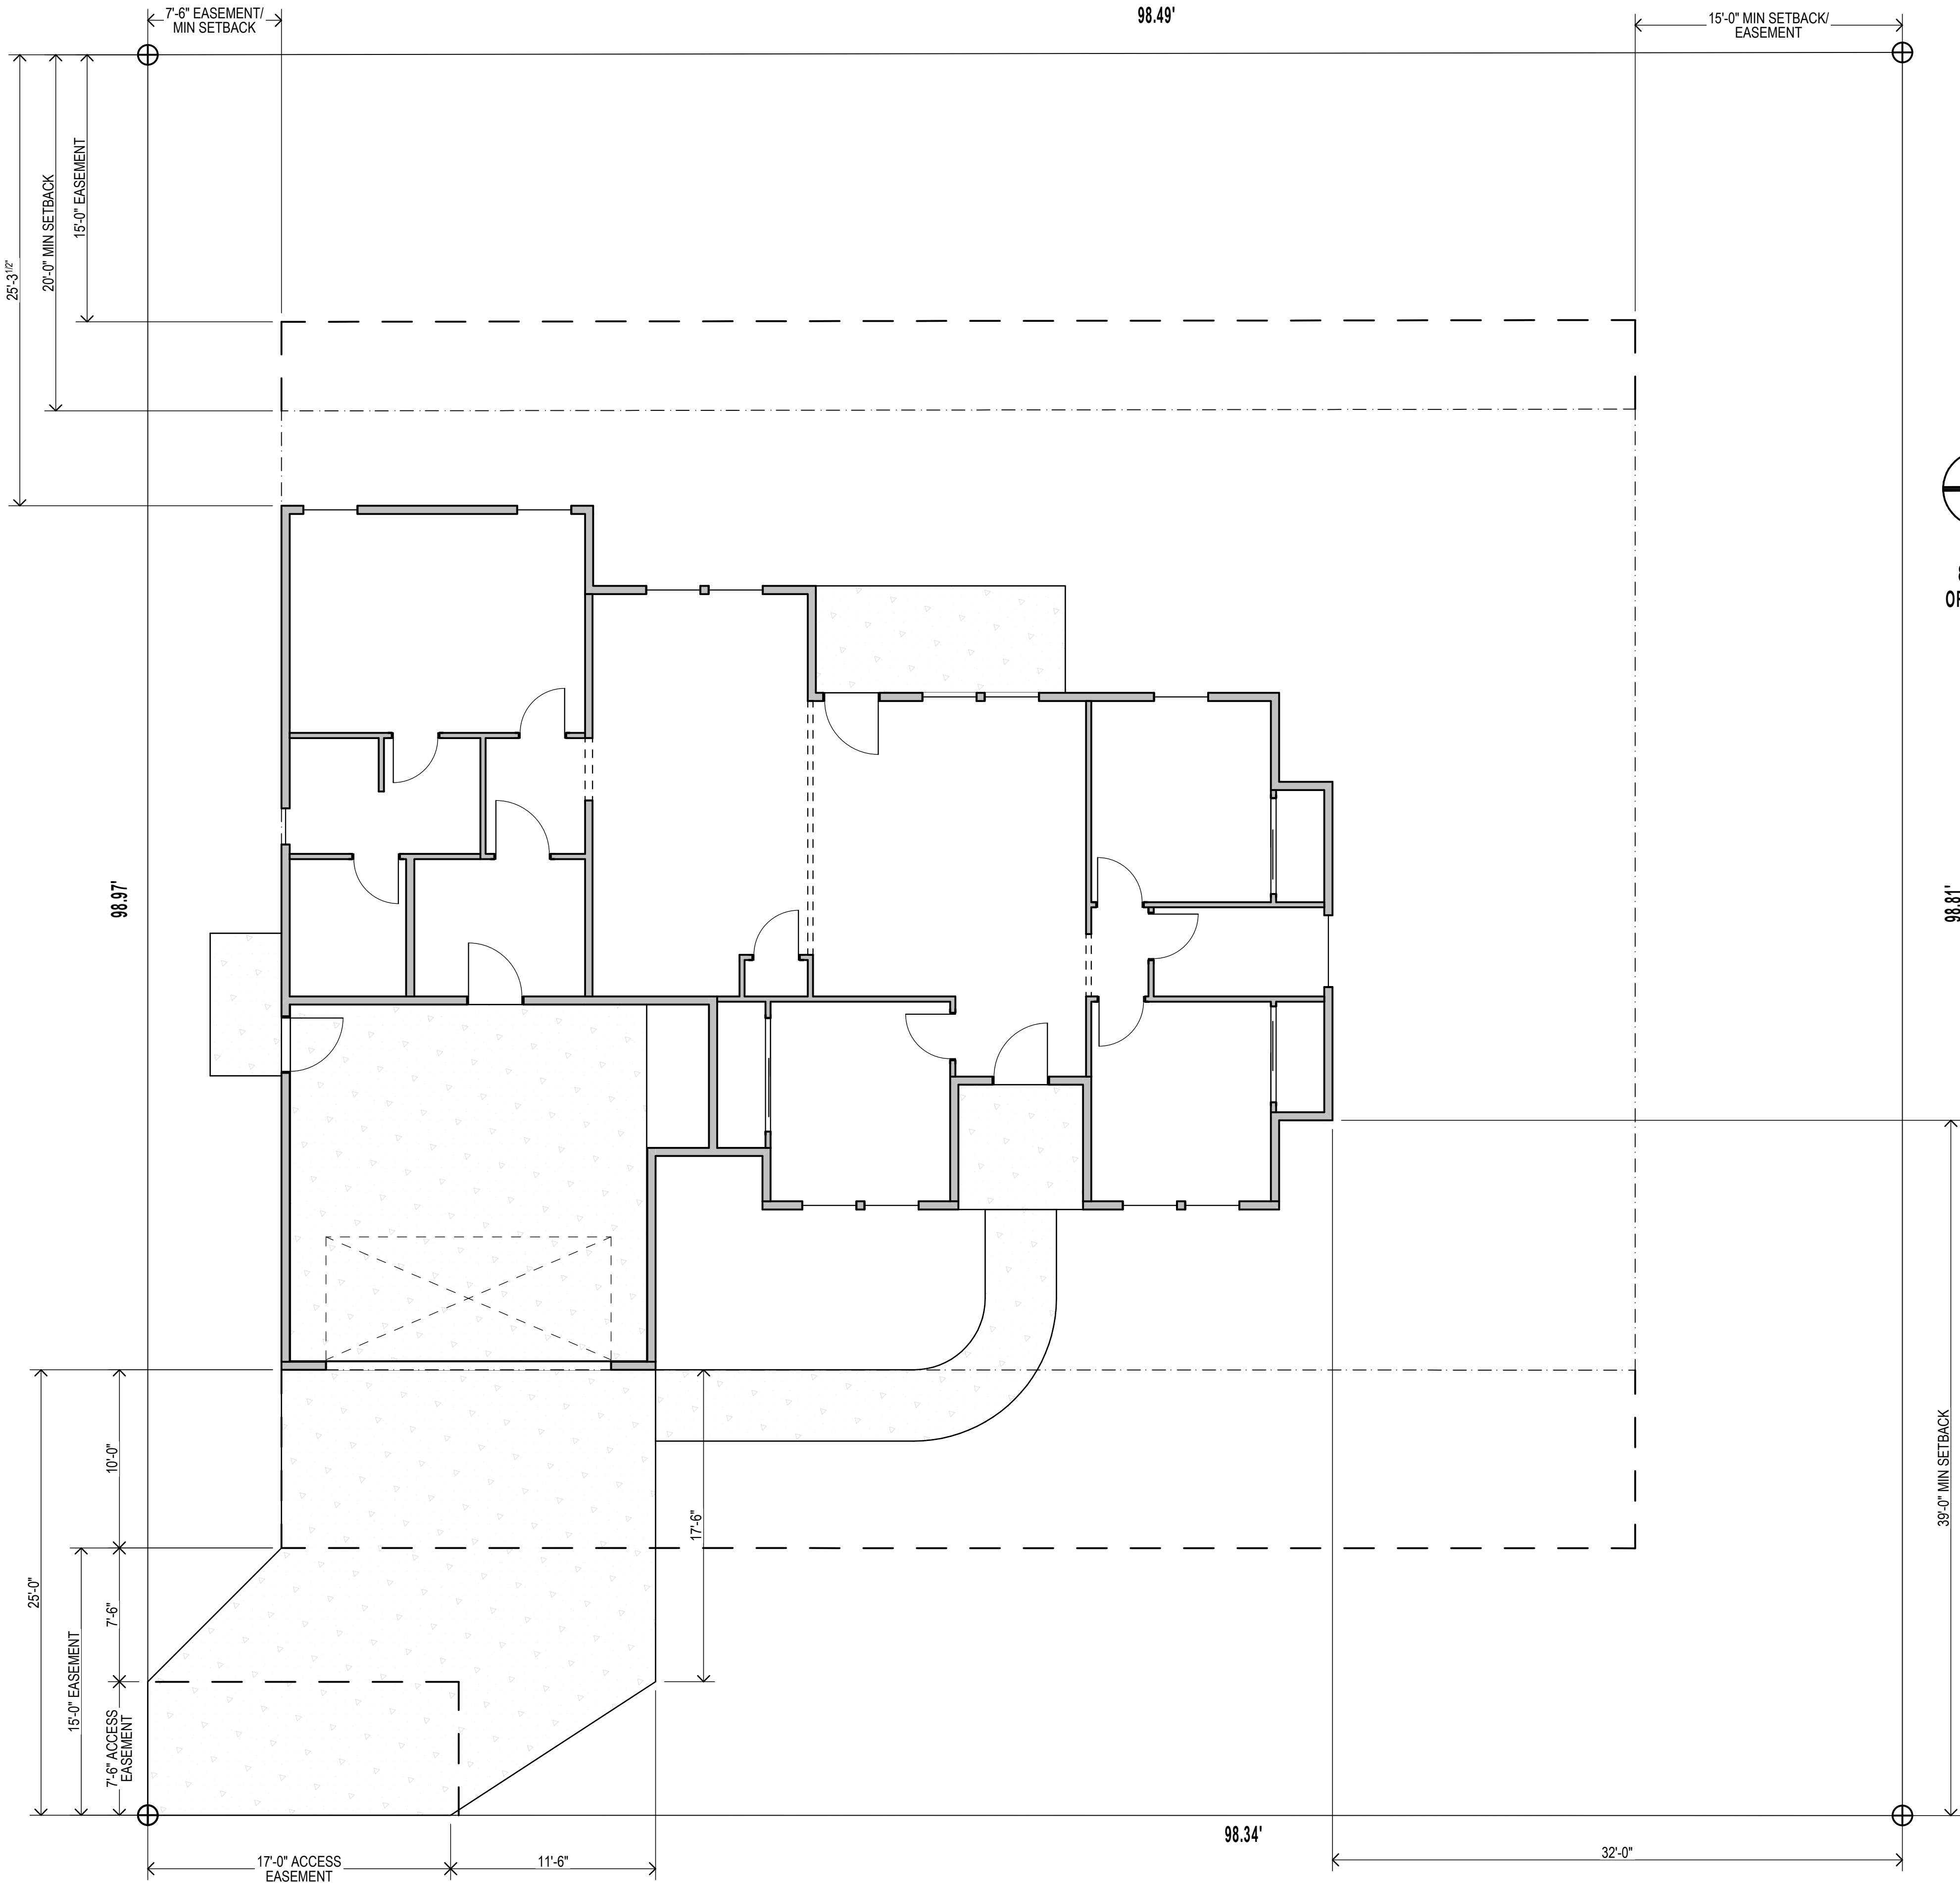

804 ADELL CIRCLE
ORTON ADDITION SUB
LOT 9
BLOCK 1
SITE PLAN
SCALE: 3/16"=1'-0"
MAIN ----- 1605 SF
GARAGE ----- 456 SF
COVERED PATIO -- 49 SF

Project Address:

804 Adell Circle
Filer, ID

Subdivision

Orton Addition Sub

Floor Plan

Filer Spec

Print Date:


3/17/2022


(TYP.) SCALE (U.N.O.)

1/4"=1'-0"

SITE PLAN

1 OF 9

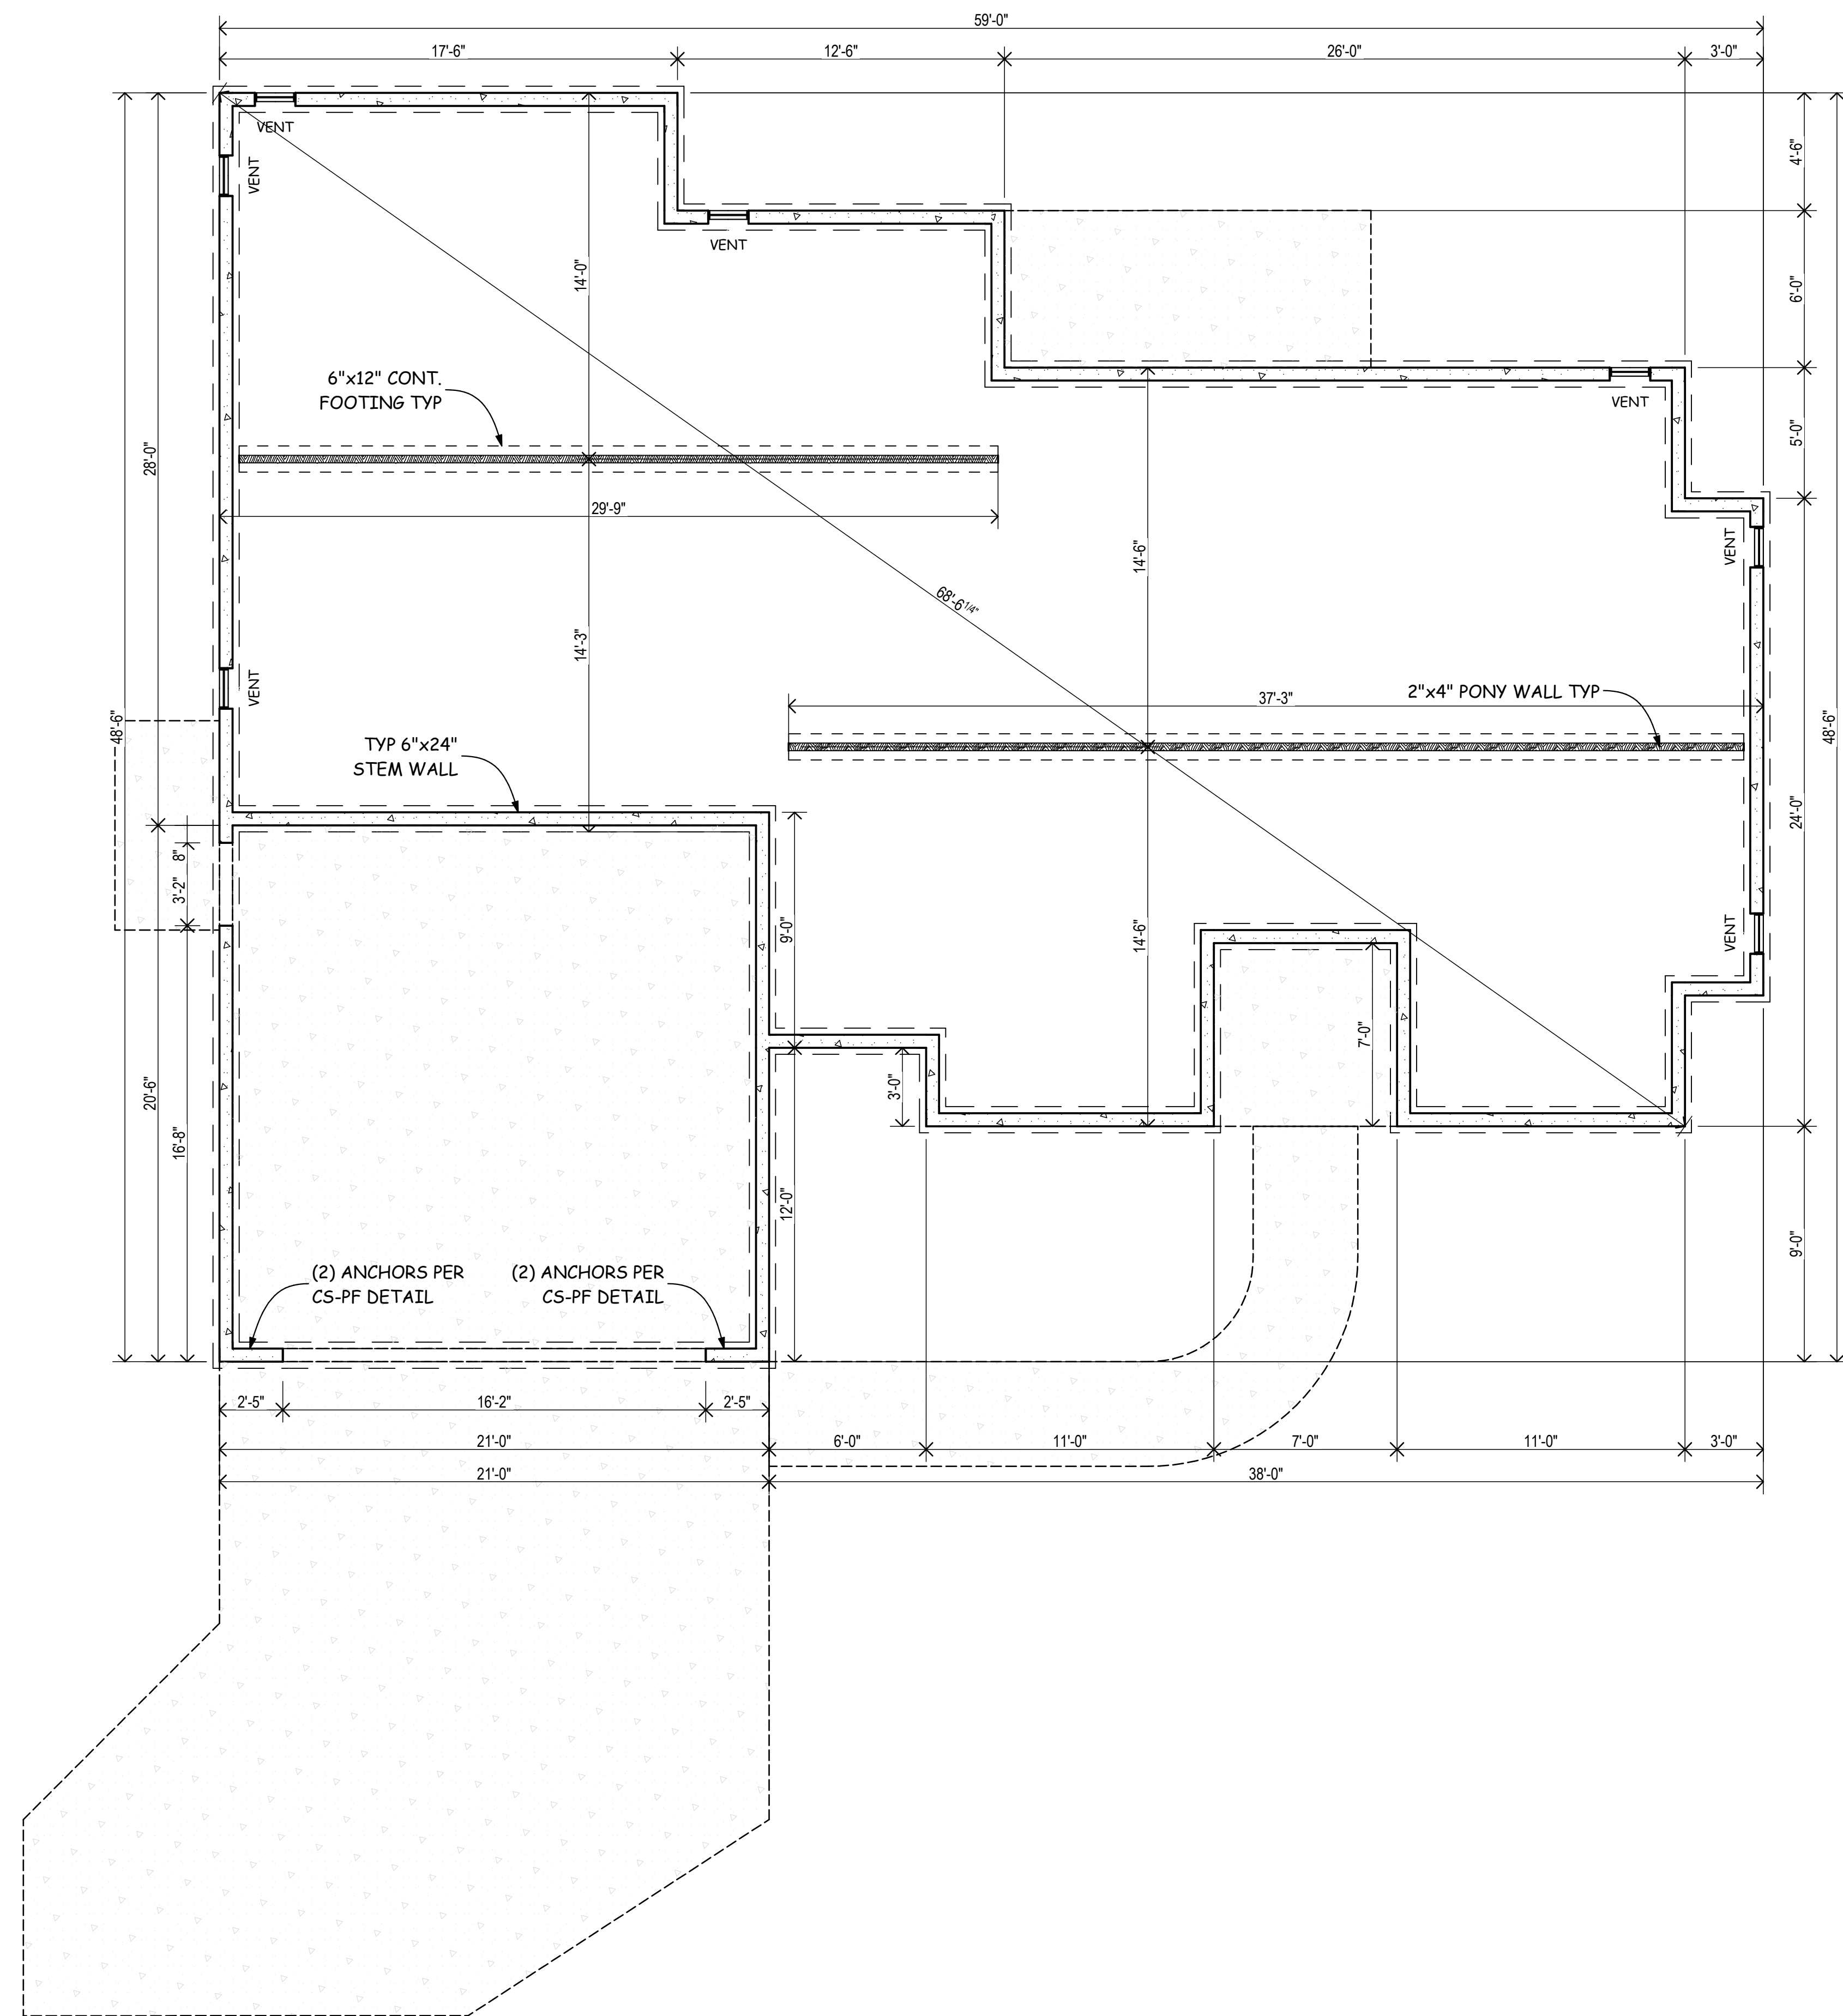

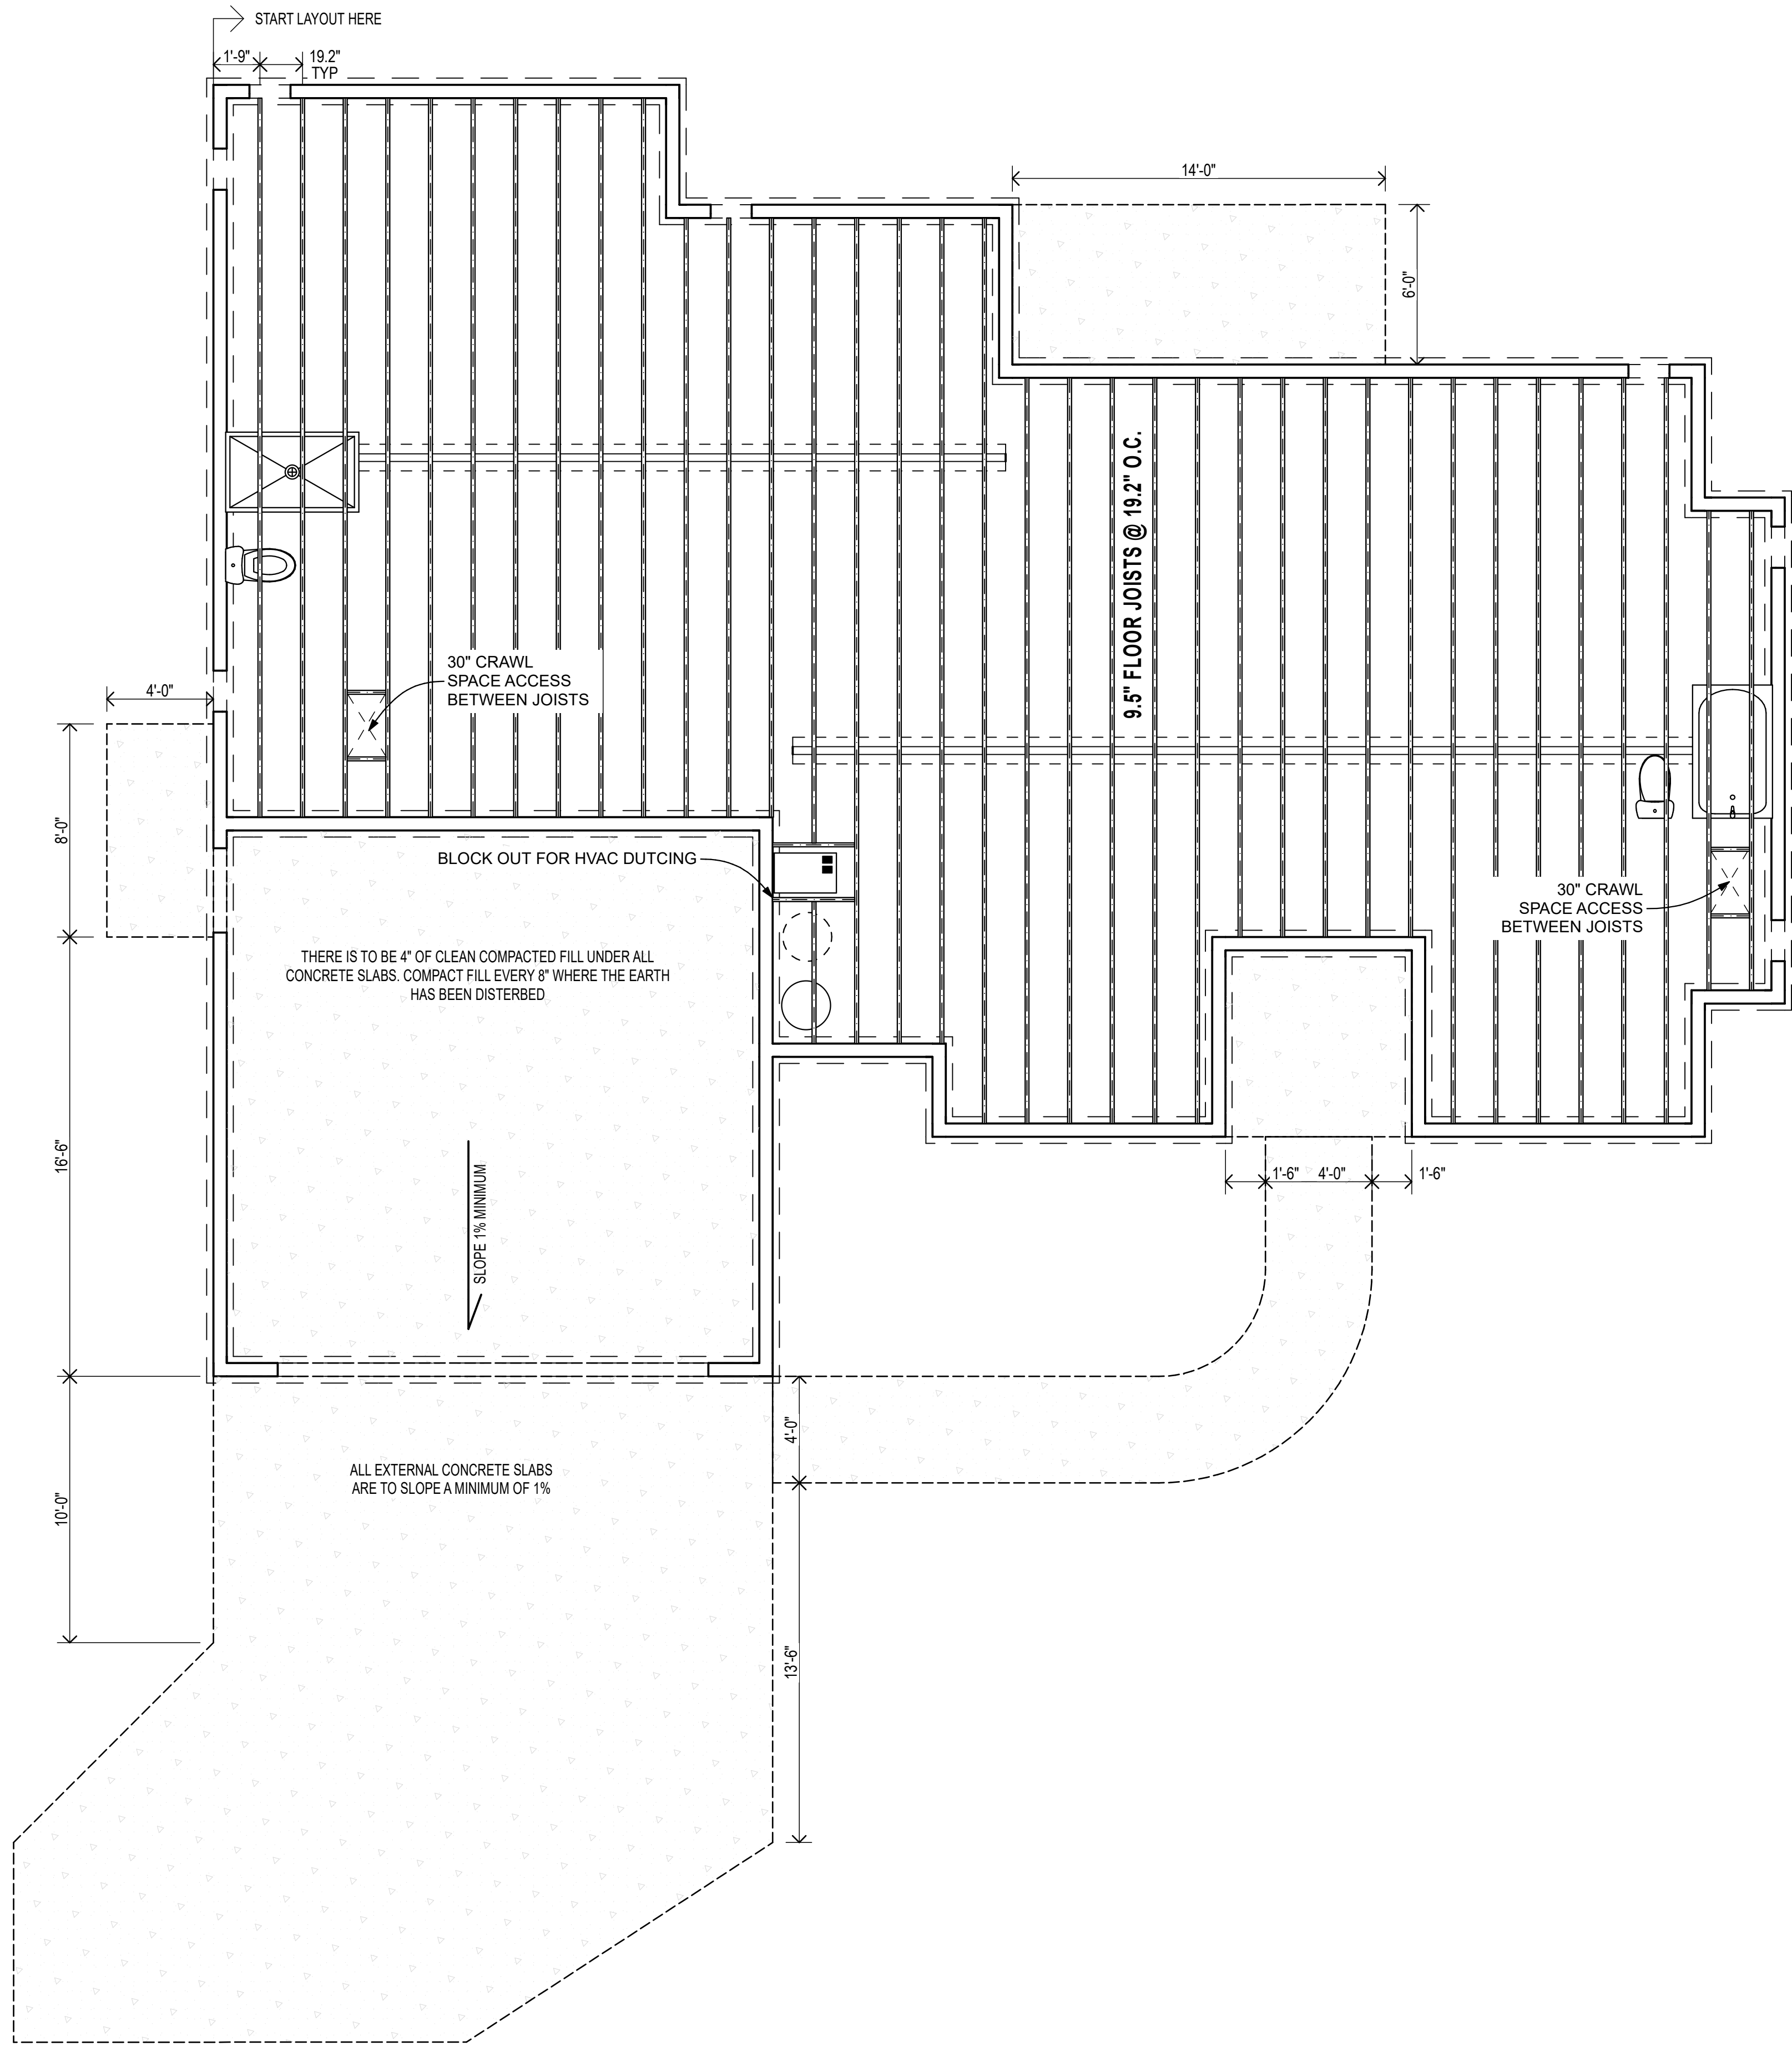

Project Address:

804 Adell Circle
Filer, ID

Subdivision

Orton Addition Sub

Floor Plan

Filer Spec


Print Date:


3/17/2022

(TYP.) SCALE (U.N.O.)

1/4"=1'-0"

JOIST PLAN

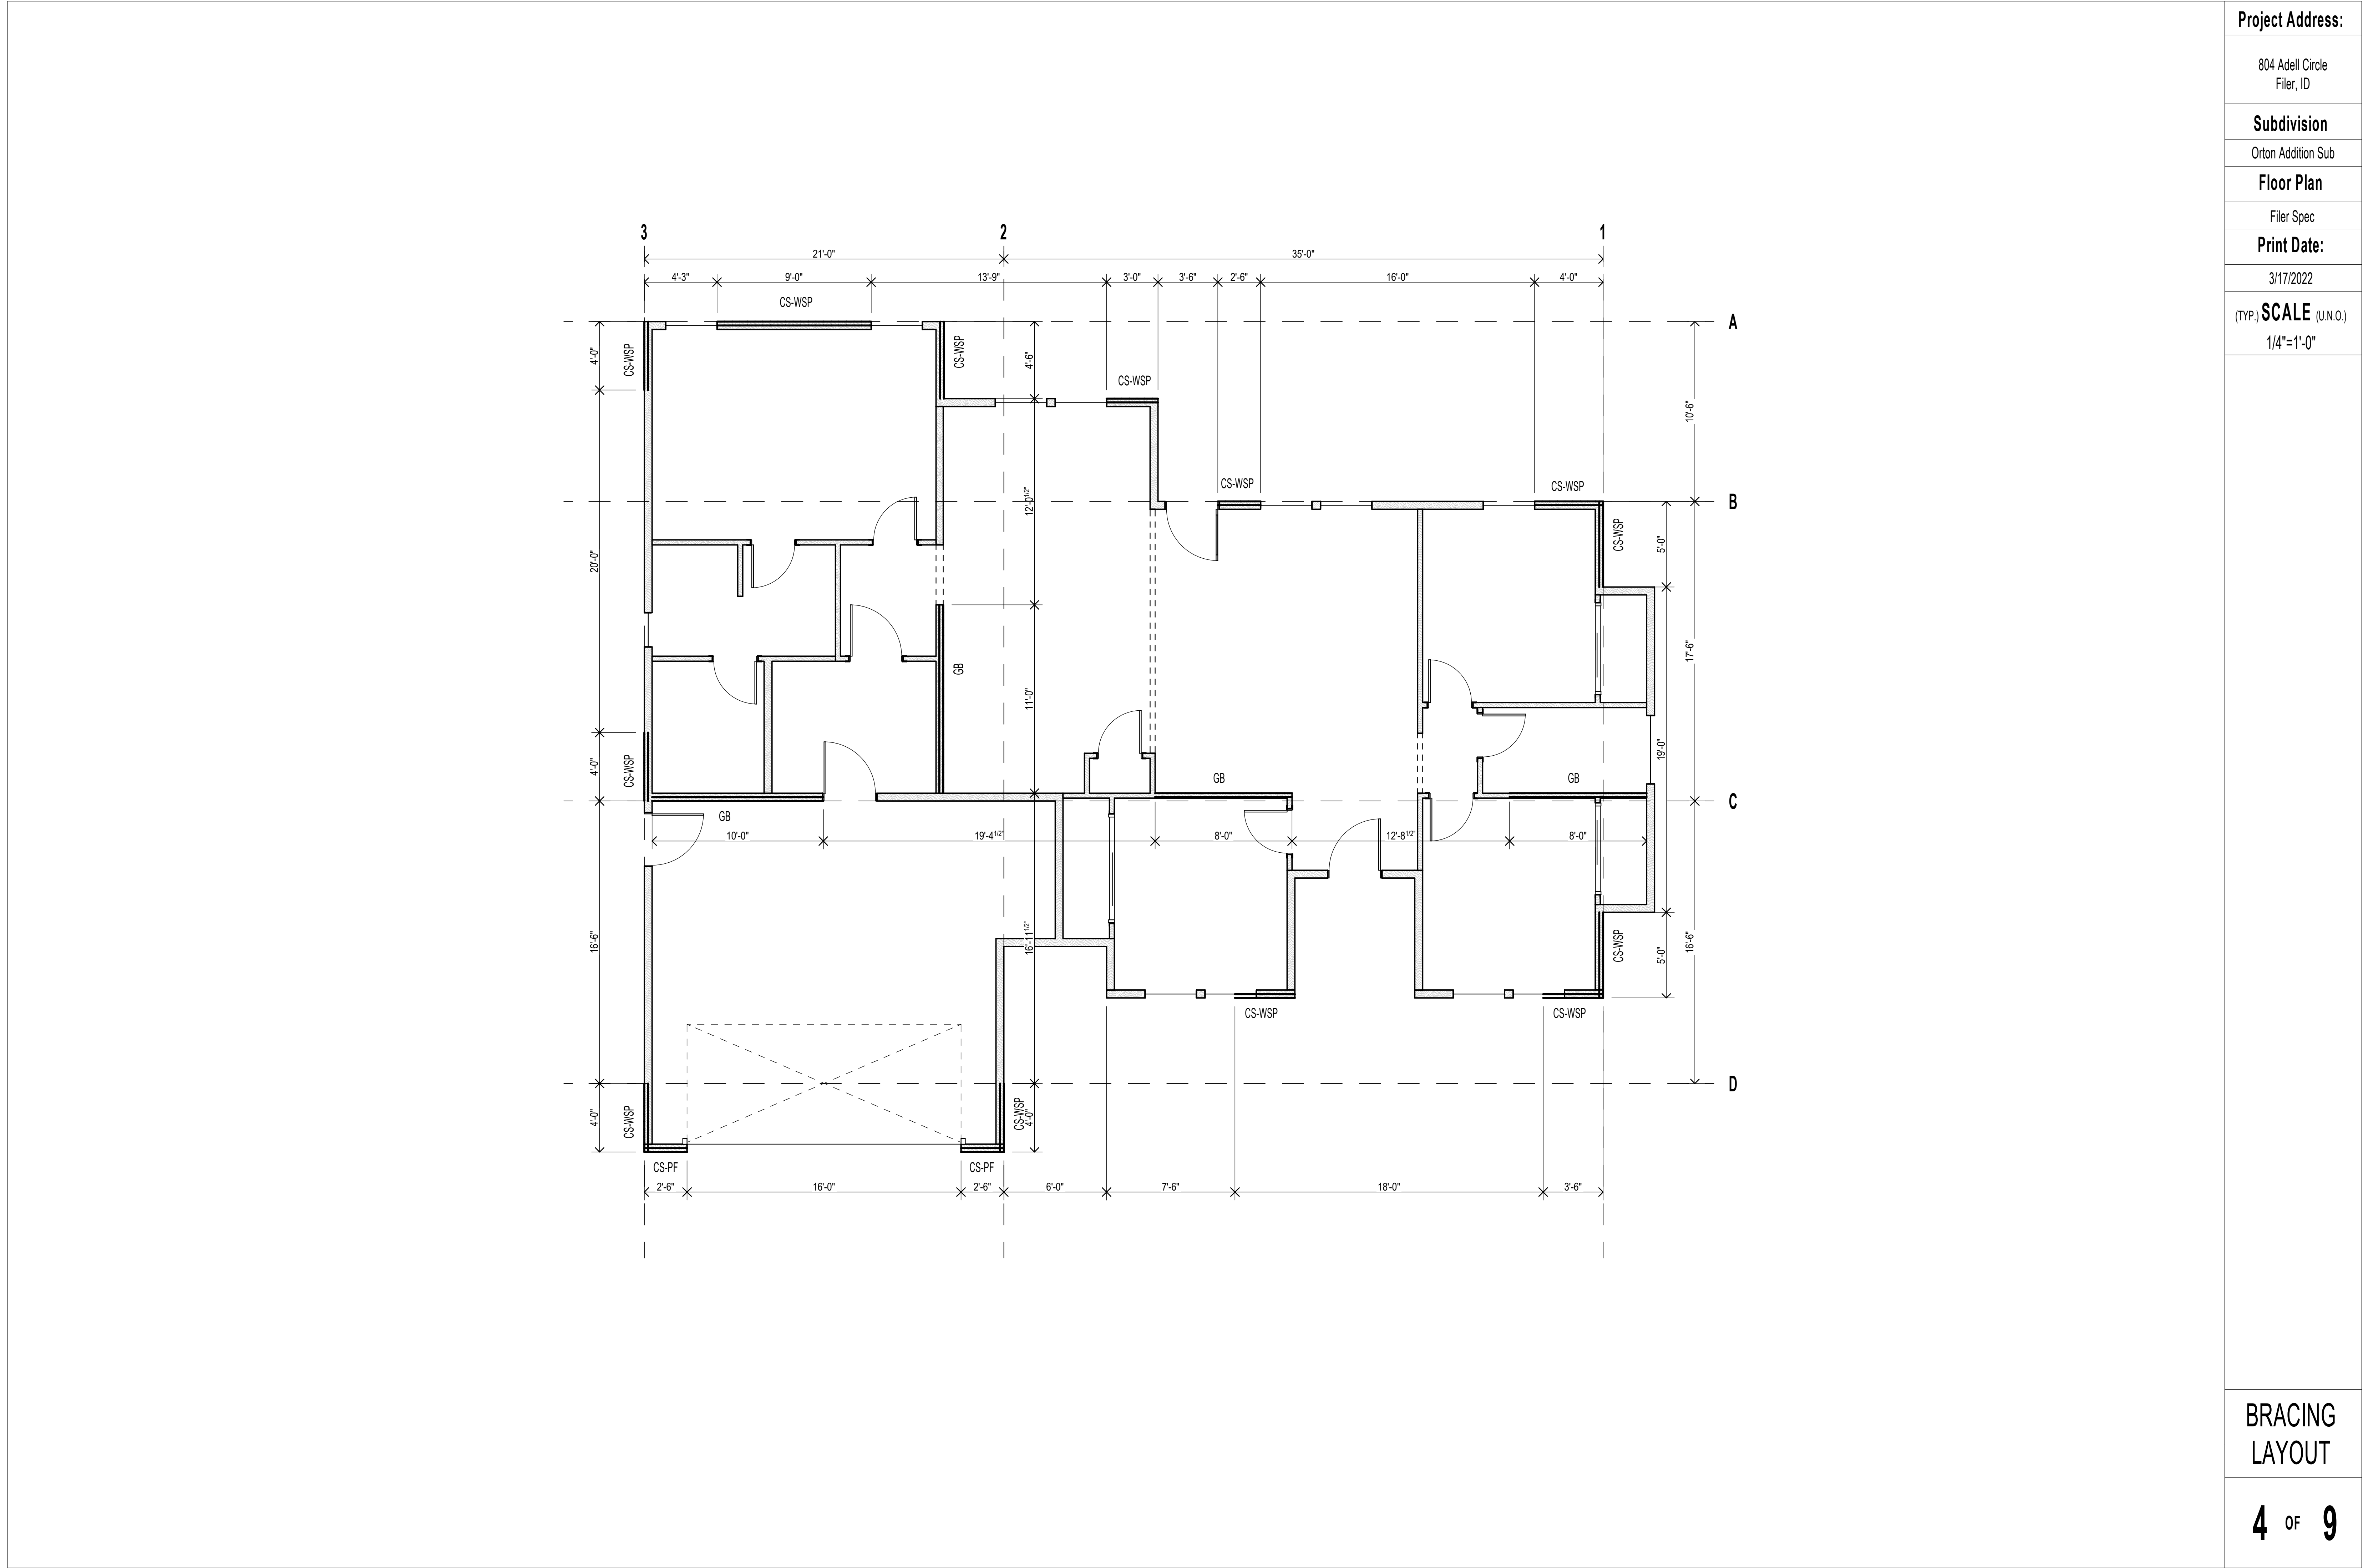

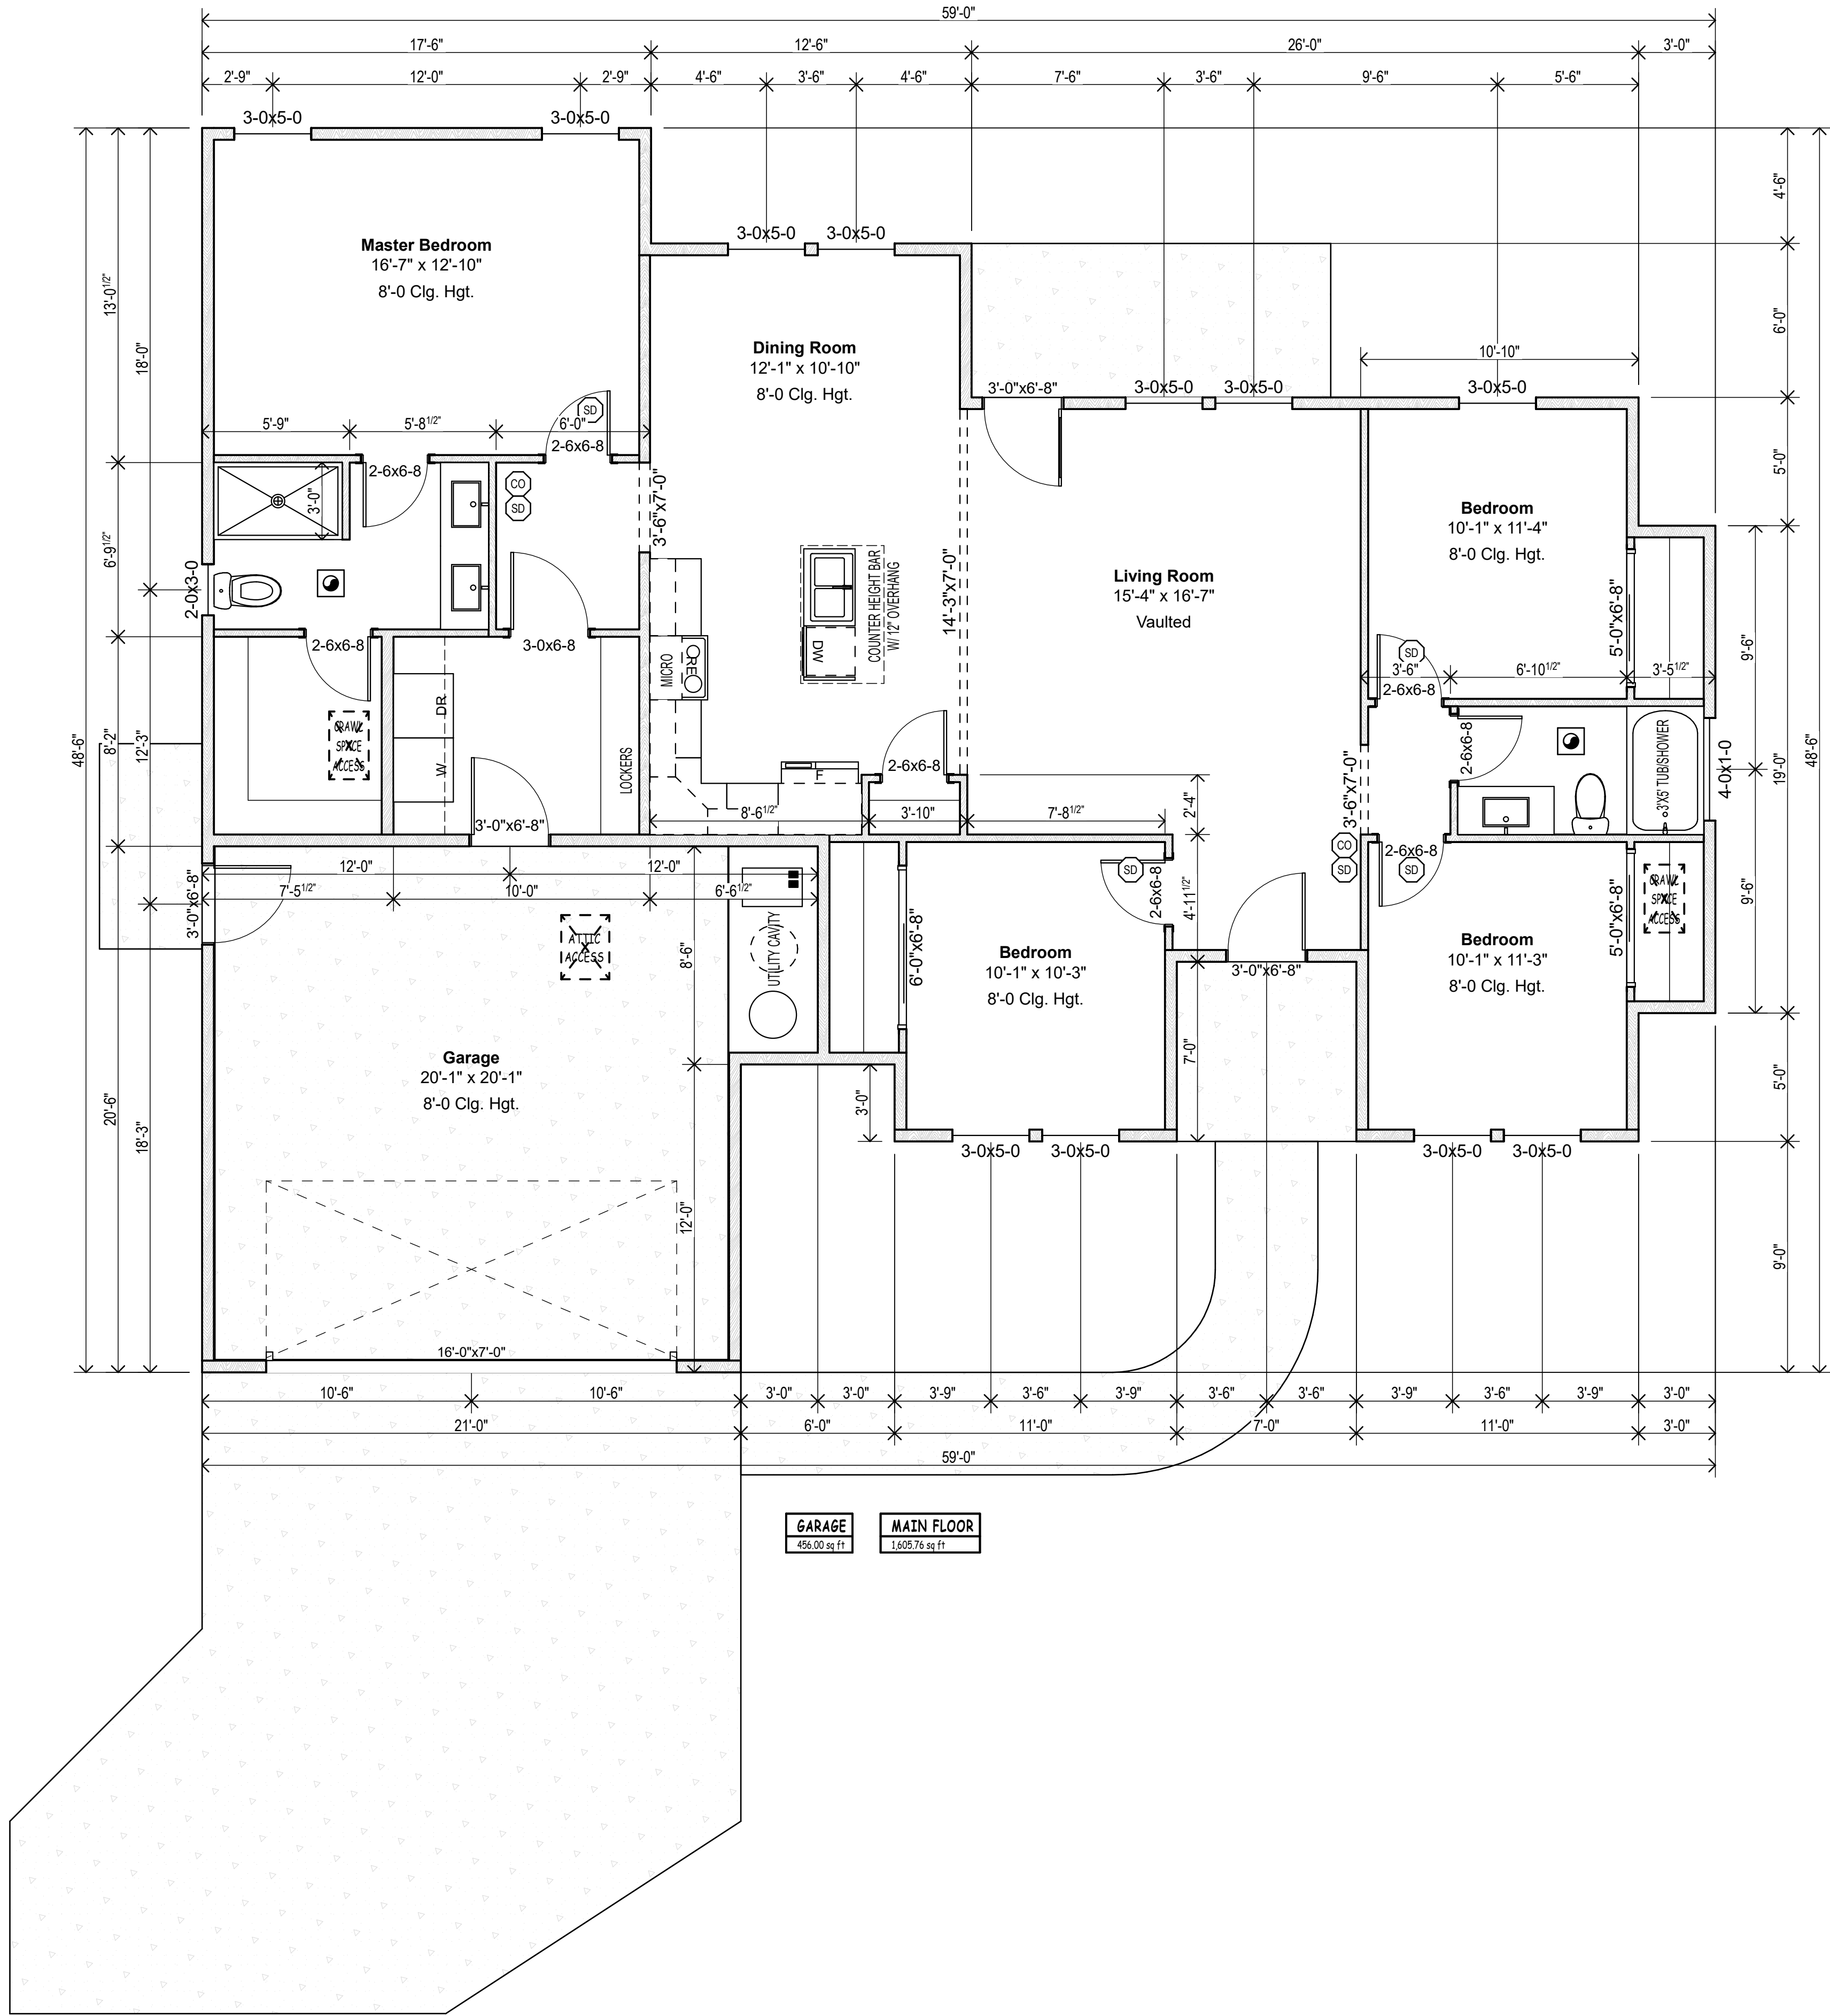

Project Address:

804 Adell Circle
Filer, ID

Subdivision

Orton Addition Sub

Floor Plan

Filer Spec


Print Date:

3/17/2022

(TYP.) SCALE (U.N.O.)

1/4"=1'-0"

FRAMING
PLAN

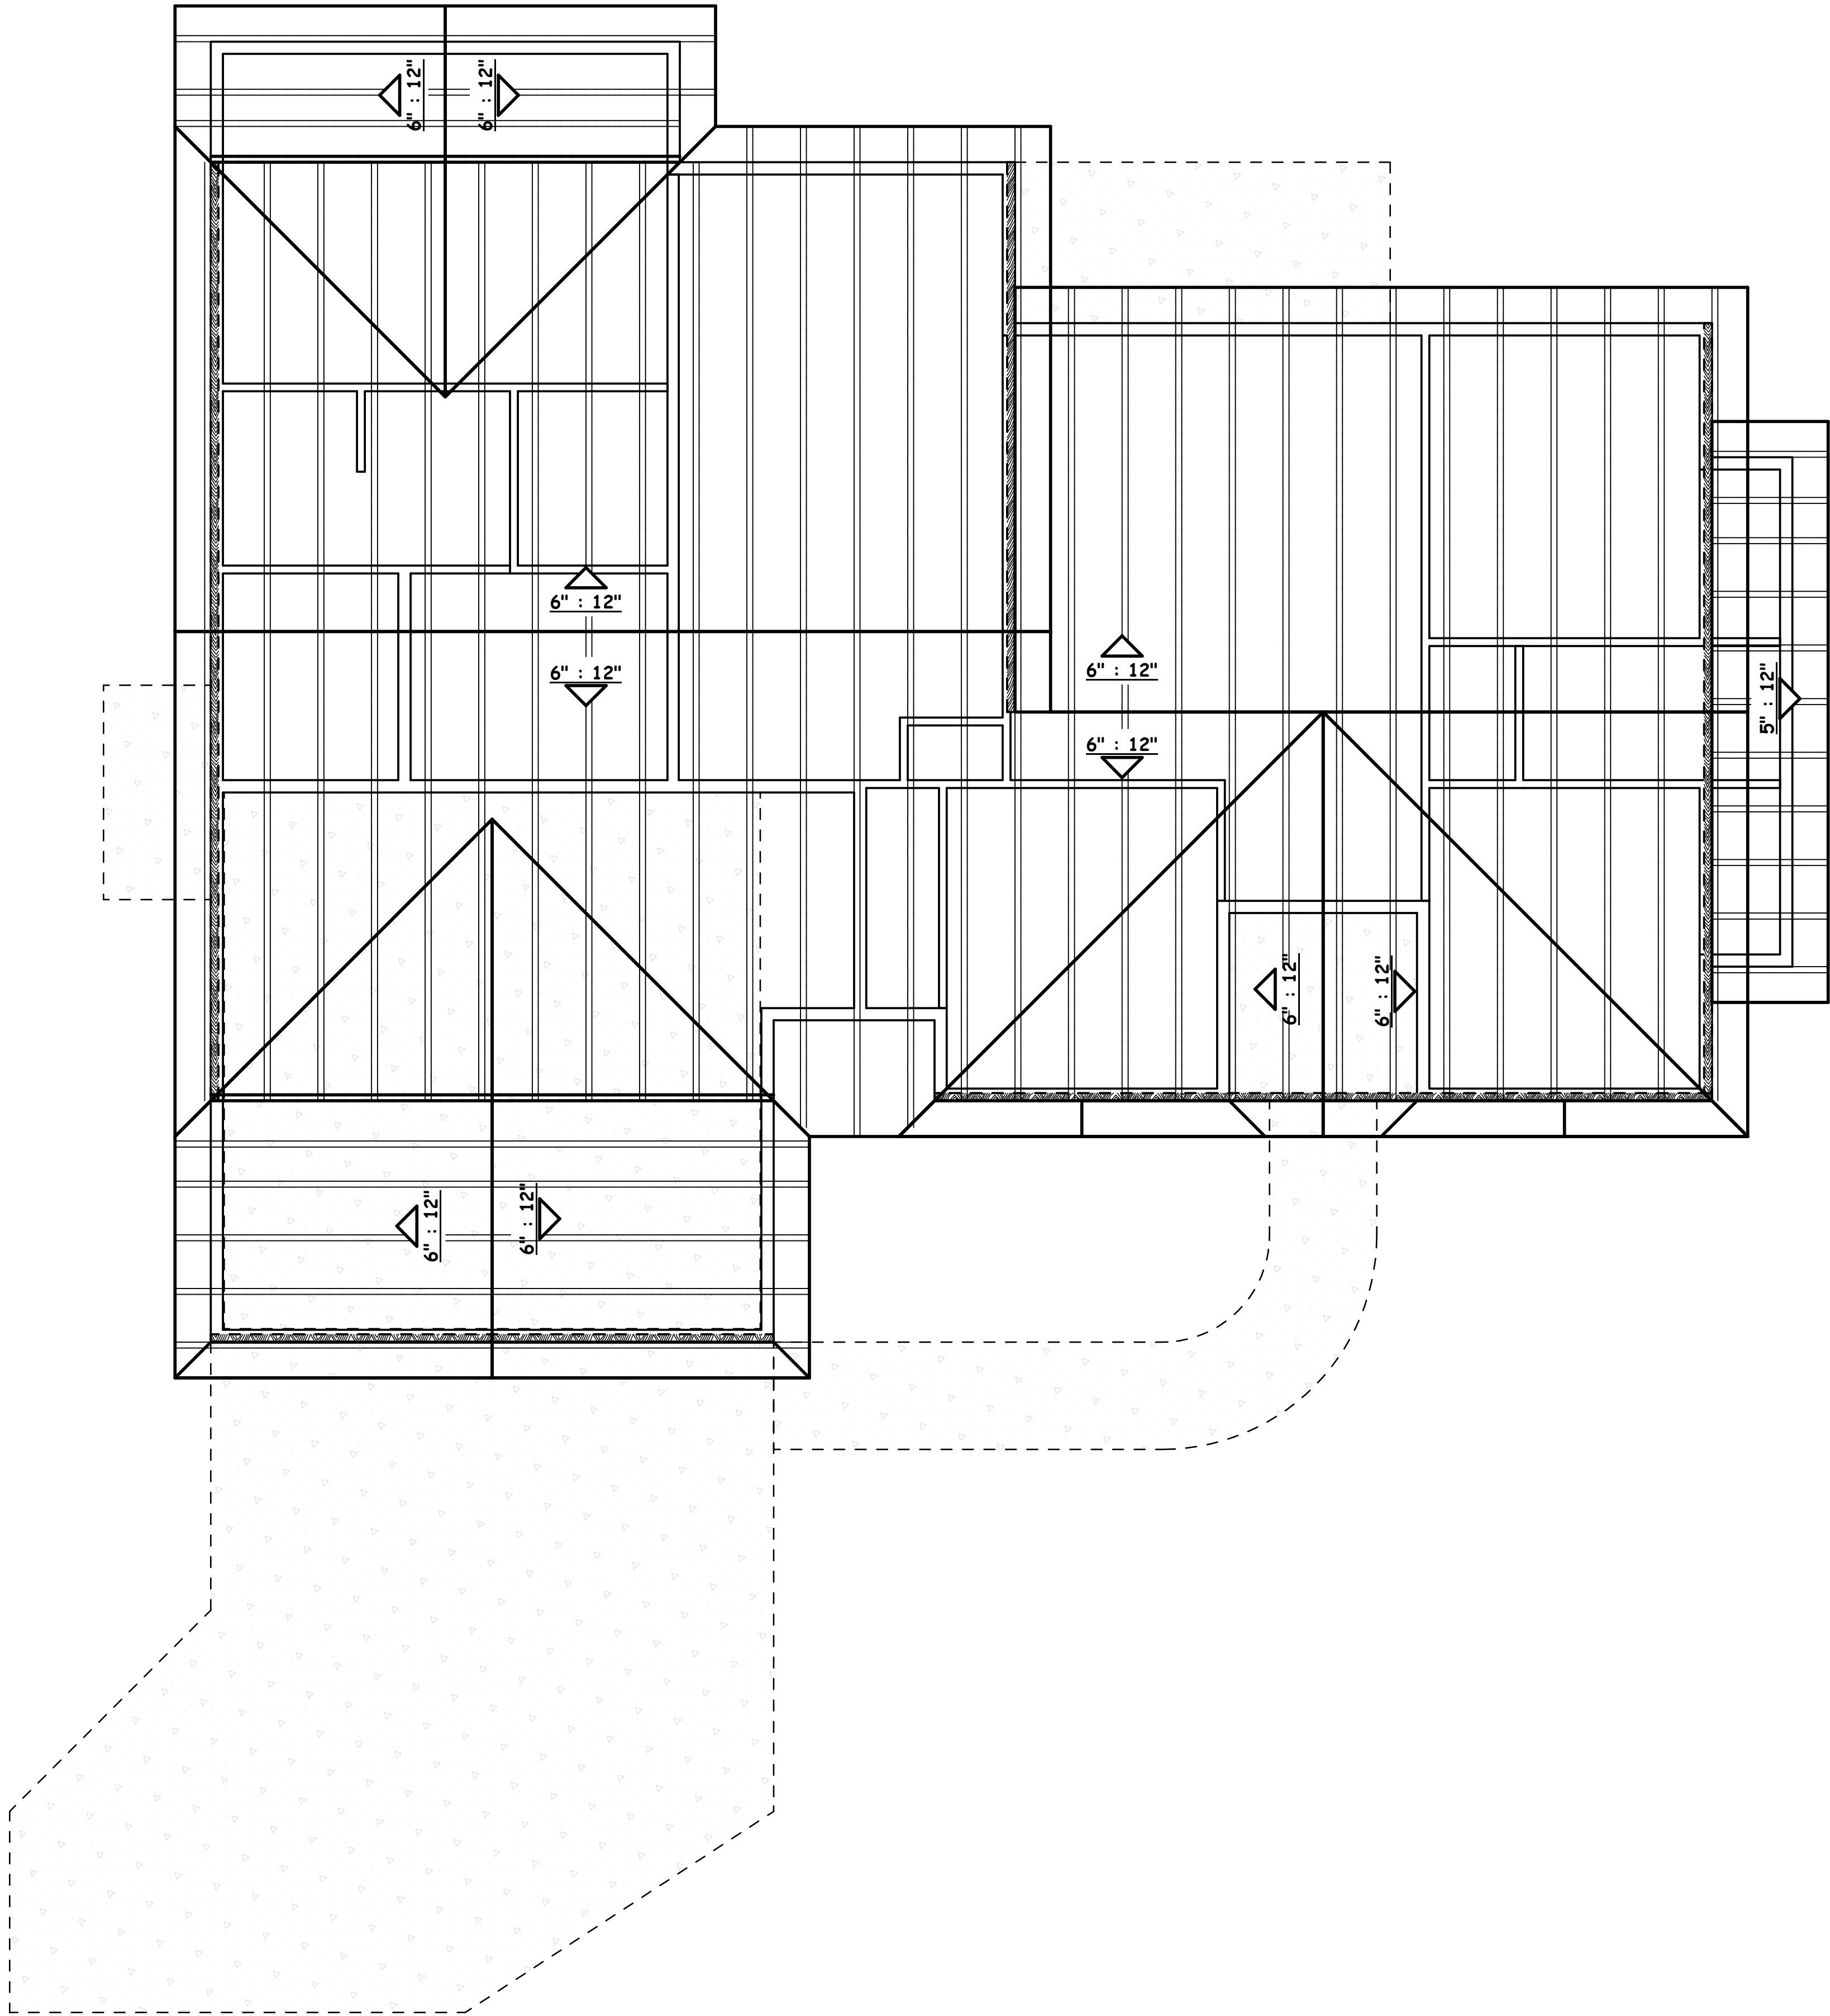

Project Address:

804 Adell Circle
Filer, ID

Subdivision

Orton Addition Sub

Floor Plan

Filer Spec


Print Date:

3/17/2022

(TYP.) **SCALE** (U.N.O.)

1/4"=1'-0"

ROOF PLAN

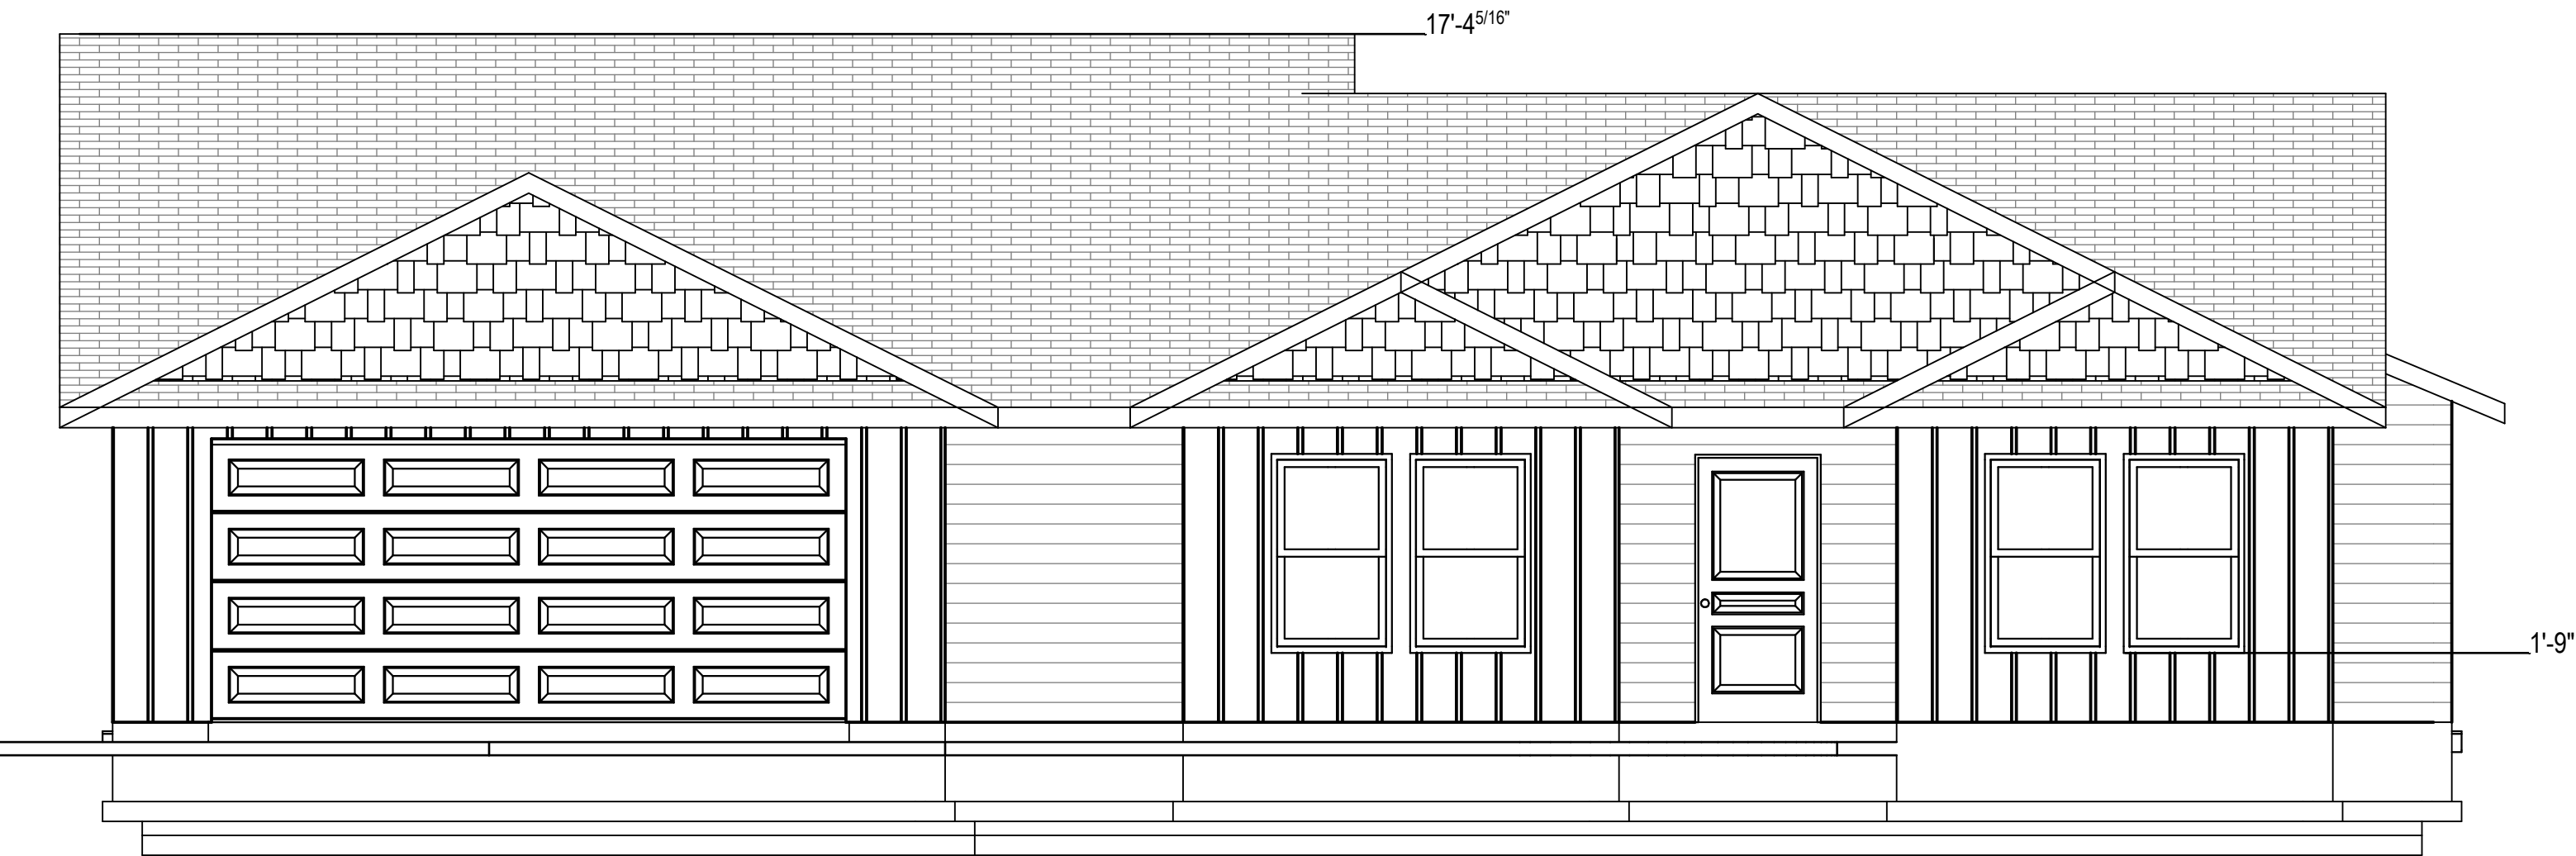


FRONT ELEVATION



BACK ELEVATION



LEFT ELEVATION

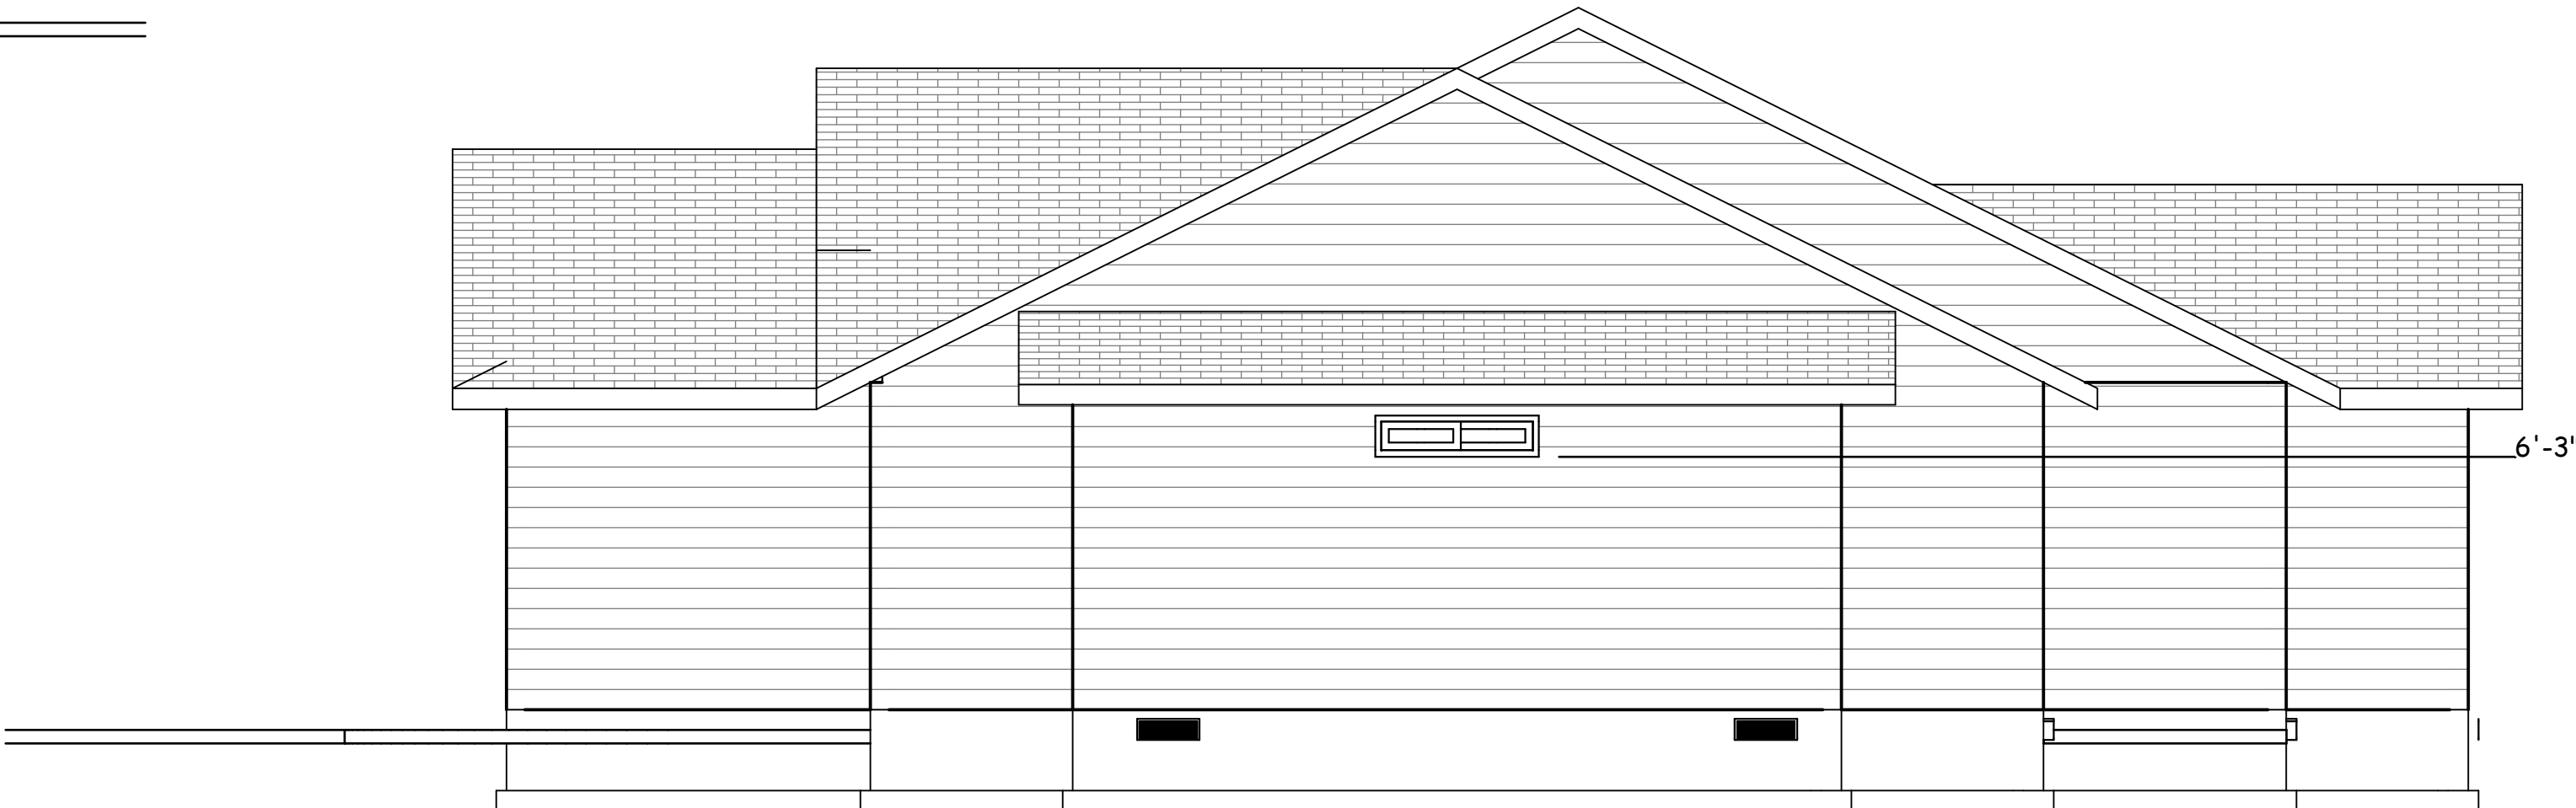

RIGHT ELEVATION

Project Address:

804 Adell Circle
Filer, ID

Subdivision

Orton Addition Sub

Floor Plan



Filer Spec

Print Date:

3/17/2022

(TYP.) SCALE (U.N.O.)

1/4"=1'-0"

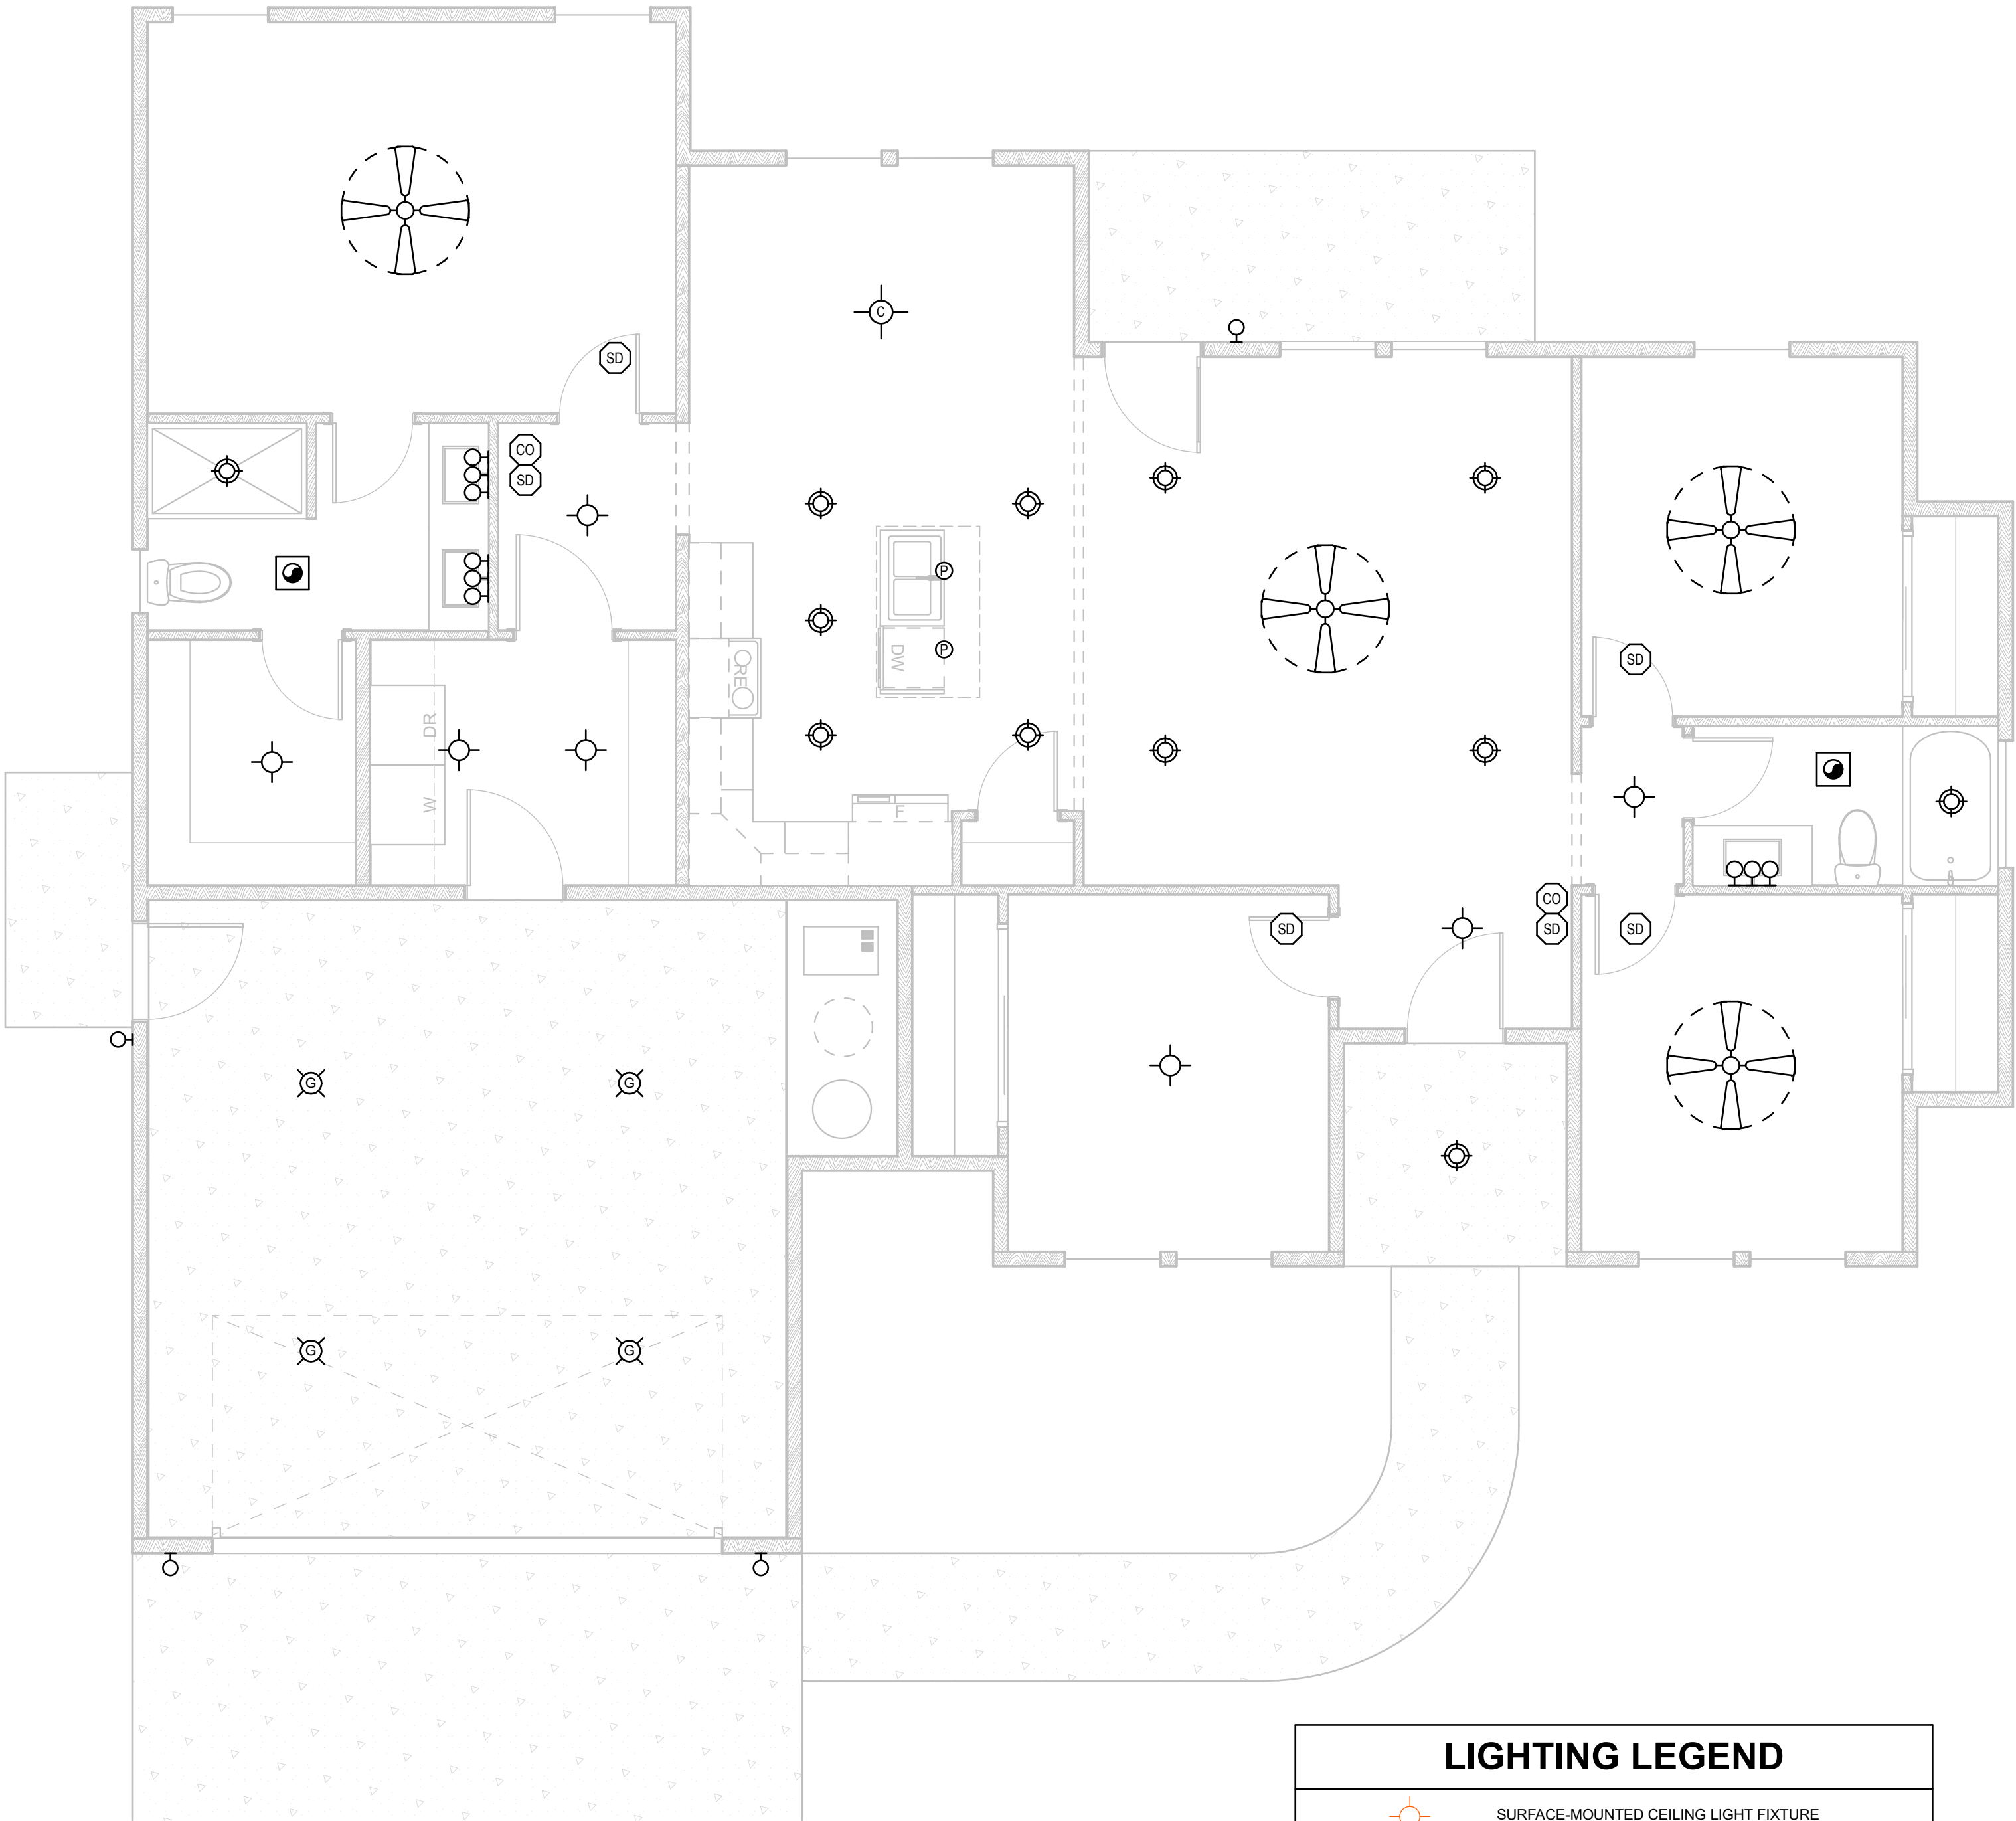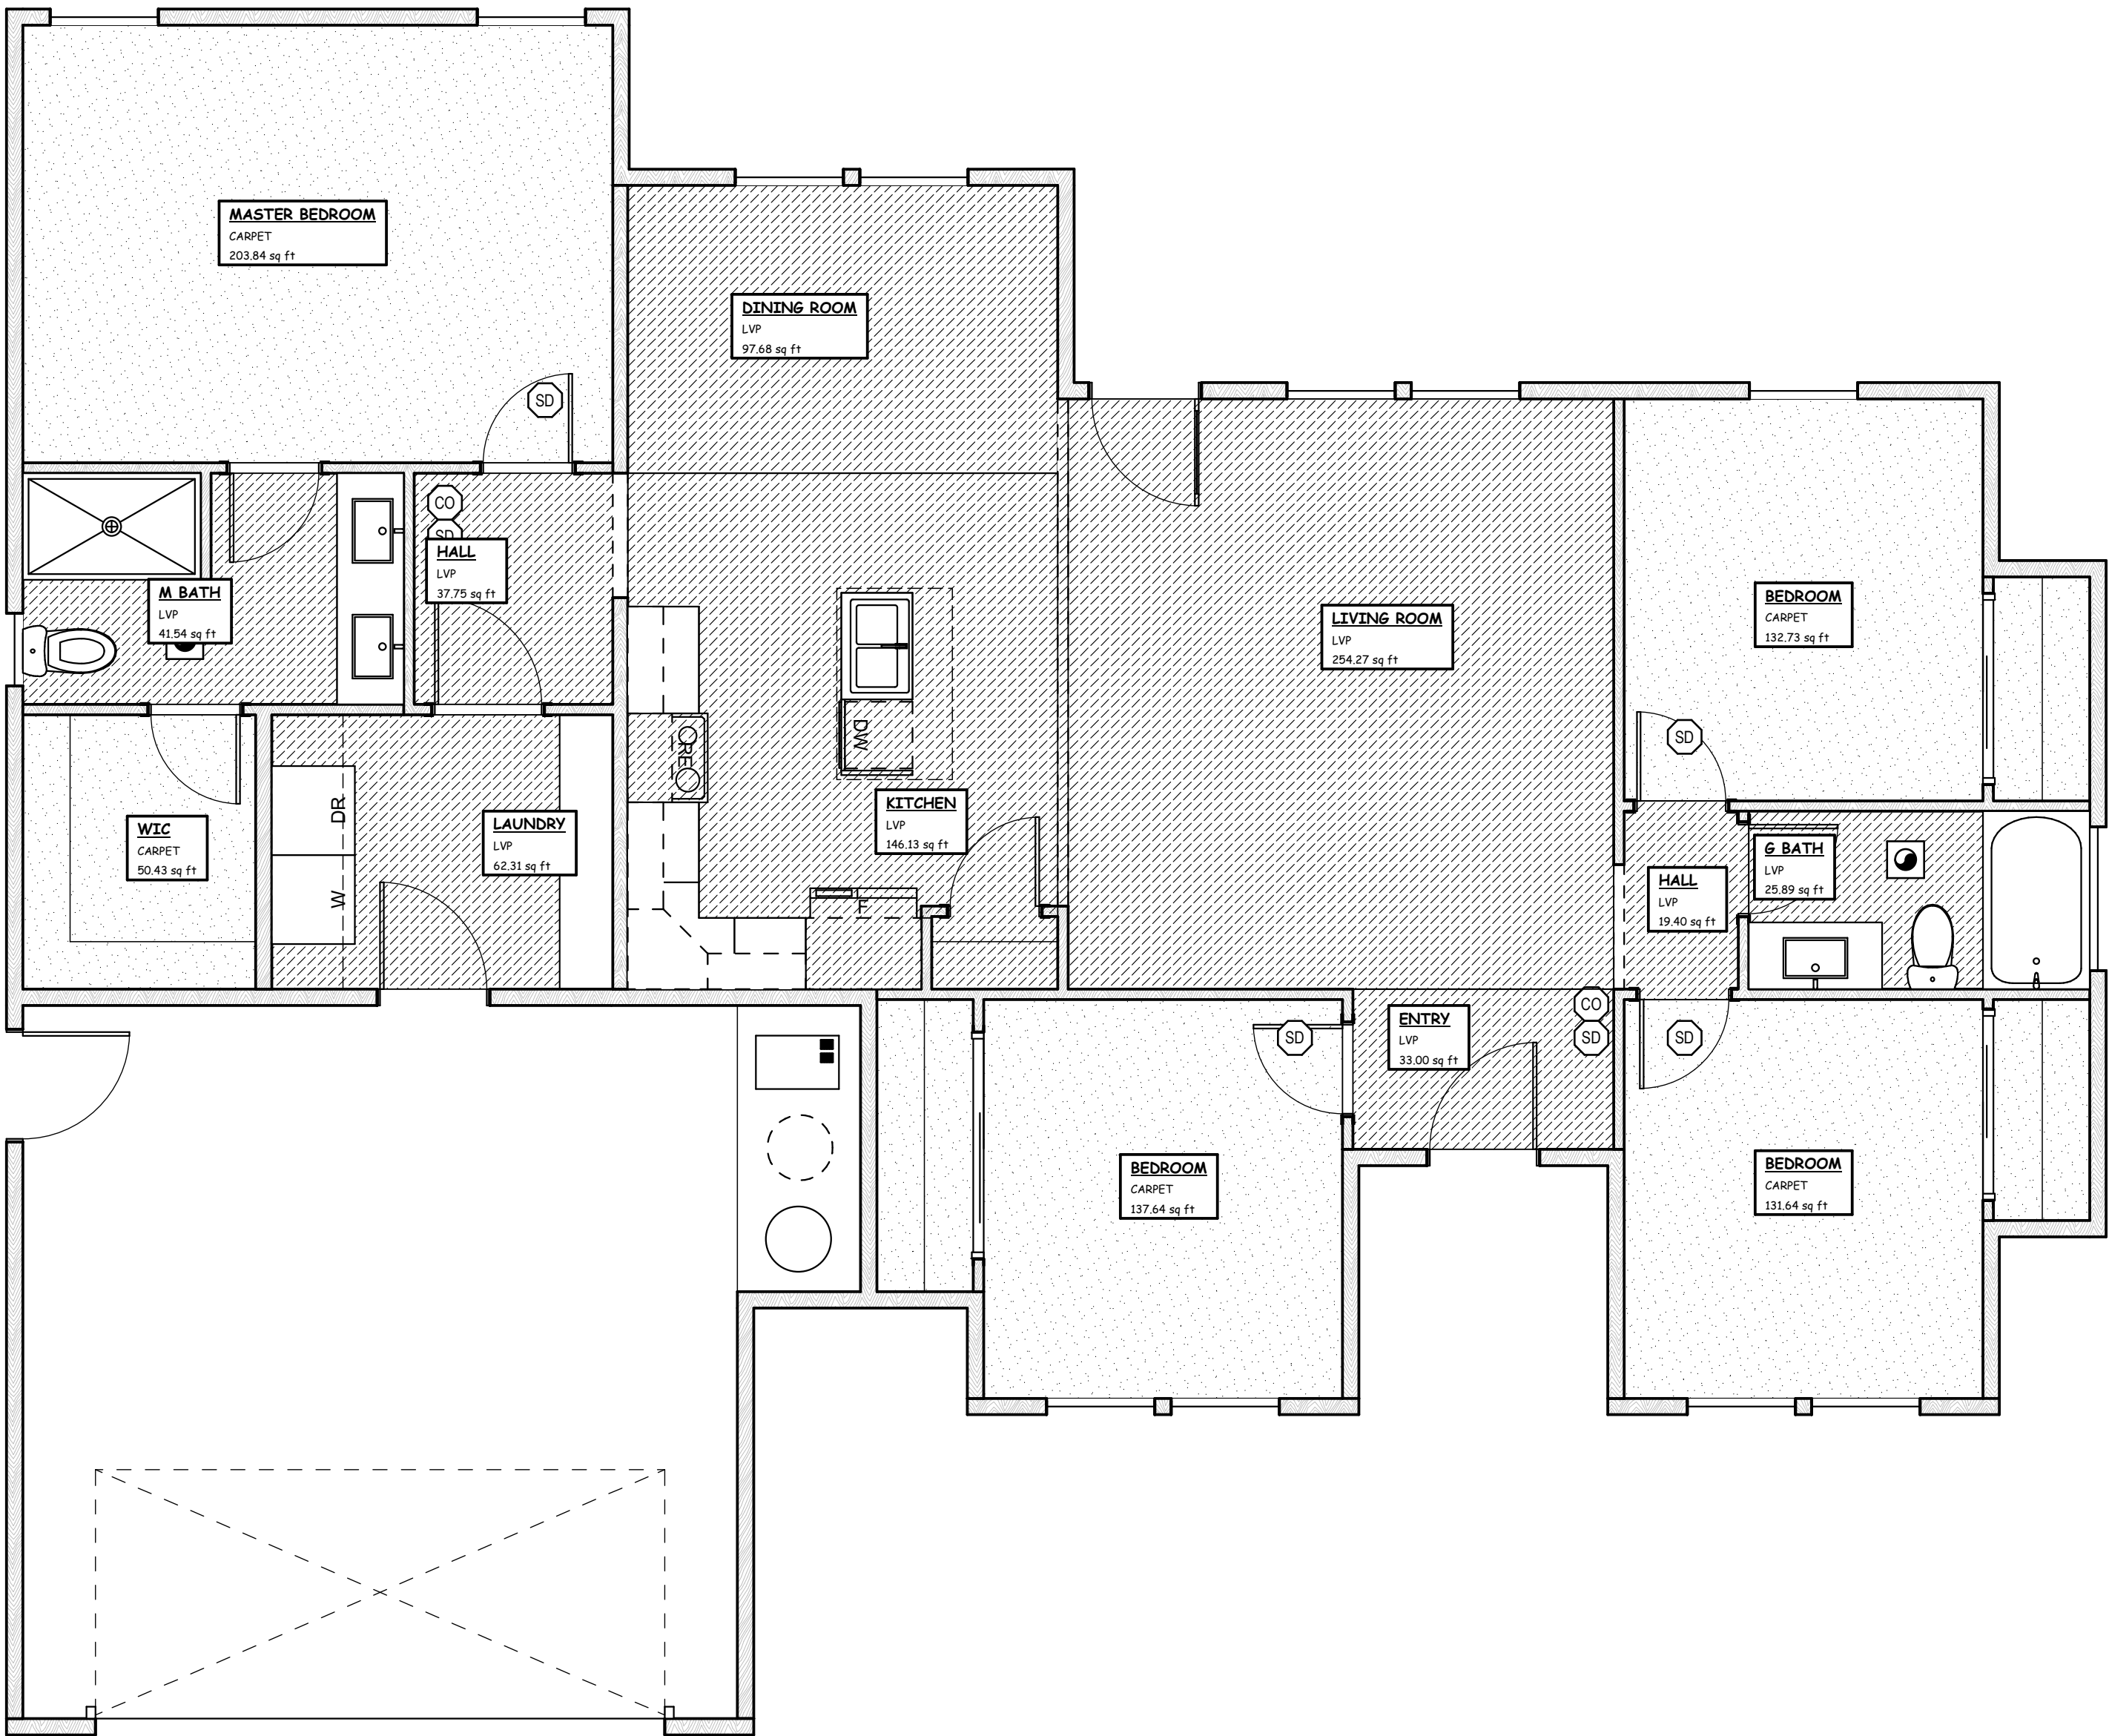

LIGHTING LEGEND	
	SURFACE-MOUNTED CEILING LIGHT FIXTURE
	CHANDELIER
	PENDANT LIGHT FIXTURE
	3 LIGHT VANITY FIXTURE
	WALL-MOUNTED INTERIOR FIXTURE
	WALL-MOUNTED EXTERIOR LIGHT FIXTURE
	FLUORESCENT LIGHT
	CEILING FAN W/ LIGHTS
	RECESSED CAN FIXTURE
	GARAGE CEILING LIGHT FIXTURE
	PUCK LIGHT FIXTURE
	EXHAUST FAN
	CO DETECTOR- DIRECT WIRED W/ BATTERY BACKUP
	SMOKE DETECTOR- DIRECT WIRED W/ BATTERY BACKUP

Project Address:

804 Adell Circle
Filer, ID

Subdivision

Orton Addition Sub

Floor Plan

Filer Spec

Print Date:

3/17/2022

(TYP.) SCALE (U.N.O.)

1/4"=1'-0"

FLOORING &
LIGHTING


TABLE R602.10.3(1) BRACING REQUIREMENTS BASED ON WIND SPEED						
EXPOSURE CATEGORY B • 30-FOOT MEAN ROOF HEIGHT • 10-FOOT WALL HEIGHT • 2 BRACED WALL LINES		MINIMUM TOTAL LENGTH (FEET) OF BRACED WALL PANELS REQUIRED ALONG EACH BRACED WALL LINE ^a				
Ultimate Design Wind Speed (mph)	Story Location	Braced Wall Line Spacing ^b (feet)	Method LIB ^c	Method GB	Methods DWB, WSP, SFB, PBS, PCP, HPS, BV-WSP, ABW, PFH, PFG, CS-SFB	Methods CS-WSP, CS-G, CS-PF
≤ 110		10	3.5	3.5	2.0	1.5
		20	6.0	6.0	3.5	3.0
		30	8.5	8.5	5.0	4.5
		40	11.5	11.5	6.5	5.5
		50	14.0	14.0	8.0	7.0
		60	16.5	16.5	9.5	8.0
		10	6.5	6.5	3.5	3.0
		20	11.5	11.5	6.5	5.5
		30	16.5	16.5	9.5	8.0
		40	21.5	21.5	12.5	10.5
		50	26.5	26.5	15.5	13.0
		60	31.5	31.5	18.0	15.5
		10	NP	9.5	5.5	4.5
		20	NP	17.0	10.0	8.5
		30	NP	24.5	14.0	12.0
		40	NP	32.0	18.5	15.5
		50	NP	39.5	22.5	19.0
		60	NP	46.5	26.5	23.0

4 R602.10.3 2018 IRC Bracing Requirements
NOT TO SCALE




TABLE R602.10.5 MINIMUM LENGTH OF BRACED WALL PANELS						
METHOD (See Table R602.10.4)		MINIMUM LENGTH ^a (inches)				
		Wall Height				
		8 feet	9 feet	10 feet	11 feet	12 feet
DWB, WSP, SFB, PBS, PCP, HPS, BV-WSP		48	48	48	53	58
GB		48	48	48	53	58
LIB		55	62	69	NP	NP
ABW	SDC A, B and C, ultimate design wind speed < 140 mph	28	32	34	38	42
	SDC D ₁ , D ₂ and D ₃ , ultimate design wind speed < 140 mph	32	32	34	NP	NP
CS-G		24	27	30	33	36
CS-WSP, CS-SFB	Adjacent clear opening height (inches)					
	≤ 64	24	27	30	33	36
	68	26	27	30	33	36
	72	27	27	30	33	36
	76	30	29	30	33	36
	80	32	30	30	33	36
	84	35	32	32	33	36
	88	38	35	33	33	36
	92	43	37	35	35	36
	96	48	41	38	36	36
	100	—	44	40	38	38
	104	—	49	43	40	39
	108	—	54	46	43	41
	112	—	—	50	45	43
	116	—	—	55	48	45
	120	—	—	60	52	48
	124	—	—	—	56	51
	128	—	—	—	61	54
	132	—	—	—	66	58
	136	—	—	—	—	62
	140	—	—	—	—	66
	144	—	—	—	—	72
METHOD (See Table R602.10.4)		Portal header height				
		8 feet	9 feet	10 feet	11 feet	12 feet
PFH	Supporting roof only	16	16	16	Note c	Note c
	Supporting one story and roof	24	24	24	Note c	Note c
PFG		24	27	30	Note d	Note d
CS-PF	SDC A, B and C	16	18	20	Note e	Note e
	SDC D ₁ , D ₂ and D ₃	16	18	20	Note e	Note e

For SI: 1 inch = 25.4 mm, 1 foot = 304.8 mm, 1 mile per hour = 0.447 m/s.
NP = Not Permitted.
a. Linear interpolation shall be permitted.
b. Use the actual length where it is greater than or equal to the minimum length.
c. Maximum header height for PFH is 10 feet in accordance with Figure R602.10.6.2, but wall height shall be permitted to be increased to 12 feet with pony wall.
d. Maximum header height for PFG is 10 feet in accordance with Figure R602.10.6.3, but wall height shall be permitted to be increased to 12 feet with pony wall.
e. Maximum header height for CS-PF is 10 feet in accordance with Figure R602.10.6.4, but wall height shall be permitted to be increased to 12 feet with pony wall.


6 R602.10.5 2018 IRC Minimum Length Braced Wall Panel
NOT TO SCALE

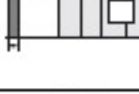TABLE R602.10.4 BRACING METHODS					
	METHODS, MATERIAL	MINIMUM THICKNESS	FIGURE	CONNECTION CRITERIA ^a	
				Fasteners	Spacing
Intermittent Bracing Methods	GB Gypsum board	$\frac{1}{2}$ "		Nails or screws per Table R602.3(1) for exterior locations Nails or screws per Table R702.3.5 for interior locations	For all braced wall panel locations: 7" edges (including top and bottom plates) 7" field
	ABW Alternate braced wall	$\frac{3}{8}$ "		See Section R602.10.6.1	See Section R602.10.6.1
Continuous Sheathing Methods	PFH Portal frame with hold-downs	$\frac{3}{4}$ " s		See Section R602.10.6.2	See Section R602.10.6.2
	CS-WSP Continuously sheathed wood structural panel	$\frac{3}{4}$ " s		Exterior sheathing per Table R602.3(3) Interior sheathing per Table R602.3(1) or R602.3(2)	6" edges 12" field Varies by fastener
	CS-G ^{b,c} Continuously sheathed wood structural panel adjacent to garage openings	$\frac{3}{4}$ " s		See Method CS-WSP	See Method CS-WSP
	CS-PF Continuously sheathed portal frame	$\frac{7}{8}$ " s		See Section R602.10.6.4	See Section R602.10.6.4

5 R602.10.4 2018 IRC Bracing Methods
NOT TO SCALE

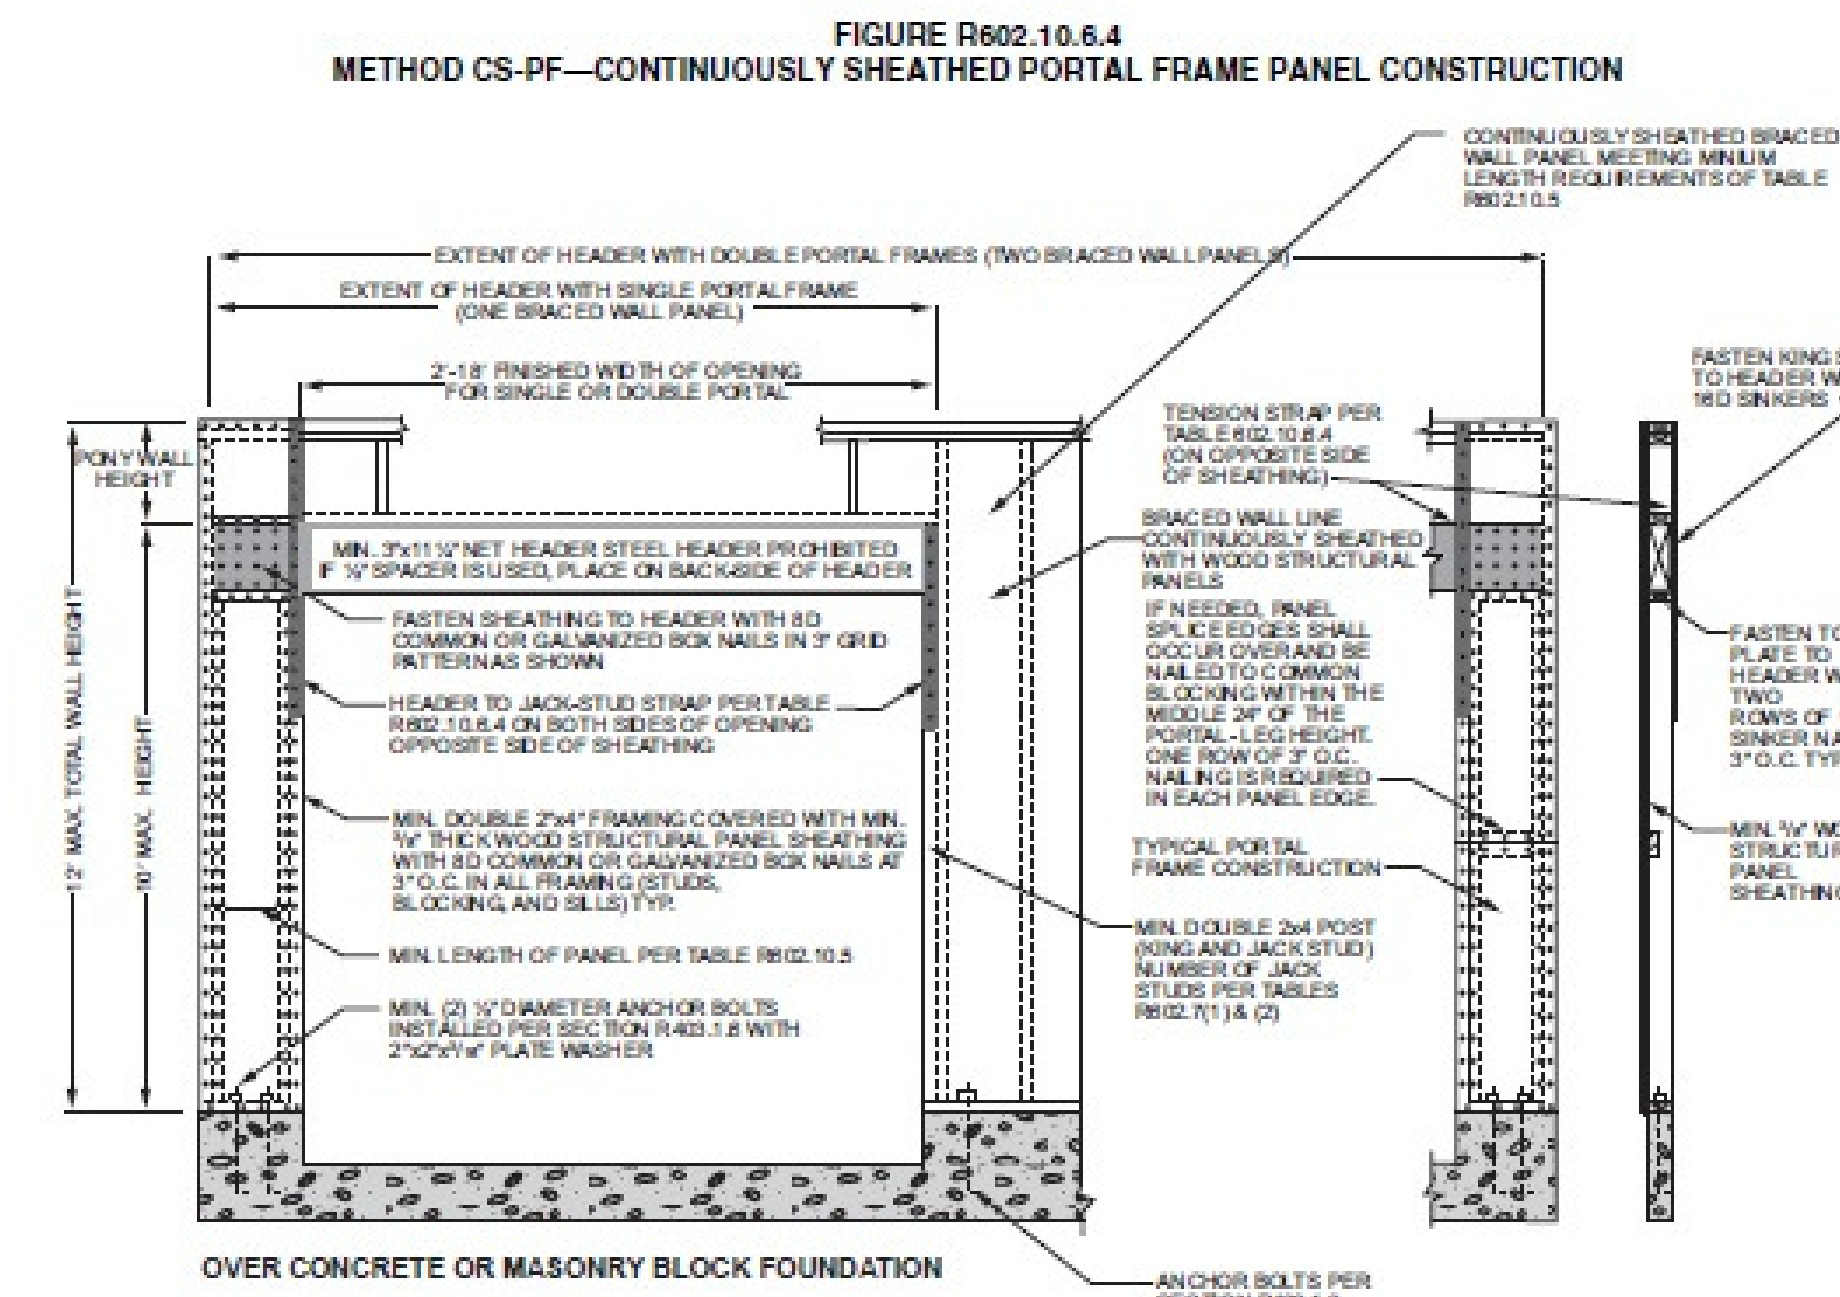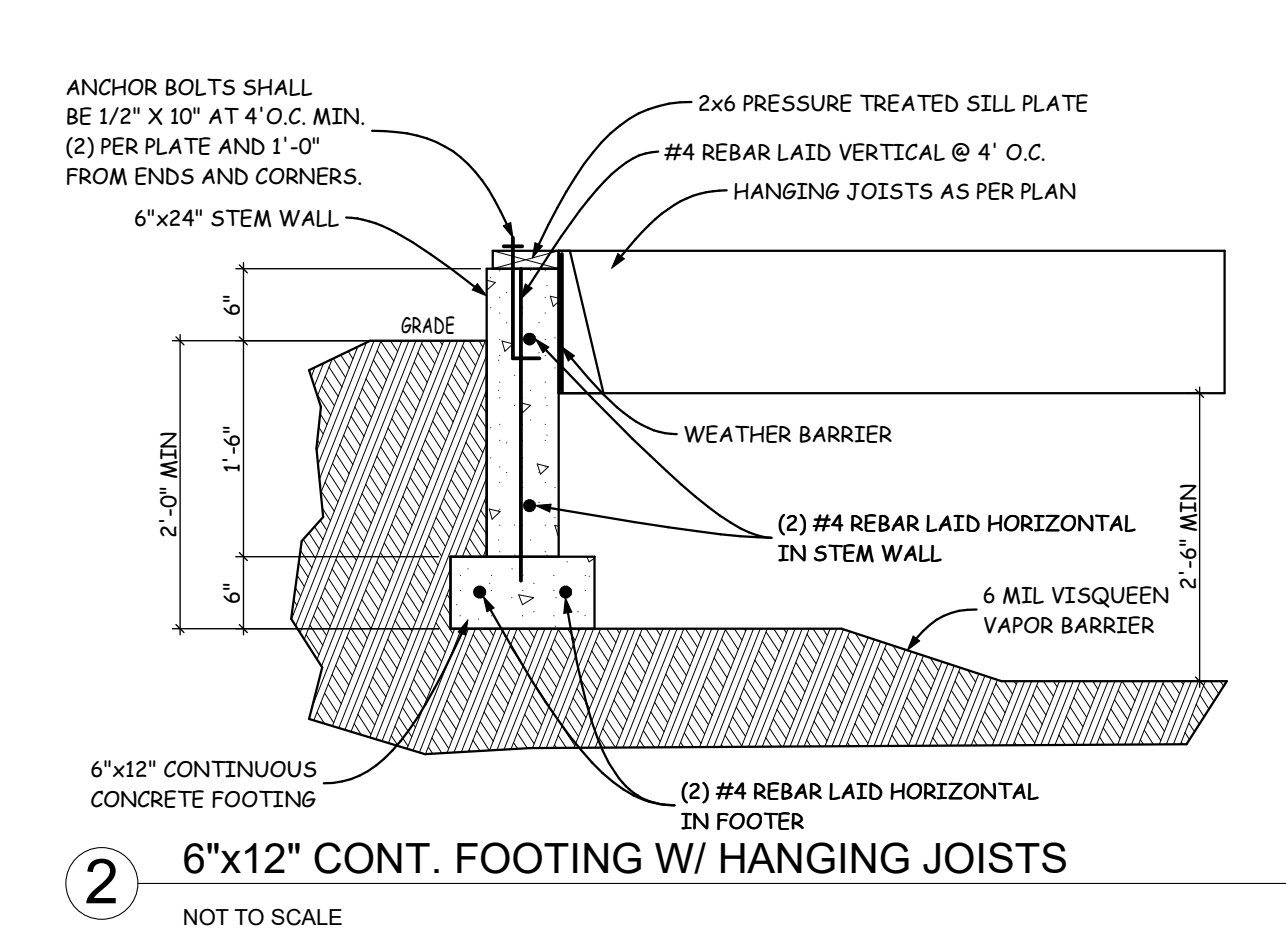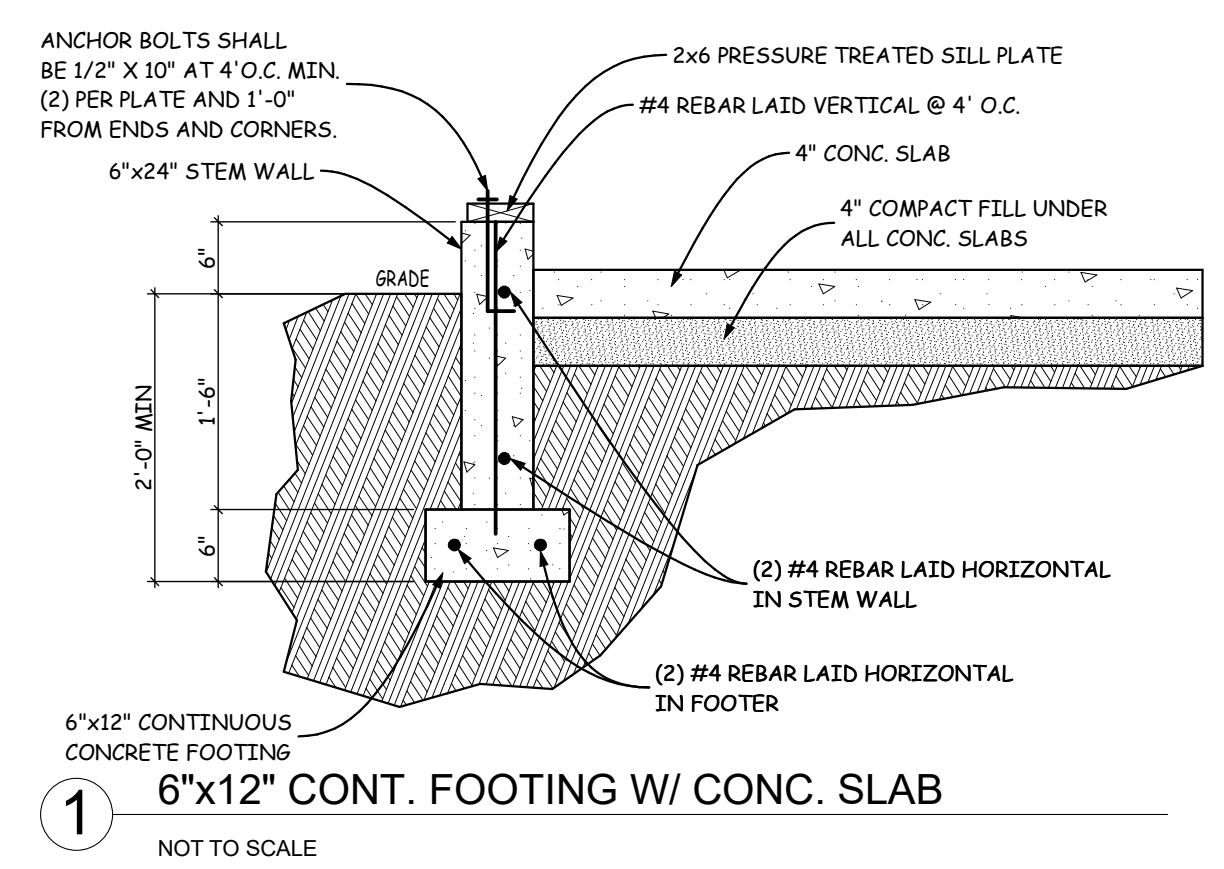

7 R602.10.6.4 CS-PF METHOD
NOT TO SCALE

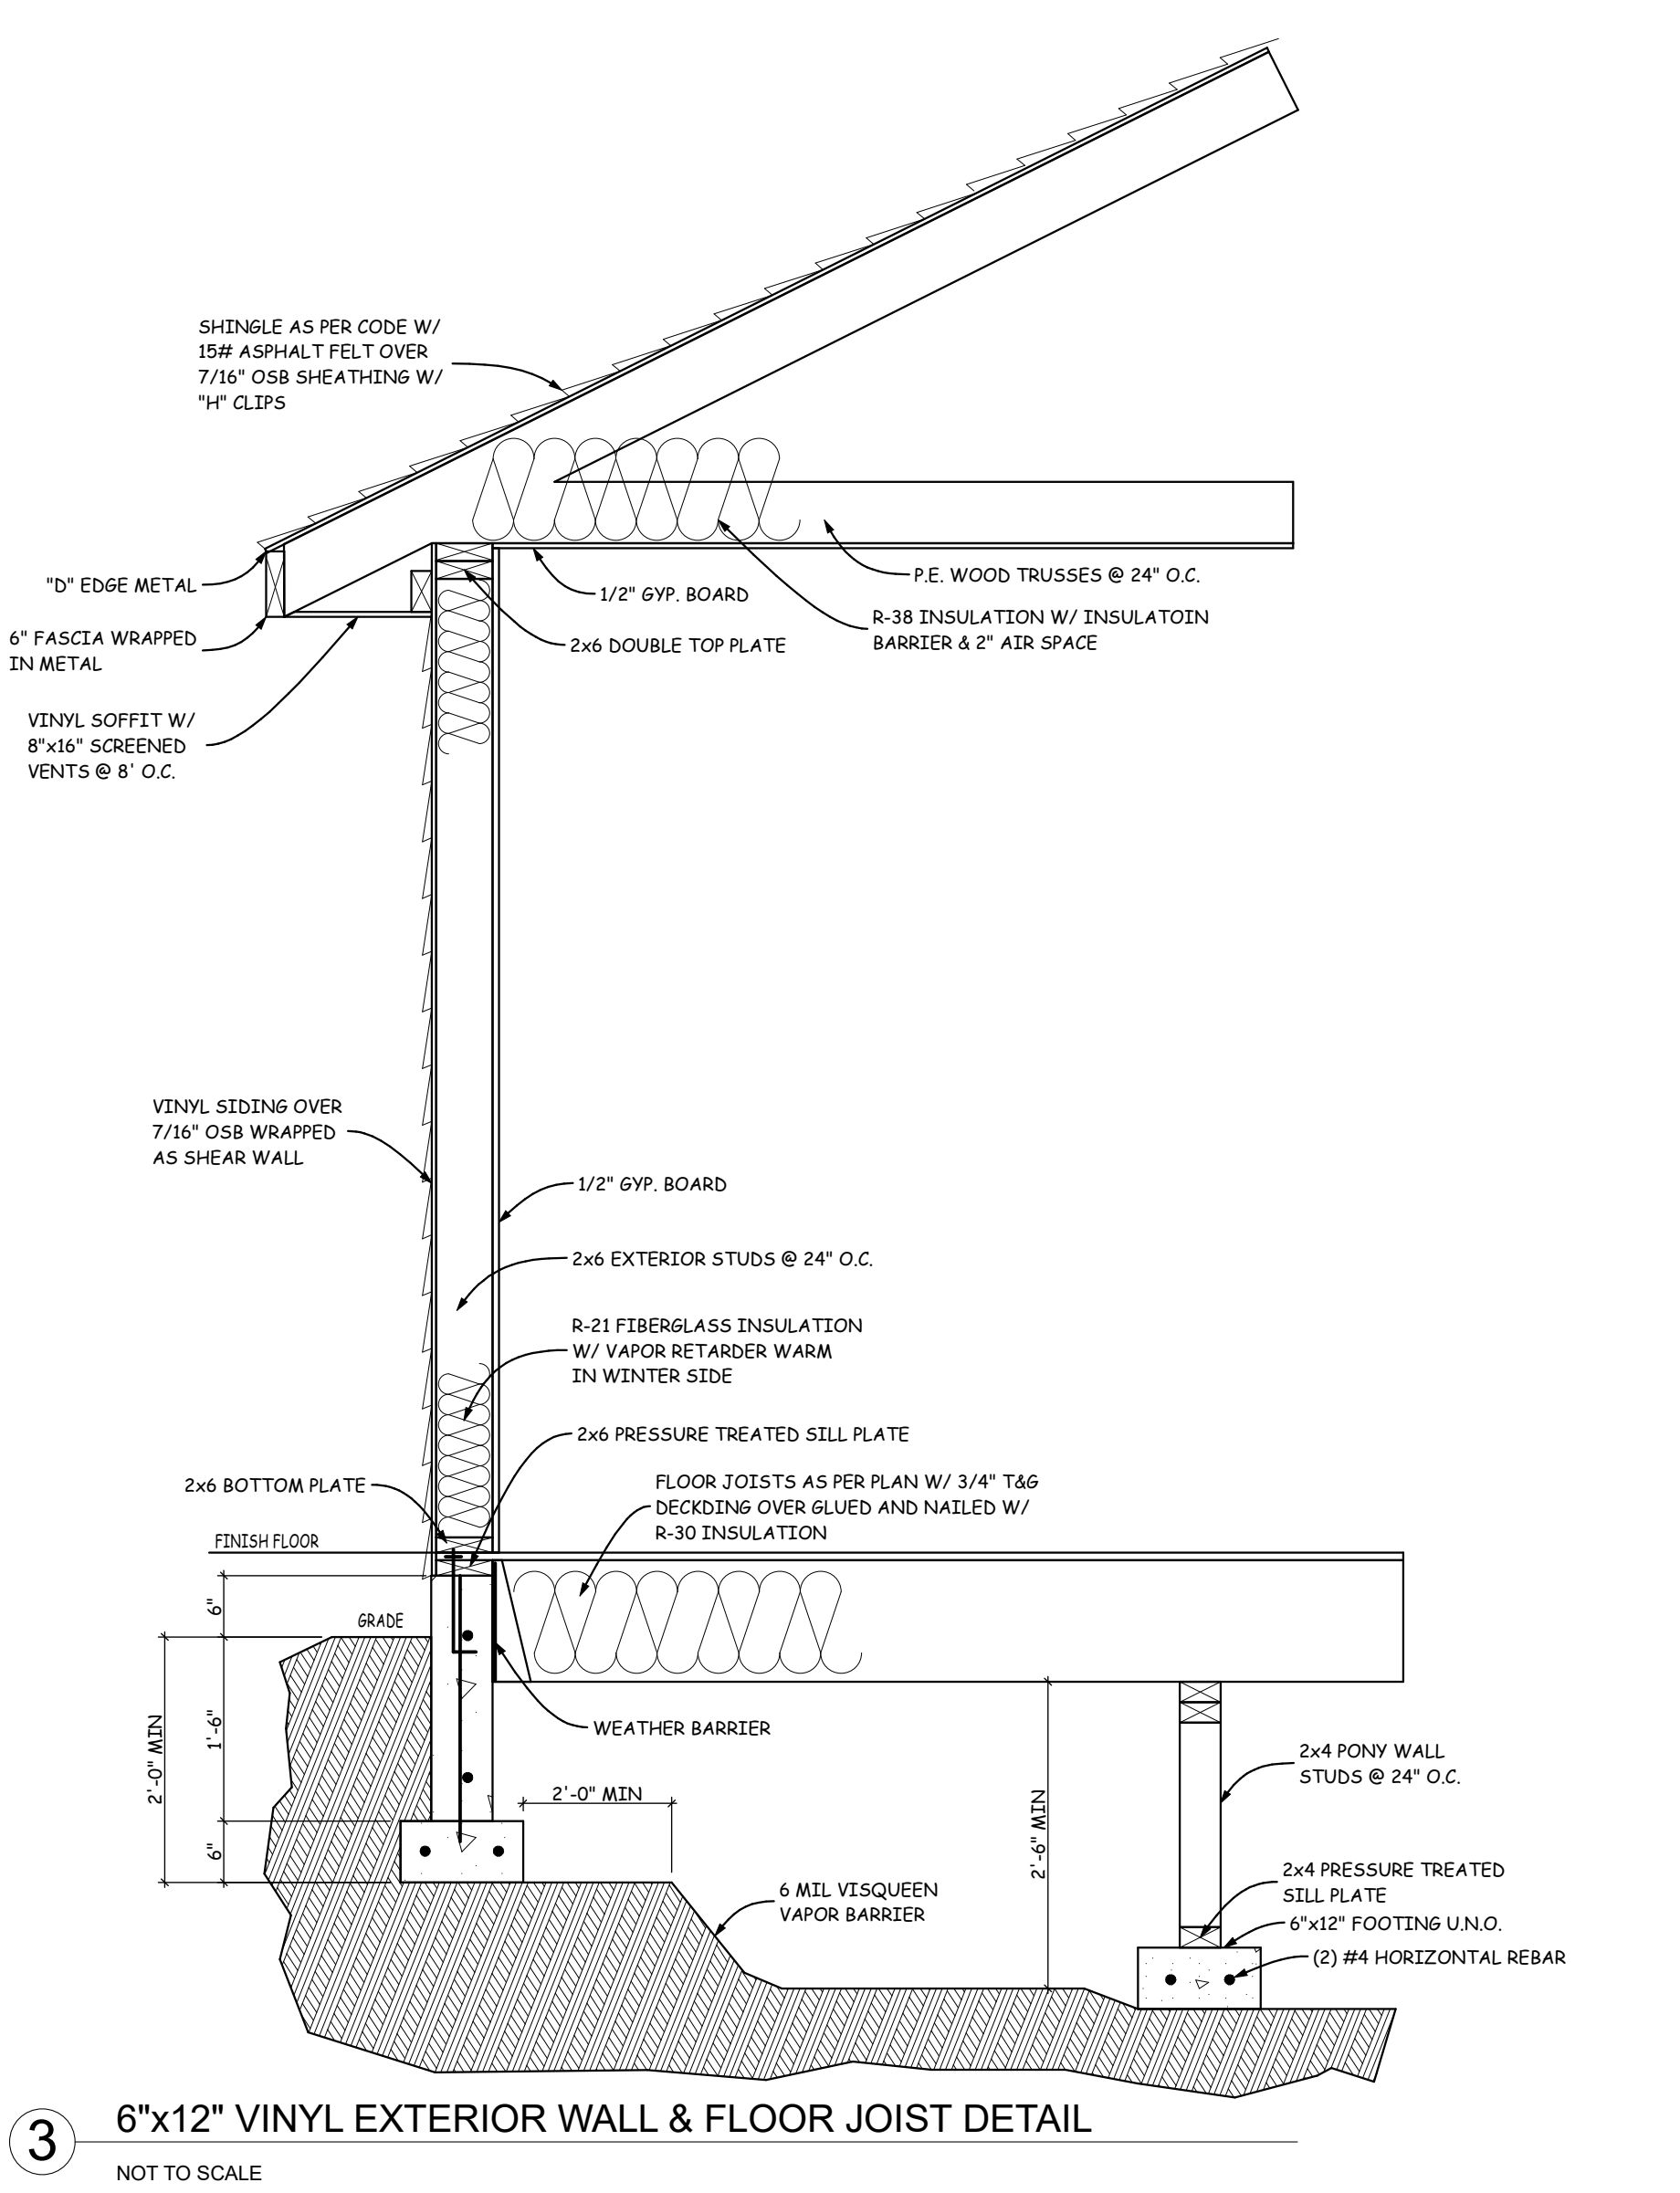

3 6"x12" VINYL EXTERIOR WALL & FLOOR JOIST DETAIL
NOT TO SCALE

Project Address:

804 Adell Circle
Filer, ID

Subdivision

Orton Addition Sub

Floor Plan

Filer Spec

Print Date:

3/17/2022

(TYP.) SCALE (U.N.O.)
1/4"=1'-0"