

Lance LeBaron Homes

COX RESIDENCE
3695 N, 2000 E, FILER, IDAHO
LOT SIZE: 1.9 ACRES
CODE COMPLIANCE: 2018 IRC
NEW CONSTRUCTION
SINGLE FAMILY RESIDENCE
MAIN LEVEL = 2203 SF
ATTACHED GARAGE = 669 SF
COVERED PATIO AREAS = 308 SF
FIRE ENVELOPE = 38,336 CF

ENERGY CODE COMPLIANCE:
Prescriptive Energy Code
R-38 Attic
R-20 Exterior Walls (Including between garage)
R-30 Floors
.35 U Value Lo-E Windows


SHEET SCHEDULE:
A1 - COVER SHEET, SITE PLAN
A2 - FOUNDATION PLAN AND DETAILS
A3 - MAIN FLOOR PLAN
A4 - ROOF PLAN
A5 - ELEVATIONS

SITE PLAN

SCALE: 1/16" = 1'0"

GENERAL NOTES

ALL WORK PERFORMED SHALL MEET CURRENT ADOPTED CODES. (IN CASE OF CONFLICTING NOTES, THE MORE STRINGENT REQUIREMENT SHALL SUPPLY).
VERIFY ALL UTILITIES BEFORE DIGGING.
PROPERTY LINES ARE CONTRACT LIMITS.
SITE AND STRUCTURE SHALL BE KEPT CLEAN. SUBCONTRACTOR TO VERIFY ALL DIMENSION. IN CASE OF ERRORS OR DISCREPANCIES CONTACT OWNER OR OWNER'S REPRESENTATIVE, BEFORE PROCEEDING. DO NOT SCALE.
DO NOT DRAIN STORM WATER ONTO ADJACENT LOTS.
STRING LINES SHALL BE PROVIDED OVER PROPERTY PINS AT TIME OF INSPECTIONS.

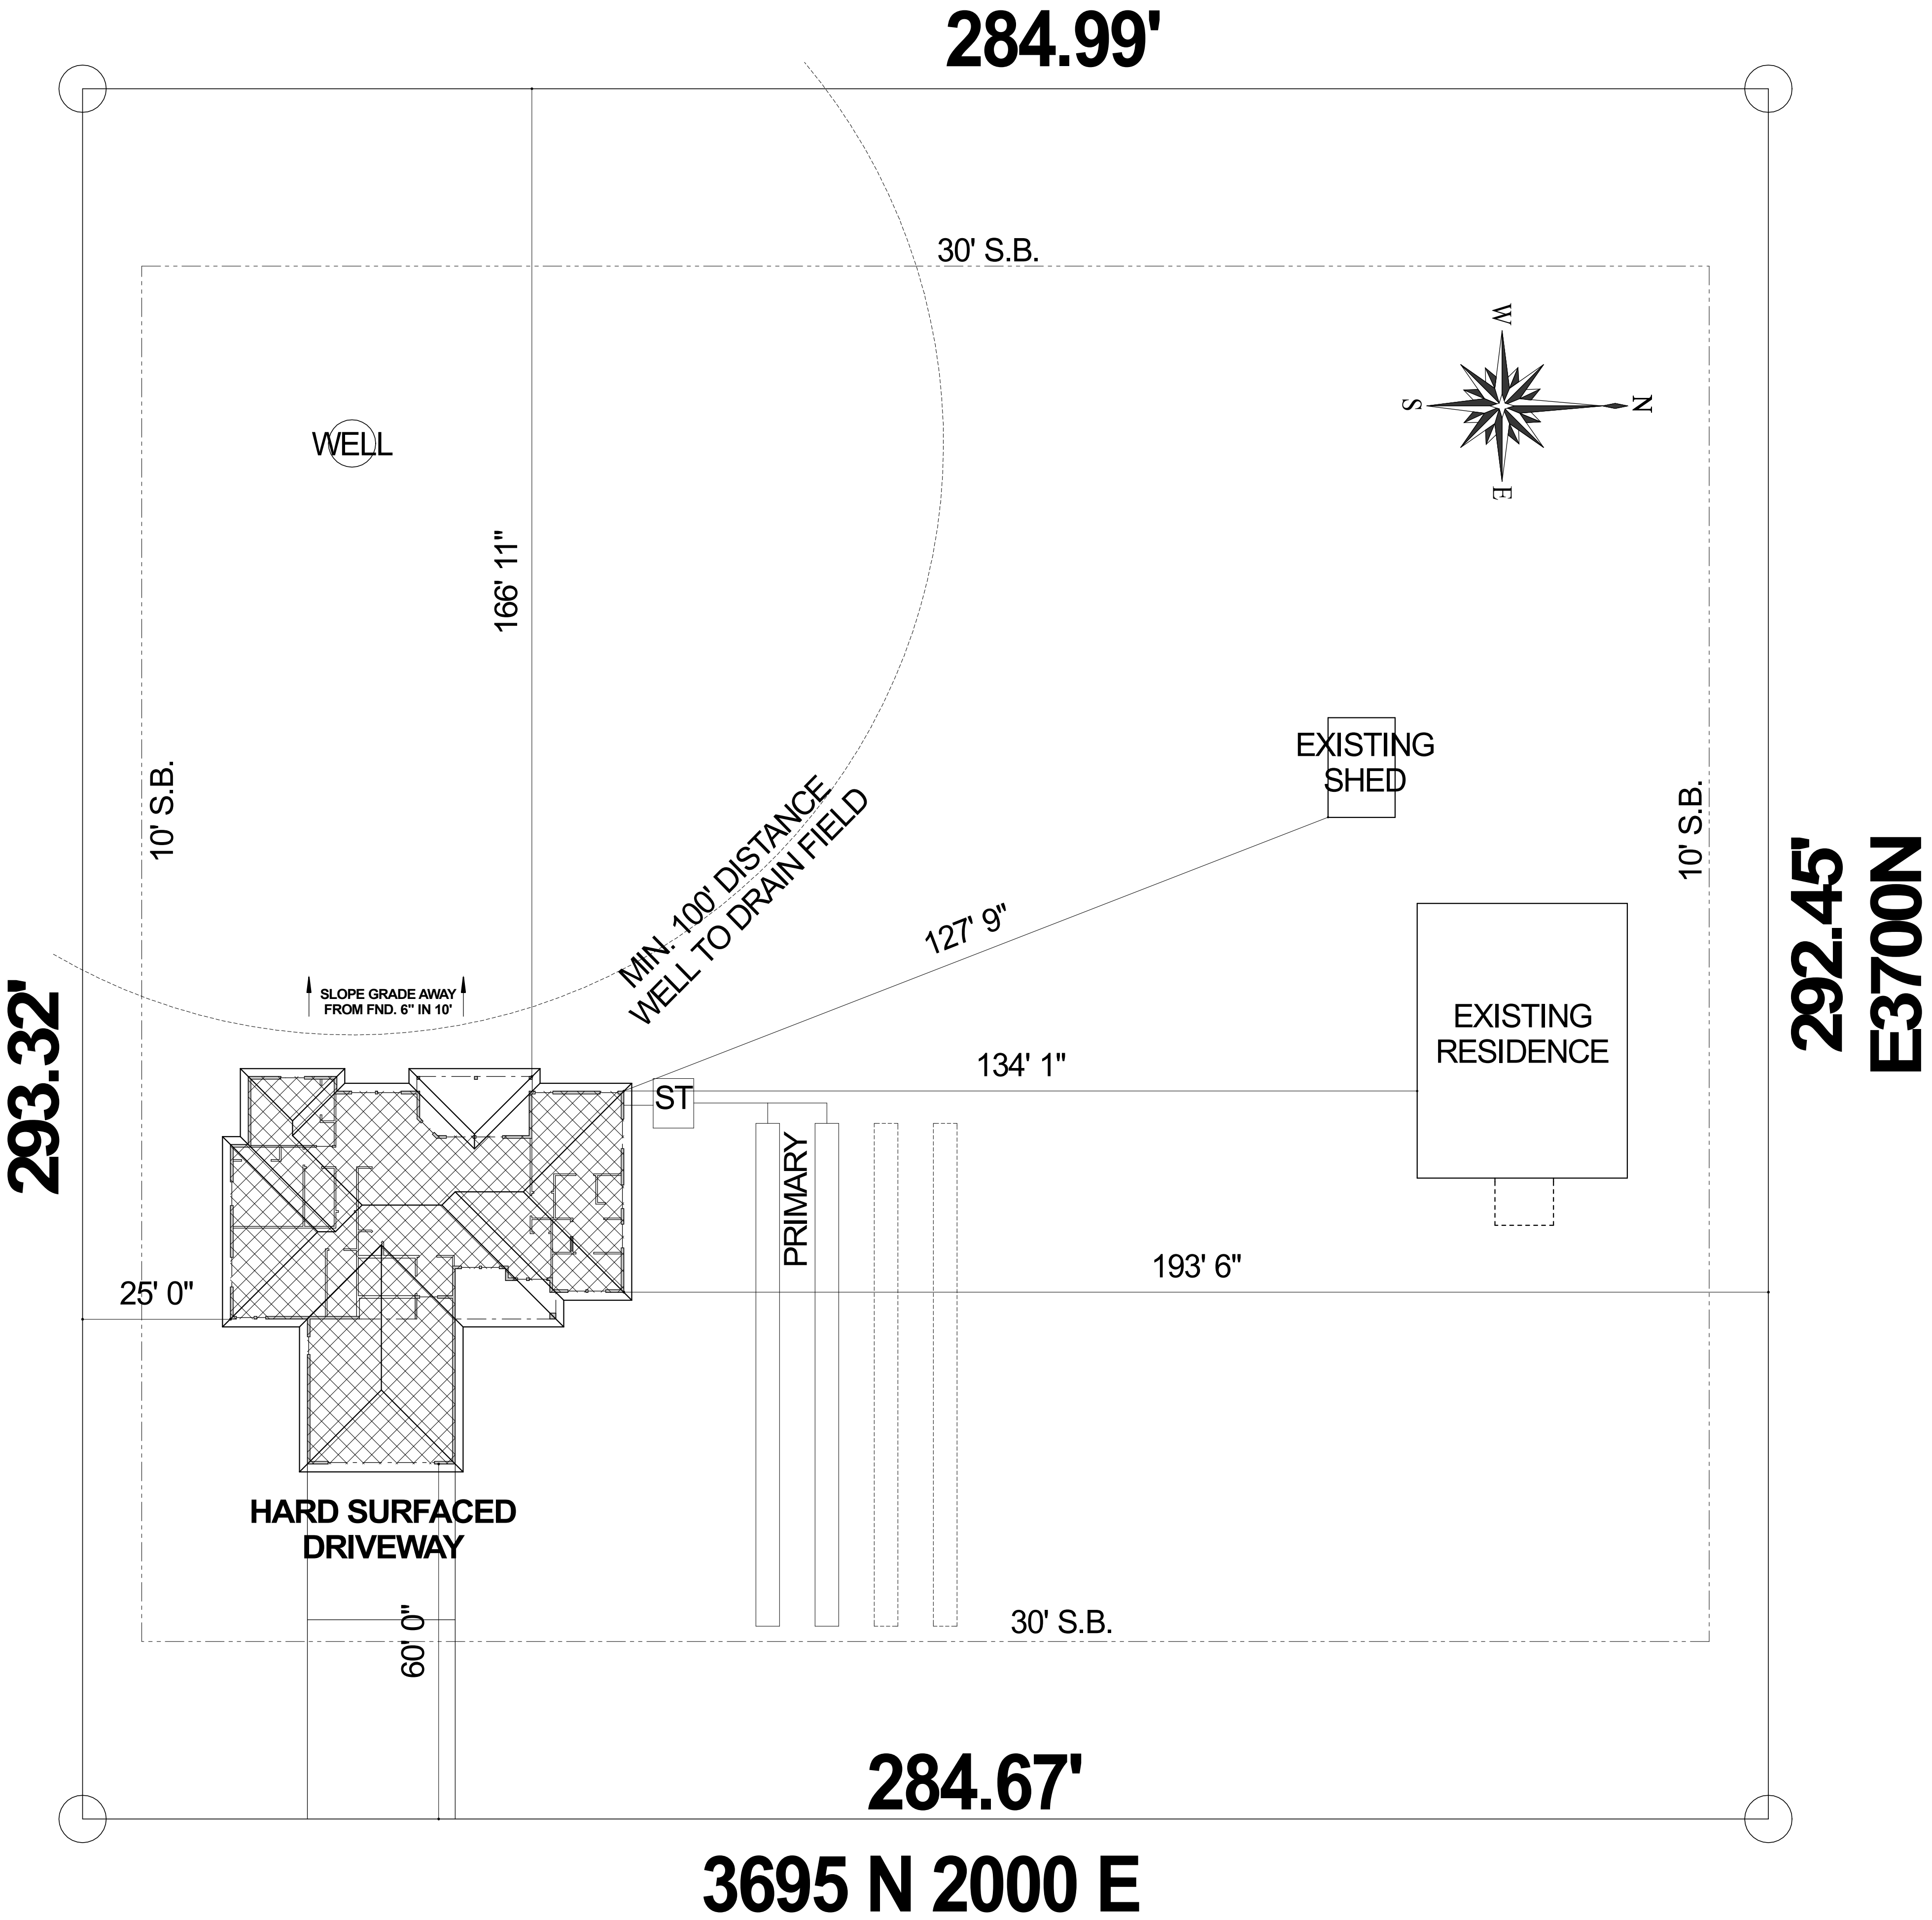

Plans and Rendering by Owens Design.

DISCLAIMER NOTE: While every attempt has been made in preparation of these plans to provide accurate information, the user of these plans is advised that they are not a substitute for a professional engineering or architectural drawing. The user of these plans is responsible for the verification of structure integrity and intended use. The user of these plans is responsible for the verification of the specifications for the building, and shall take preference over anything shown, described, or implied herein and in all contracts.

OWENS DESIGN

Twin Falls, ID 83301 ph. 208-751-6727
Email: LanneOwensDesign@gmail.com

SCALE:
1/16" = 1'0"

DRAWN BY:
Lane Owens

DATE DRAWN:
08-FEB-22

LAST REVISED:
00-00-00


PROJECT NAME:
SHEET:

Lance LeBaron Homes
COX RESIDENCE
3695 N, 2000 E, FILER, IDAHO

PLAN NAME:
SITE PLAN

A1

1 OF 5

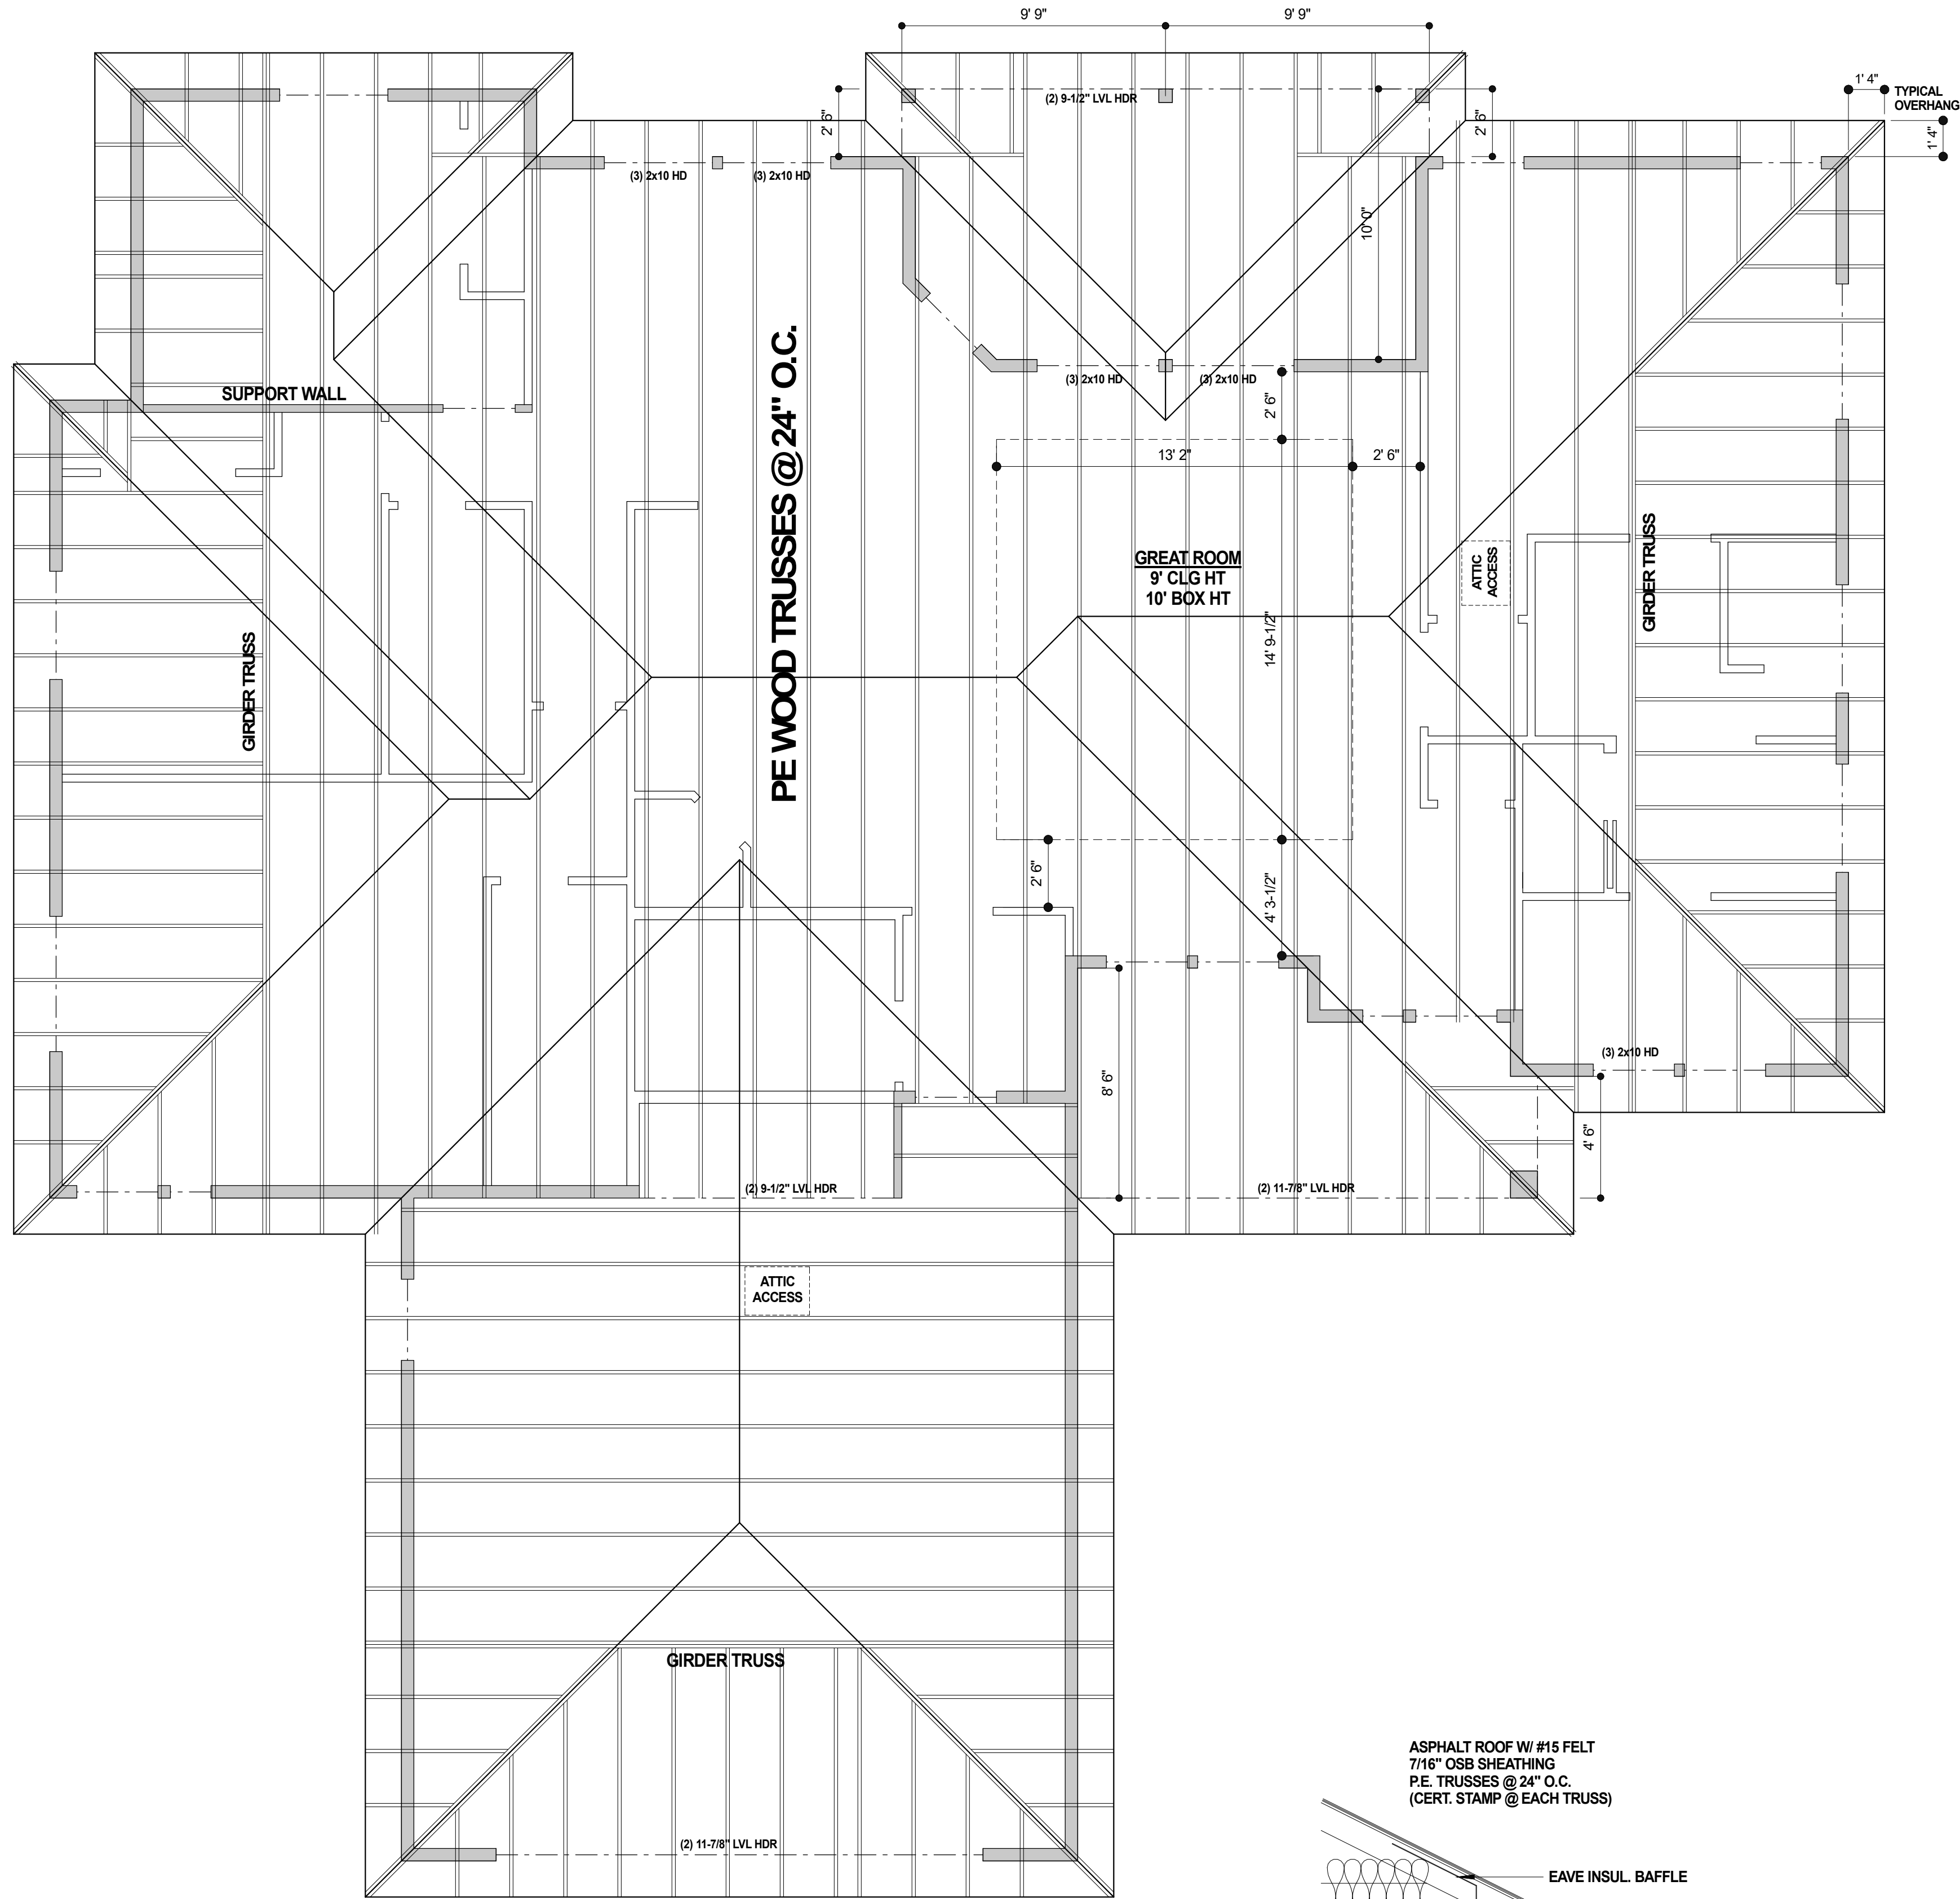


ROOF PLAN

SCALE: 1/4"=1'0"

ROOF NOTES:

1. INSTALL TRUSSES PER MANUFACTURER'S RECOMMENDATIONS INCLUDING ALL BRIDGING AND BRACING.
2. PROVIDE SIMPSON H1 OR EQUAL AT BRG. ENDS OF EACH TRUSS.
3. BEARING WALL HEADERS SHALL BE (2ea) DF 2x10 UNLESS NOTED OTHERWISE.
4. ALL ROOF OVERHANGS SHALL BE AS NOTED.
5. ROOF SHEATHING SHALL BE 7/16" OSB W/ PLY CLIPS
6. ALL SHADED AREAS REPRESENT LOAD BEARING POINTS FOR TRUSSES.
7. ROOF VENTILATION REQUIREMENTS PER IRC R806.1

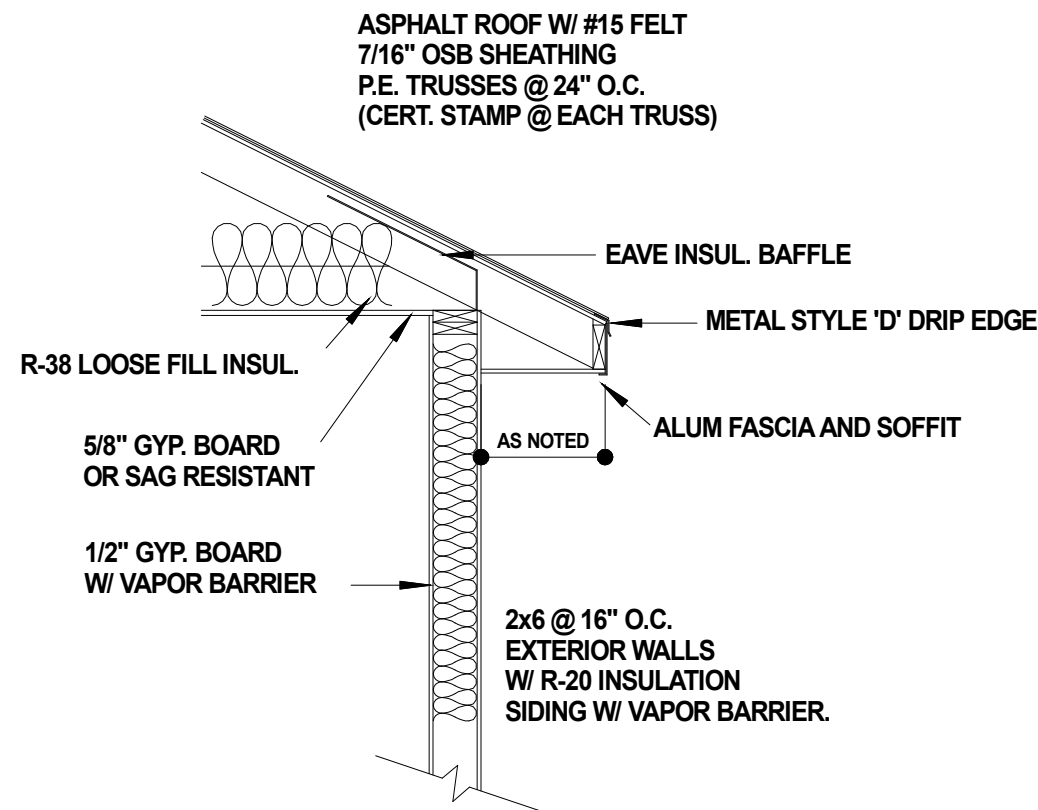

TYP. EAVE DETAIL

SCALE: 1/2" = 1'0"

PROJECT NAME:

Lance LeBaron Homes
COX RESIDENCE
3695 N, 2000 E, FILER, IDAHO

SHEET:

A4

PLAN NAME: ROOF PLAN

SCALE:

1/4" = 1'-0"

DRAWN BY:

Lane Owens

DATE DRAWN:

08-FEB-22

LAST REVISED:

00-00-00



Twin Falls, ID 83301 ph. 208-731-8727
Email: LaneOwensDesign@gmail.com

Plans and Rendering by Owens Design.

DISCLAIMER NOTE: While every attempt has been made in preparation of these plans to ensure accuracy, the user of these plans is advised that they are not a contract. The user is responsible for obtaining all necessary permits and for ensuring that the plans comply with all applicable codes and regulations. The user is also responsible for ensuring that the plans are used in accordance with the specifications and for any errors or omissions, the user shall be responsible for any and all consequences thereof. The user shall be responsible for any and all consequences thereof.

