

Lance LeBaron Homes

KRAUSE RESIDENCE
LOT-2, BLK-1, TRIPLE CROWN #2
ALLIE LANE, FILER, ID
LOT SIZE: 1.04 ACRES
CODE COMPLIANCE: 2018 IRC
NEW CONSTRUCTION
SINGLE FAMILY RESIDENCE
MAIN LEVEL = 2036 SF
BONUS ROOM = 306 SF
ATTACHED GARAGE = 906 SF
COVERED PATIO AREAS = 345 SF
FIRE ENVELOPE = 44,130 CF

ENERGY CODE COMPLIANCE:
Prescriptive Energy Code
R-38 Attic
R-20 Exterior Walls (Including between garage)
R-30 Floors
.35 U Value Lo-E Windows

SHEET SCHEDULE:
A1 - COVER SHEET, SITE PLAN
A2 - FOUNDATION PLAN AND DETAILS
A3 - MAIN FLOOR PLAN
A4 - ROOF PLAN & BONUS ROOM
A5 - ELEVATIONS & BONUS ROOM SECTION

SITE PLAN

SCALE: 1/16" = 1'0"

GENERAL NOTES

ALL WORK PERFORMED SHALL MEET CURRENT ADOPTED CODES. (IN CASE OF CONFLICTING NOTES, THE MORE STRINGENT REQUIREMENT SHALL SUPPLY).


VERIFY ALL UTILITIES BEFORE DIGGING.

PROPERTY LINES ARE CONTRACT LIMITS.

SITE AND STRUCTURE SHALL BE KEPT CLEAN. SUBCONTRACTOR TO VERIFY ALL DIMENSION. IN CASE OF ERRORS OR DISCREPANCIES CONTACT OWNER OR OWNER'S REPRESENTATIVE, BEFORE PROCEEDING. DO NOT SCALE.

DO NOT DRAIN STORM WATER ONTO ADJACENT LOTS.

STRING LINES SHALL BE PROVIDED OVER PROPERTY PINS AT TIME OF INSPECTIONS.

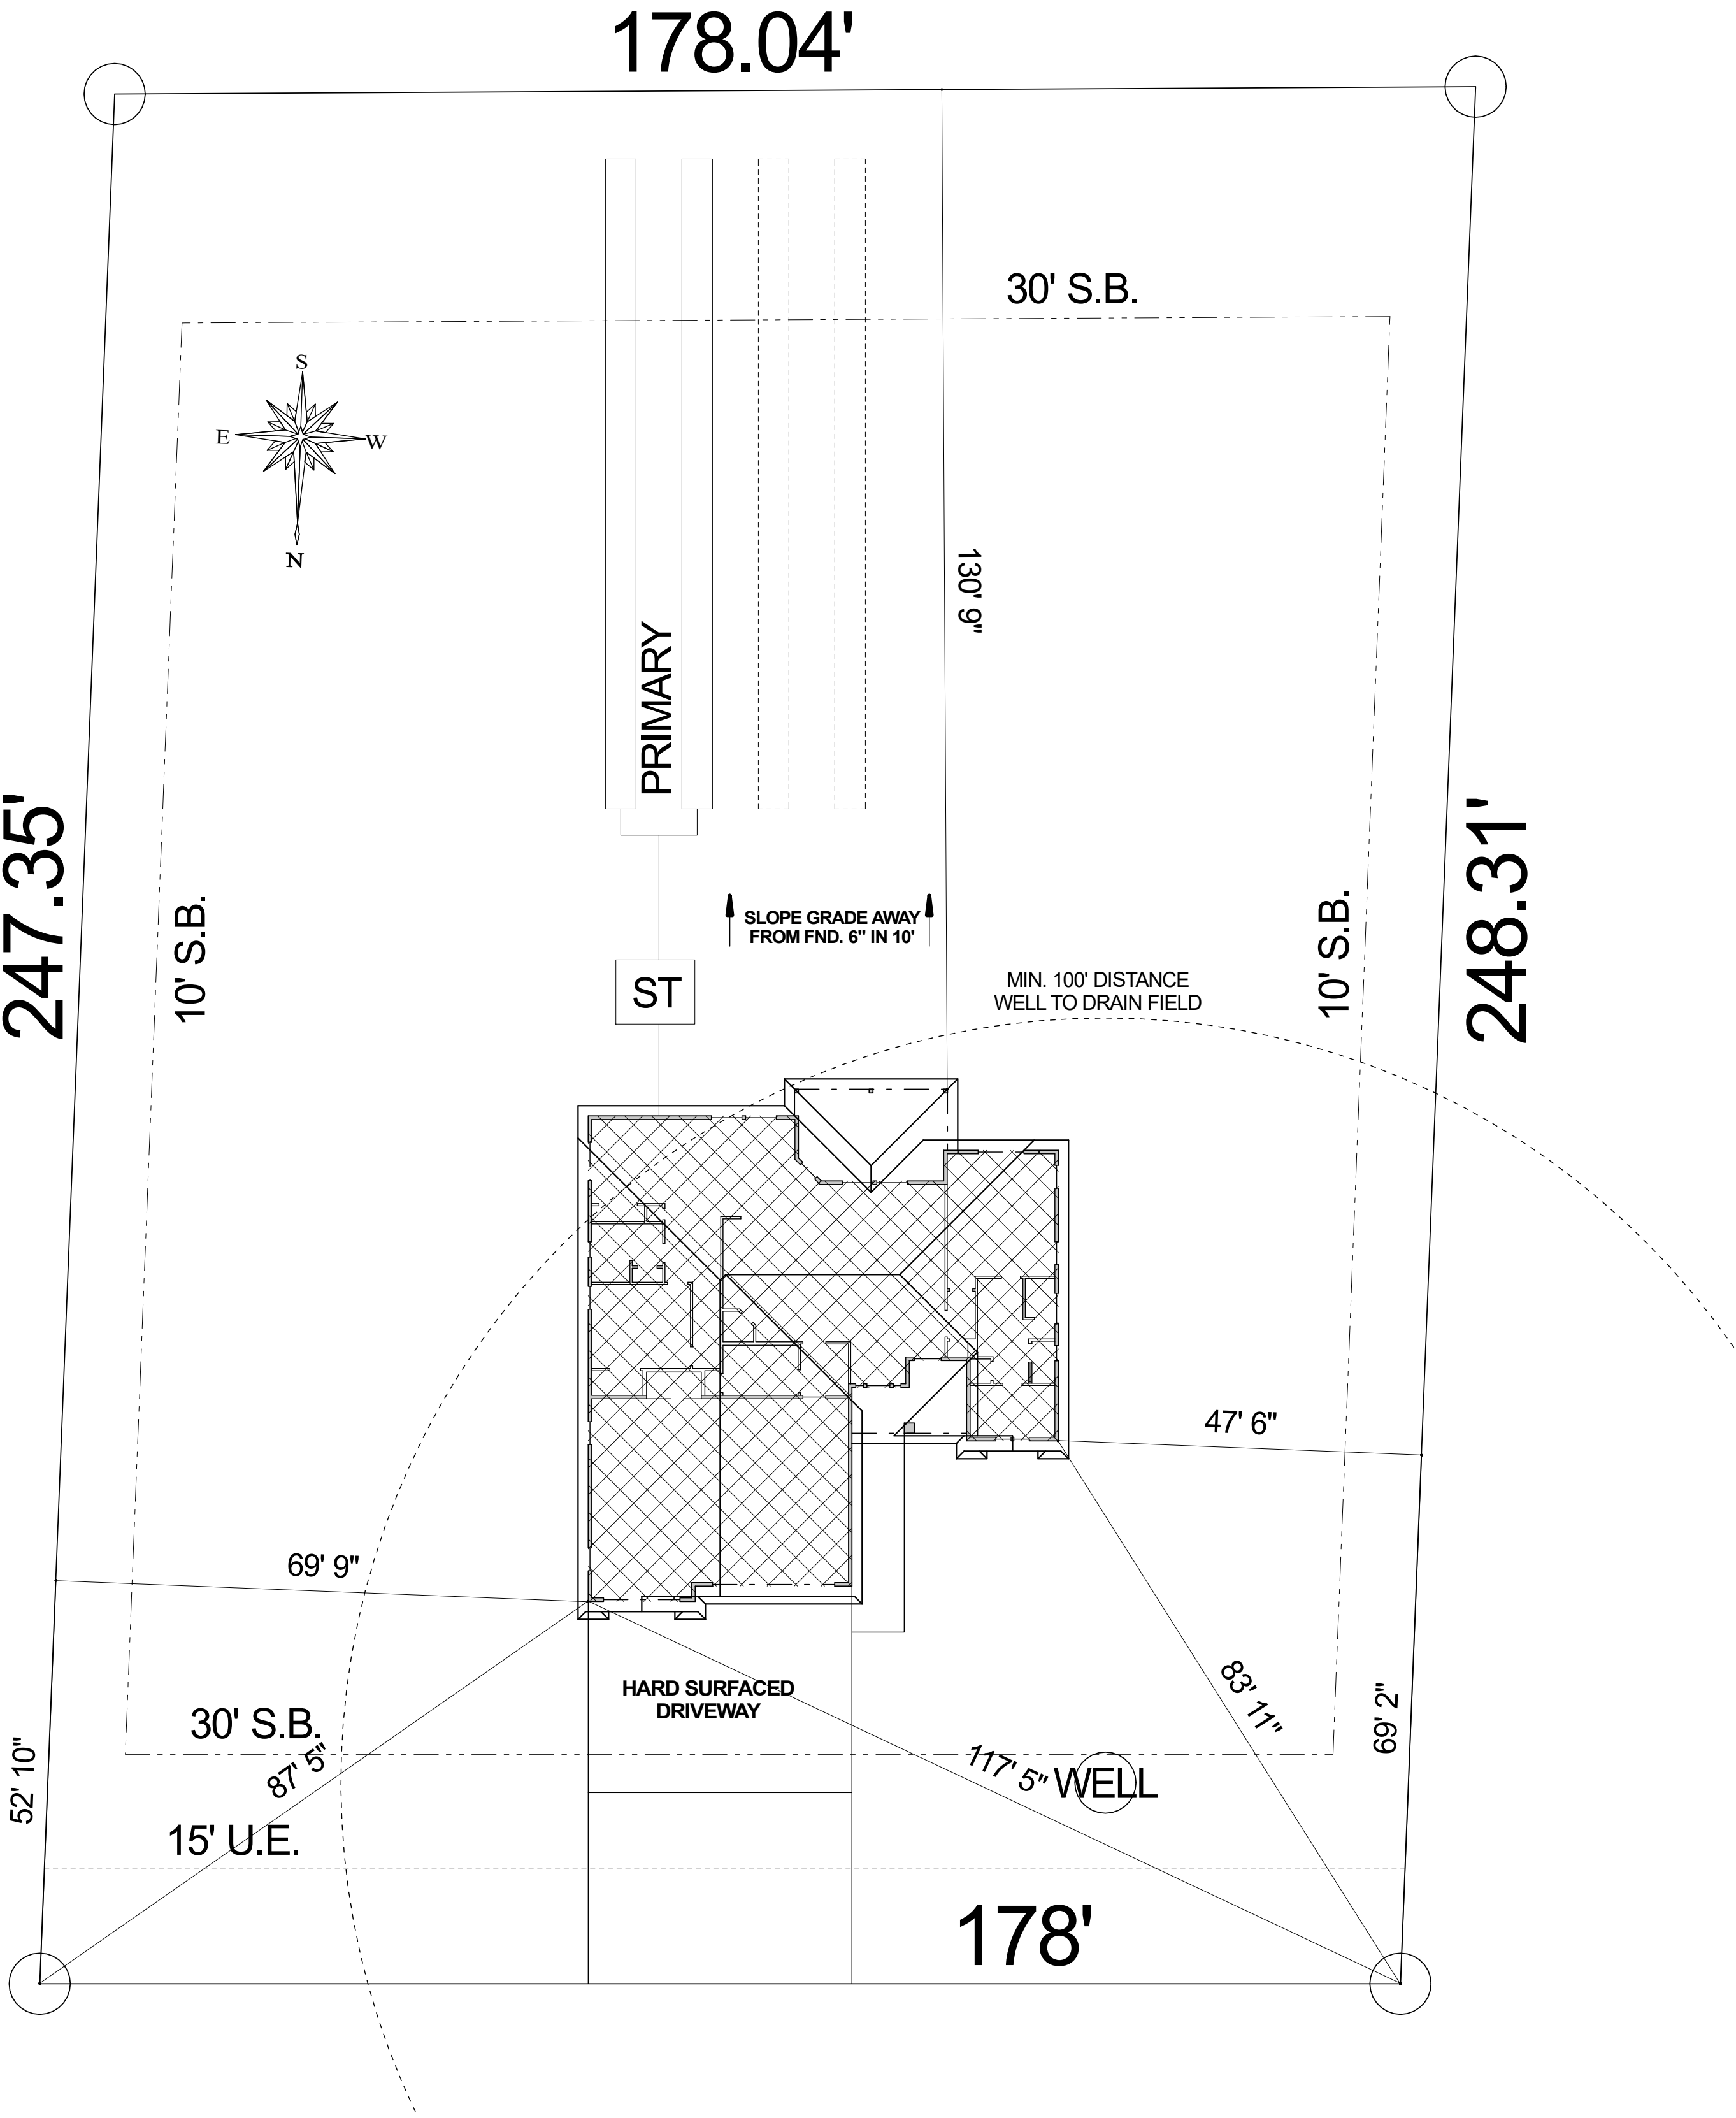

Plans and Rendering by Owens Design.

OWENS DESIGN

Twin Falls, ID 83301 ph. 208-731-4372
Email: LaneOwensDesign@gmail.com

DISCLAIMER NOTE: While every attempt has been made in preparation of these plans to provide an accurate representation of the project, the designer does not warrant or represent that the plans are free of errors or omissions. The designer shall not be responsible for any errors or omissions that may occur in the construction of the project. The contractor is responsible for the verification of the site conditions and the accuracy of the specifications for the building, and shall take preference over anything shown, described, or implied herein same as it varies.

PROJECT NAME:

Lance LeBaron Homes
KRAUSE RESIDENCE
LOT-2, BLK-1, TRIPLE CROWN #2
ALLIE LANE, FILER, IDAHO

SHEET:

A1

PLAN NAME:

SITE PLAN


1 OF 5

SCALE: 1/16" = 1'0"


DRAWN BY: Lane Owens

DATE DRAWN: 04-JAN-22


LAST REVISED: 00-00-00

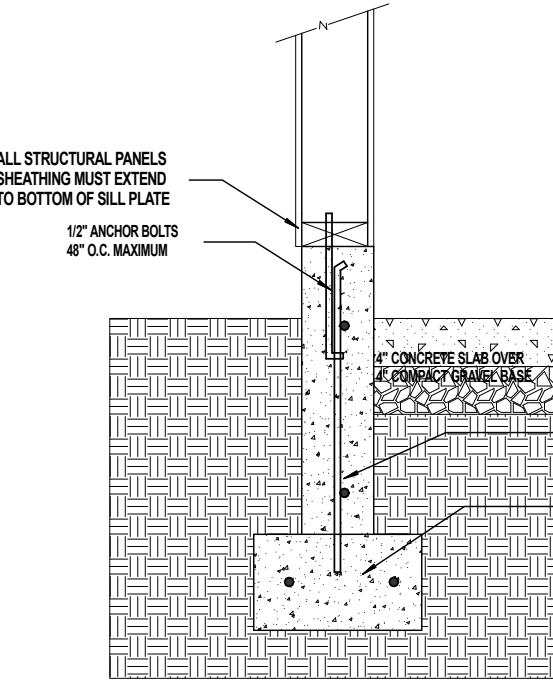


1 GARAGE FOUNDATION DETAIL
SCALE: 3/4"=1'0"

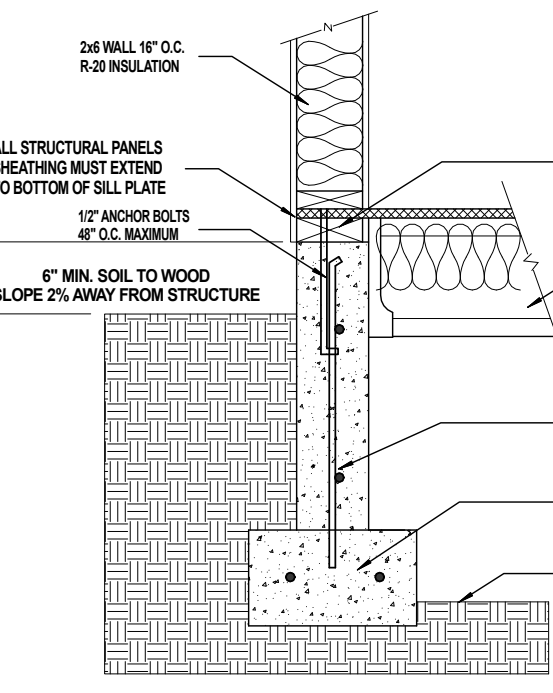


2 EXTERIOR FOUNDATION DETAIL
SCALE: 3/4"=1'0"

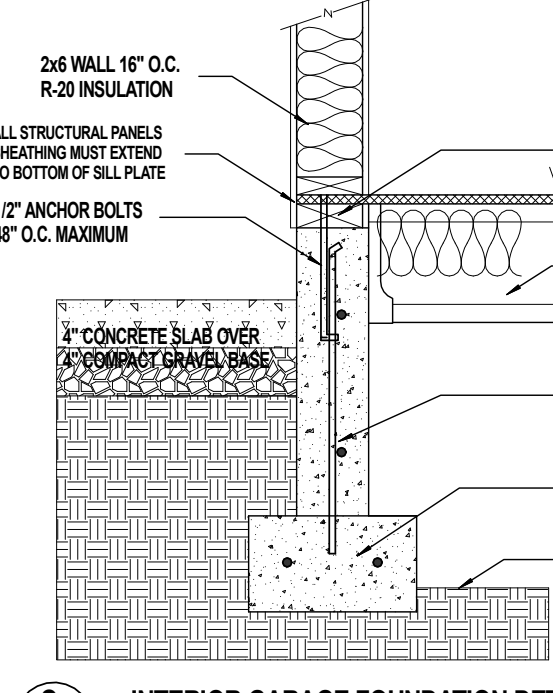

3 INTERIOR GARAGE FOUNDATION DETAIL
SCALE: 3/4"=1'0"

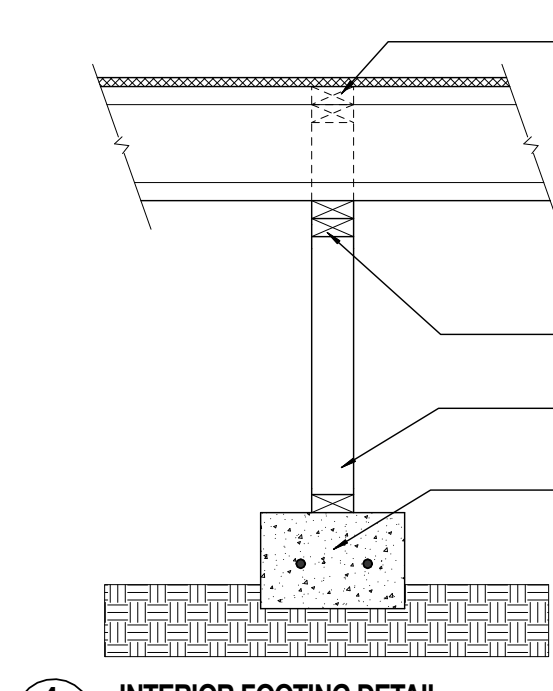

4 INTERIOR FOOTING DETAIL
SCALE: 3/4"=1'0"

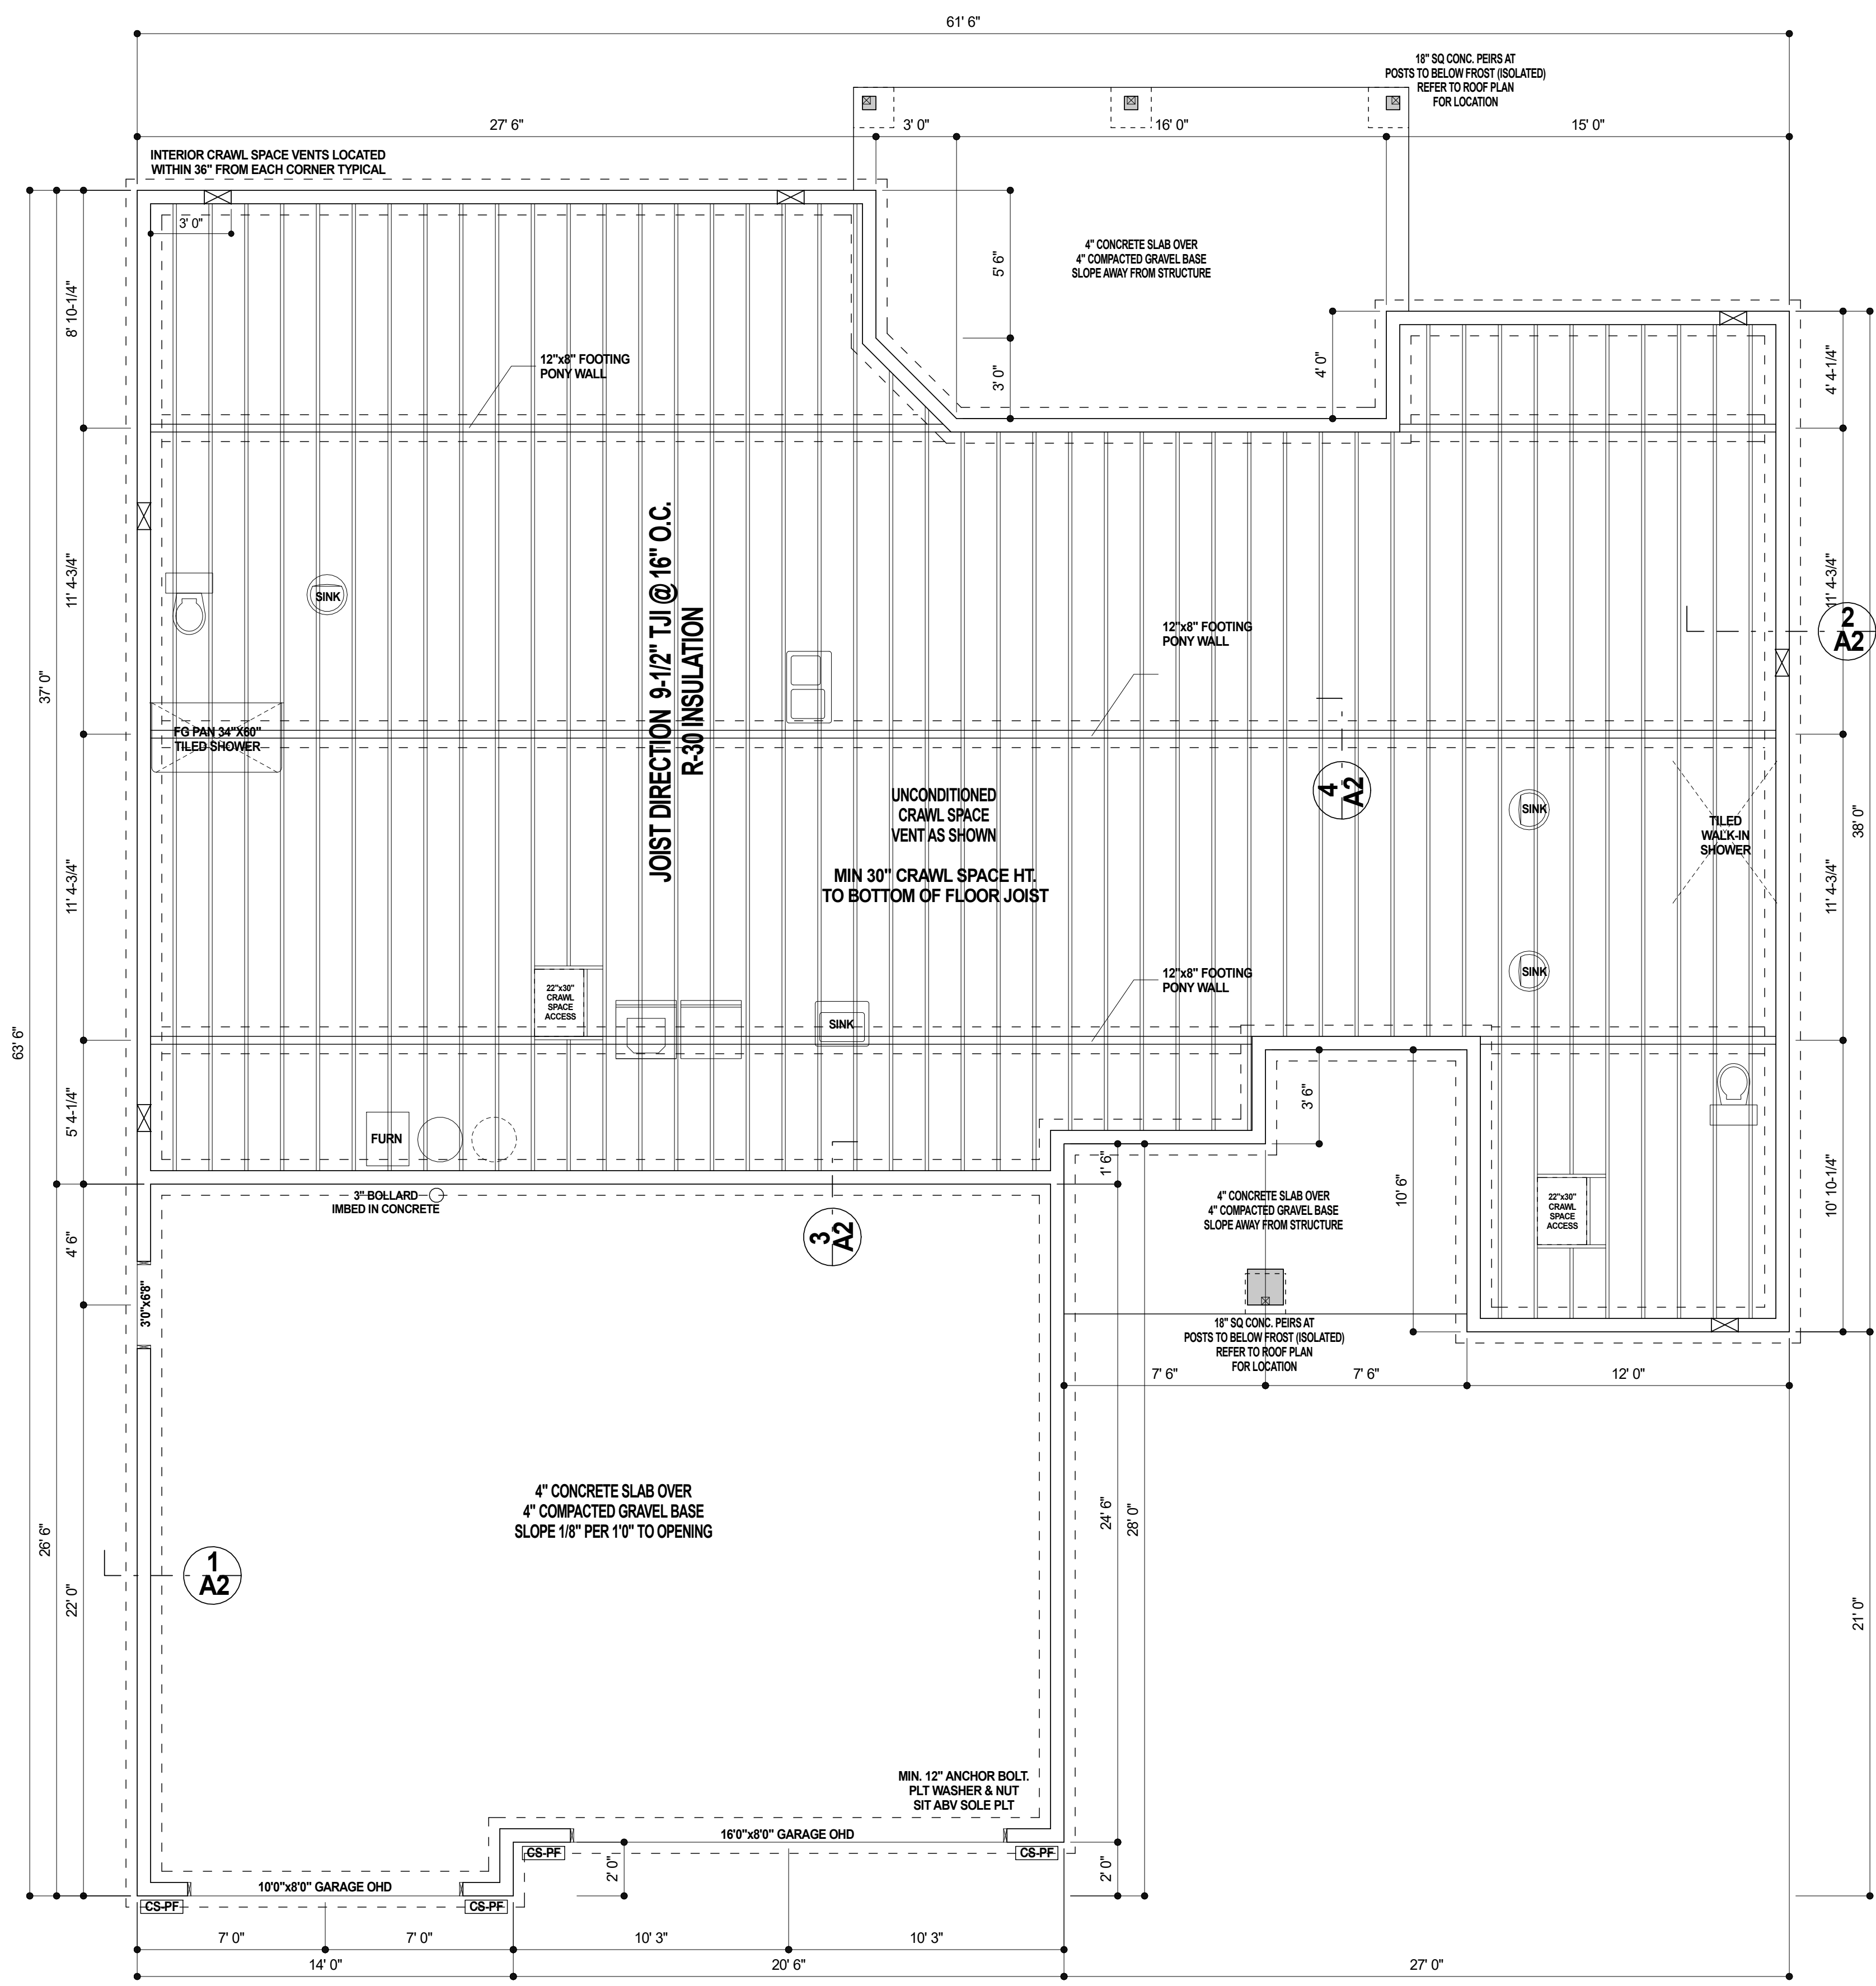

FOUNDATION PLAN

SCALE: 1/4"=1'0"

FOUNDATION NOTES:

1. BOTTOM OF FOOTING AND FOUNDATION SHALL BE BELOW LOCAL FROST LINE.
2. CONTRACTOR SHALL VERIFY ALL WINDOW AND DOOR ROUGH OPENING SIZES BEFORE FORMING BLOCK OUTS AS NECESSARY.
3. PROVIDE EXPANSION JOINTS IN ALL FLATWORK AS NECESSARY.
4. ALL FOUNDATION WALLS SHALL BE MIN. 3,000#/SQ IN. COMPRESSIVE STRENGTH @ 28 DAYS. ALL PORCHES, PARKING SLABS, STEPS AND GARAGE FLOOR SLABS SHALL BE MIN. 3,500#/SQ IN. COMPRESSIVE STRENGTH @ 28 DAYS.
5. DESIGNER ASSUMES NO RESPONSIBILITY FOR STRUCTURAL INTEGRITY. VERIFY ALL STRUCTURAL SPECIFICATIONS W/ MFG., TRUSS VENDOR OR ENGINEER.
6. SEE BRACING WALL PANEL FOR HOLD DOWN LOCATIONS AND DESCRIPTIONS.

FLOOR FRAMING NOTES:

1. INSTALL TJI'S PER MANUFACTURER'S RECOMMENDATIONS INCLUDING ALL BRIDGING AND BRACING.
2. PROVIDE DBL JOISTS UNDER ALL BEARING WALLS THAT RUN PARALLEL TO FLOOR JOISTS.
3. FRAME AROUND STAIRS USING 1.75x11-7/8 LVL.
4. ALL BEARING WALL HEADERS SHALL BE (2ea) DF 2x10 UNLESS NOTED OTHERWISE.
5. ALL EXTERIOR WALLS ARE BEARING WALLS.
6. JOIST COUNT SHOULD BE DETERMINED FROM JOIST SPACING NOT FROM DRAWING LAYOUT.

Plans and Rendering by Owens Design

DISCLAIMER NOTE: While every attempt has been made in preparation of these plans to ensure accuracy, the designer assumes no responsibility for errors or omissions. The contractor is responsible for verifying all dimensions and materials with the manufacturer and the local building department. The designer assumes no responsibility for the construction of the building, and shall take preference over anything shown, described, or implied herein.



SCALE: 1/4" = 1'-0"

DRAWN BY: Lane Owens

DATE DRAWN: 04-JAN-22

LAST REVISED: 00-00-00


PROJECT NAME: Lance LeBaron Homes

SHEET: KRAUSE RESIDENCE LOT-2, BLK-1, TRIPLE CROWN #2

ALLIE LANE, FILER, IDAHO

PLAN NAME: FOUNDATION PLAN

2 OF 5

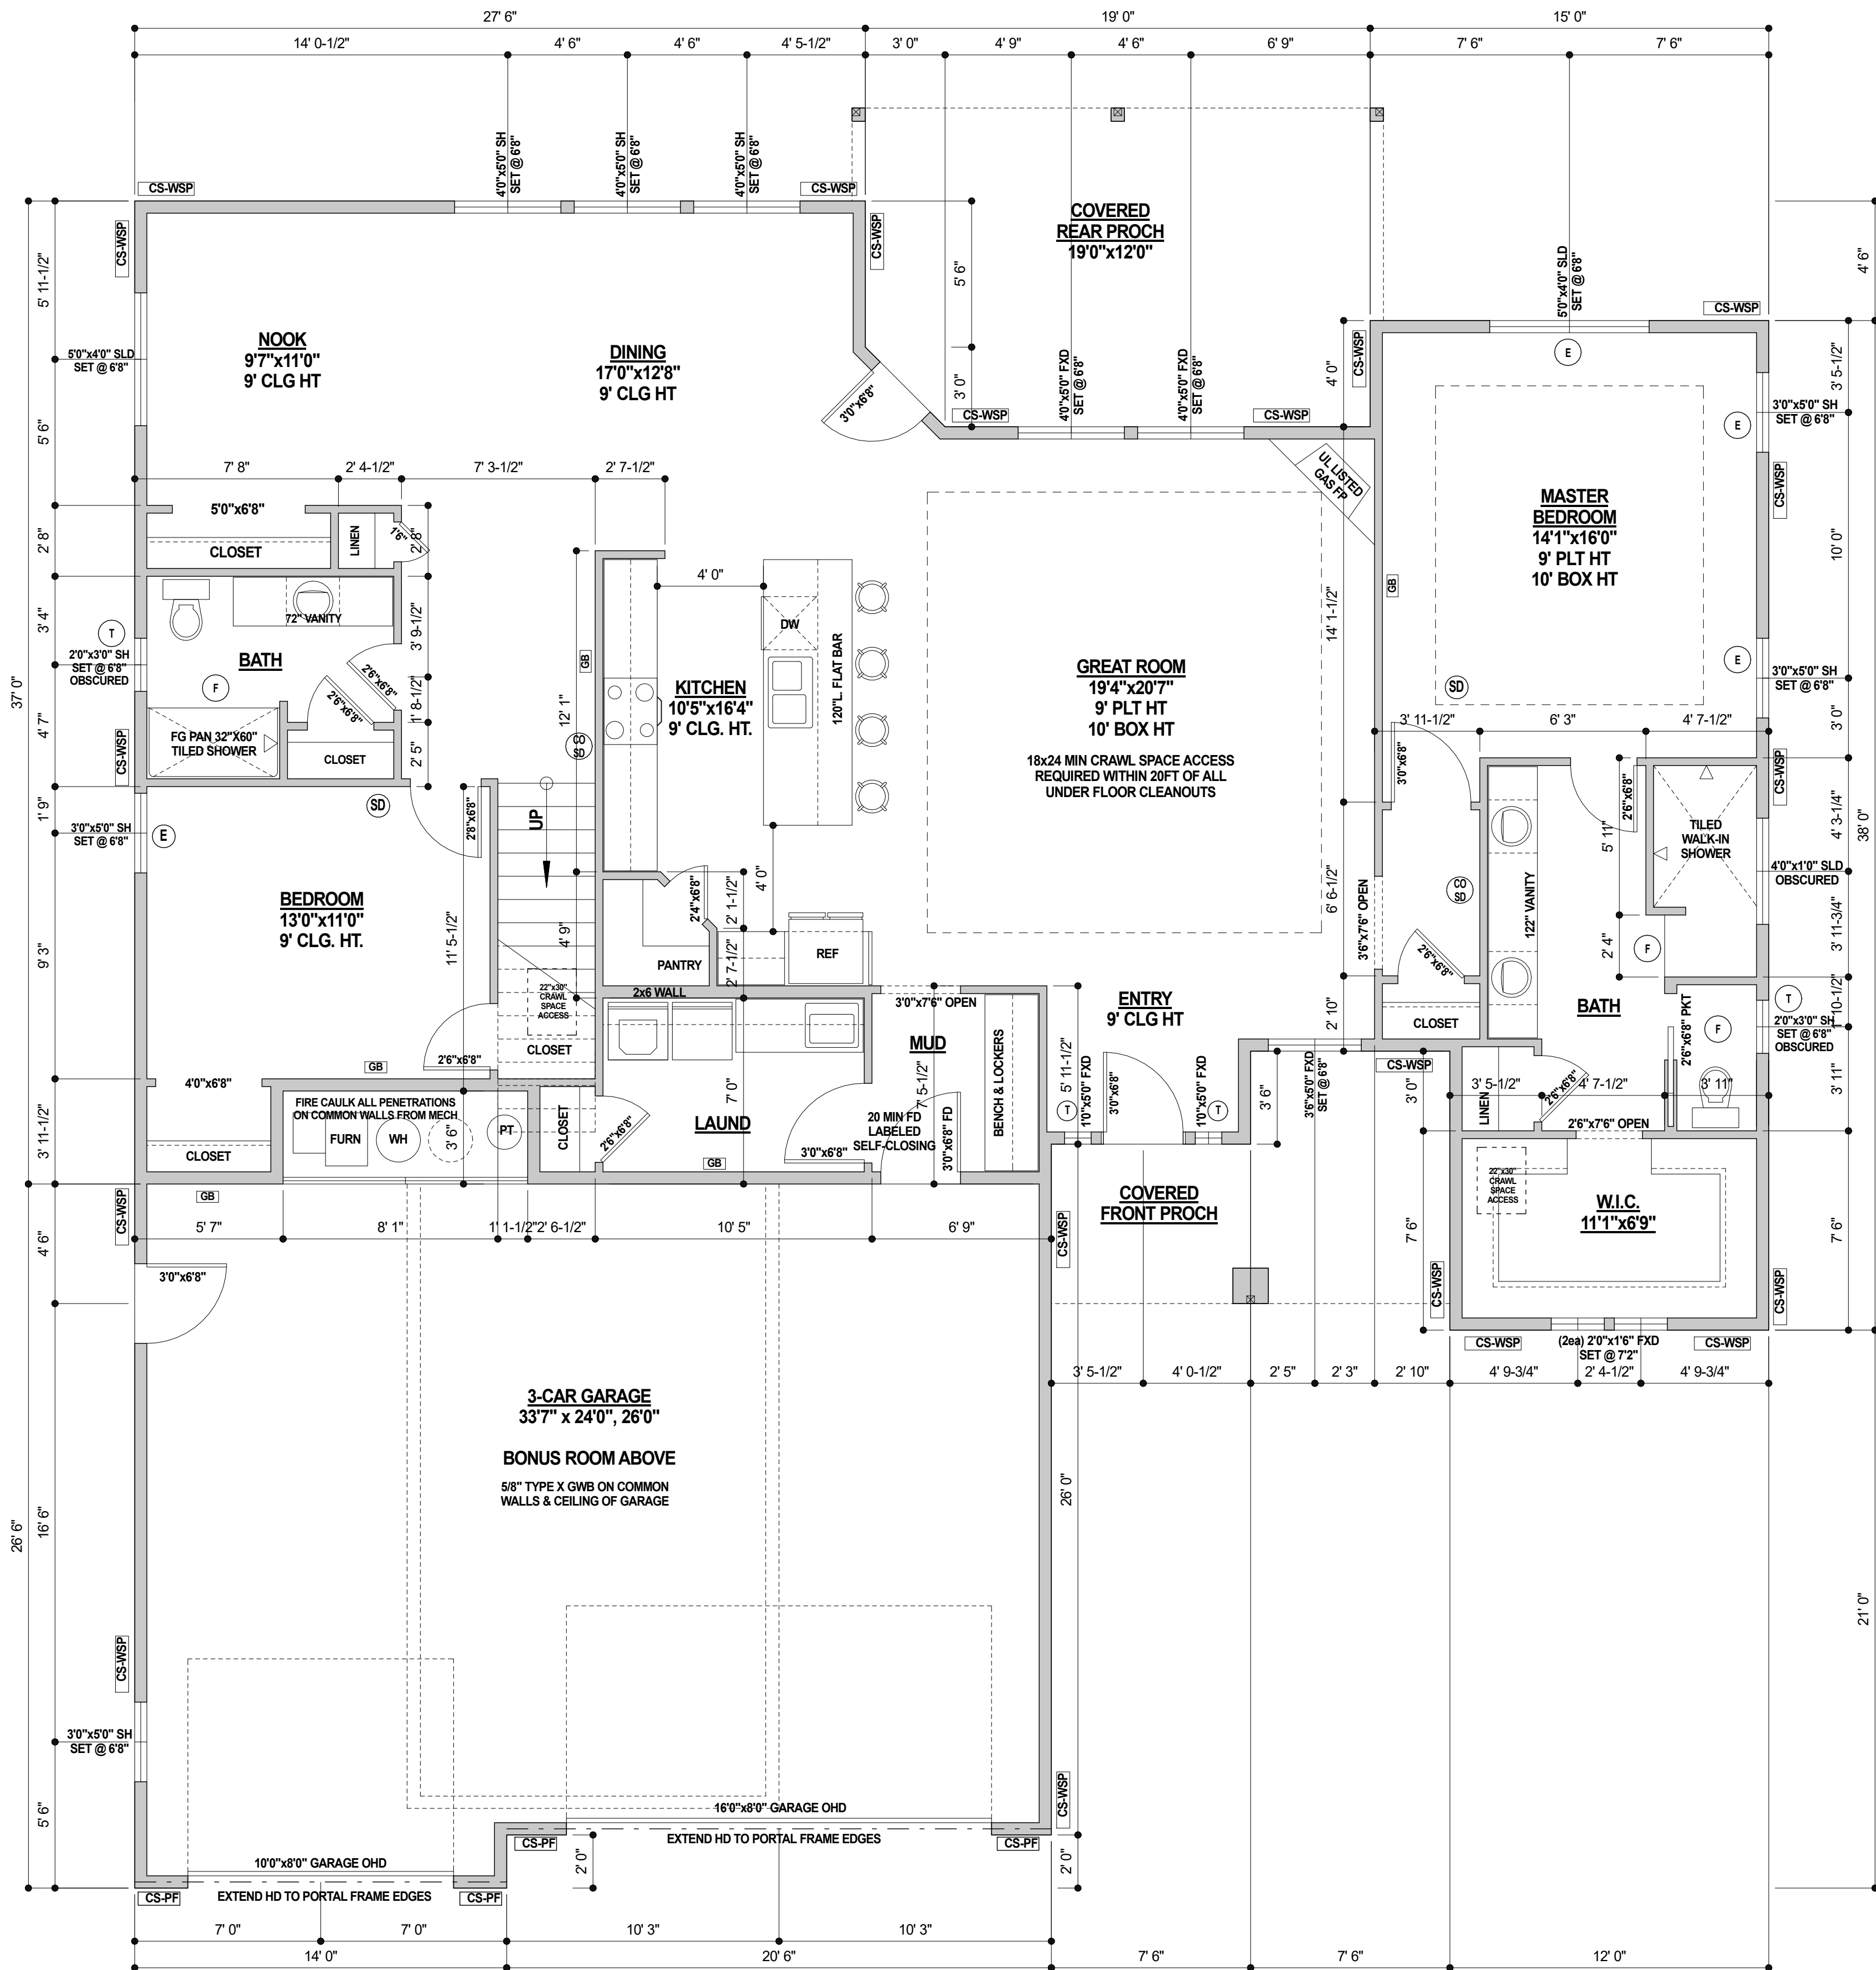

MAIN FLOOR PLAN

SCALE: 1/4"=1'0"

GENERAL NOTES:

MAIN FLOOR = 2036 SF
BONUS ROOM = 306 SF
GARAGE = 906 SF

KEY CODES:

(SD) SMOKE DETECTOR

(F) FAN UNIT

(E) EGRESS

(T) TEMPERED

(CO) CARBON MONOXIDE DETECTOR

FRAMING NOTES:

- SMOKE DETECTORS ARE REQUIRED IN ALL ROOMS USED FOR SLEEPING, AND IN THE IMMEDIATE VICINITY OUTSIDE THE SLEEPING AREA, AND ON EACH LEVEL, HARD WIRED TOGETHER WITH BATTERY BACKUP.
- CARBON MONOXIDE DETECTORS ARE REQUIRED OUTSIDE THE SLEEPING AREAS, AND ON EACH LEVEL, HARD WIRED TOGETHER WITH BATTERY BACKUP.
- ALL BATHROOMS SHALL HAVE A CEILING VENTILATION FAN WITH A MINIMUM CAPACITY OF 50 CFM.
- PROVIDE SEISMIC RESTRAINT STRAPPING FOR ALL WATER HEATERS.
- EGRESS WINDOWS SHALL MEET REQUIREMENTS OF THE IRC 2018 BUILDING CODE.
- VENT DRYER EXHAUST TO DUCT IN WALL AND VENT OUTSIDE.
- KITCHEN LAYOUT AND DESIGN AS PER OWNER.
- ALL ANGLED WALLS ARE 45 DEG. U.N.O.
- INSTALL T.J.'S PER MANUFACTURER'S RECOMMENDATIONS INCLUDING ALL BRIDGING AND BRACING.
- PROVIDE DBL. JOISTS UNDER ALL BEARING WALLS THAT RUN PARALLEL TO FLOOR JOISTS.
- FRAME AROUND STAIRS USING 1.75x11-7/8 LVL.
- ALL BEARING WALL HEADERS SHALL BE (2ea) 2x10 UNLESS NOTED OTHERWISE.
- ALL EXTERIOR WALLS ARE BEARING WALLS.
- JOIST COUNT SHOULD BE DETERMINED FROM JOIST SPACING NOT FROM DRAWING LAYOUT.
- A 20 MINUTE FIRE DOOR IS REQUIRED BETWEEN GARAGE AND LIVING AREA W/ SELF CLOSING HINGE.

WALL BRACING SCHEDULE:
WIND SPEED - 115 MPH GUST VELOCITY
WIND EXPOSURE - "B"
SEISMIC DESIGN CATEGORY - "B"
BWP METHOD - CONTINUOUS

(CS-WSP) DENOTES METHOD CS-WSP (CONTINUOUS WOOD STRUCTURE PANEL SHEATHING) 4x8 WOOD STRUCTURAL PANEL SHEATHING WITH A THICKNESS NOT LESS THAN 3/8 INCH OGB FOR 16-INCH STUD SPACING. NAILING: 6d COMMON @ 8" O.C. ALL EDGES AND 12" O.C. IN FIELD. STAPLE 16ga 1-3/4" @ 3" O.C. ALL EDGES AND 8" O.C. IN FIELD. FASTEN SHEATHING TO HEADER WITH 8d COMMON NAILS IN 3" GRID PATTERN AND 3" O.C. IN ALL FRAMING (STUDS AND SILLS) TYP.


(GB) DENOTES METHOD GB (GYPSUM BOARD PANEL) 4x8 GYPSUM BOARD PANEL WITH A THICKNESS NOT LESS THAN 1/2 INCH FOR 16-INCH STUD SPACING. NAILS AND SCREWS AT 7" O.C. EDGES AND FIELD SPACING AT PANEL EDGES INCLUDING TOP AND BOTTOM PLATES FOR ALL BRACED WALL PANEL LOCATIONS. FOR INTERIOR GYPSUM BOARD NAIL OR SCREW SIZE, SEE IRC TABLE R702.3.5

(CS-PF) DENOTES METHOD CS-PF (CONTINUOUS SHEATHING ADJACENT TO PORTAL OPENING). SEE FIGURE R602.10.6.4 BELOW.

REQUIRED LENGTH OF BRACING FOR CS-WSP, CS-G, CS-PF		STORY LEVEL SUPPORTING					
BASIC SPEED	STORY LEVEL SUPPORTING	10'	20'	30'	40'	50'	60'
LESS THAN 10 MPH	ROOF ONLY	2.0	3.5	4.5	6.0	7.5	9.0
	ROOF + 1 STORY	3.5	6.0	9.0	11.5	14	17

REQUIRED LENGTH OF BRACING FOR (GB) OR MIX OF		STORY LEVEL SUPPORTING					
BASIC SPEED	STORY LEVEL SUPPORTING	10'	20'	30'	40'	50'	60'
LESS THAN 10 MPH	ROOF ONLY	3.5	6.0	9.0	12.0	15.0	18.0
	ROOF + 1 STORY	7.0	12.0	18.0	23.0	28.0	34.0

MINIMUM LENGTH OF BRACED WALL PANELS		METHOD				
MINIMUM LENGTH OF BRACED WALL PANELS	METHOD	6 FEET	8 FEET	10 FEET	12 FEET	12 FEET
		CS-G	CS-G	CS-G	CS-G	CS-G
2" x 4" Stud	CS-WSP	16'	18'	20'	22'	24'
	CS-PF	16'	18'	20'	22'	24'
	CS-G	16'	18'	20'	22'	24'
	CS-PF	16'	18'	20'	22'	24'
2" x 6" Stud	CS-WSP	16'	18'	20'	22'	24'
	CS-PF	16'	18'	20'	22'	24'
	CS-G	16'	18'	20'	22'	24'
	CS-PF	16'	18'	20'	22'	24'

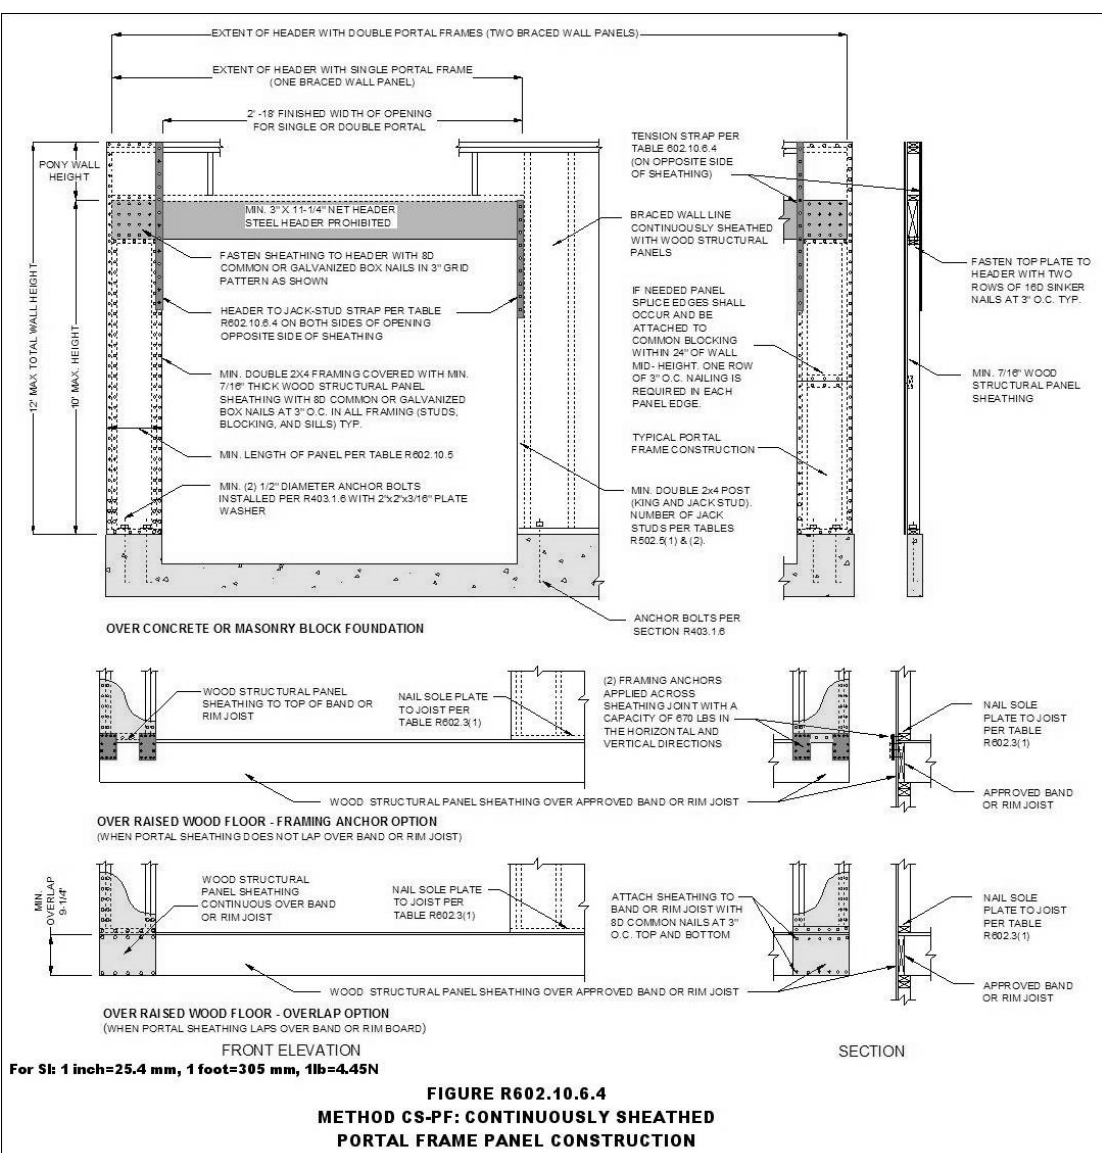

Plans and Rendering by Owens Design

DISCLAIMER NOTE: While every attempt has been made in preparation of these plans, the designer assumes no responsibility for errors or omissions. The contractor is responsible for verifying all dimensions, materials, and specifications with the owner and the building department. The contractor is also responsible for obtaining all necessary permits and licenses. The contractor is responsible for the construction of the building and for the safety of the building. 

OWENS DESIGN

Twin Falls, ID 83301 ph. 208-731-4372
Email: Lanoewdesign@gmail.com

SCALE: 1/4" = 1'-0"

DRAWN BY: Lane Owens

DATE DRAWN: 04-JAN-22

LAST REVISED: 00-00-00

PROJECT NAME: Lance LeBaron Homes


SHEET: KRAUSE RESIDENCE

PLAN NAME: MAIN FLOOR PLAN

LOT-2, BLK-1, TRIPLE CROWN #2



ALLIE LANE, FILER, IDAHO

3 OF 5

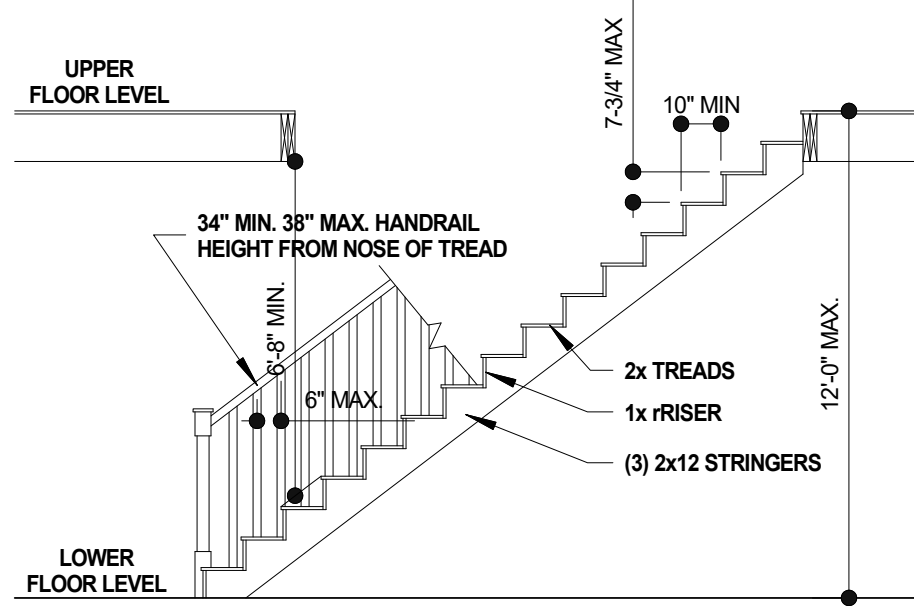

INTERNATIONAL RESIDENTIAL
BUILDING CODE SECTION R311.5 FOR STAIRWAYS

FRAME AROUND STAIRS USING 1.75x11-7/8 LVL.

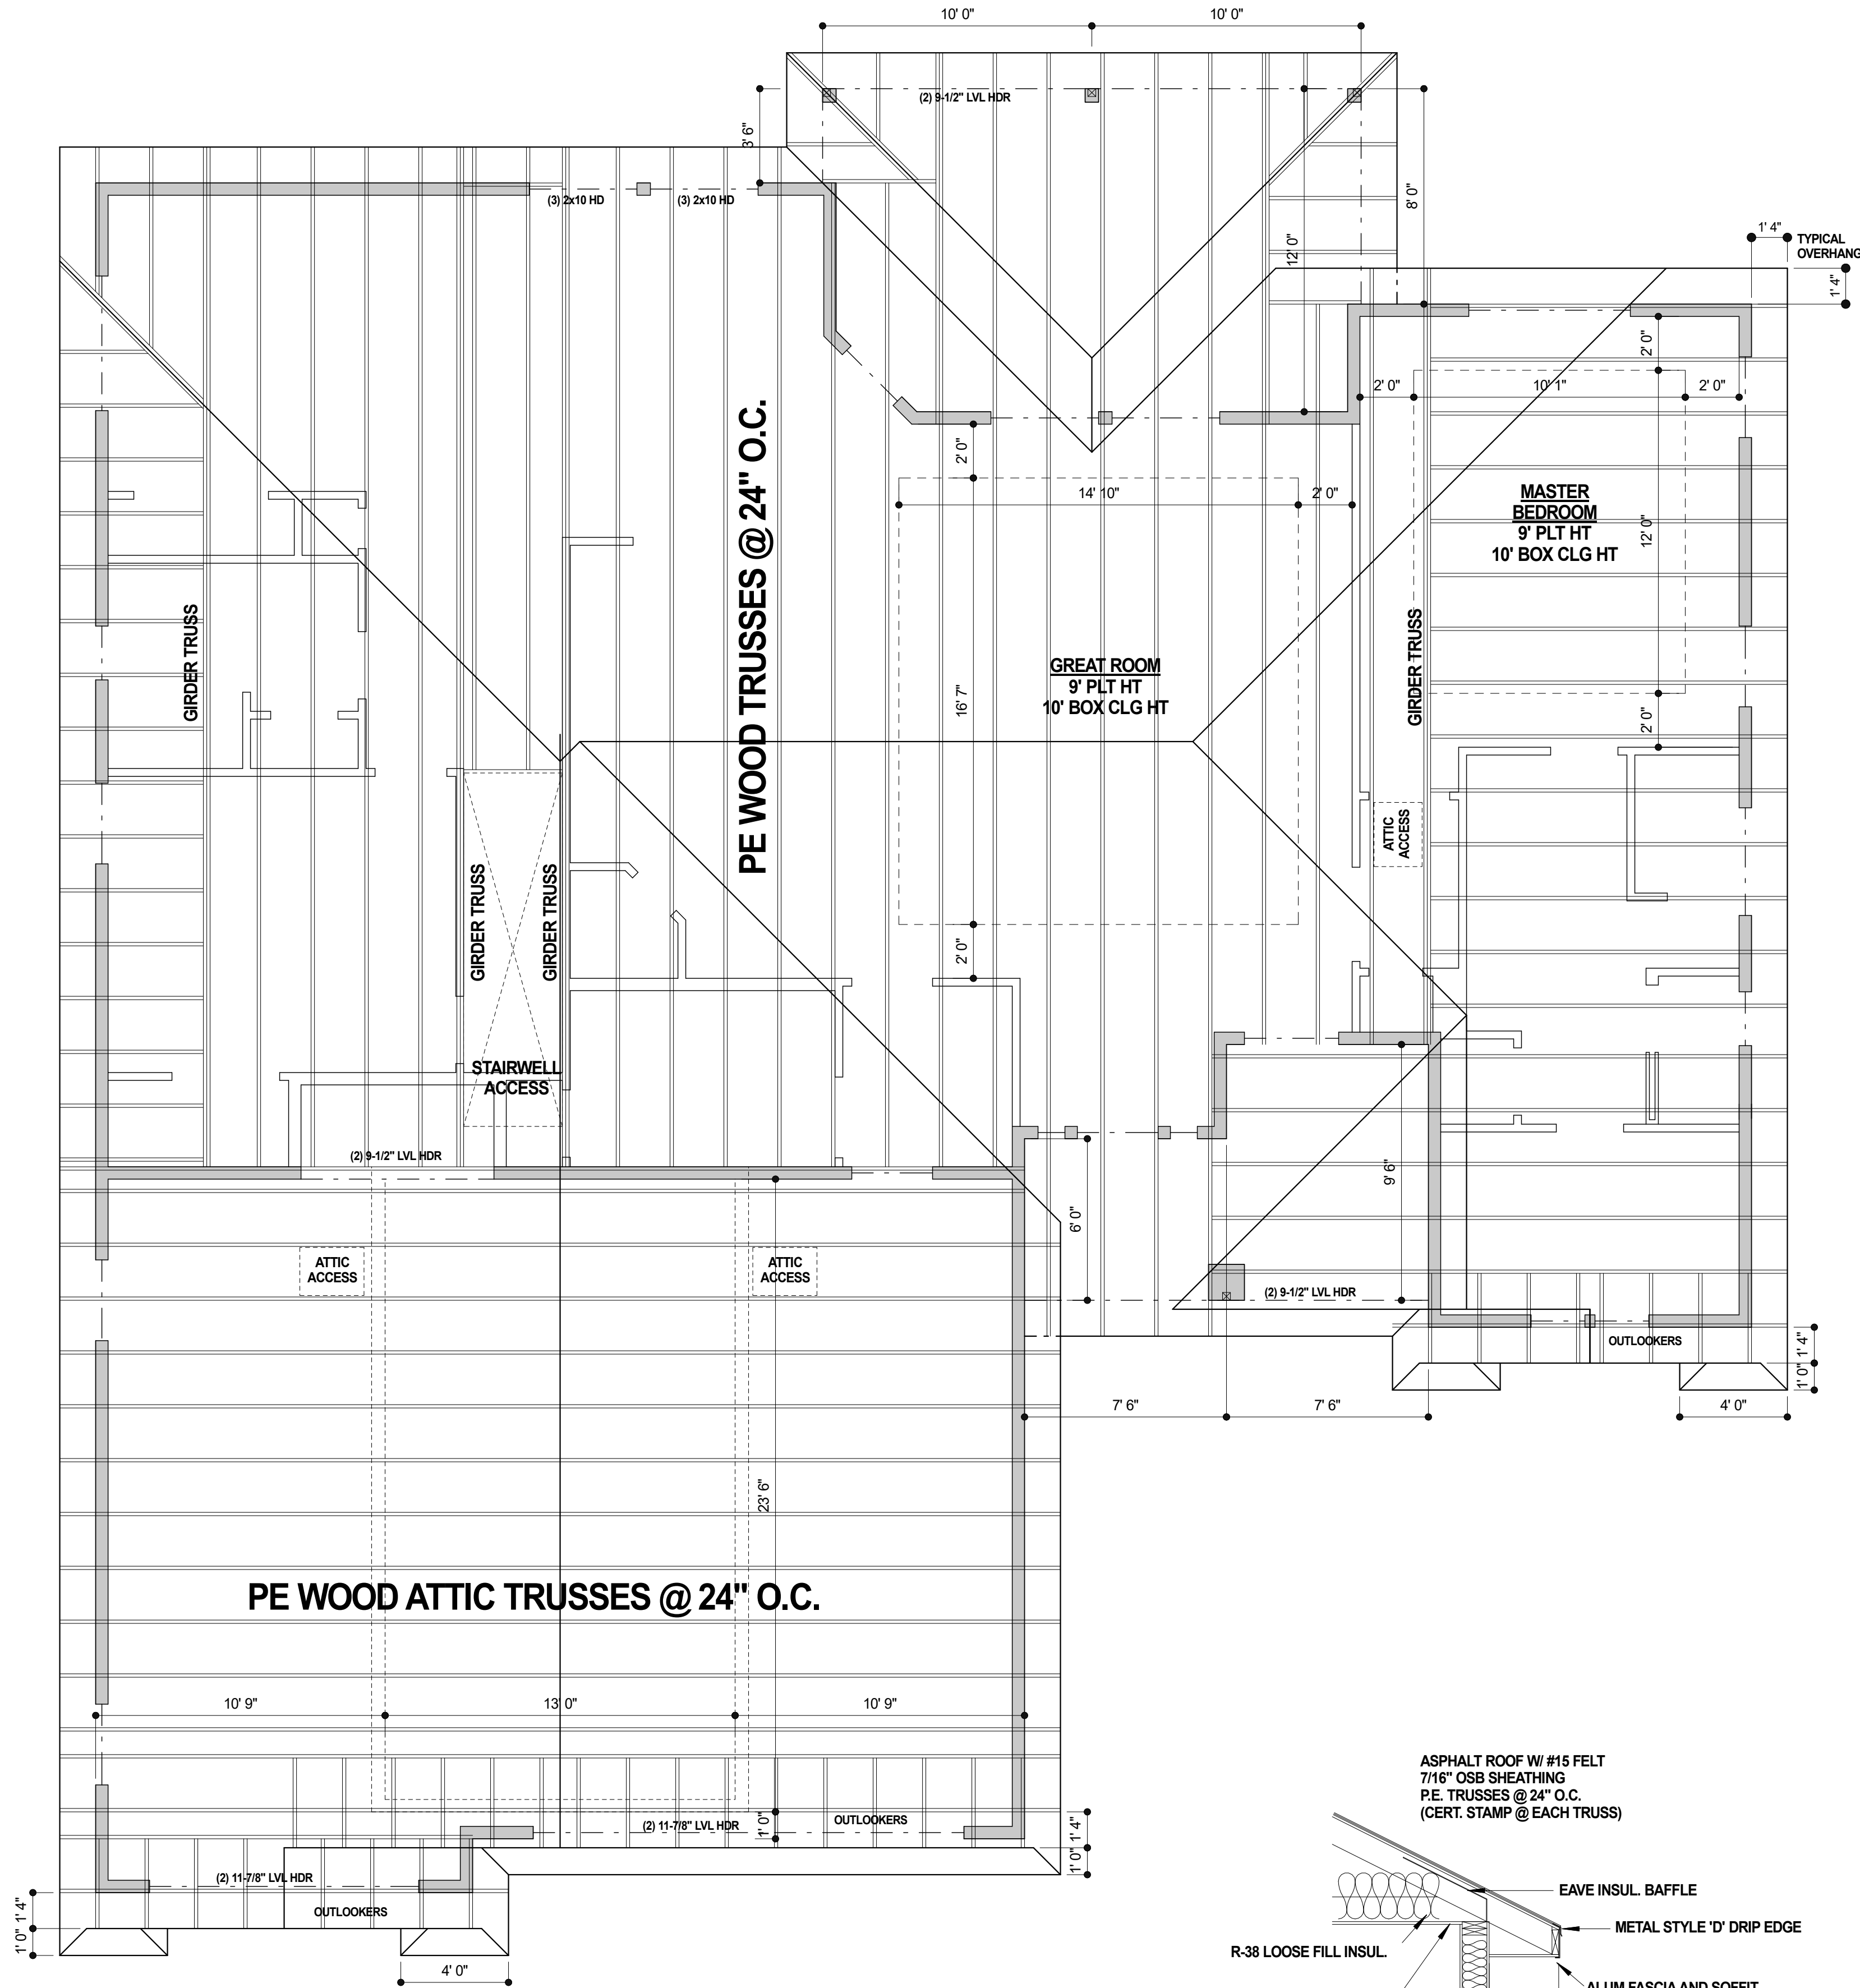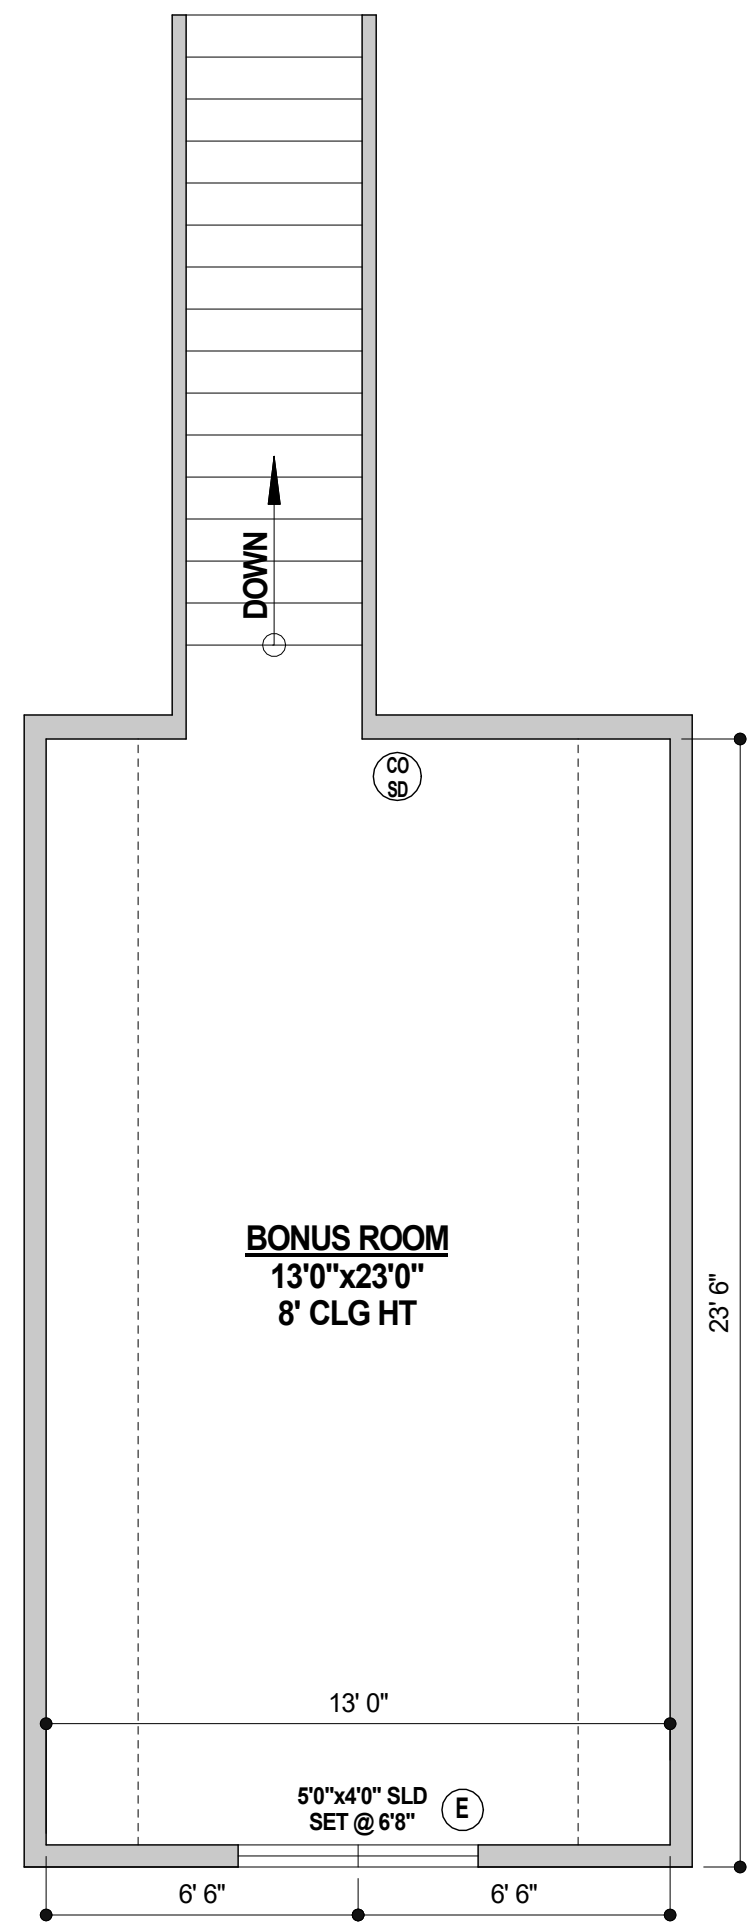


ROOF PLAN

SCALE: 1/4"=1'0"

ROOF NOTES:

1. INSTALL TRUSSES PER MANUFACTURER'S RECOMMENDATIONS INCLUDING ALL BRIDGING AND BRACING.
2. PROVIDE SIMPSON H1 OR EQUAL AT BRG. ENDS OF EACH TRUSS.
3. BEARING WALL HEADERS SHALL BE (2ea) DF 2x10 UNLESS NOTED OTHERWISE.
4. ALL ROOF OVERHANGS SHALL BE AS NOTED.
5. ROOF SHEATHING SHALL BE 7/16" OSB W/ PLY CLIPS
6. ALL SHADED AREAS REPRESENT LOAD BEARING POINTS FOR TRUSSES.
7. ROOF VENTILATION REQUIREMENTS PER IRC R806.1

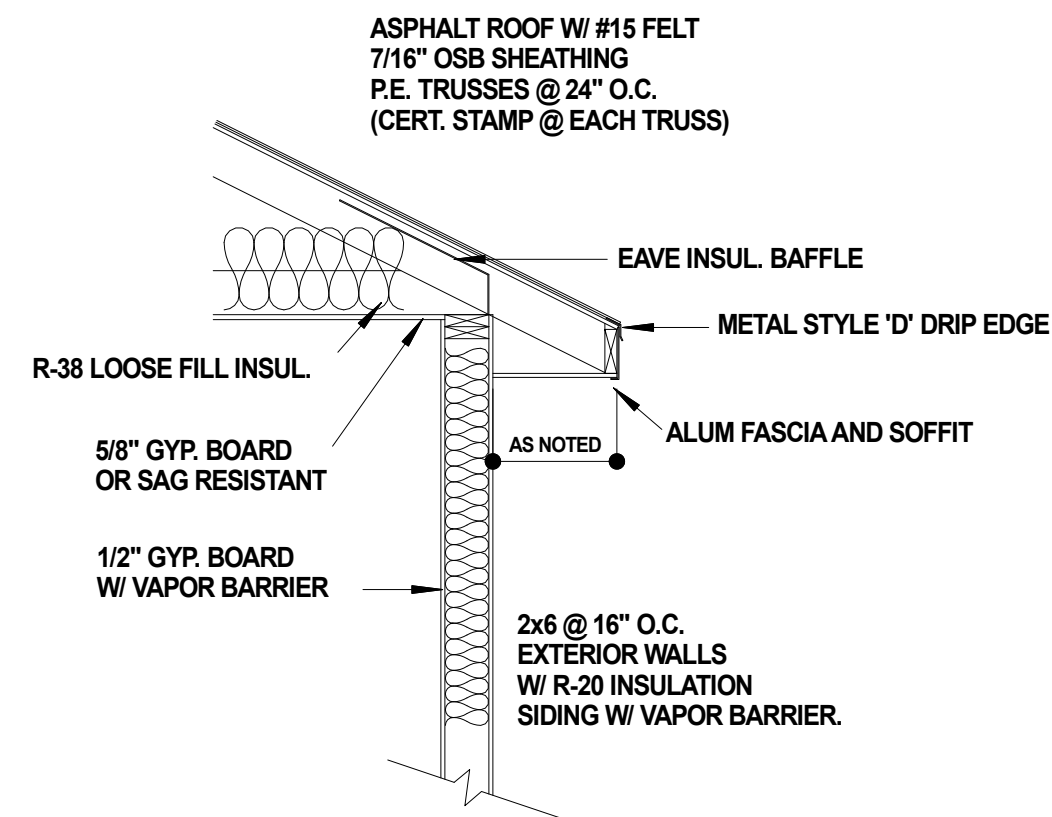

TYP. EAVE DETAIL

SCALE: 1/2" = 1'0"

Plans and Rendering by Owens Design.

DISCLAIMER NOTE: While every attempt has been made in preparation of these plans to ensure accuracy, the designer assumes no responsibility for errors or omissions. The contractor is responsible for the final construction of the building and must comply with all applicable building codes and regulations. The designer is not responsible for the final construction of the building and must comply with all applicable building codes and regulations. The designer is not responsible for the final construction of the building and must comply with all applicable building codes and regulations.



SCALE: 1/4" = 1'-0"
DRAWN BY: Lane Owens
DATE DRAWN: 04-JAN-22
LAST REVISED: 00-00-00

PROJECT NAME:
Lance LeBaron Homes
KRAUSE RESIDENCE
LOT-2, BLK-1, TRIPLE CROWN #2
ALLIE LANE, FILER, IDAHO

SHEET:

A4

PLAN NAME: ROOF PLAN
4 OF 5



Plans and Rendering by Owens Design.



**OWENS
DESIGN**

Twin Falls, ID 83301 ph. 208-731-8737
Email: Laneowensdesign@gmail.com

SCALE:	1/4" = 1'-0"
DRAWN BY:	Lane Owens
DATE DRAWN:	04-JAN-22
LAST REVISED:	00-00-00

CT NAME: Lance LeBaron Homes
KRAUSE RESIDENCE
LOT-2, BLK-1, TRIPLE CROWN #2
ALLIE LANE, FILER, IDAHO

PROJECT NAME:

SHEET

A5

PLAN NAME: ELEVATIONS