

Lance LeBaron Homes

MARTINEZ RESIDENCE
GOVT., LOT-6, SECTION-7, T.10 S., R.20 E., B.M.
JEROME COUNTY, IDAHO
LOT SIZE: 1.0 ACRES
CODE COMPLIANCE: 2018 IRC
NEW CONSTRUCTION
SINGLE FAMILY RESIDENCE
MAIN LEVEL = 1378 SF
ATTACHED GARAGE = 536 SF
COVERED PATIO AREAS = 252 SF
FIRE ENVELOPE = 26,882 CF

ENERGY CODE COMPLIANCE:
Prescriptive Energy Code
R-38 Attic
R-20 Exterior Walls (Including between garage)
R-30 Floors
.35 U Value Lo-E Windows

SHEET SCHEDULE:
A1 - COVER SHEET, SITE PLAN
A2 - FOUNDATION PLAN AND DETAILS
A3 - MAIN FLOOR PLAN
A4 - ROOF PLAN & ELEVATIONS

SITE PLAN

SCALE: 1/16" = 1'0"

GENERAL NOTES

ALL WORK PERFORMED SHALL MEET CURRENT ADOPTED CODES. (IN CASE OF CONFLICTING NOTES, THE MORE STRINGENT REQUIREMENT SHALL SUPPLY).


VERIFY ALL UTILITIES BEFORE DIGGING.

PROPERTY LINES ARE CONTRACT LIMITS.

SITE AND STRUCTURE SHALL BE KEPT CLEAN. SUBCONTRACTOR TO VERIFY ALL DIMENSION. IN CASE OF ERRORS OR DISCREPANCIES CONTACT OWNER OR OWNER'S REPRESENTATIVE, BEFORE PROCEEDING. DO NOT SCALE.

DO NOT DRAIN STORM WATER ONTO ADJACENT LOTS.

STRING LINES SHALL BE PROVIDED OVER PROPERTY PINS AT TIME OF INSPECTIONS.

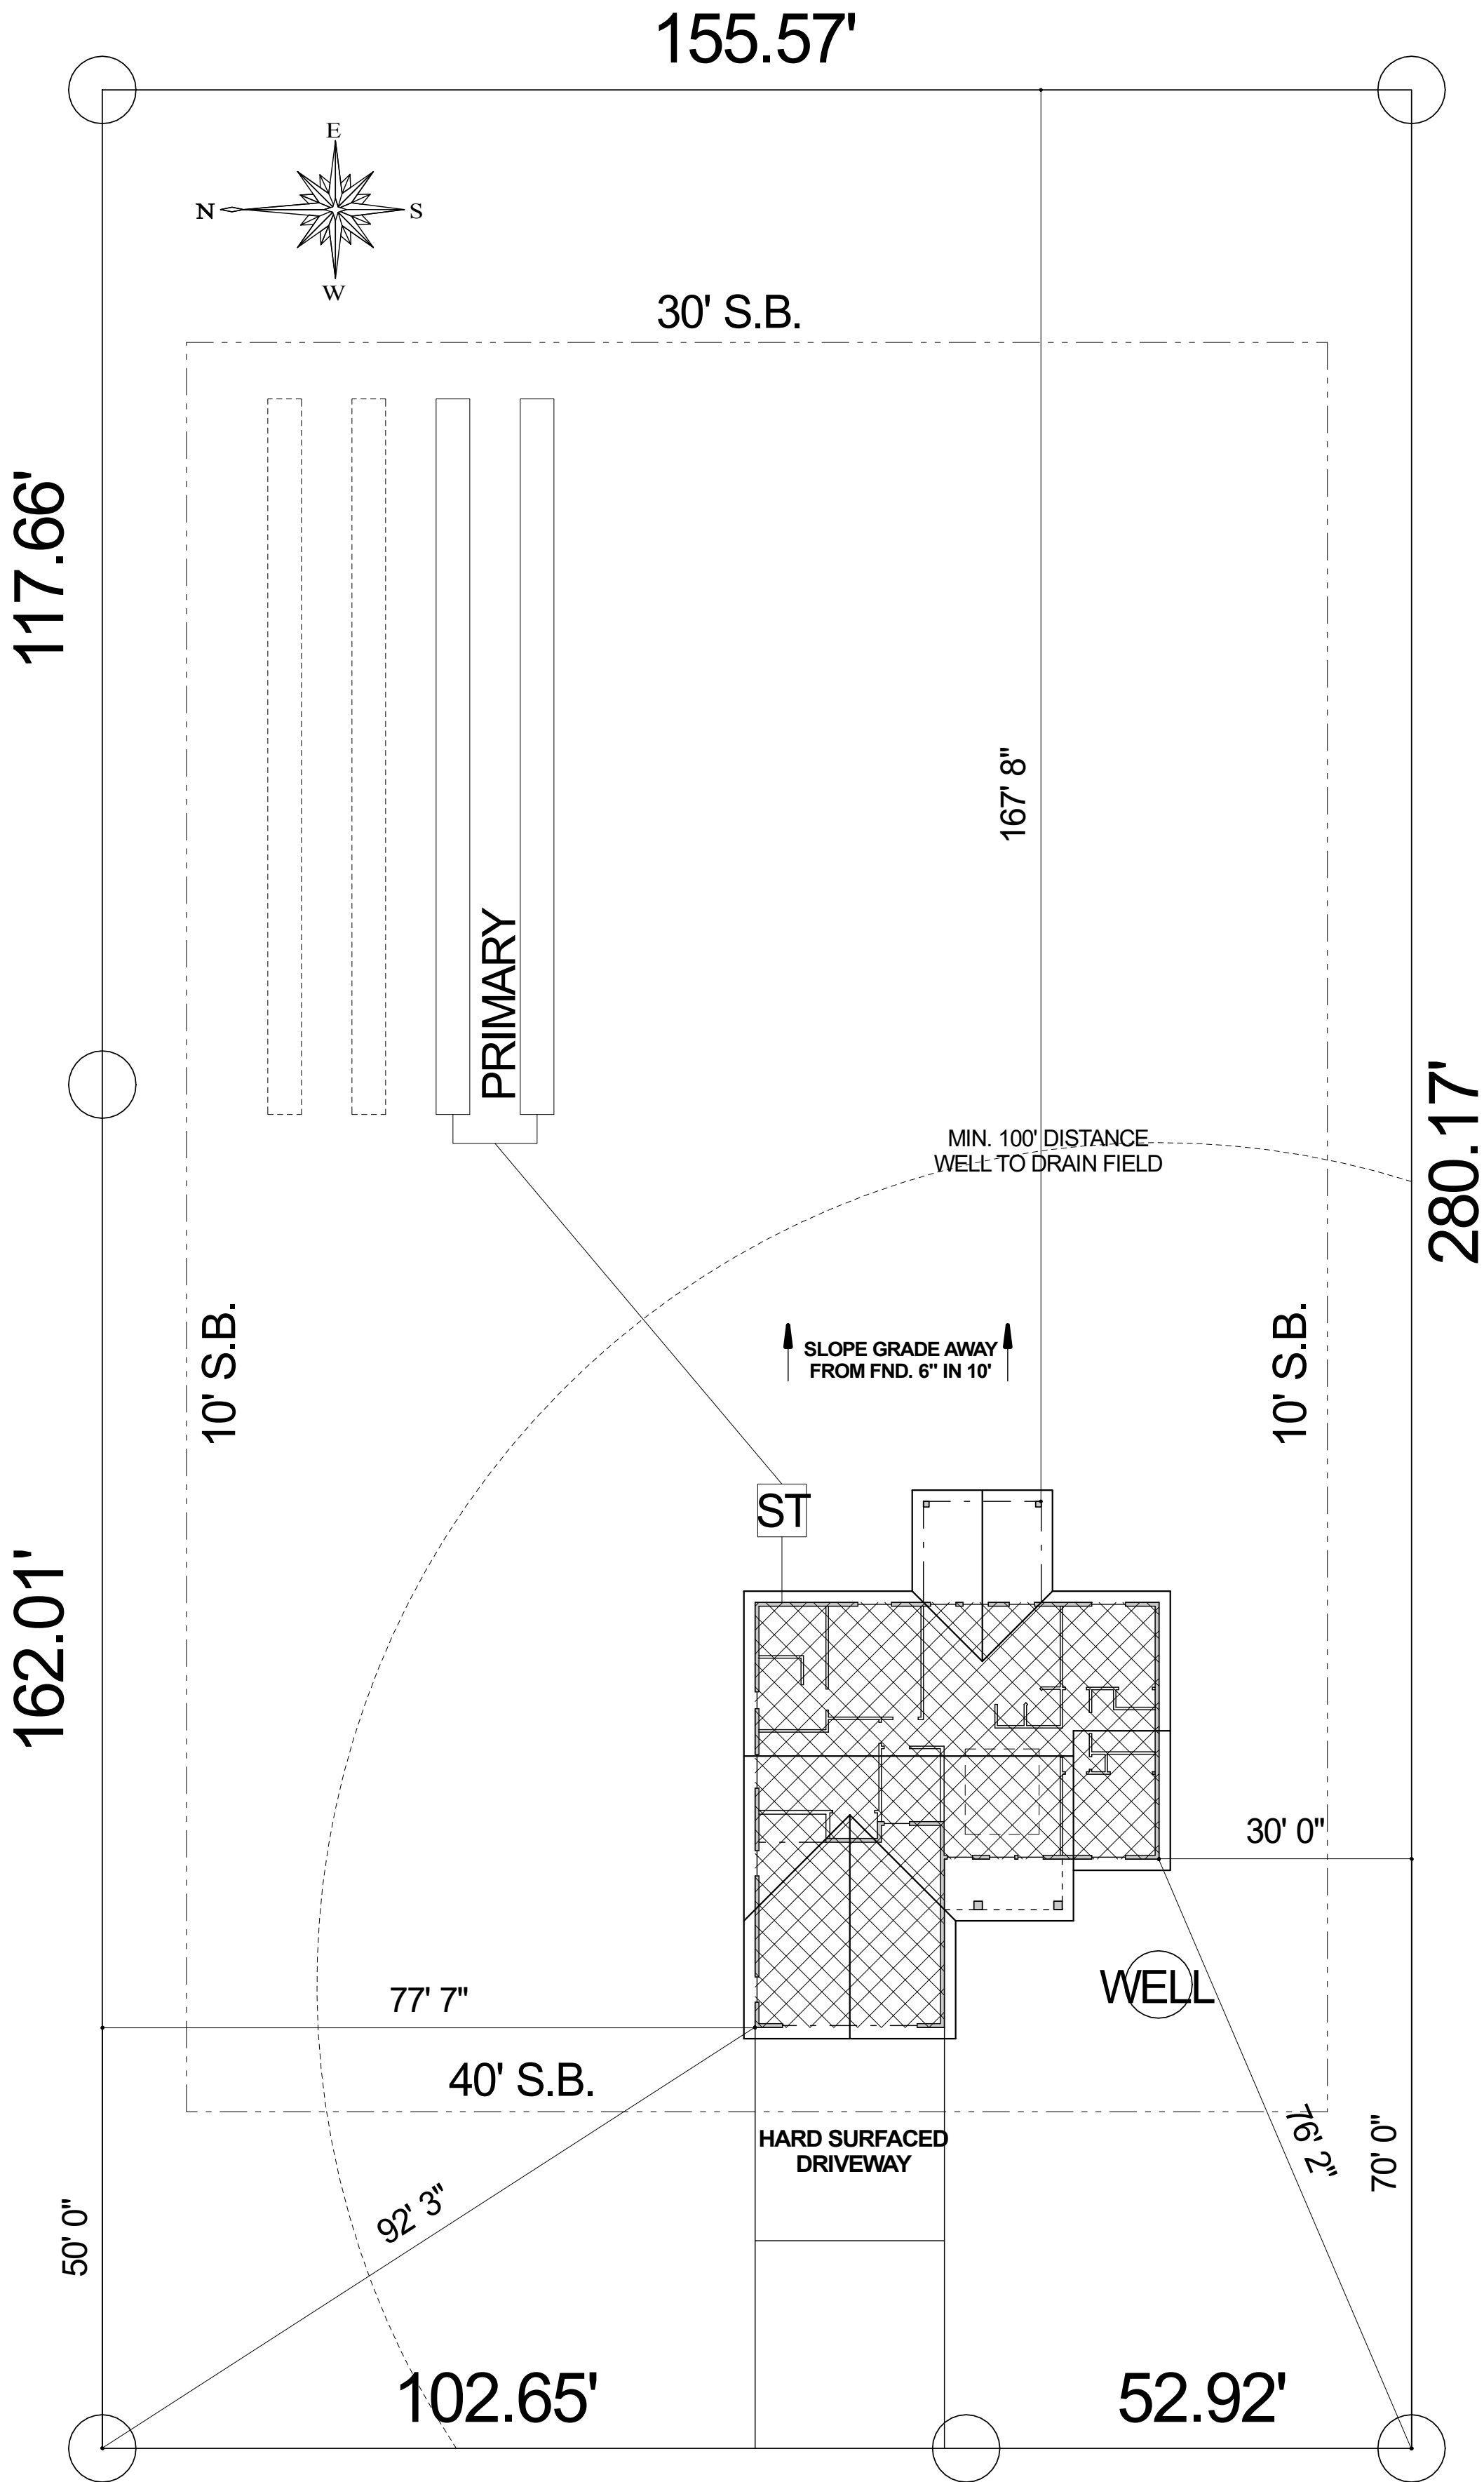

Plans and Rendering by Owens Design.

OWENS
DESIGN

Twin Falls, ID 83301 ph. 208-731-4377
Email: Lanoowensdesign@gmail.com

SCALE:
1/16" = 1'0"

DRAWN BY:
Lane Owens

DATE DRAWN:
07-JAN-22

LAST REVISED:
00-00-00

PROJECT NAME:
Lance LeBaron Homes
MARTINEZ RESIDENCE
GOVT., LOT-6, SECTION-7, T.10 S., R.20 E., B.M.
JEROME COUNTY, IDAHO

SHEET:
A1

PLAN NAME:
SITE PLAN

1 OF 4

DISCLAIMER NOTE: While every attempt has been made in preparation of these plans to ensure accuracy, the designer does not warrant or represent that the plans are free from errors or omissions. The designer shall not be responsible for any errors or omissions that may appear on the plans. The contractor is responsible for the verification of the accuracy of the information shown on the plans and for the proper interpretation of the specifications for the building, and shall take preference over anything shown, described, or implied herein same as it varies.

1. BOTTOM OF FOOTING AND FOUNDATION SHALL BE BELOW LOCAL FROST LINE.
2. CONTRACTOR SHALL VERIFY ALL WINDOW AND DOOR ROUGH OPENING SIZES BEFORE FORMING BLOCK OUTS AS NECESSARY.
3. PROVIDE EXPANSION JOINTS IN ALL FLATWORK AS NECESSARY.
4. ALL FOUNDATION WALLS SHALL BE MIN. 3,000#/SQ IN. COMPRESSIVE STRENGTH @ 28 DAYS.
ALL PORCHES, PARKING SLABS, STEPS AND GARAGE FLOOR SLABS SHALL BE MIN. 3,500#/SQ IN. COMPRESSIVE STRENGTH @ 28 DAYS.
5. DESIGNER ASSUMES NO RESPONSIBILITY FOR STRUCTURAL INTEGRITY. VERIFY ALL STRUCTURAL SPECIFICATIONS W/ MFG., TRUSS VENDOR OR ENGINEER.
6. SEE BRACING WALL PANEL FOR HOLD DOWN LOCATIONS AND DESCRIPTIONS.

1. INSTALL T.J.I'S PER MANUFACTURER'S RECOMMENDATIONS INCLUDING ALL BRIDGING AND BRACING.
2. PROVIDE DBL JOISTS UNDER ALL BEARING WALLS THAT RUN PARALLEL TO FLOOR JOISTS.
3. FRAME AROUND STAIRS USING 1.75x11-7/8 LVL.
4. ALL BEARING WALL HEADERS SHALL BE (2ea) 4F 2x10 UNLESS NOTED OTHERWISE.
5. ALL EXTERIOR WALLS ARE BEARING WALLS.
6. JOIST COUNT SHOULD BE DETERMINED FROM JOIST SPACING NOT FROM DRAWING LAYOUT.

[illegible]


SCALE:	1/4" = 1'-0"
DRAWN BY:	Lane Owens
DATE DRAWN:	07-JAN-22
LAST REVISED:	00-00-00

NAME: Lance LeBaron Homes
MARTINEZ RESIDENCE
GOVT., LOT-6, SECTION-7, T.10 S., R.20 E., B.M.
JEROME COUNTY, IDAHO

PROJECT NAME:

SHEE

PLAN NAME:
FOUNDATION PLAN

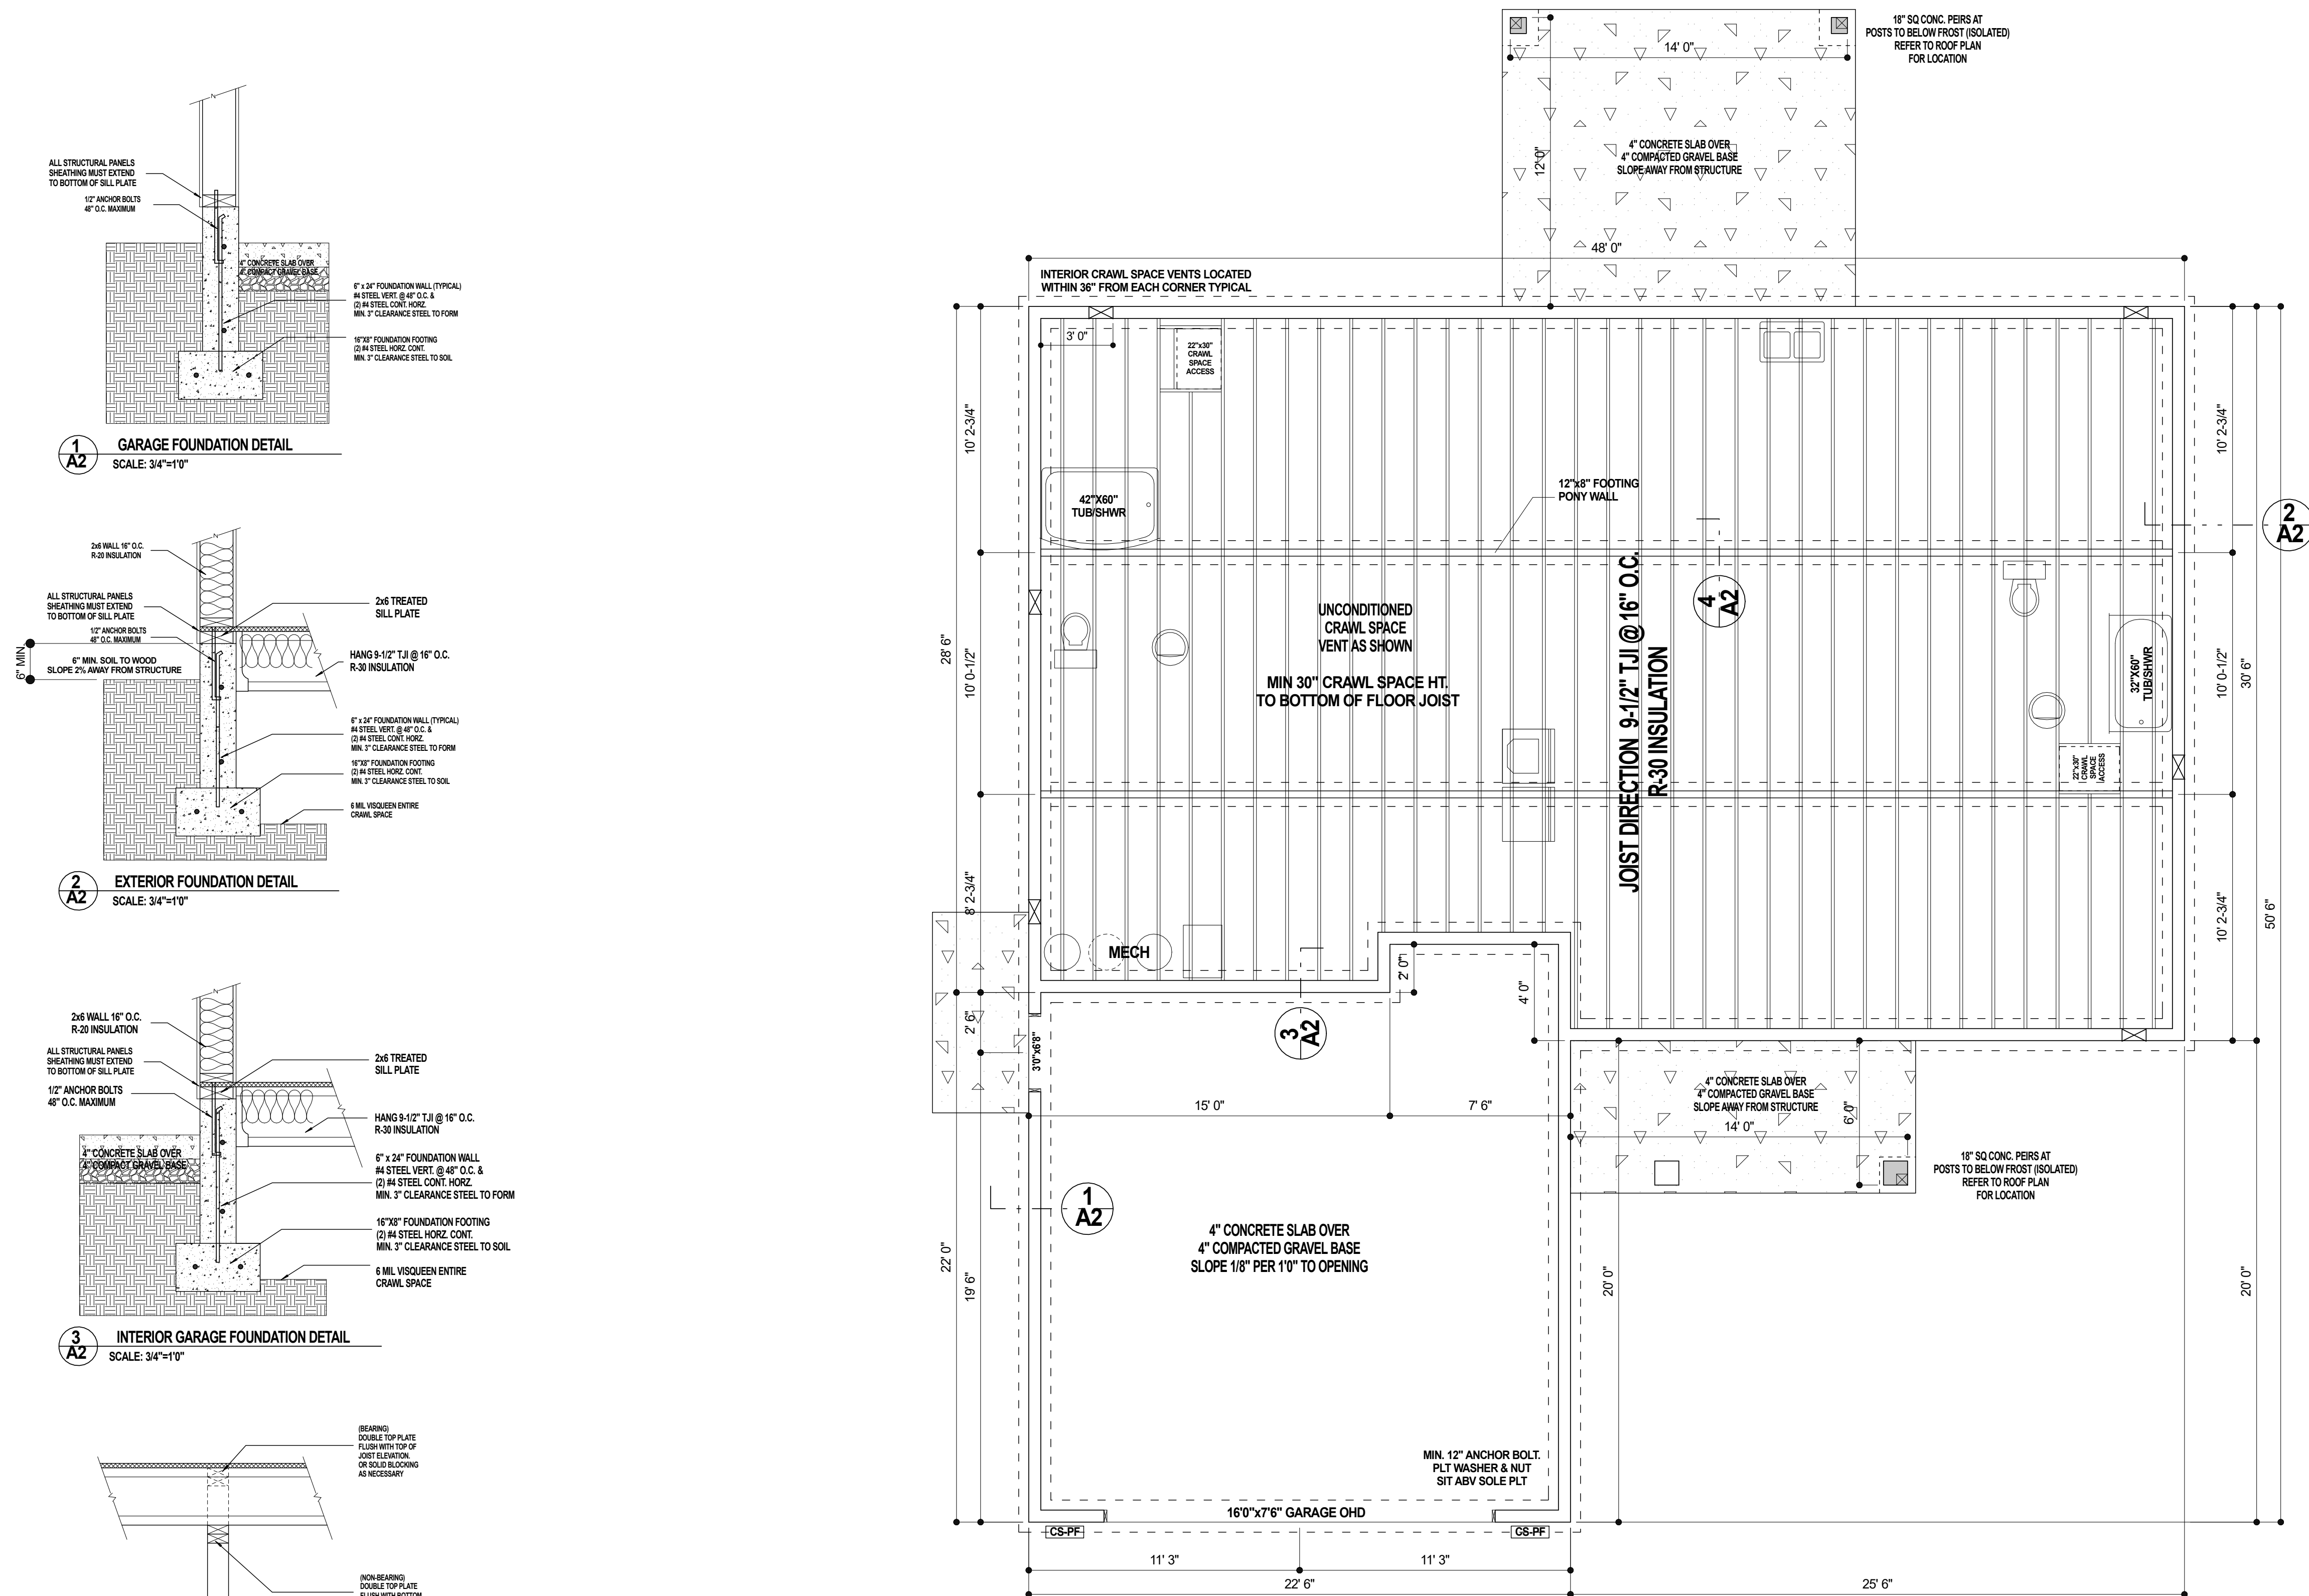

SCALE: 1/4"=1'0"

1
A2 **GARAGE FOUNDATION DETAIL**
SCALE: 3/4"=1'0"

2
A2 EXTERIOR FOUNDATION DETAIL
SCALE: 3/4"=1'0"

3
A2 INTERIOR GARAGE FOUNDATION DETAIL
SCALE: 3/4"=1'0"

4
A2 INTERIOR FOOTING DETAIL
SCALE: 3/4"=1'-0"

1. SMOKE DETECTORS ARE REQUIRED IN ALL ROOMS USED FOR SLEEPING, AND IN THE IMMEDIATE VICINITY OUTSIDE THE SLEEPING AREA, AND ON EACH LEVEL, HARD WIRED TOGETHER WITH BATTERY BACKUP.
2. CARBON MONOXIDE DETECTORS ARE REQUIRED OUTSIDE THE SLEEPING AREAS, AND ON EACH LEVEL, HARD WIRED TOGETHER WITH BATTERY BACKUP.
3. ALL BATHROOMS SHALL HAVE A CEILING VENTILATION FAN WITH A MINIMUM CAPACITY OF 50 CFM.
4. PROVIDE SEISMIC RESTRAINT STRAPPING FOR ALL WATER HEATERS.
5. EGRESS WINDOWS SHALL MEET REQUIREMENTS OF THE IRC 2018 BUILDING CODE.
6. VENT DRYER EXHAUST TO DUCT IN WALL AND VENT OUTSIDE.
7. KITCHEN ALLYARD AND DESIGN AS PER OWNER.
8. ALL ANGLED WALLS ARE 45 DEG. U.N.O.
9. INSTALL T.J.'S PER MANUFACTURER'S RECOMMENDATIONS INCLUDING ALL BRIDGING AND BRACING.
10. PROVIDE DBL. JOISTS UNDER ALL BEARING WALLS THAT RUN PARALLEL TO FLOOR JOISTS.
11. FRAME AROUND STAIRS USING 1.75x11-7/8 LVL.
12. ALL BEARING WALL HEADERS SHALL BE (2ea) DF 2x10 UNLESS NOTED OTHERWISE.
13. ALL EXTERIOR WALLS ARE BEARING WALLS.
14. JOIST COUNT SHOULD BE DETERMINED FROM JOIST SPACING NOT FROM DRAWING LAYOUT.
15. A 20 MINUTE FIRE DOOR IS REQUIRED BETWEEN GARAGE AND LIVING AREA W/ SELF CLOSING HINGE.


CS-WSP DENOTES METHOD CS-WSP (CONTINUOUS WOOD STRUCTURE PANEL SHEATHING), 4x8 WOOD STRUCTURAL PANEL SHEATHING WITH A THICKNESS NOT LESS THAN 3/8 INCH OSB FOR 16-INCH STUD SPACING, NAILING: 6d COMMON @ 6" O.C. ALL EDGES AND 12" O.C. IN FIELD, STAPLE: 16ga 1-3/4" 3" O.C. ALL EDGES AND 6" O.C. IN FIELD. FASTEN SHEATHING TO HEADER WITH 8d COMMON NAILS IN 3" GRID PATTERN AND 3" O.C. IN ALL FRAMING (STUDS AND SILLS) TYP.

CS-PF DENOTES METHOD CS-PF (CONTINUOUS SHEATHING
ADJACENT TO PORTAL OPENING).
SEE FIGURE R602.10.6.4 BELOW

BASIC WIND SPEED	STORY LEVEL SUPPORTING:	LENGTH OF PERPENDICULAR SIDE:					
		10'	20'	30'	40'	50'	60'
LESS THAN 110 MPH	ROOF ONLY	3.5'	6.5'	9.5'	12.5'	15.0'	18.0'
	ROOF + 1 STORY	7.0'	12.5'	18.0'	23.5'	29.0'	34.5'


[illegible]

MINIMUM LENGTH OF BRACED WALL PANELS						
METHOD	MINIMUM LENGTH FOR WALL HTS					
	6 FEET	9 FEET	10 FEET	11 FEET	12 FEET	
CS-G	24"	27"	30"	33"	36"	
CS-PP	16"	18"	20"	22"	24"	
CS-SPF						
ADVANTAGE CLEAR OPENING HT	64"	24"	27"	30"	33"	36"
	68"	26"	27"	30"	33"	36"
	72"	27"	27"	30"	33"	36"
	76"	30"	29"	30"	33"	36"
	80"	32"	30"	30"	33"	36"
	84"	34"	31"	30"	33"	36"
	88"	35"	33"	33"	33"	36"
	92"	38"	35"	33"	33"	36"
	96"	40"	41"	36"	36"	36"
	100"	-	44"	40"	38"	38"
	104"	-	49"	43"	40"	38"
	108"	-	54"	47"	43"	41"
112"	-	-	50"	45"	43"	
116"	-	-	55"	48"	45"	
120"	-	-	60"	52"	48"	

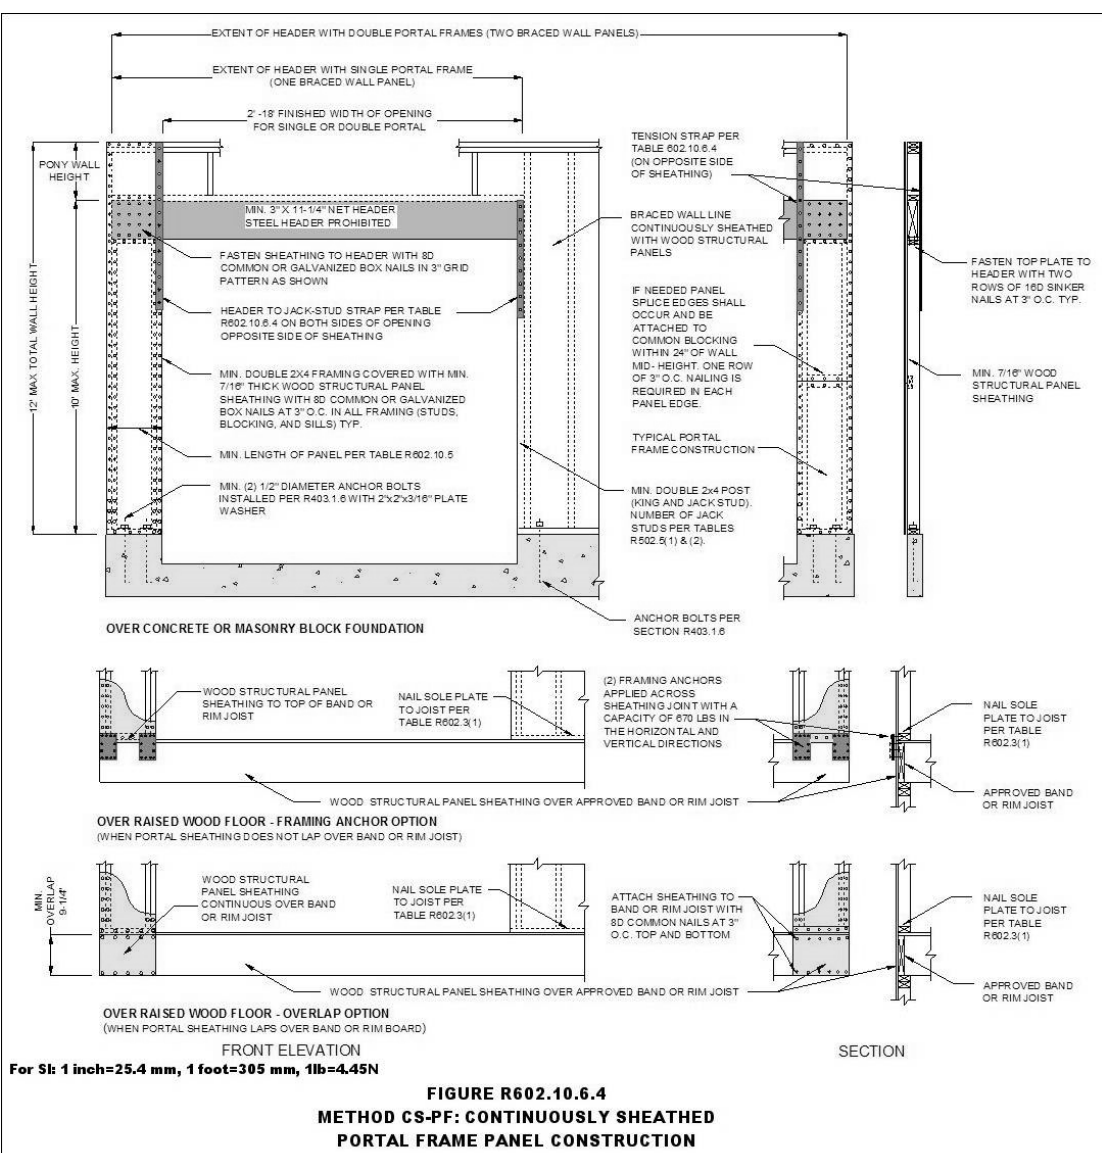

Plans and Rendering by Owens Design.

DISCLAIMER NOTE: While every attempt has been made in preparation of these plans to avoid mistakes, Owens Design cannot guarantee against human error or other variations from standard construction practices and techniques. Consequently, the homeowner and the contractors on the job site must check all dimensions, details, and applicable building codes for compliance and acceptability. Therefore all written dimensions rule over scale of the plan. Contractor is responsible for final verification of structural integrity and material list quantities (All Federal, State, and Local codes, Ordinances, Regulations Etc. shall be considered as part of the specifications for this bidding, and shall take preference over anything shown.

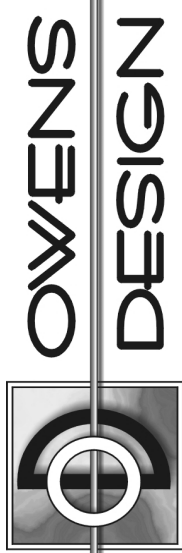

Twin Falls, ID 83301 ph. 208-731-8737
Email: Laneowensdesign@gmail.com

SCALE:

1/4" = 1'-0"

DRAWN BY:
Lane Owens

07-JAN-22

00-00-00

SCALE: 1/4"=1'0"

MAIN FLOOR = 1378 SF
GARAGE = 536 SF

KEY CODES:

(SD) SMOKE DETECTOR

F FAN UNIT

E EGRESS

T TEMPERED

CO CARBON MONOXIDE DETECTOR

PROJECT NAME:


SHEET

A3

PLAN NAME:

MAIN FLOOR PLAN

3 OF 4

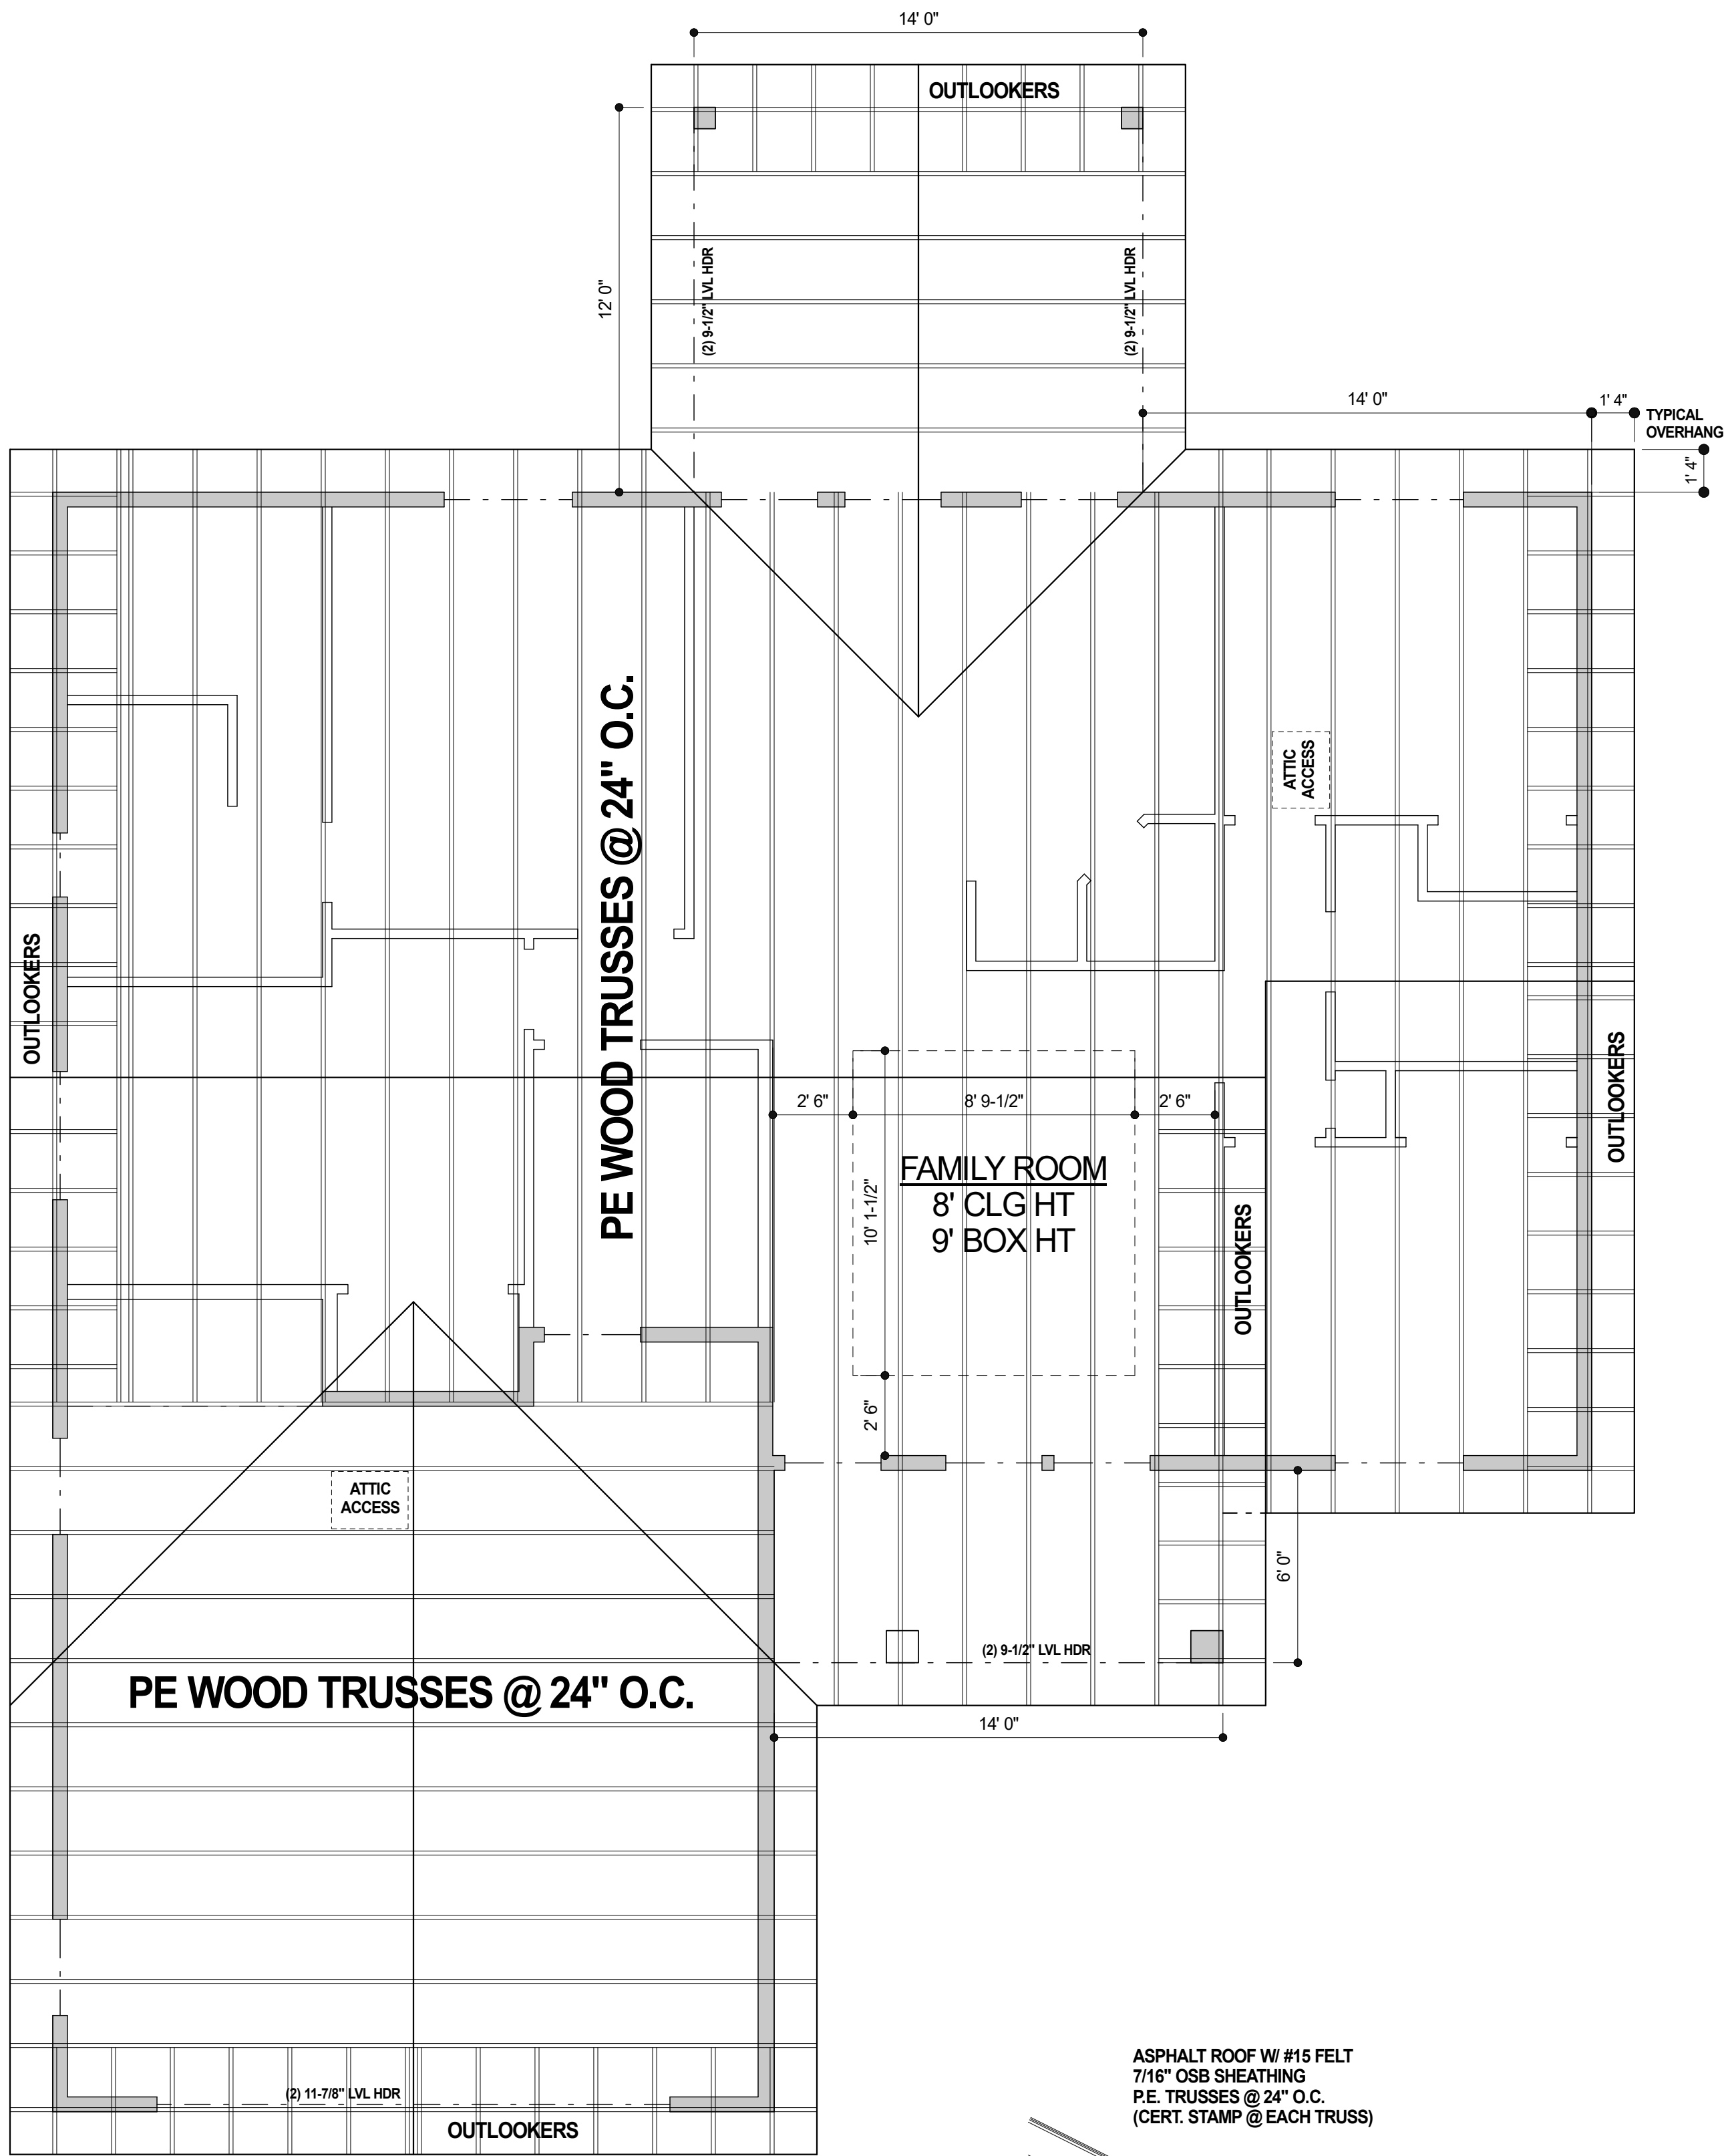


ROOF PLAN

SCALE: 1/4"=1'0"

ROOF NOTES:

1. INSTALL TRUSSES PER MANUFACTURER'S RECOMMENDATIONS INCLUDING ALL BRIDGING AND BRACING.
2. PROVIDE SIMPSON H1 OR EQUAL AT BRG. ENDS OF EACH TRUSS.
3. BEARING WALL HEADERS SHALL BE (2ea) DF 2x10 UNLESS NOTED OTHERWISE.
4. ALL ROOF OVERHANGS SHALL BE AS NOTED.
5. ROOF SHEATHING SHALL BE 7/16" OSB W/ PLY CLIPS
6. ALL SHADED AREAS REPRESENT LOAD BEARING POINTS FOR TRUSSES.
7. ROOF VENTILATION REQUIREMENTS PER IRC R806.1

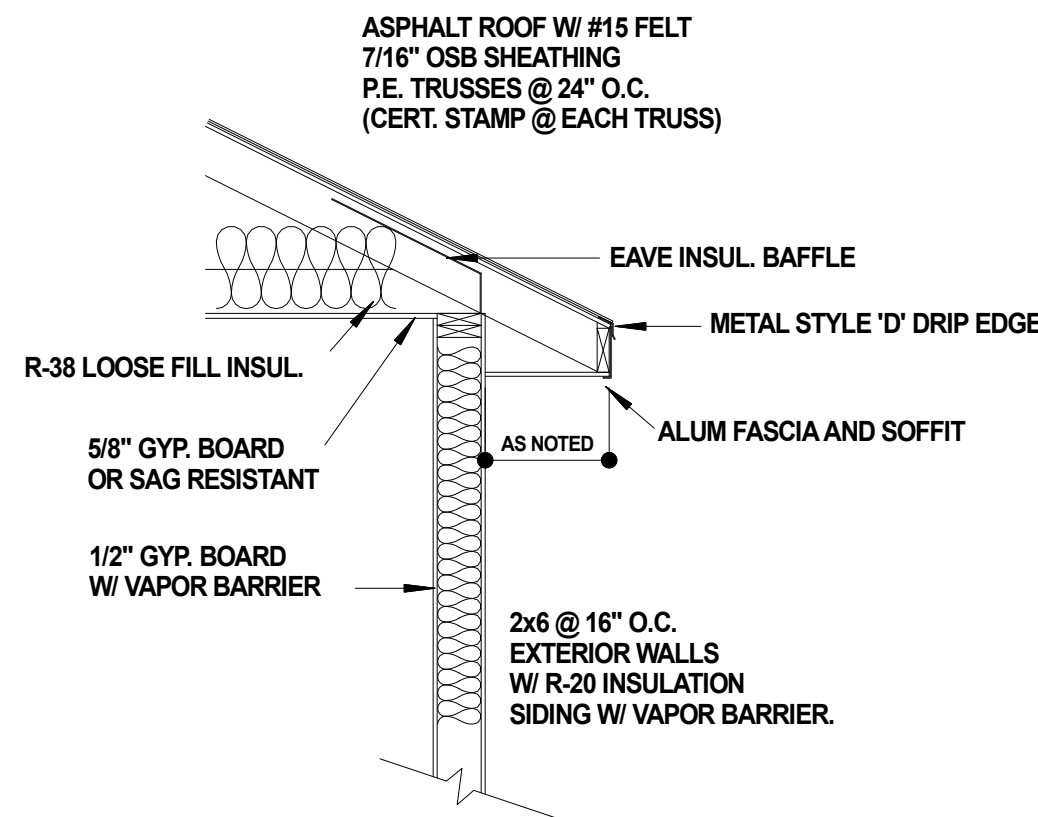


TYP. EAVE DETAIL

SCALE: 1/2" = 1'0"



FRONT ELEVATION

SCALE: 1/4"=1'0"

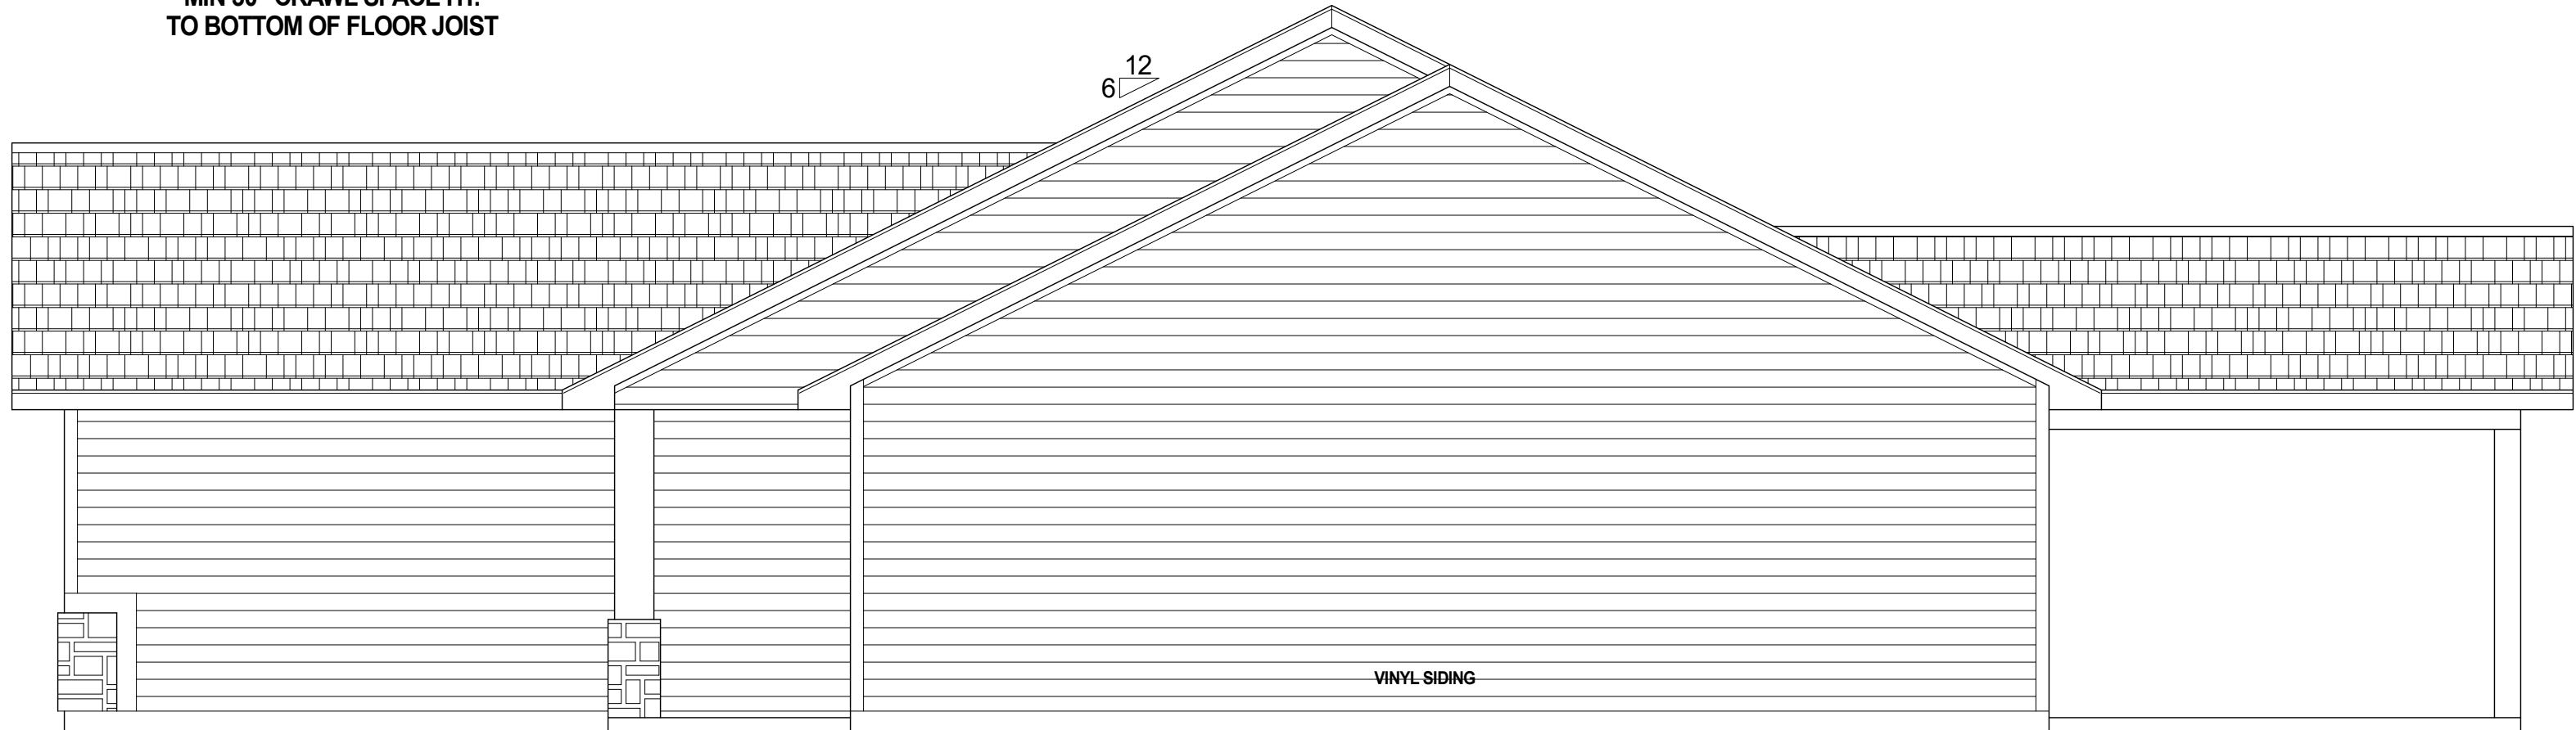


RIGHT ELEVATION

SCALE: 1/4"=1'0"



REAR ELEVATION

SCALE: 1/4"=1'0"

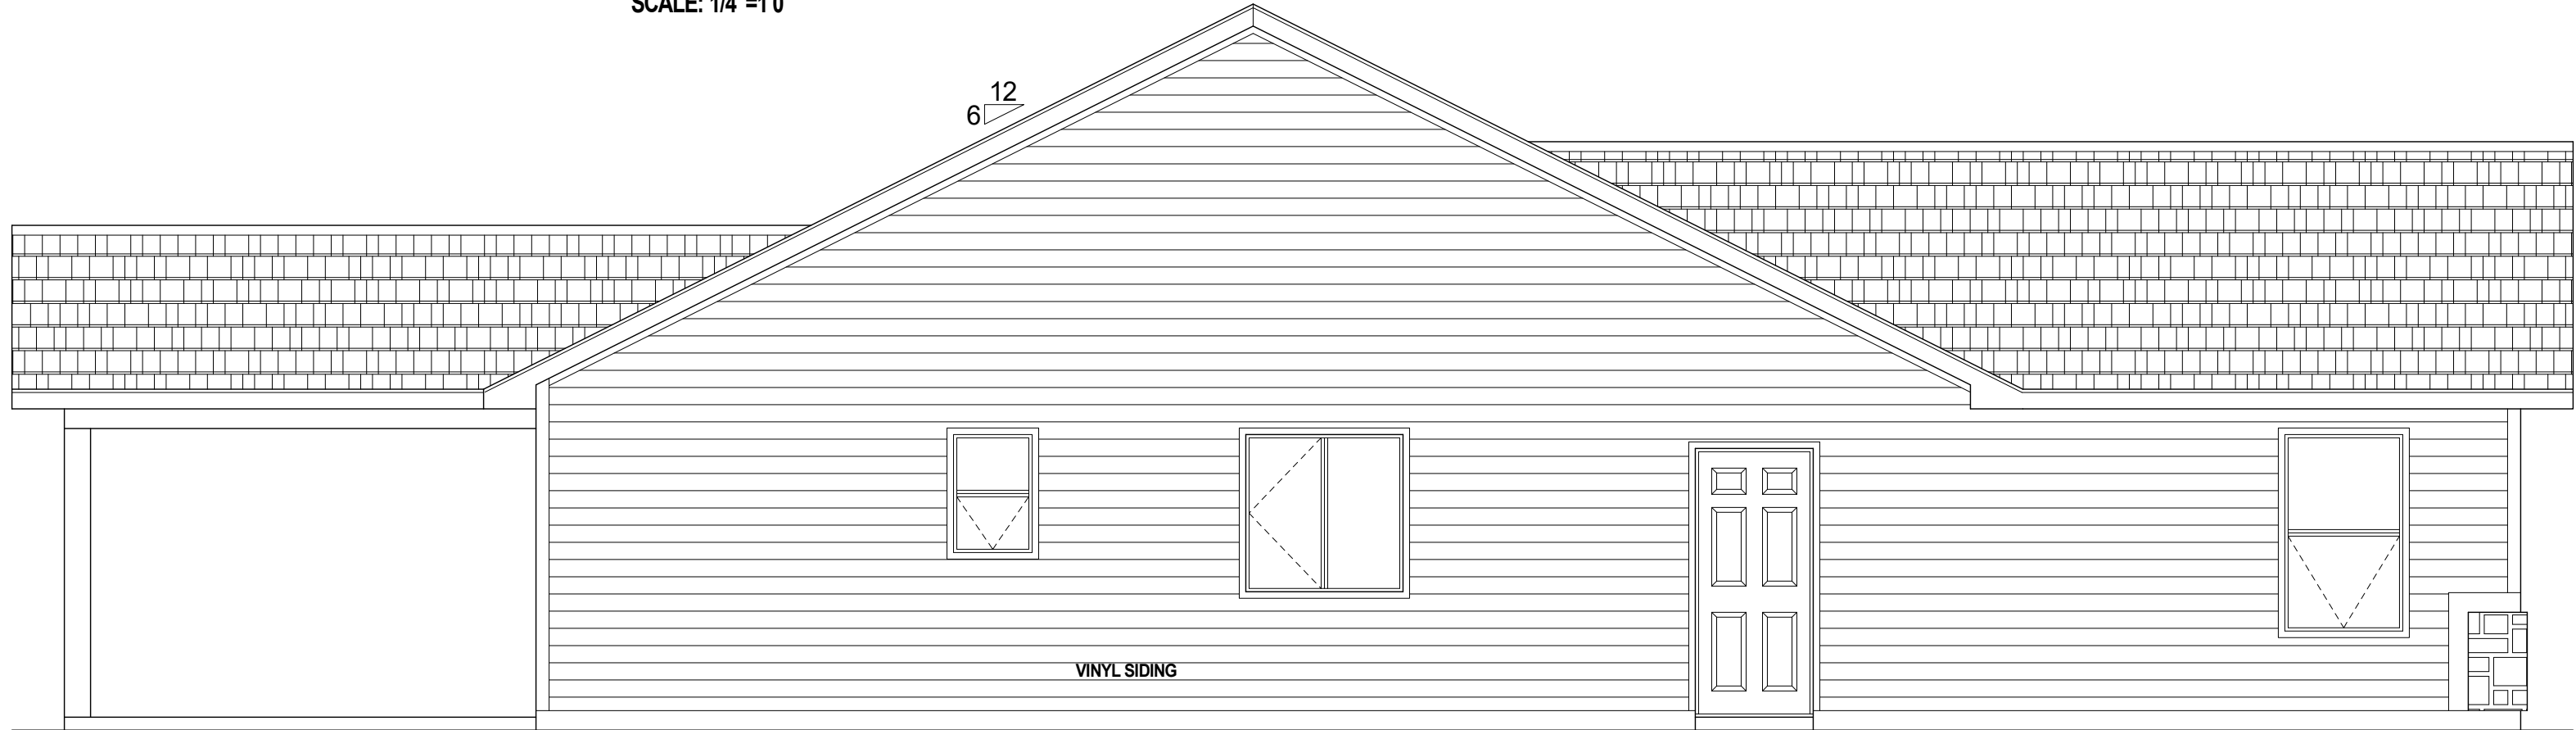

LEFT ELEVATION

SCALE: 1/4"=1'0"

Plans and Rendering by Owens Design.

DISCLAIMER NOTE: While every attempt has been made in preparation of these plans to ensure accuracy, the user assumes all responsibility for the use of these plans. The user shall be responsible for obtaining all necessary permits and for compliance with all applicable building codes and regulations. The user shall also be responsible for obtaining all necessary approvals from the local building department. 



SCALE:

1/4" = 1'-0"

DRAWN BY:

Lance Owens

DATE DRAWN:

07-JAN-22

LAST REVISED:

00-00-00

PROJECT NAME:

SHEET:

A4

PLAN NAME:

ROOF PLAN & ELEVATIONS

4 OF 4

Lance LeBaron Homes
MARTINEZ RESIDENCE
GOVT., LOT-6, SECTION-7, T.10 S., R.20 E., B.M.
JEROME COUNTY, IDAHO