


EXISTING ZONE: INDUSTRIAL
EXISTING USE: VACANT LOT
PROPOSED USE: COMMERCIAL DEVELOPMENT
DEVELOPMENT AREA: ±18,806 SF
BENCH MARK:
DOMESTIC WATER: SUBDIVISION WILL USE CITY OF WENDELL WATER SUPPLY.
SEWER: SUBDIVISION WILL USE CITY OF WENDELL SEWER SYSTEM.
STREETS: ACCESS TO SUBDIVISION WILL BE FROM THE S WALLACE ST.
UTILITIES: LOTS WILL BE SERVICED BY UNDERGROUND POWER, NATURAL GAS, AND COMMUNICATION.
STORM RUNOFF: STORM WATER RUN-OFF WILL BE RETAINED ON SITE AS REQUIRED BY THE CITY CODE.

ENGINEER AND SURVEYOR:
TD&H ENGINEERING, INC.
161 5TH AVENUE S., SUITE 105
TWIN FALLS, IDAHO 83301
PHONE: 208-733-2446
EMAIL: tdhengineering.com


OWNER:
SNAKE RIVER PROPERTIES WENDELL II.
2184 CHANNING WAY #463
IDAHO FALLS, IDAHO 83404
CONTACT PERSON: Attn: ERIC IVIE
PHONE: 208-390-9679

STORM WATER CALCULATIONS													
50 YR 24HR STORM													
PROJECT NAME:		SNAKE RIVER PROPERTIES											
DATE:		4/20/2021											
STORM DEPTH (IN):		1.90											
DRYWELL VOID S:		40%											
LOCATION	BUILDING		LANDSCAPING		CONCRETE		GRAVEL		TOTAL (SF)	RUNOFF (CF)	SWALE (CF)	DRYWELL (CF)	
	AREA (SF)	C	AREA (SF)	C	AREA (SF)	C	AREA (SF)	C					
SITE PLAN LOTS 2, 3, 4	7,680	0.95	5,632	0.25	1,280	0.95	4,215	0.75	18,806	2,071	2,071	5,178	
TOTAL RETENTION REQUIRED BEFORE CREDITS												2,071	5,178
PRE DEVELOPMENT CREDIT			NO		PRE DEVELOPMENT RUNOFF COEFFICIENT					0.35		0.00	0.00
TOTALS												2,071	5,178
EQUATION: VOLUME (CF) = DEPTH (IN) / 12 * AREA (SF) * COEFFICIENT													

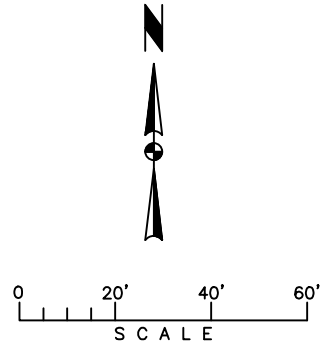

GENERAL NOTES

1. ALL WORK SHALL CONFORM TO IDAHO STANDARDS FOR PUBLIC WORKS CONSTRUCTION CURRENT EDITION AND CITY OF WENDELL STANDARD SPECIFICATIONS.
2. THE CONTRACTOR SHALL MAINTAIN ALL EXISTING DRAINAGE FACILITIES WITHIN THE CONSTRUCTION AREA UNTIL THE DRAINAGE IMPROVEMENTS ARE IN PLACE AND FUNCTIONING.
3. ALL CONTRACTORS WORKING WITHIN THE PROJECT BOUNDARIES ARE RESPONSIBLE FOR COMPLIANCE WITH ALL APPLICABLE SAFETY LAWS OF ANY JURISDICTIONAL BODY. THE CONTRACTOR SHALL BE RESPONSIBLE FOR ALL BARRICADES, SAFETY DEVICES AND CONTROL OF TRAFFIC WITHIN AND AROUND THE CONSTRUCTION AREA.
4. ALL MATERIAL FURNISHED ON OR FOR THE PROJECT MUST MEET OR EXCEED THE MINIMUM REQUIREMENTS OF THE APPROVING AGENCIES OR AS SET FORTH HEREIN, WHICHEVER IS MORE RESTRICTIVE. CONTRACTORS MUST FURNISH PROOF THAT ALL MATERIALS INSTALLED ON THIS PROJECT MEET THE REQUIREMENTS OF ITEM #7 AT THE REQUEST OF THE APPROVING AGENCY AND/OR THE DESIGN ENGINEER.
5. THE LOCATIONS OF EXISTING UNDERGROUND UTILITIES ARE SHOWN IN AN APPROXIMATE WAY ONLY. THE CONTRACTOR SHALL DETERMINE THE EXACT LOCATION OF ALL EXISTING UTILITIES BEFORE COMMENCING WORK. THE CONTRACTOR ASSUMES ALL RESPONSIBILITY FOR ANY AND ALL DAMAGES CAUSED BY HIS FAILURE TO EXACTLY LOCATE AND PRESERVE ANY AND ALL UNDERGROUND UTILITIES. CONTACT DIGLINE AT 1-800-342-1585 OR AT WWW.DIGLINE.COM
6. WORK SUBJECT TO APPROVAL BY ANY POLITICAL SUBDIVISION OR AGENCY MUST BE APPROVED PRIOR TO (A) BACKFILLING TRENCHES FOR PIPE; (B) PLACING OF AGGREGATE BASE; (C) PLACING OF CONCRETE; (D) PLACING OF ASPHALT PAVING. WORK DONE WITHOUT SUCH APPROVAL DOES NOT RELIEVE THE CONTRACTOR FROM THE RESPONSIBILITY OF PERFORMING THE WORK IN AN ACCEPTABLE MANNER.
7. LOCATE SUBSURFACE STORMWATER DISPOSAL FACILITIES (INCLUDING INFILTRATION BEDS AND DRYWELLS) AT LEAST 25 FEET FROM WATER MAINS. THIS REQUIREMENT DOES NOT APPLY TO CATCH BASINS OR SAND AND GREASE VAULTS.
8. THE CONTRACTOR SHALL KEEP ON SITE AT ALL TIMES A COPY OF THE APPROVED CONSTRUCTION PLANS ON WHICH IS RECORDED THE ACTUAL LOCATIONS OF THE CONSTRUCTED PIPE LINE AND ANY OTHER UTILITIES ENCOUNTERED. THE CONTRACTOR SHALL PROVIDE THESE LOCATIONS TO THE DESIGN ENGINEER FOR USE IN THE PRODUCTION OF RECORD DRAWINGS PRIOR TO FINAL APPROVAL OF THE PIPE LINE INSTALLATION.
9. "THE CONTRACTOR SHALL BE RESPONSIBLE FOR OBTAINING ALL LOCAL, STATE, AND FEDERAL PERMITS REQUIRED FOR STORMWATER POLLUTION PREVENTION AS A RESULT OF CONSTRUCTION ACTIVITIES. THE CONTRACTOR SHALL PREPARE A STORMWATER POLLUTION PREVENTION PLAN FOR REVIEW BY THE ENGINEER. IF THE CONSTRUCTION WILL DISTURB MORE THAN ONE ACRE, THE CONTRACTOR SHALL OBTAIN A COPY OF THE U.S. ENVIRONMENTAL PROTECTION AGENCY'S NPDES GENERAL PERMIT FOR STORMWATER DISCHARGE ASSOCIATED WITH CONSTRUCTION ACTIVITY (OTHERWISE KNOWN AS THE CONSTRUCTION GENERAL PERMIT OR CGP) AND SUBMIT A "NOTICE OF INTENT" (NOI) [EPA FORM 3510-9 (6/03)] FOR PERMIT COVERAGE UNDER THE GENERAL PERMIT. THE CGP MAY BE FOUND ON THE INTERNET AT [HTTPS://WWW.EPA.GOV/NPDES/2022-CONSTRUCTION-GENERAL-PERMIT-CGP](https://www.epa.gov/npdes/2022-construction-general-permit-cgp) OR BY CONTACTING THE U.S. EPA OFFICE OF WATER DIRECTLY AT (800) 424-4372. THE NOI MAY BE FILED ELECTRONICALLY AT THE FOLLOWING WEBSITE: [HTTP://CFPUB.EPA.GOV/NPDES/STORMWATER/ENOL.CFM](http://cfpub.epa.gov/npdes/stormwater/enol.cfm). THE CGP DOES NOT RELIEVE THE CONTRACTOR FROM COMPLIANCE WITH OTHER REGULATIONS OR CONTRACT REQUIREMENTS REGARDING STORMWATER POLLUTION PREVENTION INCLUDING BUT NOT LIMITED TO: PROTECTION OF SURFACE WATERS, PREVENTION OF SOIL RUNOFF INTO DRAINS, DUST CONTROL, PREVENTION OF TRACKING SOILS TO ADJACENT STREETS, FUEL CONTAINMENT, SPILL CONTROL, ETC.

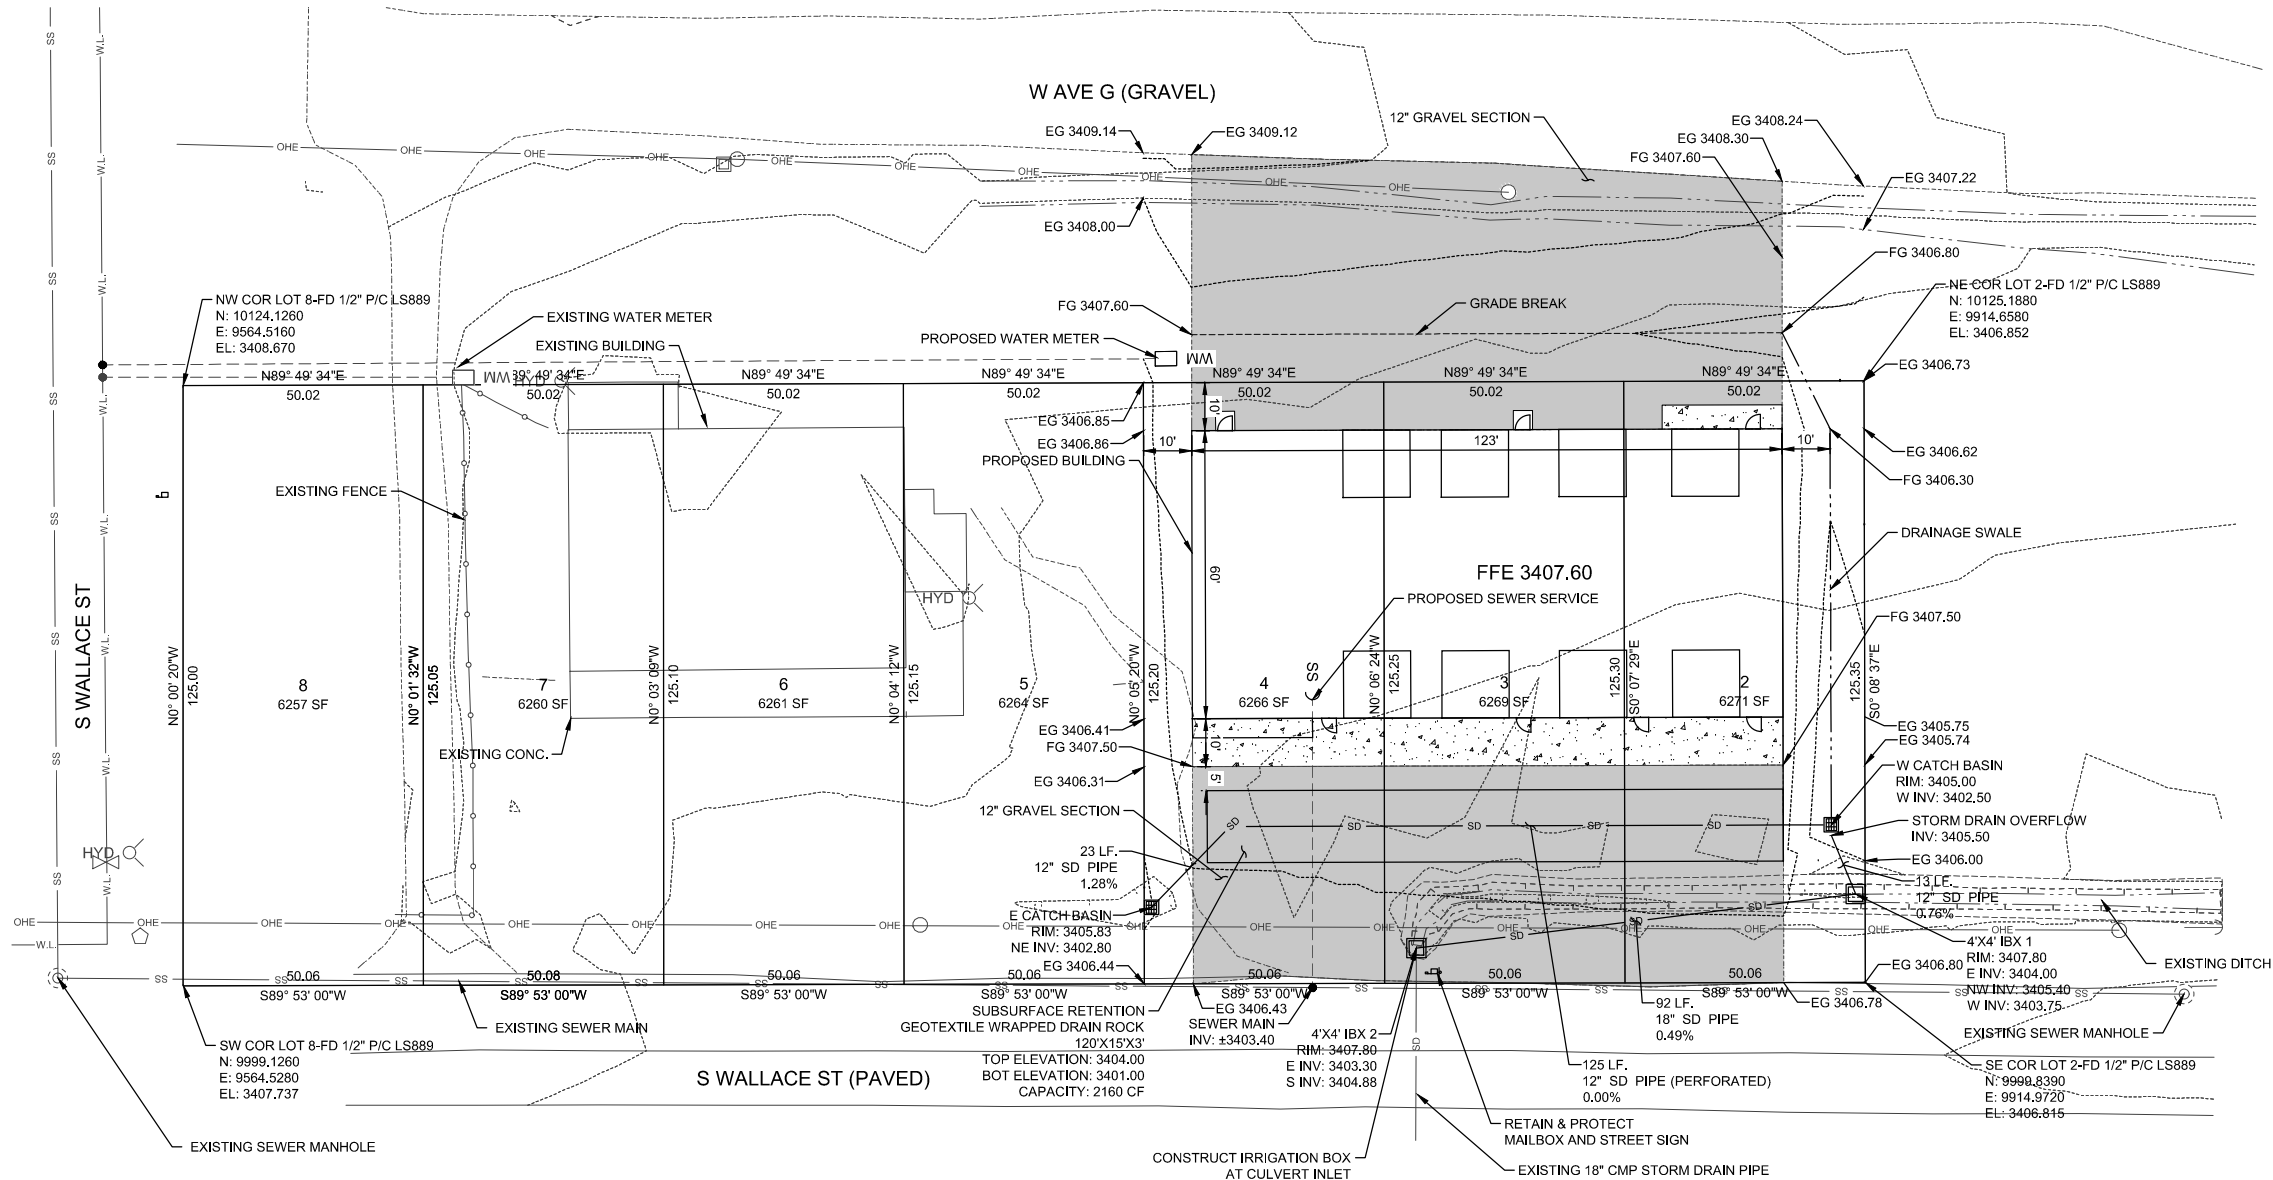

DRAWN BY: LD
DESIGNED BY: LD
QUALITY CHECK: CLB
DATE: 6/16/2022
JOB NO. TF21-054
FIELDBOOK

SNAKE RIVER PROPERTIES
WENDELL, IDAHO
SITE PLAN